



**A** ENCONTRO  
ESCALA 1:5

 

**B** CANTO EM L — PLANTA  
ESCALA 1:5

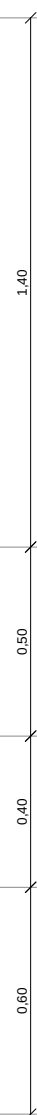

**C** REFORÇO PARA CARGA SUSPensa — ELEVACAO DA PAREDE  
ESCALA 1:20



**D** RODAPE  
ESCALA 1:5



**E** JUNTA DE MOVIMENTACAO DE FACHADA — PLANTA (montante duplo)  
ESCALA 1:5

| ITEM    | AMB   | FAMILIA       | KG | PAISIDE    | Z mm     | MONC. | OSB m2 |
|---------|-------|---------------|----|------------|----------|-------|--------|
| LC-05-G | T-COR | galimės butas | 90 | Vien 12000 | 600-1200 | 3     | 0.24   |
| LC-15-G | T-REV | galimės butas | 90 | Vien 12000 | 600-1200 | 3     | 0.28   |
| LC-05-G | S-02  | galimės butas | 90 | Vien 12000 | 600-1200 | 3     | 0.28   |
| LC-05-G | S-03  | galimės butas | 90 | Vien 12000 | 600-1200 | 3     | 0.28   |
| LC-15-G | S-04S | galimės butas | 90 | Vien 12000 | 600-1200 | 5     | 0.17   |
| LY-05-P | T-03C | paletė tv     | 70 | Vien 12000 | 600-1200 | 5     | 2.52   |
| LY-08-C | T-REV | calimės       | 25 | Vien 12000 | 300-1200 | 5     | 2.64   |
| LY-10-C | S-02  | calimės       | 25 | Vien 7800  | 300-1200 | 5     | 2.64   |
| LY-15-C | S-03  | calimės       | 25 | Vien 7800  | 300-1200 | 5     | 2.64   |
| LY-12-C | S-04S | calimės       | 25 | Vien 2600  | 300-1200 | 6     | 3.04   |
| LY-05-C | S-04S | paletė tv     | 70 | Vien 12000 | 600-1200 | 5     | 2.7    |
| LY-05   | T-03C | tv            | 35 | Vien 12000 | 600-1200 | 4     | 0.99   |
| LY-14   | S-04S | tv            | 35 | Vien 2500  | 600-1200 | 4     | 0.94   |

ENCONTROS EM T — 12

| PAY | T     | Y     | CONTRIBUTA | EXTERNA |
|-----|-------|-------|------------|---------|
| T   | 1400  | 13300 | H          | NOB     |
| T   | 8400  | 13300 | H          | NOB     |
| T   | 10350 | 9600  | H          | NOB     |
| T   | 2400  | 13300 | V          | NOB     |
| T   | 9600  | 22300 | V          | NOB     |
| T   | 13600 | 22300 | V          | NOB     |
| S   | 13600 | 10000 | H          | NOB     |
| S   | 13300 | 10000 | H          | NOB     |
| S   | 2400  | 10000 | V          | NOB     |
| S   | 7800  | 18800 | V          | NOB     |
| S   | 7800  | 18300 | V          | NOB     |
| S   | 15600 | 18300 | V          | NOB     |

## NOTAS

- Encontro em T: 12 na casa, derivados das paredes (ponta de uma parede dentro de outra). Detalhe unico: montante adicional na parede continua, clip de guia, 4 parafusos 4,8 x 19 por metro.

\* Carga superior: 12 litros (gabinete de banho, painéis de TV, cabecelas e as duas TVs) localizados na parede que os recebe; reforço de OSB 18 mm entre montantes na faixa de altura do item, 19,0 m2. Parede de LSF não segura bucha; segura montante e reforço.

- Junta de movimentação de fachada: 23 (x) cada 6 m e em cada canto, 10 mm com poliuretano com tarugo, sobre montante duplo, placas não passam pela junta.

|   |                                                                                          |   |                                                          |
|---|------------------------------------------------------------------------------------------|---|----------------------------------------------------------|
| PROJETO PORTO REAL   |                                                                                          |   |                                                          |
| RESIDENCIAL UNIFAMILIAR   MANAUS - AM   SUBS. TÁBUA 01                                                                     |                                                                                          |   |                                                          |
| PROJETO ARQUITETÔNICO   |                                                                                          |   |                                                          |
| DETALHES DO LSF — ENCONTROS, CARGA SUSPensa, RODAPE E JUNTA DE FACHADA                                                     |                                                                                          |   |                                                          |
| <div>BASE GEOMÉTRICA</div> <div>Lista Complementa</div> <div>plan022 (planoset)</div> <div>USINAGEM INTERIORE - 04x4</div> | <div>ESCALA</div> <div>1:5 • 1:20</div> <div>FORMATO A4</div> <div>MALHA 600000000</div> | <div>DESENHO</div> <div>ESTUDO PRELIMINAR R7B</div> <div>SINCRONIZADO PARA OBRA</div> <div>SEMA ANT 1 ANT</div> | <div>VERSÃO</div> <div>68</div> <div>01-72 REV R7B</div> |