




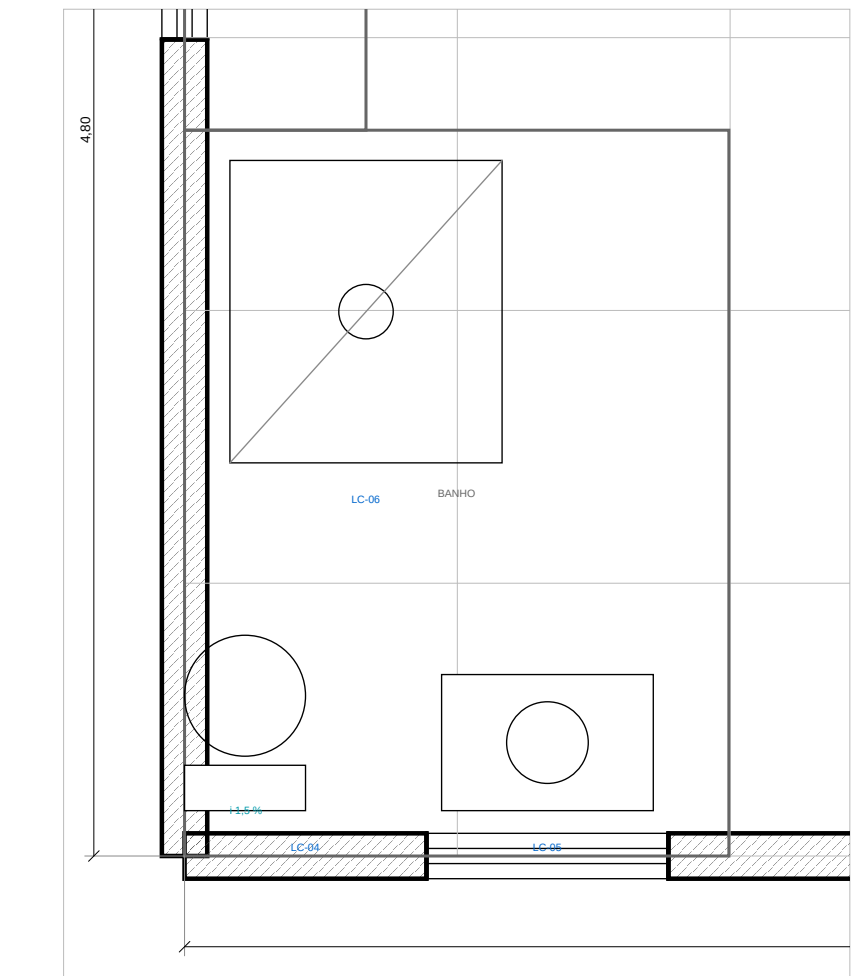


1 SUITE 02 — BANHO  
ESCALA 1:25

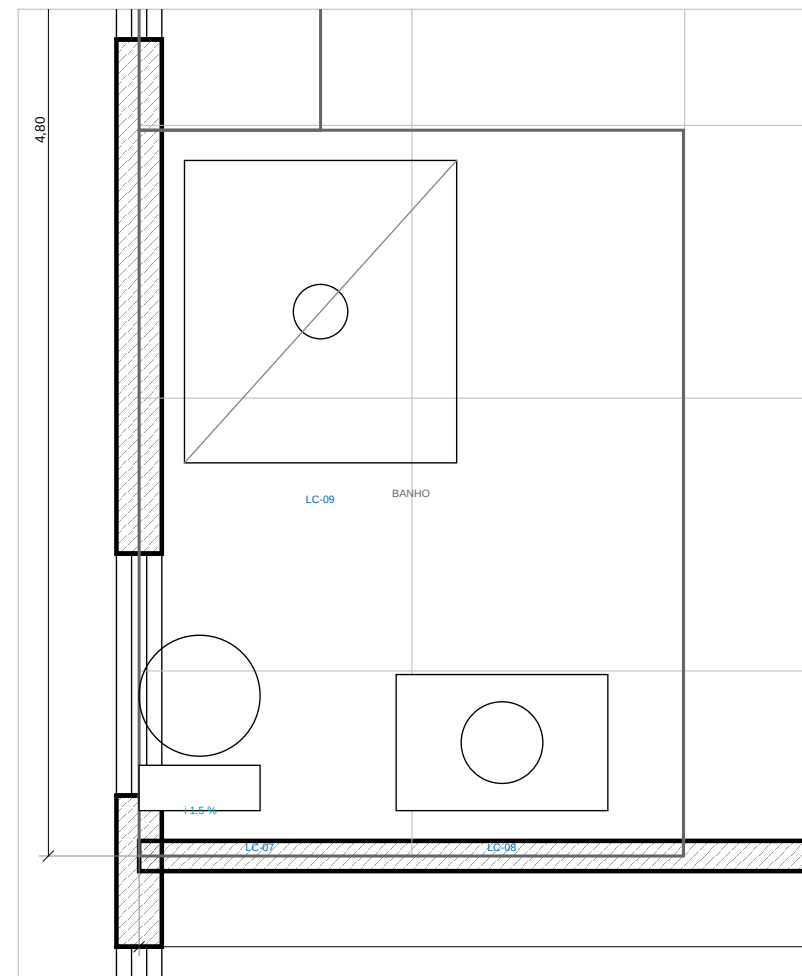

2 SUITE 03 — BANHO  
ESCALA 1:25

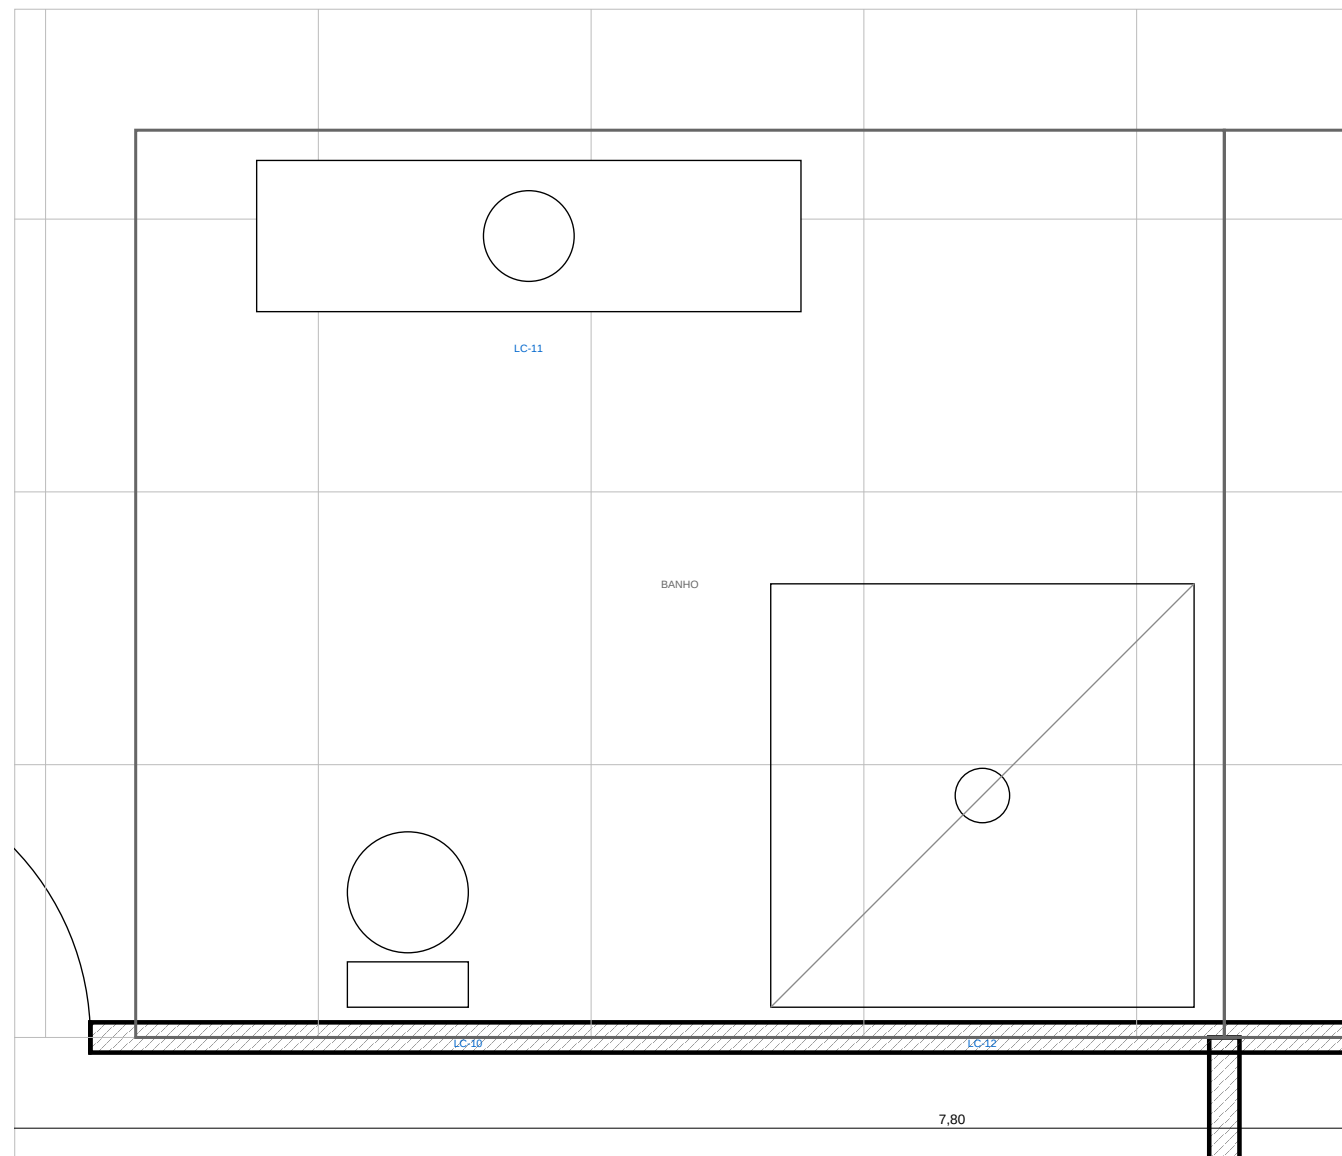

3 MASTER — BANHO  
ESCALA 1:25

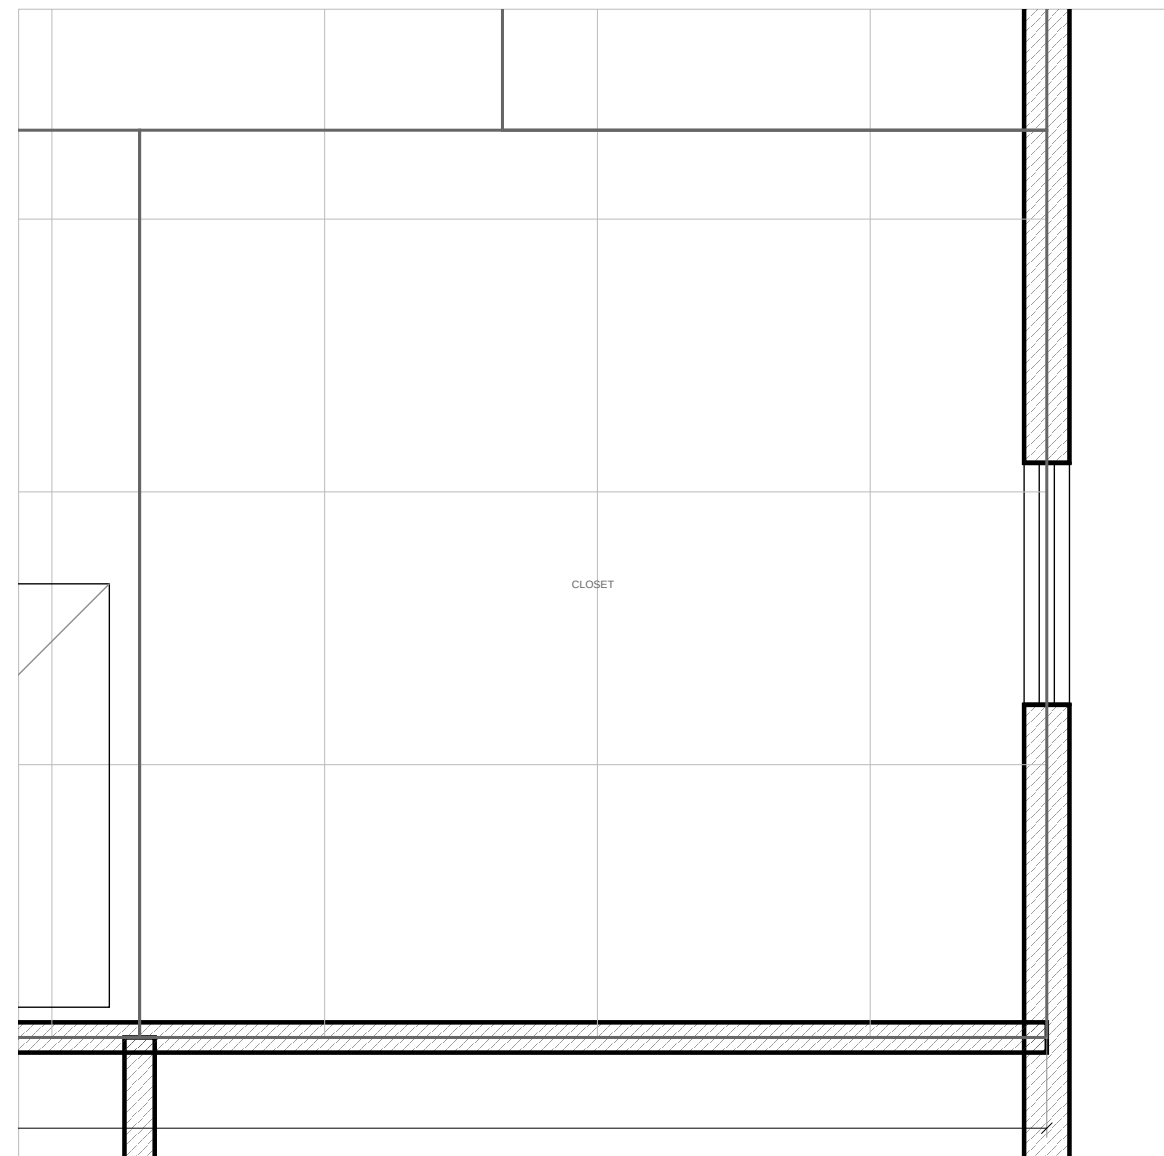

4 MASTER — CLOSET  
ESCALA 1:25

PAGINACAO VERIFICADA — PECAS INTEIRAS + RECORTE EM CADA PONTA

| AMB   | AMBIENTE         | ZONA | PEÇA | EXO X  | EXO Y    | ALTURA (mm) |
|-------|------------------|------|------|--------|----------|-------------|
| S-002 | SUITE 02 — BANHO | ZP-3 | gno  | S-0000 | S-0000   | ---         |
| S-003 | SUITE 03 — BANHO | ZP-3 | gno  | S-0000 | A-000007 | ---         |
| S-005 | MASTER — BANHO   | ZP-2 | gno  | S-0000 | C-0000   | ---         |
| S-006 | MASTER — CLOSET  | ZP-2 | gno  | S-0000 | S-0000   | ---         |

- NOTAS
- \* Pignoneiros de piso em linha fina, a malha vem da ZONA de pignoneiros, não do canto do ambiente.
  - \* Peca de piso porcelanado retificado 300 x 300, parede ceramico retificado 300 x 600, porta 2 mm.
  - \* Cimento de 1,5 kg para o piso em toda area molhada, soltura elevada 15 mm nos bicos.
  - \* Representação: porta ligada em 2 dimensões, altura 200 mm na parede e 1.800 mm nos bicos.

PROJETO PORTO REAL

RESIDENCIA UNIFAMILIAR (MANAUS - AM) | SUITE TATIANA-PS

PROJETO ARQUITETONICO

AMPLIACOES DE AREA MOLHADA — SUPERIOR

|                                                                                    |                                                     |                                                                               |                                |
|------------------------------------------------------------------------------------|-----------------------------------------------------|-------------------------------------------------------------------------------|--------------------------------|
| BASE GEOMETRICA<br>Linha Consolidada<br>Projeto (previsão)<br>UNIDADE: METROS - MM | ESCALA<br>1:25<br>FORMATO: A1<br>MILHA: 600/500/300 | EMISSAO<br>ESTUDO PRELIMINAR R56<br>Linha LIBERADO PARA OBRA<br>SEM ART / RNT | PROJETA<br>23<br>06-45 REV 006 |
|------------------------------------------------------------------------------------|-----------------------------------------------------|-------------------------------------------------------------------------------|--------------------------------|