


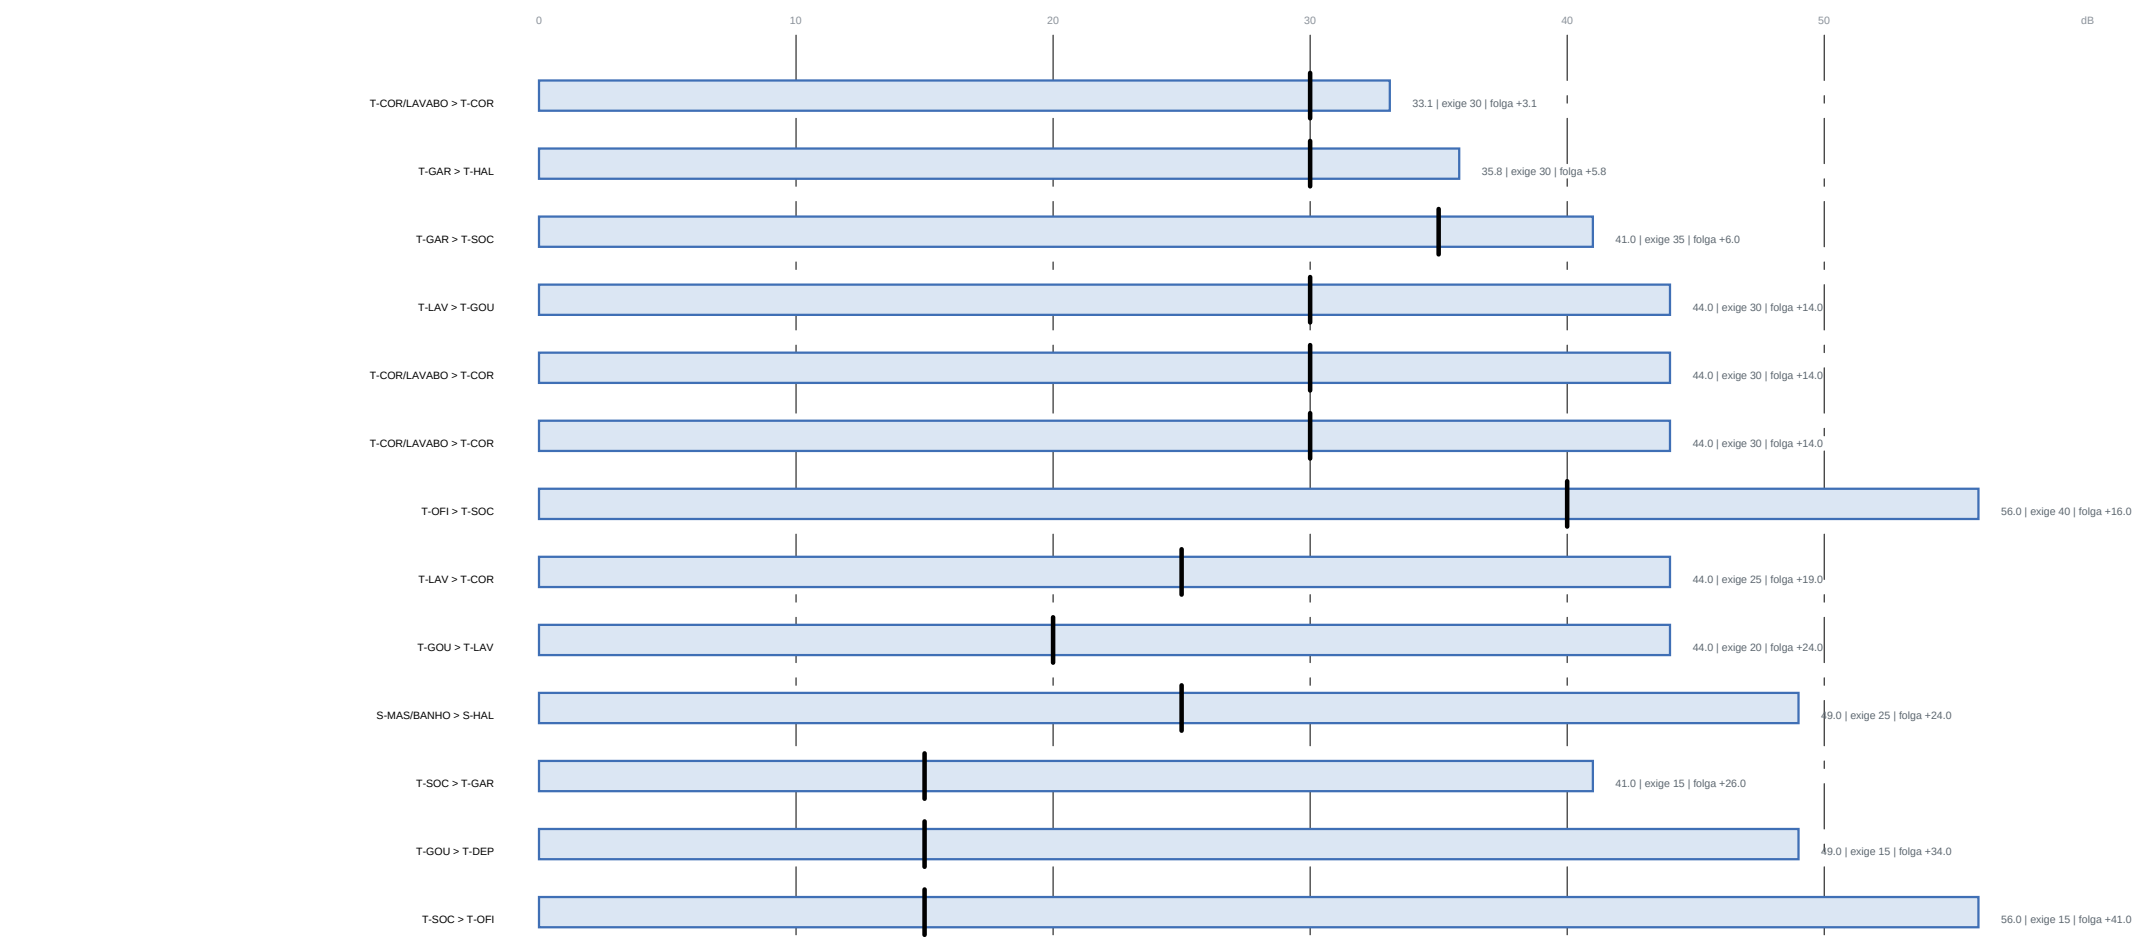

Barra = isolamento obtido; traço vertical = exigência (valor da fonte menos limite do receptor, NBR 15552)

O QUE MUDOU EM R52

ONDE	ANTES	DEPOIS	POR QUE
Banho compartilhado + hall de entrada	porta de correr (Pw 20) — conjunto de 20,2 dB	parede CEGSA, 44 dB	o acesso de volta passou para a circulação
Banho compartilhado + quarto eventual	porta com (Pw 20) — conjunto de 20,5 dB, exigia 25	parede CEGSA, 44 dB	era a por passagem da casa, e não era a saída
Hall + garagem	porta com — 36,9 dB, exigia 30	PDS isolou entrada — 50,9 dB	porta entre garagem e casa tem dupla função para ser morda
Banho compartilhado + circulação	não havia porta	PDS isolou entrada — 35,7 dB, exigia 25	único acesso do banho, e abria para fora
Bloco do chuveiro	encostado na parede do hall	canto arredado, told e janela alta	consequência da porta nova, a regra dos 900 cm de box obrigou a primeira tentativa

TABELAS ADOTADAS

ITEM	VALOR	FONTE
Fonte: caixa sanitária	75 dB(A)	prática corrente de acústica
Fonte: bloco do chuveiro	70 dB(A)	prática corrente de acústica
Fonte: cozinha e gourmet	70 dB(A)	prática corrente de acústica
Fonte: sala e jantar	70 dB(A)	prática corrente de acústica
Fonte: garagem	70 dB(A)	prática corrente de acústica
Fonte: máquina de lavar e secar	70 dB(A)	prática corrente de acústica
Fonte: oficina	60 dB(A)	prática corrente de acústica
Limite: banho	45 dB(A)	NBR 15552:2017 (circulação e entrada adaptada)
Limite: circulação	45 dB(A)	NBR 15552:2017 (circulação e entrada adaptada)
Limite: cozinha	45 dB(A)	NBR 15552:2017 (circulação e entrada adaptada)
Limite: dormitório	50 dB(A)	NBR 15552:2017 (circulação e entrada adaptada)
Limite: escritório	50 dB(A)	NBR 15552:2017 (circulação e entrada adaptada)
Limite: entrada	45 dB(A)	NBR 15552:2017 (circulação e entrada adaptada)
Limite: estar	45 dB(A)	NBR 15552:2017 (circulação e entrada adaptada)
Limite: sala	45 dB(A)	NBR 15552:2017 (circulação e entrada adaptada)
Limite: oficina	50 dB(A)	NBR 15552:2017 (circulação e entrada adaptada)
Limite: serviço	50 dB(A)	NBR 15552:2017 (circulação e entrada adaptada)
Fonte: academia	Pw 25 dB	Nota de mercado declarada
Fonte: cinema	Pw 25 dB	Nota de mercado declarada
Fonte: sala	Pw 20 dB	Nota de mercado declarada
Fonte: sala de	Pw 25 dB	Nota de mercado declarada
Fonte: sala de visita	Pw 20 dB	Nota de mercado declarada

NOTAS

1 Esta planilha existe porque o proprietário perguntou o que 100 verificações não sabem responder: quem entra na casa ouve o chuveiro do banheiro da entrada?

2 Ouviu. A parede era boa (Pw 44), mas ali é a porta era do corredor (Pw 20), o conjunto entregava 20 dB. Em acústica o teto faz toda a diferença, se não tem nada, se não tem nada, se não tem nada.

3 Isolamento no seu engelo ENTRE, mas. Dentro da sala social o teto não é perfeito, é o problema.

4 O isolamento igual ao 10 cm (comprimento declarado), não é pre-verificação de projeto, não é verificação de projeto, não é verificação de projeto, não é verificação de projeto.

PROJETO PORTO REAL

RESIDENCIA UNIFAMILIAR (MANSÃO - AM) | SOBR TATIANA-PS

PROJETO ARQUITETÔNICO

DESEMPENHO ACUSTICO ENTRE AMBIENTES

BASE GEOMÉTRICA	ESCALA	EMISSÃO	PROVA
Lista Consolidada	s/ escala	ESTUDO PRELIMINAR R52	
ISO R52 (previsão)	FORMATO A1	ISO LIBERADO PARA CRIA	39
UNIDADE MESTRE: mm	MILHA 605/500/500	SEM ART / INT	06-48 REVISO