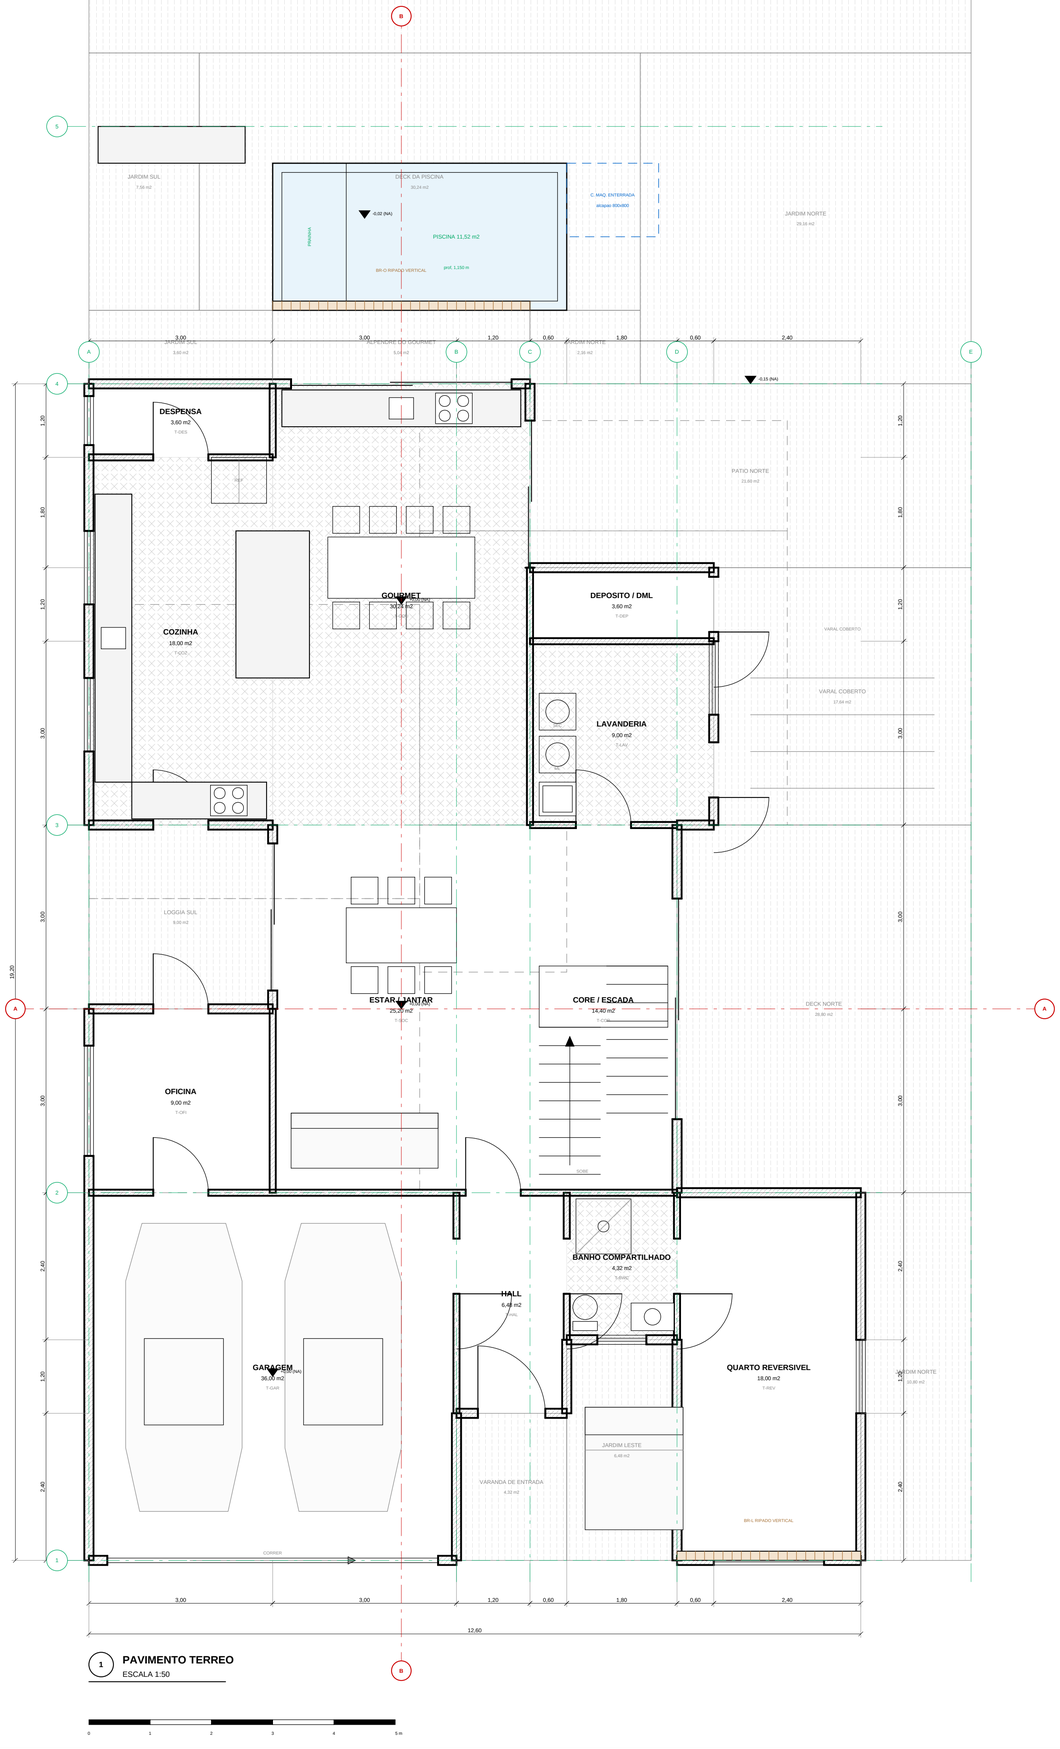


1 **PAVIMENTO TERREO**
ESCALA 1:50

QUADRO DE AREAS — PAVIMENTO TERREO

COD	AMBIENTE	MODULO (mm)	AREA (m2)
T-GAR	GARAGEM	6000x6000	36,00
T-HAL	HALL	1800x3600	6,48
T-BWC	BANHO COMPARTILHADO	1800x2400	4,32
T-REV	QUARTO REVERSIVEL	3000x6000	18,00
T-OFI	OFICINA	3000x3000	9,00
T-SOC	ESTAR / JANTAR	4200x6000	25,20
T-COR	CORE / ESCADA	2400x6000	14,40
T-COZ	COZINHA	3000x6000	18,00
T-GOU	GOURMET	4200x7200	30,24
T-DES	DESPENSA	3000x1200	3,60
T-LAV	LAVANDERIA	3000x3000	9,00
T-DEP	DEPOSITO / DML	3000x1200	3,60
	TOTAL FECHADO		177,84
T-VAR	VARANDA DE ENTRADA (aberta)	1800x2400	4,32
T-JLE	JARDIM LESTE (aberta)	1800x3600	6,48
T-JNO	JARDIM NORTE (aberta)	1800x6000	10,80
T-LOG	LOGGIA SUL (aberta)	3000x3000	9,00
T-DKL	DECK NORTE (aberta)	4800x6000	28,80
T-VRL	VARAL COBERTO (aberta)	4200x4200	17,64
T-PAT	PATIO NORTE (aberta)	7200x3000	21,60
T-ALP	ALPENDRE DO GOURMET (aberta)	4200x1200	5,04
T-DKP	DECK DA PISCINA (aberta)	7200x4200	30,24
T-JSU	JARDIM SUL (aberta)	3000x1200	3,60
T-JS2	JARDIM SUL (aberta)	1800x4200	7,56
T-JN2	JARDIM NORTE (aberta)	1800x1200	2,16
T-JN3	JARDIM NORTE (aberta)	5400x5400	29,16
T-JFU	JARDIM DE FUNDO (aberta)	1440x7800	112,32

MAPA DE ESQUADRIAS DO PAVIMENTO

REF	VAO (mm)	PEIT.	QTD	TIPO
J01	1200x1200	1100	4	janela de dormitorio, aluminio
J04	800x900	1500	2	janela alta de banheiro, basculante
J05	1800x1200	1100	2	janela ampla de dormitorio, aluminio
P01	1100x2800	0	1	porta principal, alta opaca
P02	900x2100	0	5	porta interna (familia unificada)
P04	900x2100	0	6	porta de servico, resistente a umidade
PG01	5400x2400	0	1	portao de correr, aluminio ripado
PVS1	3600x2400	0	2	vao social posterior
PVS2	2400x2400	0	2	porta-balcao do estar (familia adicional — ver

LEGENDA E CONVENCOES (NBR 6492 / 8403)

- Elemento seccionado pelo plano de corte (h = 1,50 m)
- Aresta vista / folha de esquadria
- Mobiliario fixo, equipamentos e simbologia
- Projecao do pavimento superior e da cobertura
- Eixo modular e linha de corte
- Linha de cota e linha auxiliar

N

PERCURSO SOLAR — MANAUS 3 S

O

S

N

L

fachs L e O: sol a 30 graus

-> exigem brise VERTICAL

fachs N e S: sol 63 a 87 graus

-> beiral de 1.200 mm resolve

NOTAS

- Dimensoes em milimetros; cotas de nivel em metros.
- Malha modular 600 mm; cotas eixo a eixo.
- Parede externa 150 mm / divisoria interna 100 mm (h=).
- Mobiliario fixo indica pontos de agua e esgoto (NBR 6492).

PROJETO PORTO REAL

RESIDENCIA UNIFAMILIAR | MANAUS - AM | SUS8 TARUMA (H)

PROJETO ARQUITETONICO

PLANTA DE LAYOUT — PAVIMENTO TERREO

BASE GEOMETRICA	ESCALA	EMISSAO	PRANCHA
Lista Consolidada	1:50	ESTUDO PRELIMINAR	04
psis-R32 (prevalece)	FORMATO A1	NAO LIBERADO PARA OBRA	de 19
UNIDADE MESTRE: mm	MALHA 600/3000/150	SEM ART / RRT	