


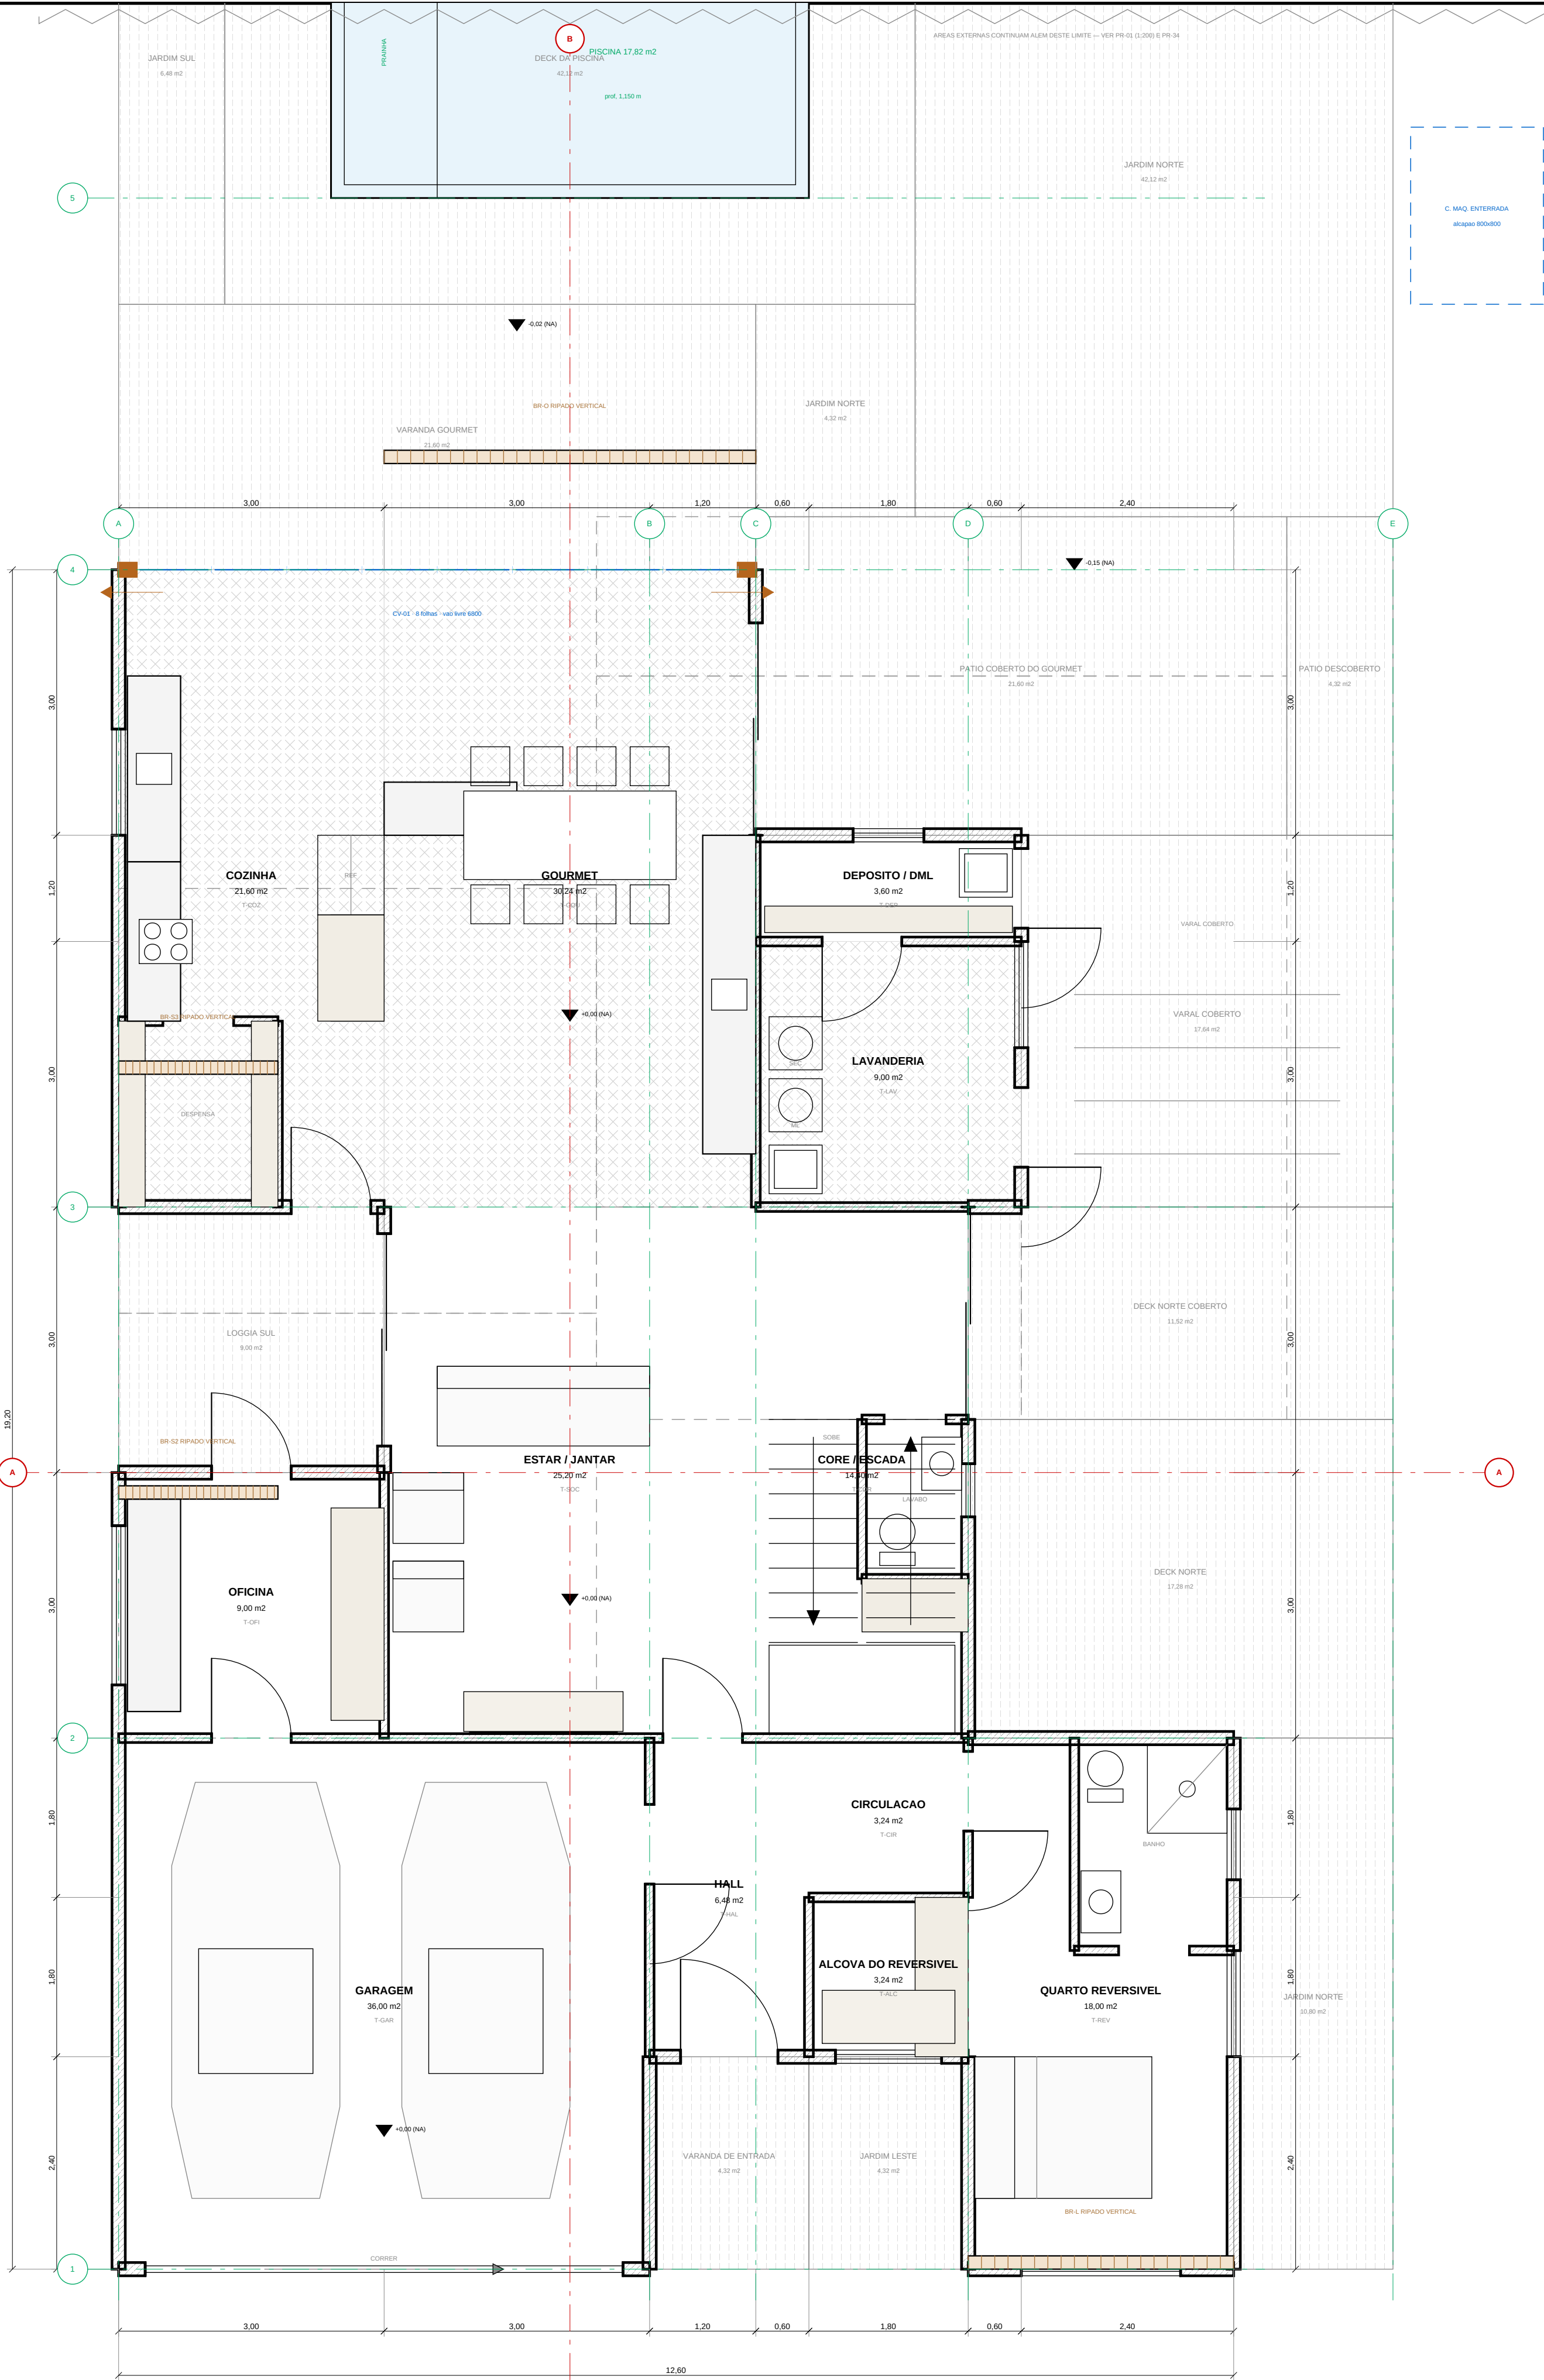

1 PAVIMENTO TERREO
ESCALA 1:50



QUADRO DE ÁREAS — PAVIMENTO TERREO


COD	AMBIENTE	MODULO (mm)	AREA (m²)
T-GAR	GARAGEM	600x600	36,00
T-HAL	HALL	180x300	6,48
T-ALC	ALCOVA DO REVERSIVEL	180x300	5,34
T-QR	CIRCULACAO	180x300	3,24
T-REV	QUARTO REVERSIVEL	300x300	18,00
T-OFI	OFICINA	300x300	9,00
T-SOC	ESTAR / JANTAR	450x600	25,20
T-COR	CORE / ESCADA	240x600	14,40
T-COZ	COZINHA	300x750	22,50
T-GOU	GOURMET	450x750	33,75
T-LAV	LAVANDERIA	300x300	9,00
T-DEP	DEPOSITO / DML	300x1200	3,60
TOTAL FECHADO			188,08
T-VAR	VARANDA DE ENTRADA (aberta)	180x240	4,32
T-J-E	JARDIM LESTE (aberto)	180x240	4,32
T-J-N	JARDIM NORTE (aberto)	180x300	5,40
T-LOG	LOGGIA SUL (aberto)	300x300	9,00
T-DKL	DECK NORTE (aberto)	480x300	14,40
T-DKC	DECK NORTE COBERTO (aberto)	480x240	11,52
T-VRL	VARAL COBERTO (aberto)	450x450	20,25
T-PAT	PATIO COBERTO DO GOURMET (aberto)	600x300	18,00
T-PDZ	PATIO DESCOBERTO (aberto)	1200x300	3,60
T-VLP	VARANDA GOURMET (aberto)	750x300	22,50
T-DEP	DECK DA PISCINA (aberto)	780x340	26,52
T-J-SZ	JARDIM SUL (aberto)	120x600	7,20
T-J-NZ	JARDIM NORTE (aberto)	180x240	4,32
T-J-NZ	JARDIM NORTE (aberto)	540x780	42,12
T-J-PV	JARDIM DE PUNDO (aberto)	1400x400	56,00

MAPA DE ESQUADRIAS DO PAVIMENTO


REF	VALOR (mm)	REF	QTD	TIPO
CVE1	720x240	0	1	CORTINA DE VIDRO vertical, 0 folha de 900 mm
JL1	120x120	120	4	porta de banheiro, alumínio
JL2	80x80	180	1	porta de banheiro, alumínio
JL3	80x80	120	2	porta de banheiro, alumínio
JL4	80x80	120	2	porta de banheiro, alumínio
JL5	180x120	120	2	porta de banheiro, alumínio
JL6	120x120	0	1	porta principal, alumínio
JL7	80x120	0	2	porta interna (aberto)
JL8	80x120	0	6	porta de serviço, alumínio
JL9	80x120	0	1	porta interna de fumaça SOLADA com vidros (pvc)
JL10	540x240	0	1	porta de correr, alumínio
JL11	360x240	0	1	porta de correr, alumínio

LEGENDA E CONVENCOES (NBR 6492 / 8403)

- Elemento seccionado pelo plano de corte (h = 1,50 m)
- Área vista / folha de espelho
- Modulador fixo, equipamento e sinologia
- Propriedade do pavimento superior e da cobertura
- Eixo modular e linha de corte
- Linha de vista e linha auxiliar

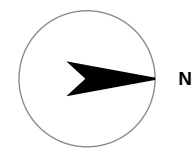

PERCURSO SOLAR — MANUS 1.5

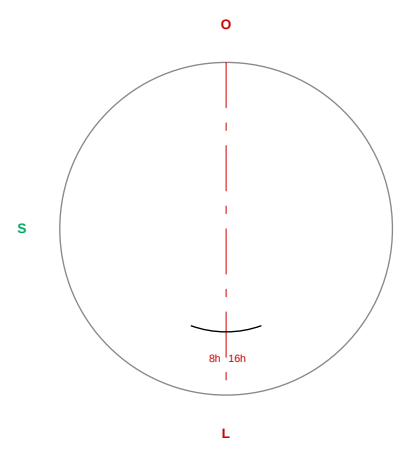

Nota: 1:50 m x 1:50 m
= escala para o projeto
Nota: 1:50 m x 1:50 m
= escala para o projeto

- Dimensões em milímetros, cotas de nível em metros.
- Malha modular 600 mm, cotas em 6 mm.
- Planta externa 120 mm / planta interna 120 mm (p).
- Modulador fixo indica pontos de água e energia (NBR 6492).

PROJETO PORTO REAL

RESIDENCIA UNIFAMILIAR (MANUS - AM) (SOL TARTARUGA)

PROJETO ARQUITETONICO

PLANTA DE LAYOUT — PAVIMENTO TERREO

BASE GEOMETRICA Linha Consolidada pvc 120 (previsão) UNIDADE: METRO (m)	ESCALA 1:50 FORMATO A1 MALHA: 600/600 (mm)	EXIBICAO ESTUDIO PRELIMINAR RIS Linha Consolidada para o projeto SEM ART / RNT	PROJETO 04 06.42 REV. RIS
--	---	---	---------------------------------