


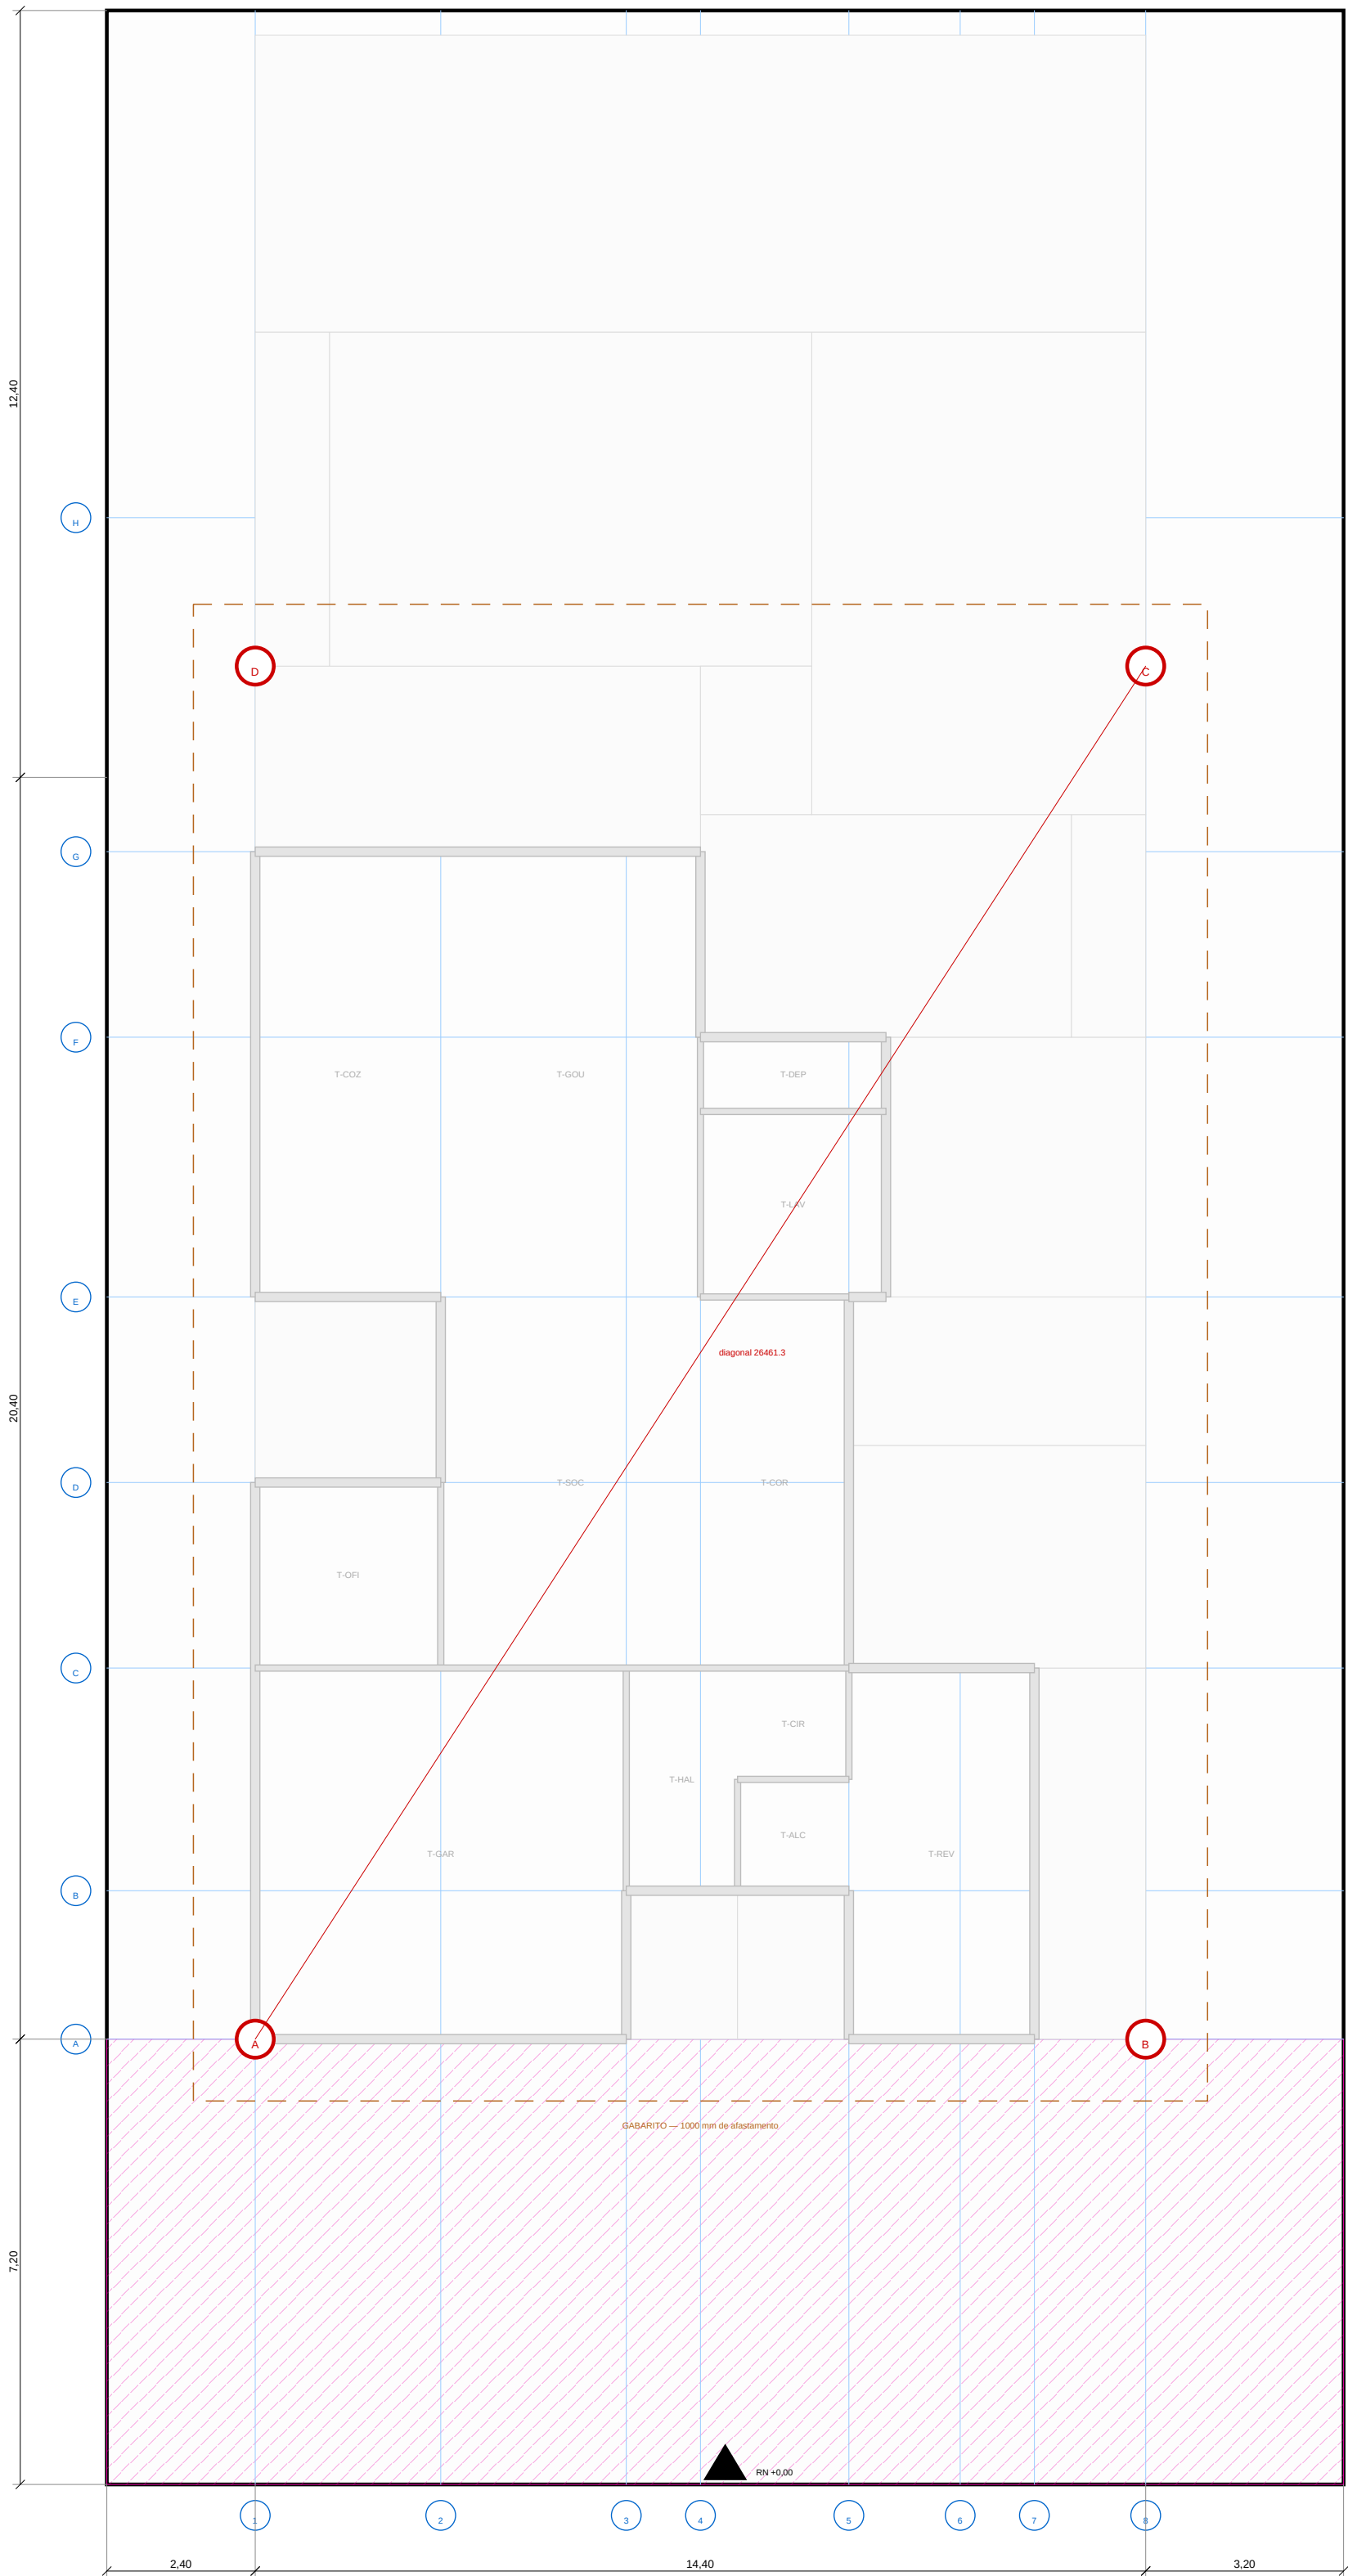

COORDENADAS DOS CANTOS (mm)

CANTO	X	Y	DISSA-ALA	DISSA-NORTE	TESTADA	QUIBO	DIAGONAL
A	2400	7200	2400	17600	7200	32800	26461,3
B	18800	7200	18800	3200	7200	32800	26461,3
C	18800	28400	18800	3200	28400	19600	26461,3
D	2400	28400	2400	17600	28400	19600	26461,3

PROCEDIMENTO DE LOCAÇÃO

#	PASSO	CRITÉRIO DE ACEITE
1	Conferir as divisões com o material de mão de obra	divergência acima de 10 mm interromper a locação
2	Instalar o RMC marca de concreto 200 x 200 x 100 mm, fora da área de obra	fora da área de obra
3	Montar o gabarito a 1000 mm do cantoneiro	perguntar 75 x 75 a tubos 20 x 100
4	Marcar os eixos X (1) e Y (1) a 10 m no gabarito	linha coordenada múltipla de 200 mm
5	Cotar cada canto dos QUADs diretos	verificar em cada canto, erro de cada lado
6	Conferir a diagonal A-C	26461,3 mm com tolerância de 20 mm
7	Conferir o quadrado por 3-4-5 em cada canto	antes de qualquer concretagem
8	Registrar em ata com foto e modelo	gabarito continuo nos dois lados da obra, conferência

EIXOS MODULARES

DIREÇÃO	VALORES (mm)
X (1) e Y (1)	2400 - 5400 - 8400 - 9600 - 12200 - 12800 - 15800 - 16800
Y (1) e X (1)	7200 - 9600 - 13200 - 14200 - 15000 - 28400 - 29400 - 32800
Módulo	principal 600 mm - submódulo 300 mm
Origem	canto frontal esquerdo da base
Unidade	módulo

NOTAS

- Locação é o único documento em que o erro não tem contorno técnico e caso se dê lugar.
- Cada canto e cada lado dos QUADs diretos, marca em cada lado acumulado — erro de cada soma, erro de referência independente não.
- Conferência obrigatória pela diagonal 26461,3 mm entre A e C antes de concretar o núcleo.
- Ata ou plano de locação, elaborado no momento da locação, com foto e modelo.

PROJETO PORTO REAL

RESIDÊNCIA UNIFAMILIAR (MANSÃO) - AM | SOBR TATIANA-PS

PROJETO ARQUITETÔNICO

LOCAÇÃO DE OBRA E GABARITO

BASE GEOMÉTRICA Linha Consolidada Projeto (previsão) Unidade: metro, mm	ESCALA 1:100 Formato A1 Módulo: 600/300/300	DISSAÇÃO ESTUDO PRELIMINAR RIS Linha Libertada PARA OBRA SEM ART / RNT	PROJECÇÃO 31 06/42 REV-RIS
--	---	---	---