


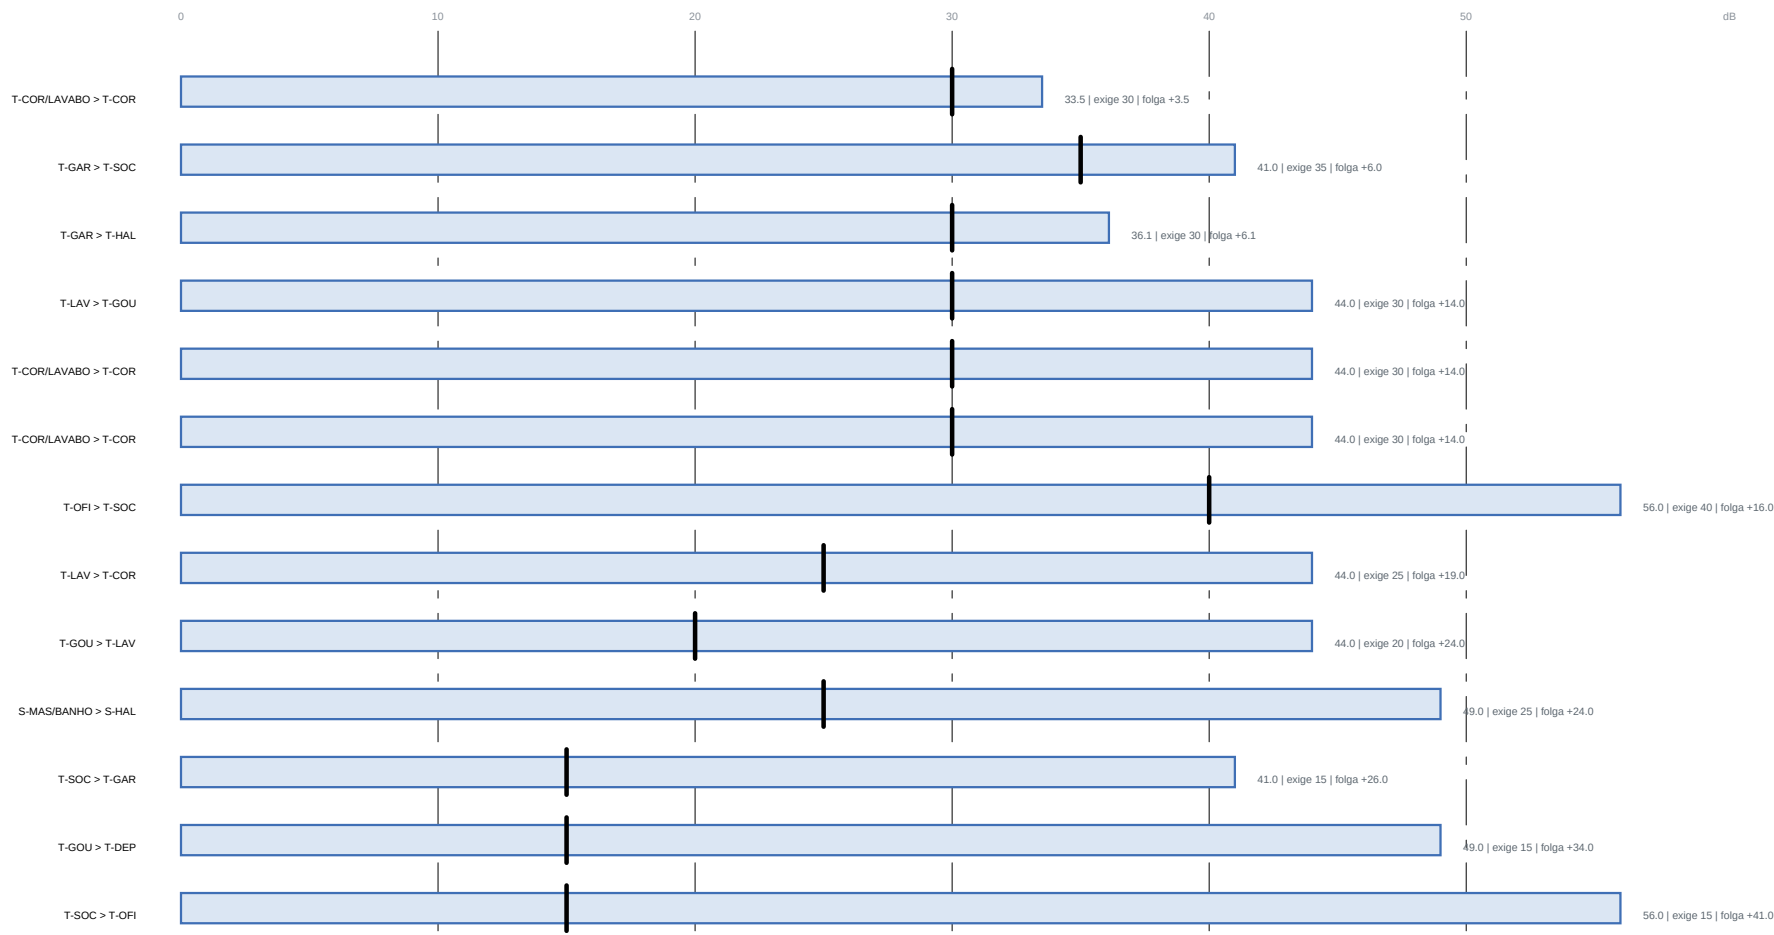

Fonte: s/ isolamento externo; traço vertical = nível (nível da fonte menos nível do receptor, NBR 10152)

O QUE MUDOU EM R\$2

ONDE	ANTES	DEPOIS	POR QUE
Banho compartilhado + hall de entrada	porta de correr (Rw 25) — conjunto de 20,2 dB	parede CEGSA, 44 dB	o acesso de volta passou para a circulação
Banho compartilhado + quarto eventual	porta com (Rw 25) — conjunto de 25,3 dB, nível 35	parede CEGSA, 44 dB	era a por passagem da casa, e não era a saída
Hall + garagem	porta com — 36,9 dB, nível 35	PDS isolada vedada — 50,9 dB	porta entre garagem e casa tem dupla função para ser morda
Banho compartilhado + circulação	não havia porta	PDS isolada vedada — 35,7 dB, nível 25	único acesso do banho, e abria para fora
Bloco do chuveiro	encostado na parede do hall	canto arredondado, toldo e janela alta	consequência da porta nova, a regra dos 900 cm de box obrigou a primeira tentativa

TABELAS ADOTADAS

ITEM	VALOR	FONTE
Fonte: caixa sanitária	15 dB(A)	prática corrente de acústica
Fonte: bloco do chuveiro	15 dB(A)	prática corrente de acústica
Fonte: cozinha e gourmet	15 dB(A)	prática corrente de acústica
Fonte: sala e jantar	15 dB(A)	prática corrente de acústica
Fonte: garagem	15 dB(A)	prática corrente de acústica
Fonte: máquina de lavar e secar	15 dB(A)	prática corrente de acústica
Fonte: oficina	55 dB(A)	prática corrente de acústica
Limite: banho	45 dB(A)	NBR 10152:2017 (circulação e entrada adiabática)
Limite: circulação	45 dB(A)	NBR 10152:2017 (circulação e entrada adiabática)
Limite: cozinha	45 dB(A)	NBR 10152:2017 (circulação e entrada adiabática)
Limite: depósito	55 dB(A)	NBR 10152:2017 (circulação e entrada adiabática)
Limite: dormitório	35 dB(A)	NBR 10152:2017 (circulação e entrada adiabática)
Limite: entrada	45 dB(A)	NBR 10152:2017 (circulação e entrada adiabática)
Limite: estar	45 dB(A)	NBR 10152:2017 (circulação e entrada adiabática)
Limite: garagem	55 dB(A)	NBR 10152:2017 (circulação e entrada adiabática)
Limite: office	45 dB(A)	NBR 10152:2017 (circulação e entrada adiabática)
Limite: oficina	55 dB(A)	NBR 10152:2017 (circulação e entrada adiabática)
Limite: serviço	55 dB(A)	NBR 10152:2017 (circulação e entrada adiabática)
Fonte: academia	Rw 25 dB	tela de mercado declarada
Fonte: cinema	Rw 25 dB	tela de mercado declarada
Fonte: sala	Rw 25 dB	tela de mercado declarada
Fonte: sala de estar	Rw 25 dB	tela de mercado declarada
Fonte: sala de jantar	Rw 25 dB	tela de mercado declarada
Fonte: sala de estar	Rw 25 dB	tela de mercado declarada

NOTAS

1 Esta planilha serve para o proprietário perguntar o que 100 verificações não sabem responder: quem entra na casa ouve o chuveiro do banheiro da entrada?

2 Ouviu. A parede era tipo (Rw 15), mas não a porta era do corredor (Rw 25), o conjunto entregava 20 dB. Em acústica o nível médio aritmético do isolamento, se somar energia que passa.

3 Isolamento no seu nível ENTRE portas. Dentro da sala social o nível não é definido, é o programa.

4 O aditivo igual ao R2 (compensação decorativa), não é pre-verificação de projeto, mas ensaio de campo da NBR 10152-3.

PROJETO PORTO REAL

RESIDENCIA UNIFAMILIAR (MANSÃO - AM) | SOBR TATIANA-PS

PROJETO ARQUITETÔNICO

DESEMPENHO ACUSTICO ENTRE AMBIENTES

BASE GEOMÉTRICA	ESCALA	EMISSÃO	PROVA
Lista Consolidada	s/ escala	ESTUDO PRELIMINAR R15	
ISO R152 (previsão)	FORMATO A1	ISO LIBERADO PARA CRIAÇÃO	39
UNIDADE MÉTRICA: mm	MILIMETROS (600/900/1200)	SEM ART / RNT	60 42 REV R15