
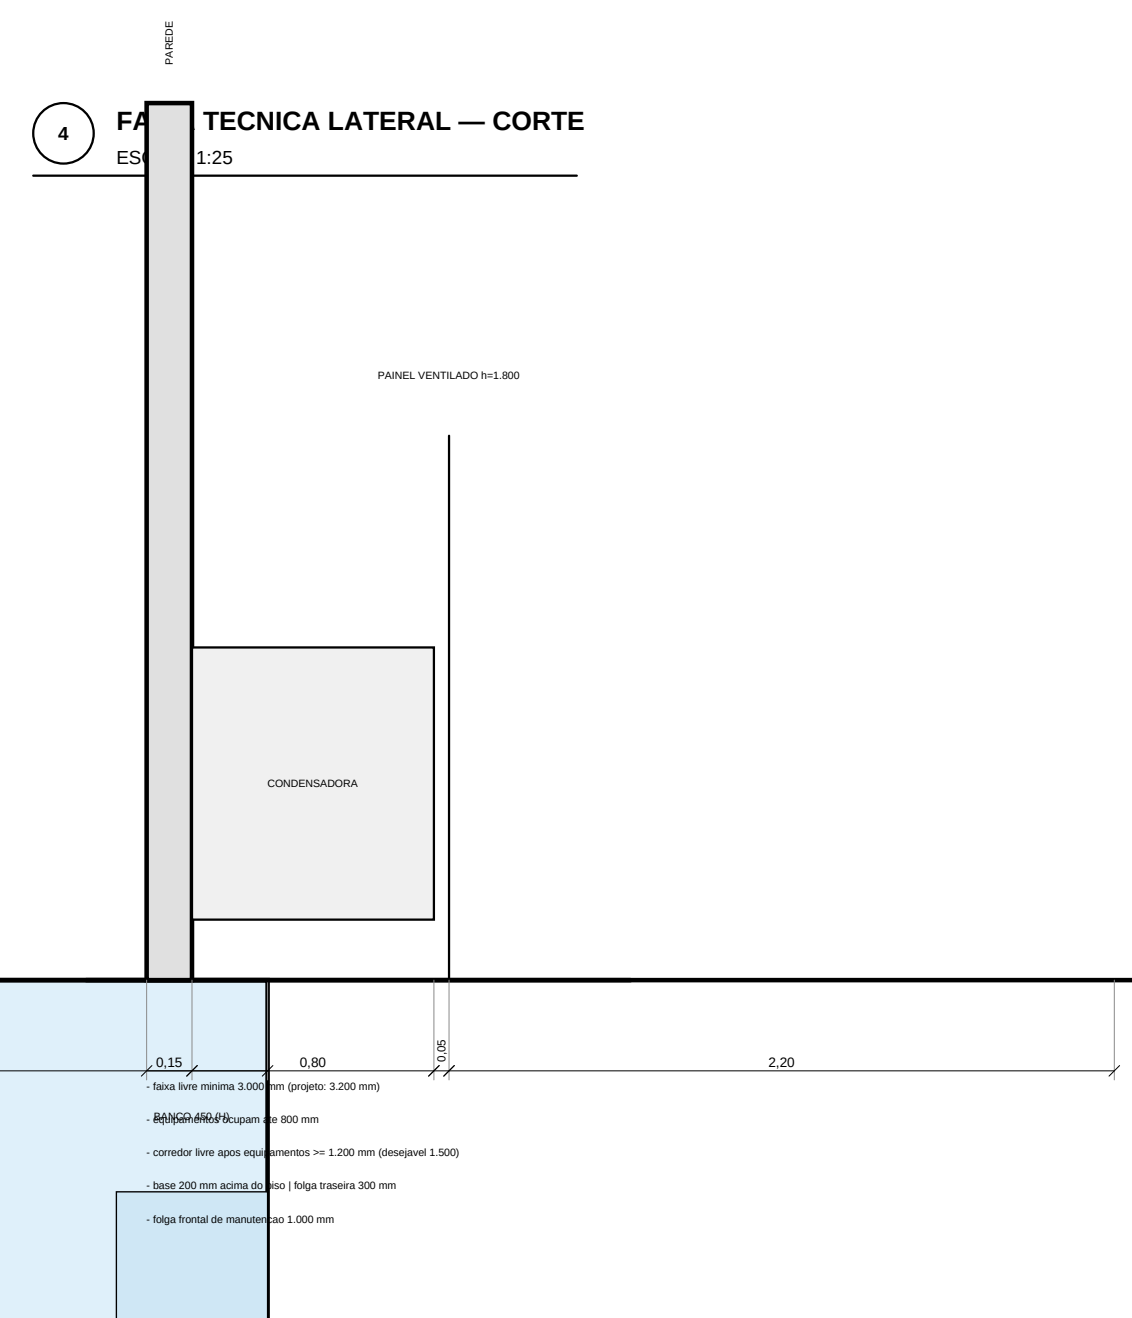
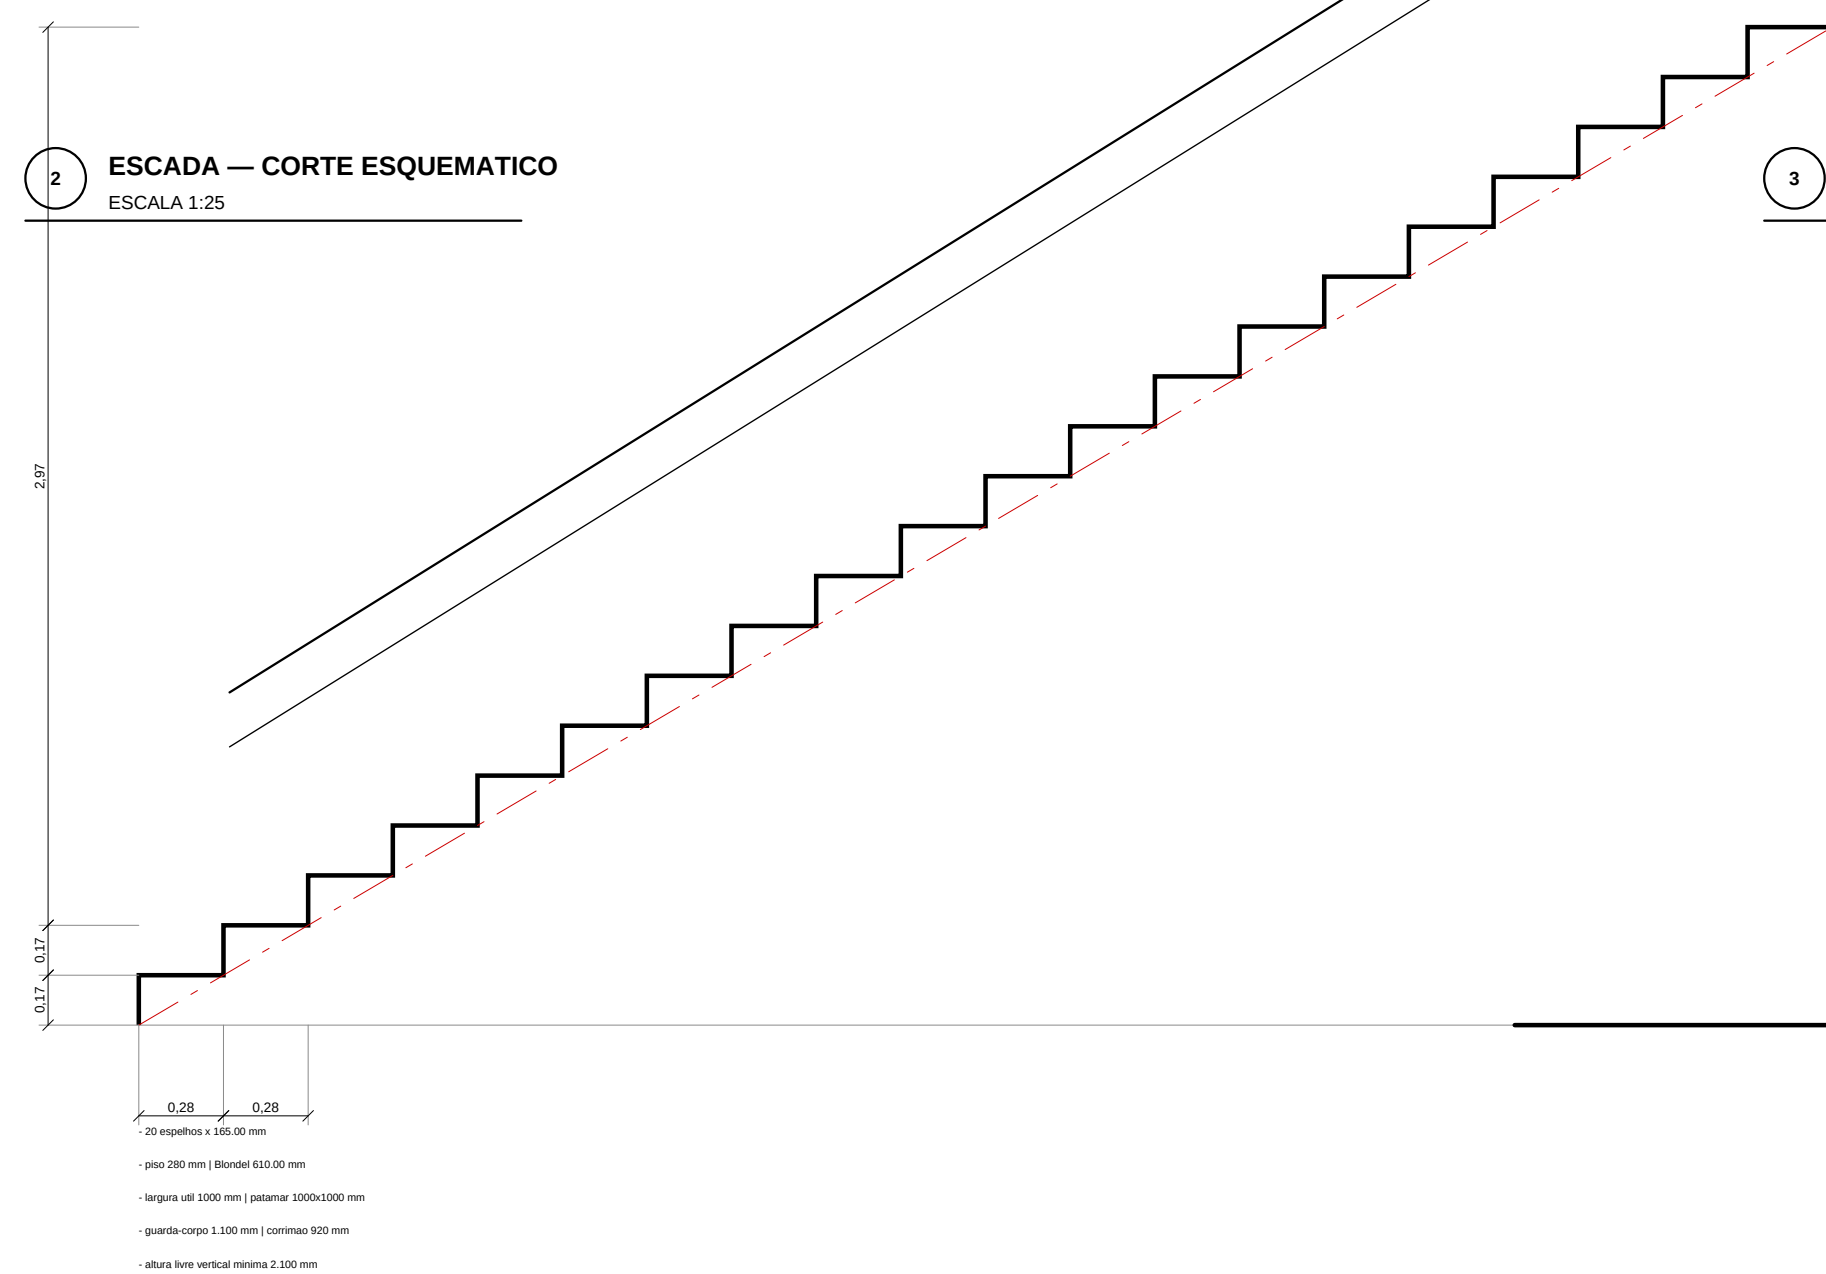


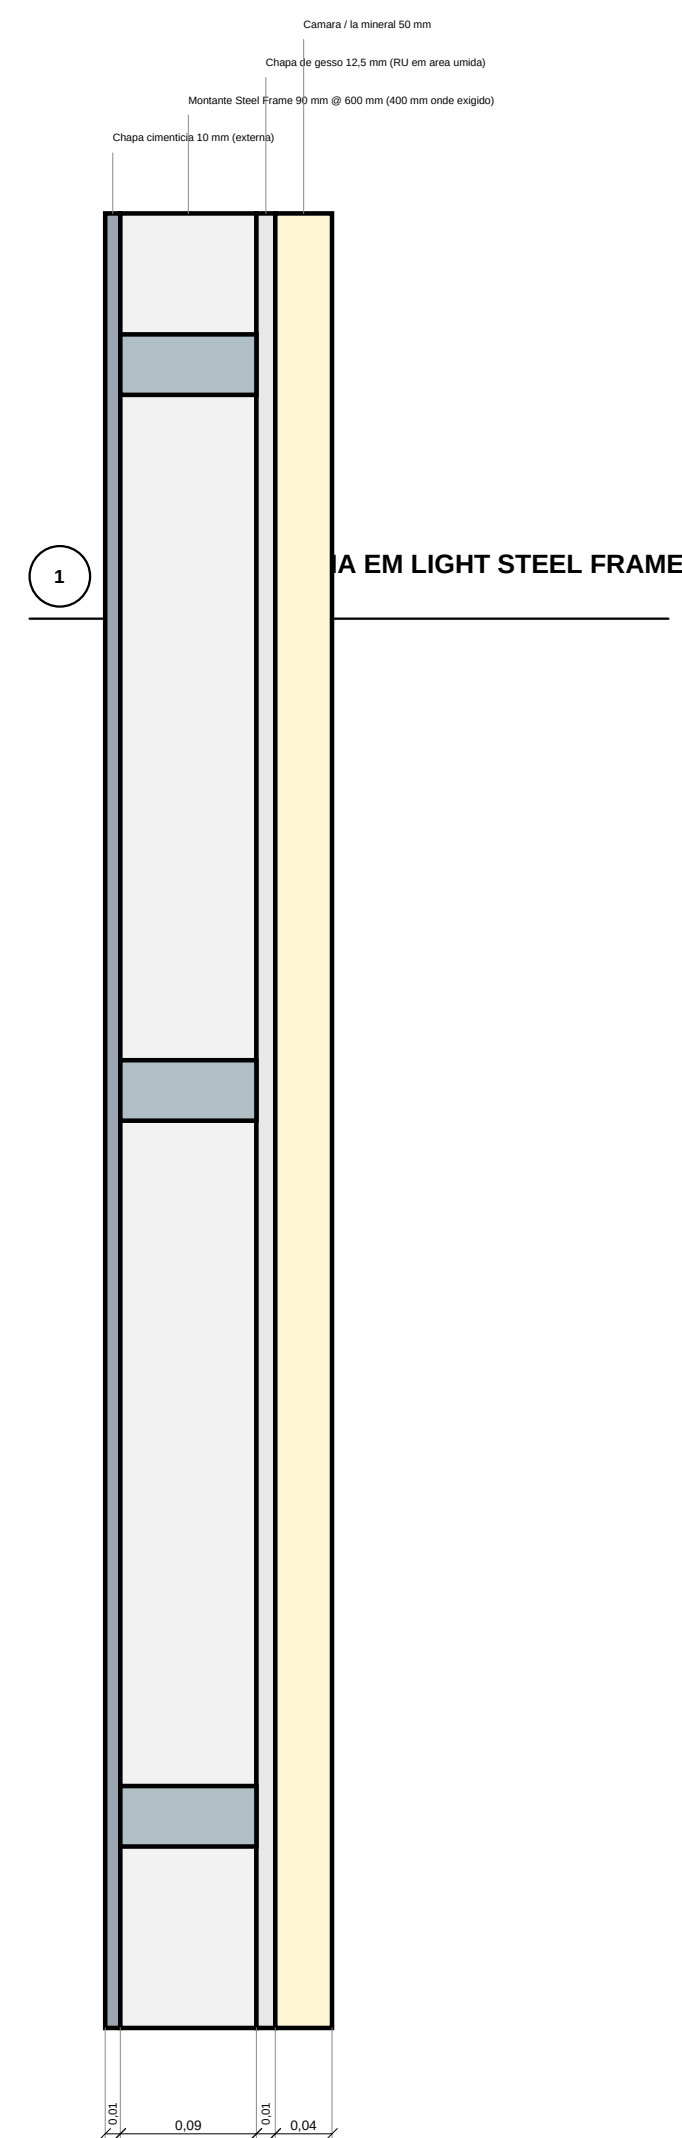

NOTAS

- Detalhes de estudo — não liberados para fabricação ou corte (sem nesting codificado).
- Parede externa consolidada em 150 mm; divisória interna em 100 mm (H).
- Escada reconciliar com estrutura, guarda-corpo e espessura de acabamento antes de definitiva.

PROJETO PORTO REAL RESIDENCIA UNIFAMILIAR (MANAUS - AM) (SOL 7 ANTERA 20)			
PROJETO ARQUITETONICO DETALHES CONSTRUTIVOS AMPLIADOS			
BASE GEOMETRICA Lista Consolidada pos-R22 (gratuitos) UNIDADE MESTRE - 044	ESCALA indicada FORMATO A1 MALHA 600/600/350	EMISSAO ESTUDO PRELIMINAR R21 NOVO LIBERACAO PARA OBRA SEM ART / RBT	FRANQUIA 10 de 55 REV R21