
**VERIFICACAO URBANISTICA (H)**

PARAMETRO	PROYECTO	LIMITE	
Tasa de ocupación	33,33 %	max 50 %	OK
Coef. de aprovechamiento	0,372	max 1,00	OK
Cobertura	2 pavimentos	max 4	OK
Recor. frontal	7200 mm	confirma 5500 p/s	OK
Recor. lateral est.	2400 mm	será pasado en diseño	OK
Flecha técnica de	8000 mm	max 5000 mm	OK
Recor. de fondo	13000 mm	max 5000 mm	OK

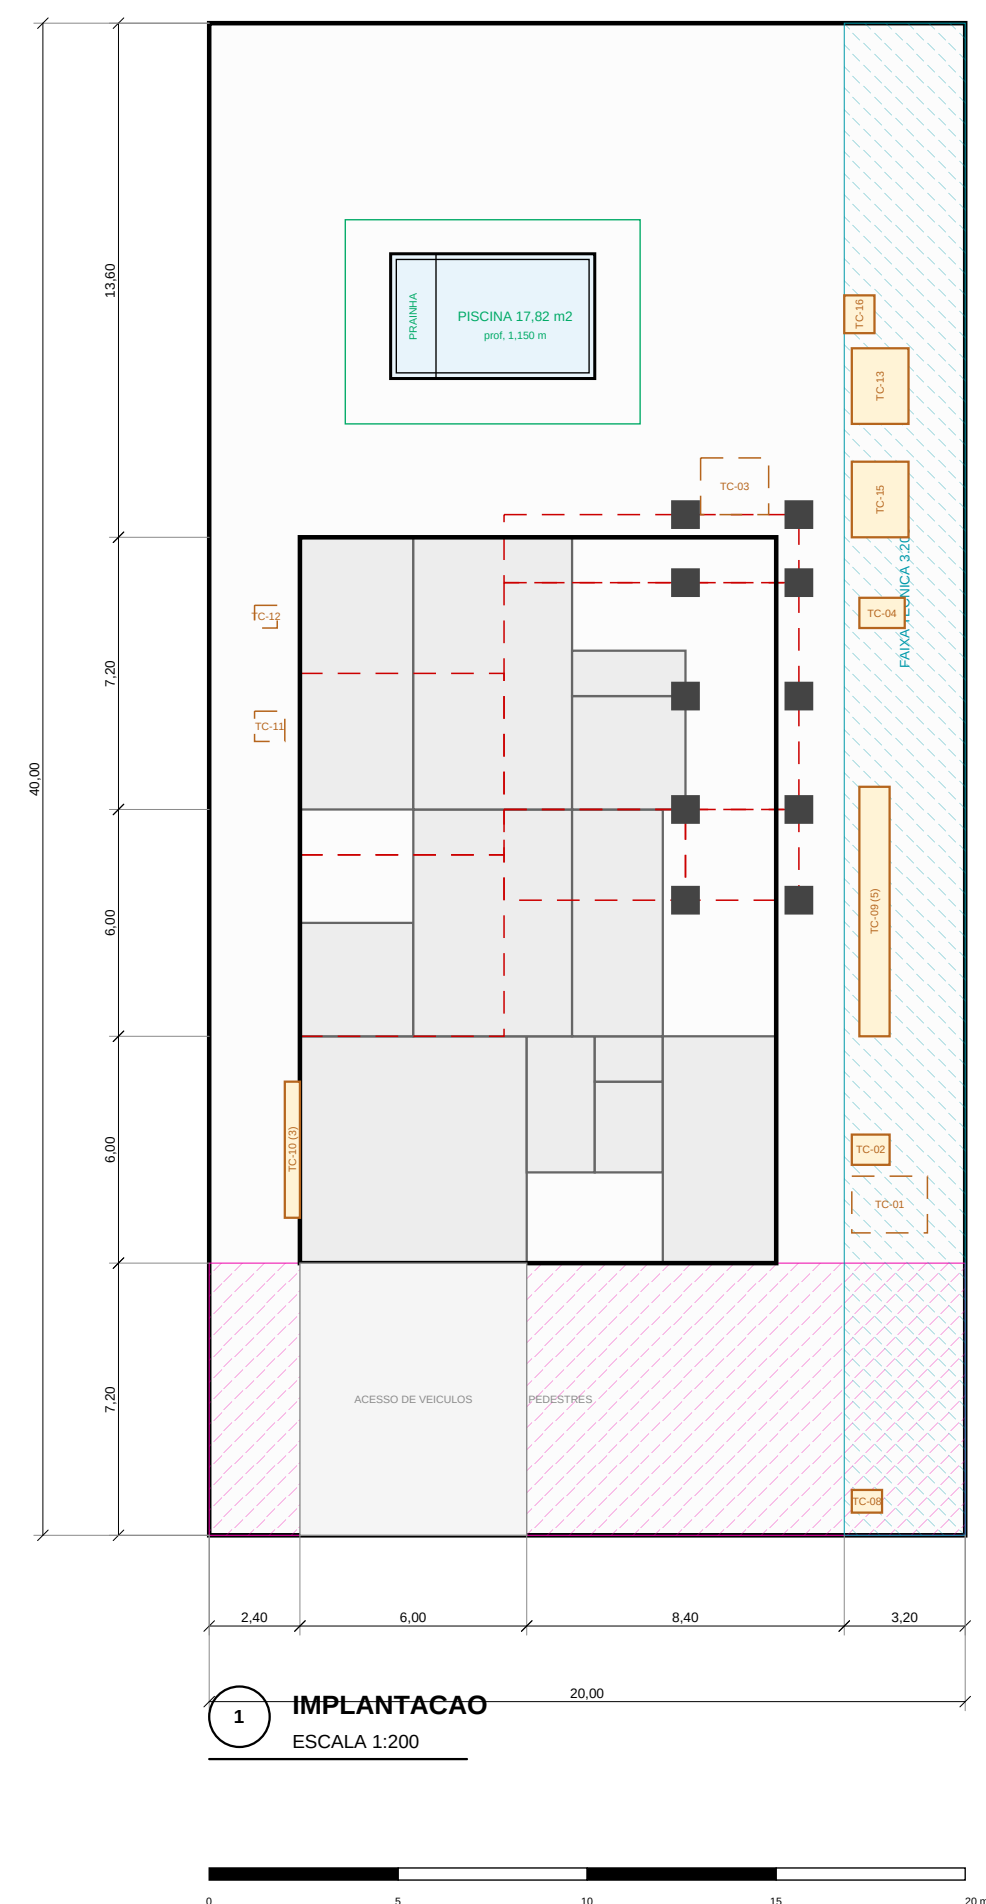

NOTAS

- Lote 20.000 x 40.000 mm = 800.00 m².
- Recuos: frontal 7.200 / lateral esq. 2.400 / faixa técnica dir. 3.200 / fundo 13.600 mm.
- Parâmetros de SU05 Tarumã/Tarumã-Açu são hipóteses (H) – pendente certidão de uso do solo.
- Sers muro frontal; muros laterais e de fundo h = 2.200 mm.

PROJETO PORTO REAL

RESIDENCIA UNIFAMILIAR | MANAUS - AM | SU16 TARRUMA (H)

IMPLANTACAO E SITUACAO

BASE GEOMÉTRICA	ESCALA	EMISSÃO	PROPOSTA
Lista Consolidada	1:200	ESTUDO PRELIMINAR R-8	01
pro-R22 (previável)	FORMATO A1	NÃO LIBERANDO PARA OBRA	
ENDEREÇO: MESTRE JOÃO	MAQUETA: 000/000/000	SERVIÇO: 1/001	DE 15 REV. R-8