


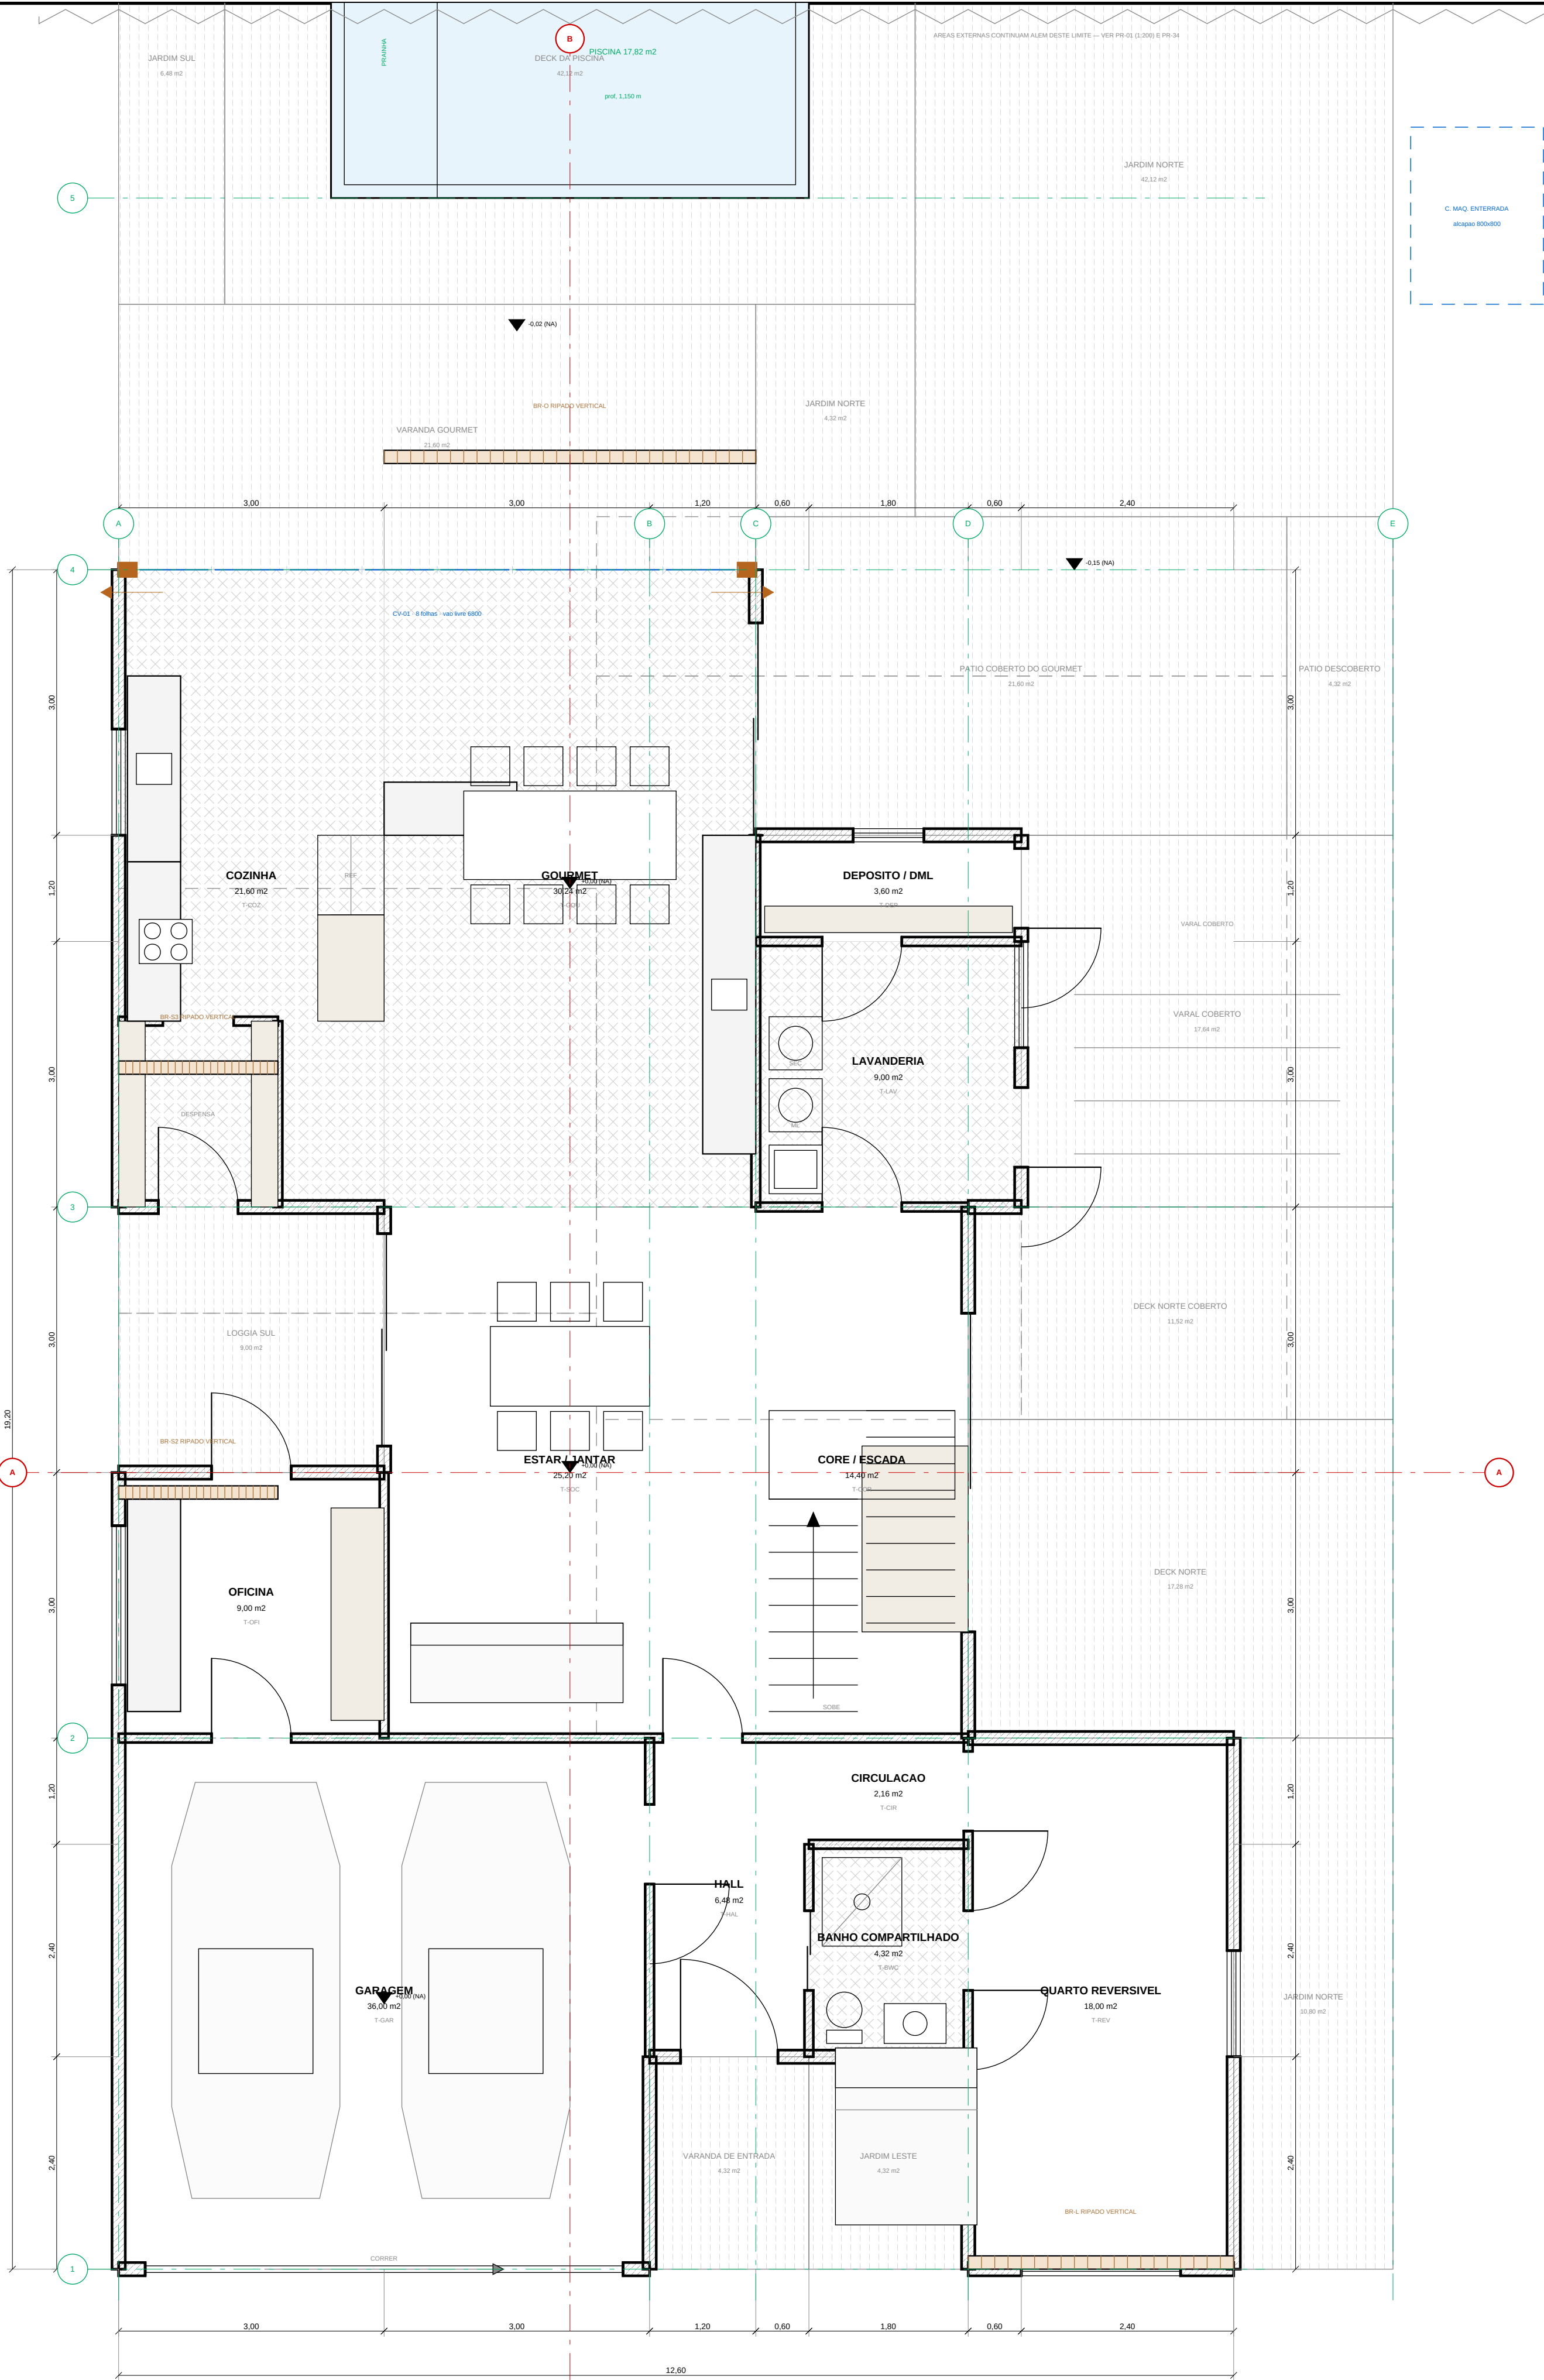

1 PAVIMENTO TERREO
ESCALA 1:50





QUADRO DE ÁREAS — PAVIMENTO TERREO			
COD	AMBIENTE	MÓDULO (mm)	ÁREA (m²)
T-GAR	CARACEM	600x600	36,00
T-HAL	HALL	1800x3000	5,40
T-BNC	BANHO COMPARTILHADO	1800x2400	4,32
T-CIR	CIRCULACAO	1800x1200	2,16
T-REV	QUARTO REVERSIVEL	3000x3000	9,00
T-OFI	OFICINA	3000x3000	9,00
T-SOC	ESTAR / JANTAR	4500x6000	27,00
T-COR	CORE / ESCADA	2400x6000	14,40
T-COZ	COZINHA	3000x2700	21,87
T-GOU	GOURMET	4500x2700	36,24
T-LAV	LAVANDERIA	3000x3000	9,00
T-DEP	DEPOSITO / DML	3000x1200	3,60
TOTAL FECHADO			198,09
T-VAR	VARANDA DE ENTRADA (aberta)	1800x2400	4,32
T-J-E	JARDIM LESTE (aberto)	1800x2400	4,32
T-J-N	JARDIM NORTE (aberto)	1800x3000	5,40
T-LOG	LOGGIA SUL (aberto)	3000x3000	9,00
T-DML	DECK NORTE (aberto)	4800x3000	14,40
T-DNC	DECK NORTE COBERTO (aberto)	4800x2400	11,52
T-VAR	VARAL COBERTO (aberto)	4500x4500	20,25
T-PAT	PATIO COBERTO DO GOURMET (aberto)	6000x3000	18,00
T-PAT	PATIO DESCOBERTO (aberto)	1200x3000	3,60
T-VAR	VARANDA GOURMET (aberto)	7500x3000	22,50
T-DEP	DECK DA PISCINA (aberto)	7800x4500	35,10
T-J-S	JARDIM SUL (aberto)	1200x4500	5,40
T-J-N	JARDIM NORTE (aberto)	1800x2400	4,32
T-J-E	JARDIM LESTE (aberto)	5400x7800	42,12
T-PAT	JARDIM DE FUNDO (aberto)	14400x4800	69,12

REF	VALOR (mm)	QUANT.	QTD.	TIPO
CVE1	7000x2000	0	1	CORTINA DE VIDRO vertical, 0 folha de 900 mm
J01	1200x1200	1200	3	porta de banheiro, alumínio
J04	800x800	1800	2	porta de banheiro, alumínio
J05	1800x1200	1200	2	porta de banheiro, alumínio
P01	1100x800	0	1	porta principal, alta espacia
P02	900x1200	0	4	porta interna (diversas aberturas)
P04	800x1200	0	7	porta de serviço, resistente a umidade
P05	900x1200	0	1	porta de COZINHA — ver área de varanda
P06	5400x2400	0	1	porta de correr, alumínio espacia
P07	3000x2400	0	1	varal social paralelo
P08	3000x2400	0	2	porta blindada de vidro (diversas aberturas) — ver

LEGENDA E CONVENCOES (NBR 6492 / 8403)

- Elemento seccionado pelo plano de corte (0 = 1,50 m)
- Área vista / folha de esquadria
- Mobiliário fixo, equipamento e simbologia
- Propriedade do pavimento superior e da cobertura
- Eixo modular e linha de corte
- Linha de vista e linha auxiliar

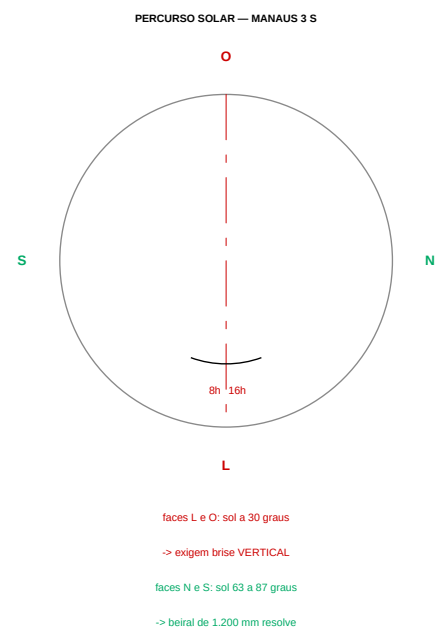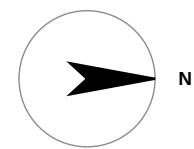

- NOTAS
- Dimensiones em milímetros; cotas de nível em metros.
 - Malha modular 600 mm; cotas elevadas a 600 mm.
 - Pavimento externo 120 mm / drenagem interna 120 mm (P).
 - Mobiliário fixo indica pontos de água e energia (NBR 6492).

PROJETO PORTO REAL

RESIDENCIA UNIFAMILIAR (MANAUS - AM) | SOUZA TAVARES

PROJETO ARQUITETONICO

PLANTA DE LAYOUT — PAVIMENTO TERREO

BASE GEOMETRICA Linha Consolidada PLOT (PLOT) (PLOT) UNIDADE: METRO (m)	ESCALA 1:50 FORMATO: A1 MATERIAL: 600x600 (mm)	EXIBICAO ESTUDIO PRELIMINAR RMB Linha Consolidada PARA ORCA SEM ART / RMB	PROJETO 04 06/25 REV RMB
--	---	--	--------------------------------