
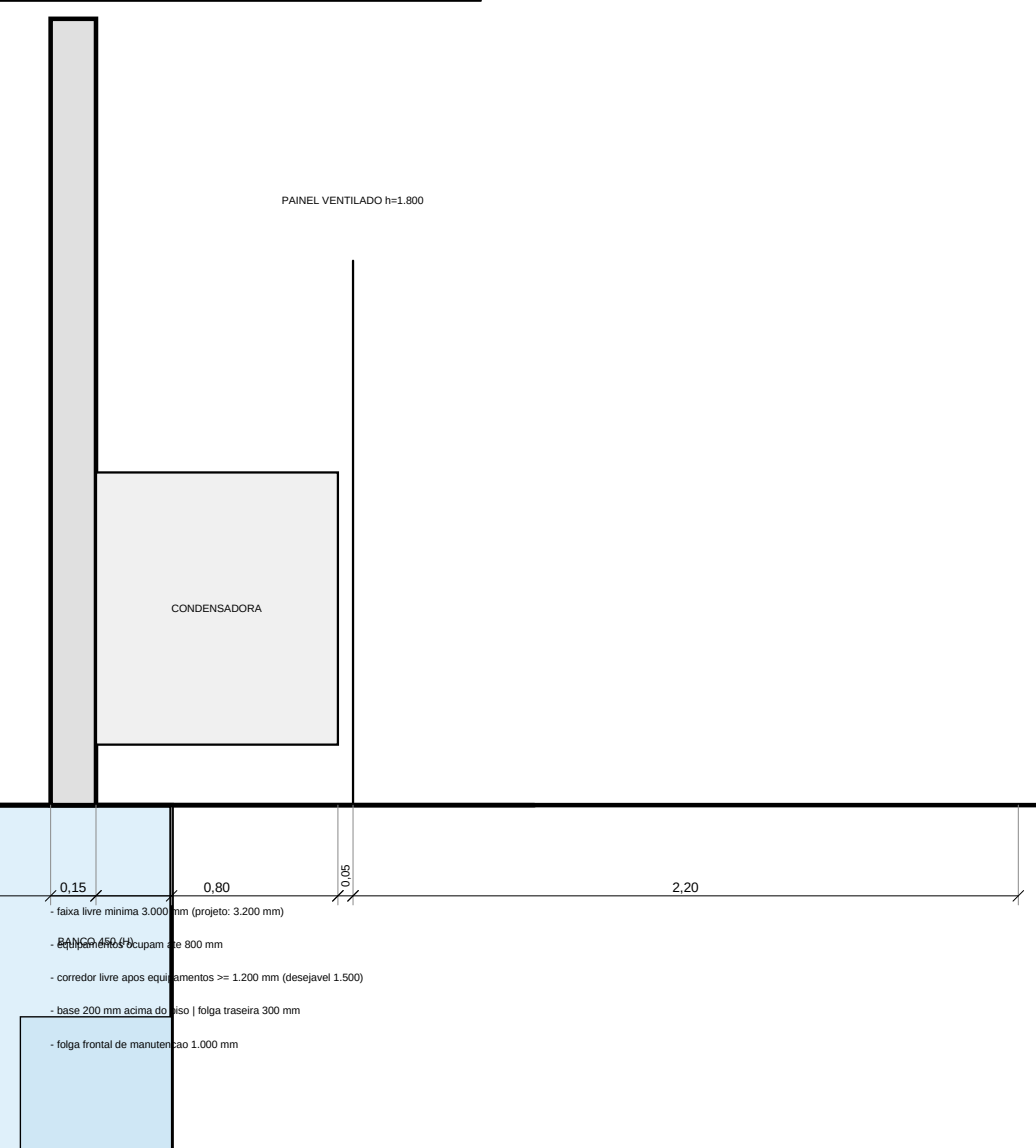


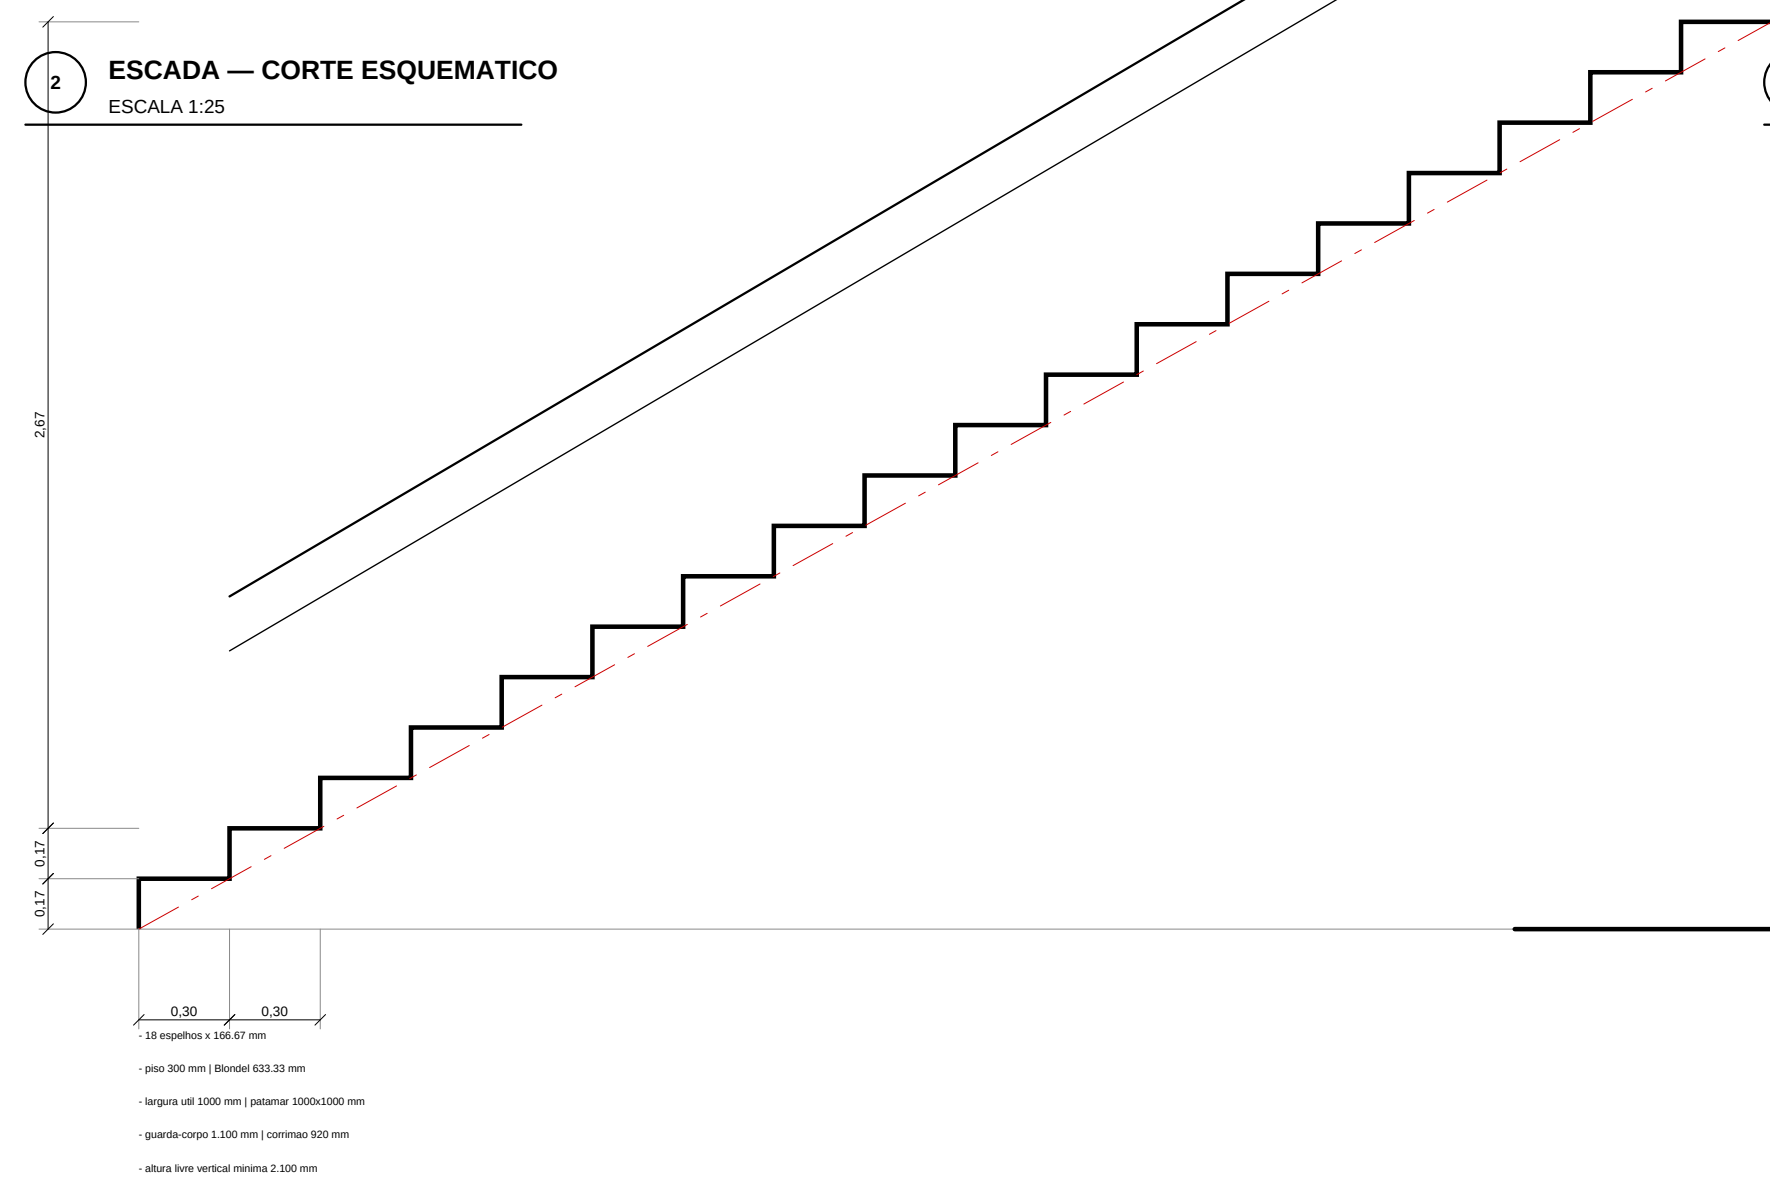

- Detalhes de estudo — não liberados para fabricação ou corte (sem nesting codificado).
- Parede externa consolidada em 150 mm; divisória interna em 100 mm (tô).
- Escada reconciliar com estrutura, guarda-corpo e espessura de acabamento antes de definitiva.

PROJETO PORTO REAL RESIDENCIA UNIFAMILIAR (MANAUS - AM) (SOLTA TAMBORA 05)			
PROJETO ARQUITETONICO DETALHES CONSTRUTIVOS AMPLIADOS			
BASE GEOMETRICA Linha Consolidada pos-022 (provisoria) USO:DE MESTRE - AM	ESCALA indicada FORMATO A1 MANUS 600/900/300	ENTRADA ESTUDIO PRELIMINAR R-08 NÃO LIBERADO PARA COPIA SEM ART. / IMPR	FUNÇÃO 10 05.10.2014 14:42