




-  luminária embuída, 3.000 K, IRC 90
-  alçapão técnico 600 x 600 mm
-  forro absorvente (alfa 0,70)

FORROS POR AMBIENTE

AMBIENTE	SOLUÇÃO	ÁREA	NOTA
T-03A	forro absorvente (α=0,70) aparente no por	36,24	único ponto que demanda a instalação de 3,20 x por
T-03C	gesso fio + cortina e tapetes	25,20	abscisão entre do mobiliário, forro técnico aqui for
T-03D	gesso fio aparente	13,00	superfície de fácil limpeza sem necessidade de for
S-03D	gesso fio + la mineral sobre o for	25,80	la sobre o forro técnica tudo de ruído no poro P
S-03E	gesso fio + la mineral sobre o for	25,80	idem
S-04D	gesso fio + la mineral sobre o for	25,80	idem
T-04A	sem forro (estrutura aparente)	36,00	ambiente semi-escuro, acústica não for
T-04B	sem forro (estrutura aparente)	9,00	idem
T-04C	sem forro (estrutura aparente)	3,00	idem

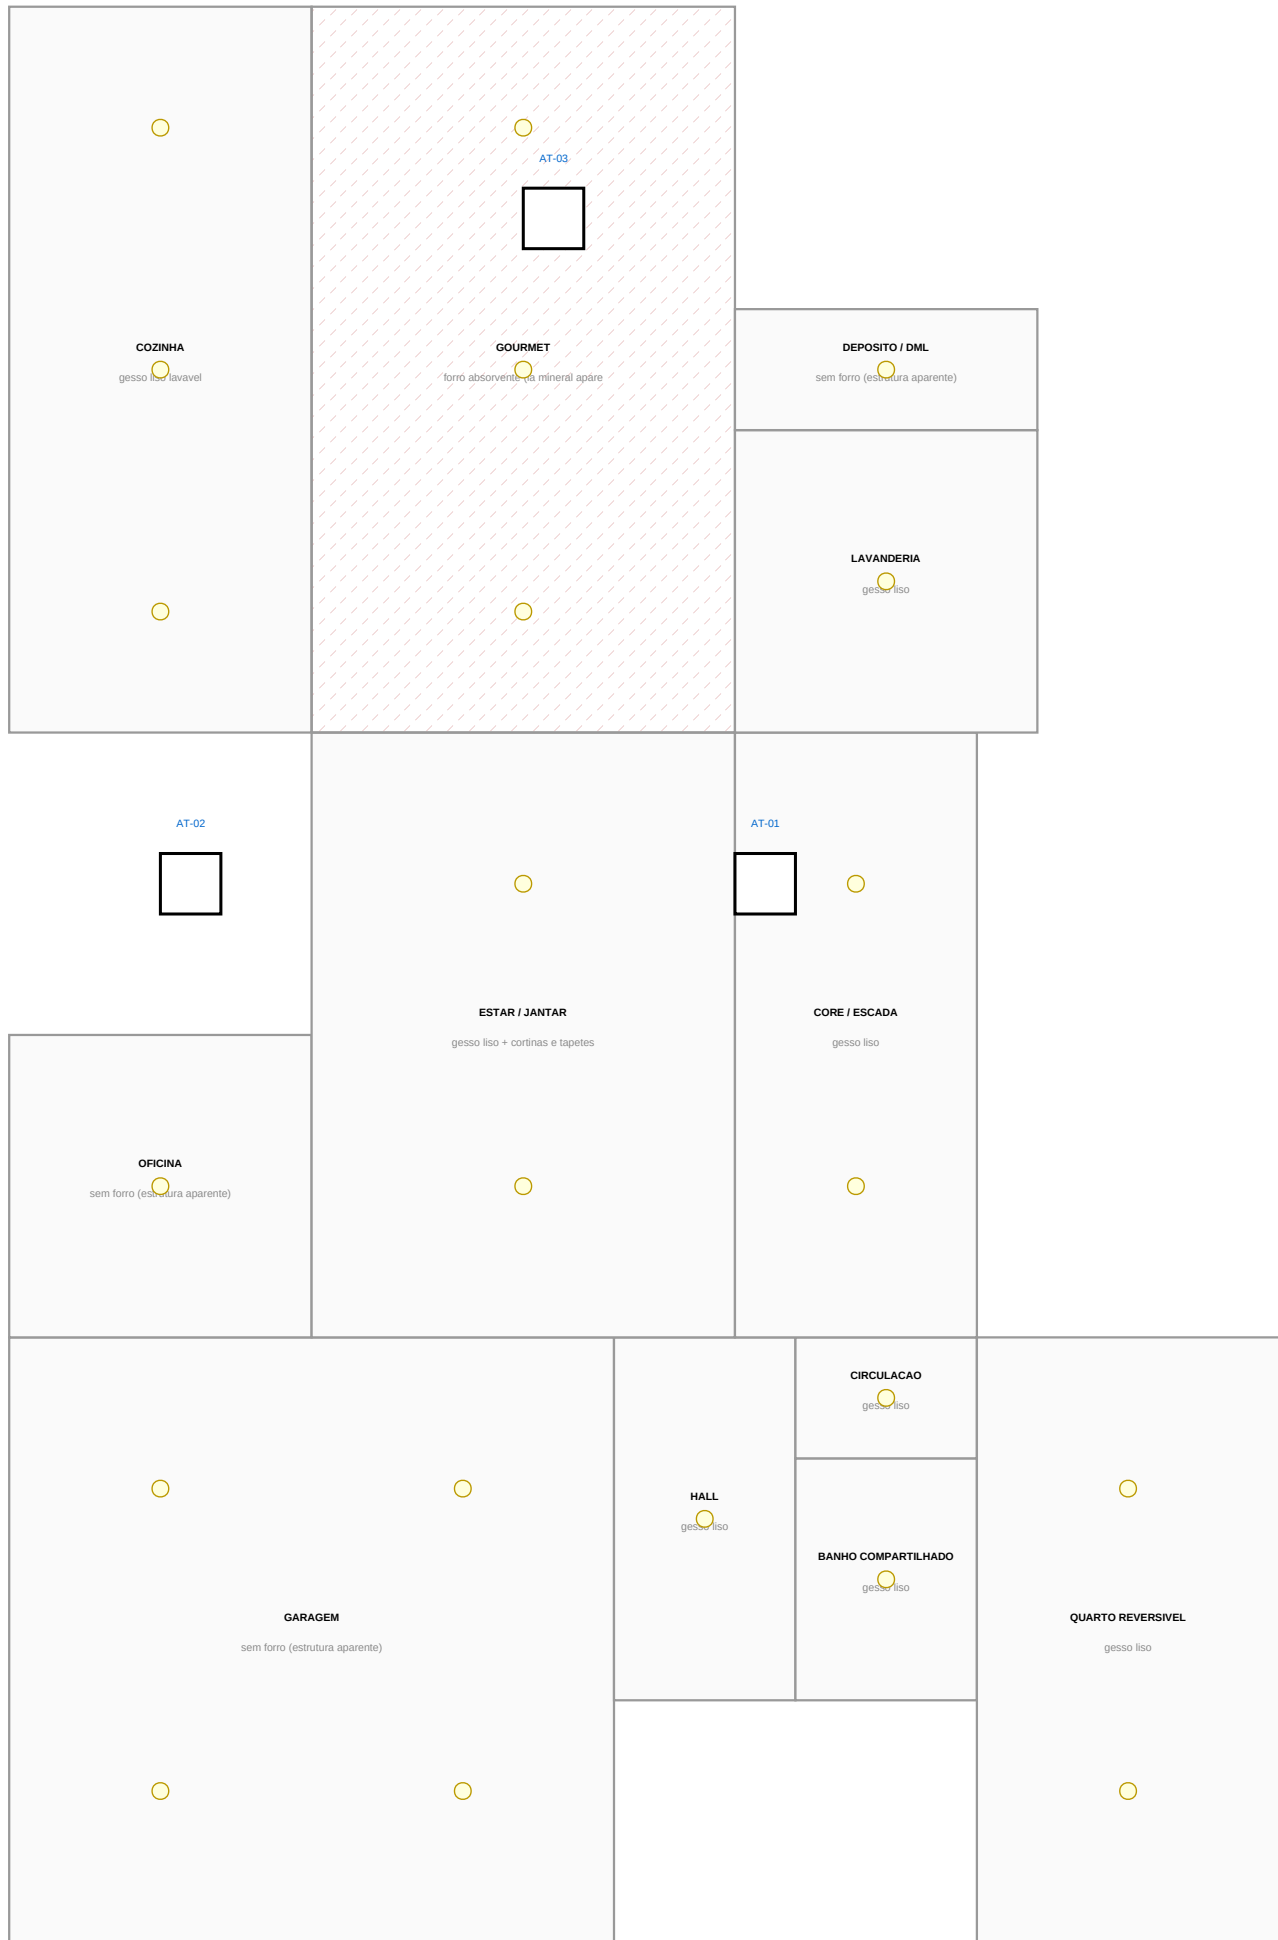

1 FORRO REFLETIDO — TERREO
ESCALA 1:75

- NOTAS
- * Planta refletida: vista do forro projetada no plano horizontal.
 - * Forro absorvente apenas no gourmet — único ponto com necessidade crítica.
 - * Alçapões técnicos de 600 x 600 mm, passando de cobertura de 600 mm.
 - * Luminárias para 3.000 K, IRC mínimo 90.

PROJETO PORTO REAL

RESIDÊNCIA UNIFAMILIAR (MANAUS - AM) | 2024 | TATIANA P.

PROJETO ARQUITETÔNICO

PLANTA DE FORRO E ILUMINAÇÃO

BASE GEOMÉTRICA Linha Consolidada ISO 8582 (previsão) UNIDADE: METROS - MM	ESCALA 1:75 FORMATO A1 MILHA 455/500/500	EMISSÃO ESTUDO PRELIMINAR R&B LIVRO LIBERADO PARA ORÇ SEM ART / RNT	PROVA 16 06-25 REV 04E
---	---	--	------------------------------