



QUANTITATIVO DE PAINÉIS E MONTANTES

FAMÍLIA	PAINÉIS	MONTANTES	MT de perfil	COMPOSIÇÃO
PA-1	12	45	127,4	dupla chapa 12,5 + montante 45 x 14 x 10 + dupla chapa 12,5
PA-2	1	6	15,6	dupla chapa 12,5 + perfil isolante + montante 70 x 14 x 30
PE-1	30	283	883,8	Unimold 32 x 30 x 30 (SD anel) + montante 30 x 14 x 30 +
PA-3	6	31	30,6	perfil 60 12,5 + montante 30 x 14 x 30 + perfil 12,5 + rebordo
PA-4	4	22	57,2	perfil 12,5 + montante 70 x 14 x 30 + perfil 12,5
TOTAL	73	371	964,6	

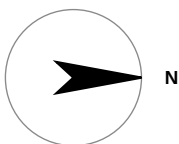

EXTRATO DA LISTA DE PAINÉIS (26 de 73)

CODIGO	FAMÍLIA	LARGO (mm)	ALT (mm)	MONT.	PRV
PT-001	PE-1	3000	2000	6	T
PT-002	PE-1	3000	2000	6	T
PT-003	PE-1	3000	2000	6	T
PT-004	PE-1	3000	2000	7	T
PT-005	PE-1	3000	2000	7	T
PT-006	PE-1	3000	2000	6	T
PT-007	PE-1	3000	2000	6	T
PT-008	PA-1	3000	2000	6	T
PT-009	PE-1	3000	2000	6	T
PT-010	PE-1	3000	2000	6	T
PT-011	PE-1	3000	2000	6	T
PT-012	PA-2	3000	2000	6	T
PT-013	PE-1	3000	2000	6	T
PT-014	PA-1	3000	2000	6	T
PT-015	PE-1	2100	2000	4	T
PT-016	PE-1	2100	2000	4	T
PT-017	PE-1	2400	2000	5	T
PT-018	PA-1	3000	2000	7	T
PT-019	PE-1	1800	2000	4	T
PT-020	PA-1	1200	2000	3	T
PT-021	PA-1	3000	2000	6	T
PT-022	PA-1	1200	2000	3	T
PT-023	PE-1	3000	2000	6	T
PT-024	PA-1	3000	2000	6	T
PT-025	PA-1	600	2000	2	T
PT-026	PA-1	2400	2000	6	T

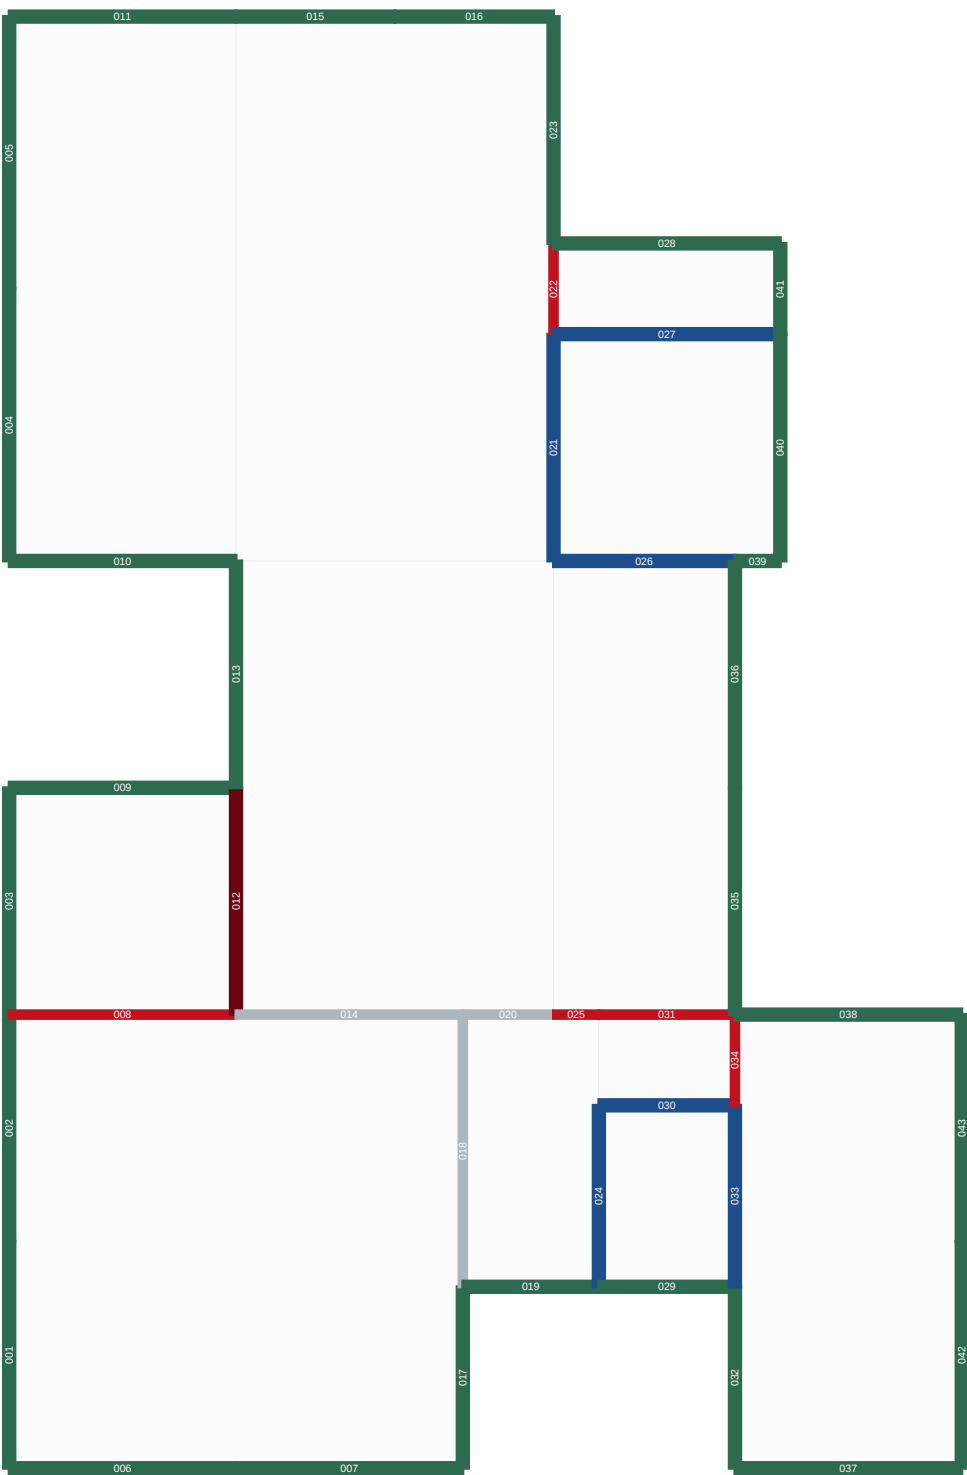

1 PAGINACAO — TERREO
ESCALA 1:100

- NOTAS
- * Painéis limitados a 3000 mm por manuseio e transporte.
 - * Montantes a cada 600 mm, 400 mm onde cabido no revestimento exigido.
 - * Não fixar a peça entre em moldes sem código, largura, altura, espessura, material e revest.
 - * Numeração por pavimento, a família define a composição interna do painel.

PROJETO PORTO REAL

RESIDENCIA UNIFAMILIAR (MANSÃO - AM) | SOUSA TATIANA-PS

PROJETO ARQUITETONICO

PAGINACAO DE PAINÉIS — LIGHT STEEL FRAME

BASE GEOMETRICA Lista Consolidada em PDF (previsão) UNIDADE: METROS - MM	ESCALA 1:100 FORMATO: A1 MÁQUINA: 6050/50000	EMISSÃO ESTUDO PRELIMINAR R31 TUDO LIBERADO PARA OBRA SEM ART / RNT	PROVA 18 06-25 REV R31
--	--	---	-------------------------------------