


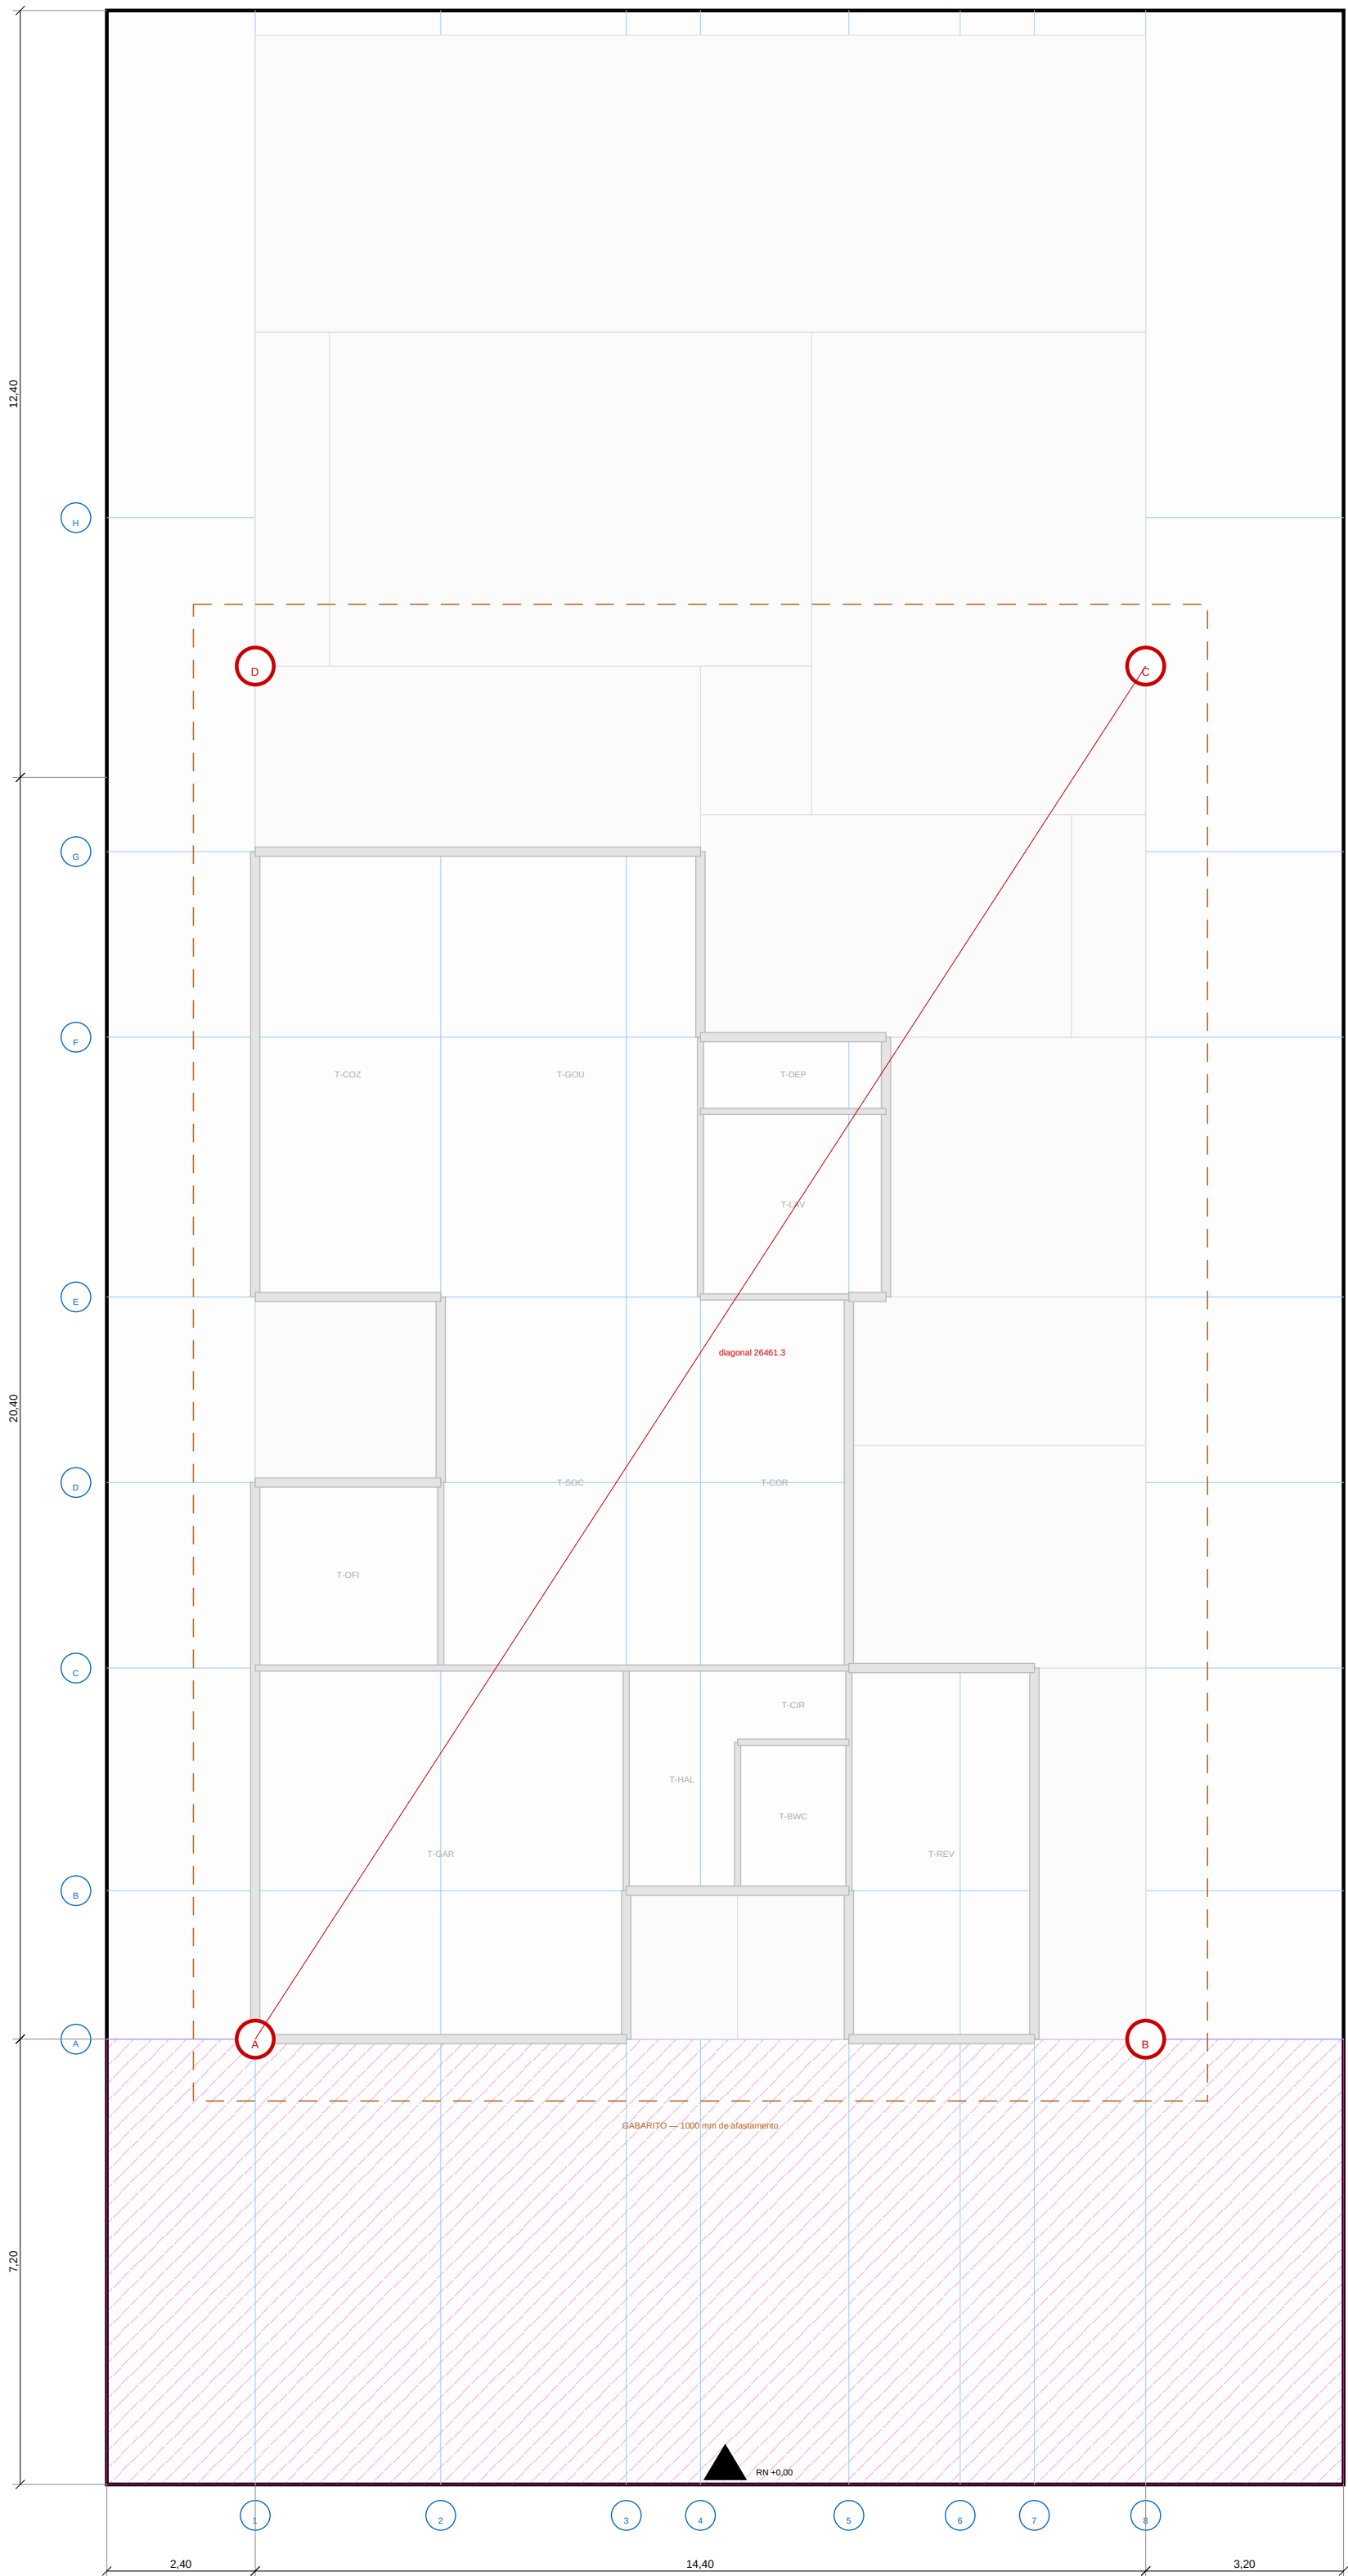

COORDENADAS DOS CANTOS (mm)

| CANTO | X     | Y     | DIVISA SUL | DIVISA NORTE | TESTADA | QUIBO | DIAGONAL |
|-------|-------|-------|------------|--------------|---------|-------|----------|
| A     | 2400  | 7200  | 2400       | 17600        | 7200    | 32800 | 26461,3  |
| B     | 18800 | 7200  | 18800      | 3200         | 7200    | 32800 | 26461,3  |
| C     | 18800 | 28400 | 18800      | 3200         | 28400   | 19600 | 26461,3  |
| D     | 2400  | 28400 | 2400       | 17600        | 28400   | 19600 | 26461,3  |

PROCEDIMENTO DE LOCAÇÃO

| # | PASSO                                                                     | CRITÉRIO DE ACEITE                                    |
|---|---------------------------------------------------------------------------|-------------------------------------------------------|
| 1 | Conferir as divisões com o material de mão de obra                        | divergência acima de 10 mm interromper a locação      |
| 2 | Instalar o RMC marca de concreto 100 x 200 x 100 mm, fora da área de obra | fora da área de obra                                  |
| 3 | Montar o gabarito a 1000 mm do cantoneiro                                 | perguntar 75 x 75 a tubos 20 x 100                    |
| 4 | Marcar os eixos X (L) e Y (L) a 10 m no gabarito                          | linha coordenada múltipla de 200 mm                   |
| 5 | Cotar cada canto dos QUADs dividos                                        | verificar em cada canto, erro de cada lado            |
| 6 | Conferir a diagonal A-C                                                   | 26461,3 mm com tolerância de 10 mm                    |
| 7 | Conferir o quadrado por 3-4-5 em cada canto                               | antes de qualquer concretagem                         |
| 8 | Registrar em ata com foto e modelo                                        | gabarito continuo nos dois lados da obra, conferência |

EIXOS MODULARES

| DIREÇÃO       | VALORES (mm)                                                |
|---------------|-------------------------------------------------------------|
| X (L) e Y (L) | 2400 - 5400 - 8400 - 9600 - 12600 - 13800 - 15000 - 18000   |
| Y (L) e X (L) | 7200 - 9600 - 13200 - 14200 - 15000 - 28400 - 29400 - 32800 |
| Módulo        | principal 600 mm - submódulo 300 mm                         |
| Origem        | canto frontal esquerdo da base                              |
| Unidade       | módulo                                                      |

NOTAS

- Locação é o único documento em que o erro não tem contorno técnico: a casa sai do lugar.
- Cada canto é cotado dos QUADs dividos, nunca em cadeia acumulada — erro de cadeia soma, erro de referência independente não.
- Conferência obrigatória pela diagonal 26461,3 mm entre A e C antes de concretar o radier.
- Ata ou livro de locação, elaborado no momento da locação, com foto e modelo.

PROJETO PORTO REAL

RESIDÊNCIA UNIFAMILIAR (MANSÃO - AM) | SOBR TATIANA-PS

PROJETO ARQUITETÔNICO

LOCAÇÃO DE OBRA E GABARITO

|                                                                                   |                                                             |                                                                               |                                     |
|-----------------------------------------------------------------------------------|-------------------------------------------------------------|-------------------------------------------------------------------------------|-------------------------------------|
| BASE GEOMÉTRICA<br>Linha Consolidada<br>Projeto (previsão)<br>UNIDADE: METRO - MM | ESCALA<br><b>1:100</b><br>FORMATO A1<br>MÁQUILA 605/500/300 | EMISSÃO<br>ESTUDO PRELIMINAR R31<br>LIVRO LIBERADO PARA OBRA<br>SEM ART / RNT | PROVA<br><b>31</b><br>06-25 REV R31 |
|-----------------------------------------------------------------------------------|-------------------------------------------------------------|-------------------------------------------------------------------------------|-------------------------------------|