




luminária embuída, 3.000 K, IRC 90

afcapso técnico 600 x 600 mm

forro absorvente (alfa 0,70)

FORROS POR AMBIENTE

AMBIENTE	SOLUÇÃO	ÁREA	NOTAS
T.CC1	forro absorvente (α=0,70) aplicado ao teto	36,24	único ponto que demanda a instalação de 3,20 x 3,20 x 60
T.BC2	gesso liso + cantoneira e lapelas	25,20	abertura entre as molduras, forro branco aqui forro
T.CC2	gesso liso branco	18,00	superfície de fácil limpeza sem necessidade de pintura
S.BC2	gesso liso + la mineral sobre o forro	25,80	la sobre o forro branco tudo de 2,00 x 2,00 x 60
S.BC3	gesso liso + la mineral sobre o forro	25,80	idem
S.BC4	gesso liso + la mineral sobre o forro	25,80	idem
T.GAR	sem forro (estrutura aparente)	36,00	ambiente semi-escuro, acústica não forrada
T.OP1	sem forro (estrutura aparente)	9,00	idem
T.CCP	sem forro (estrutura aparente)	3,00	idem

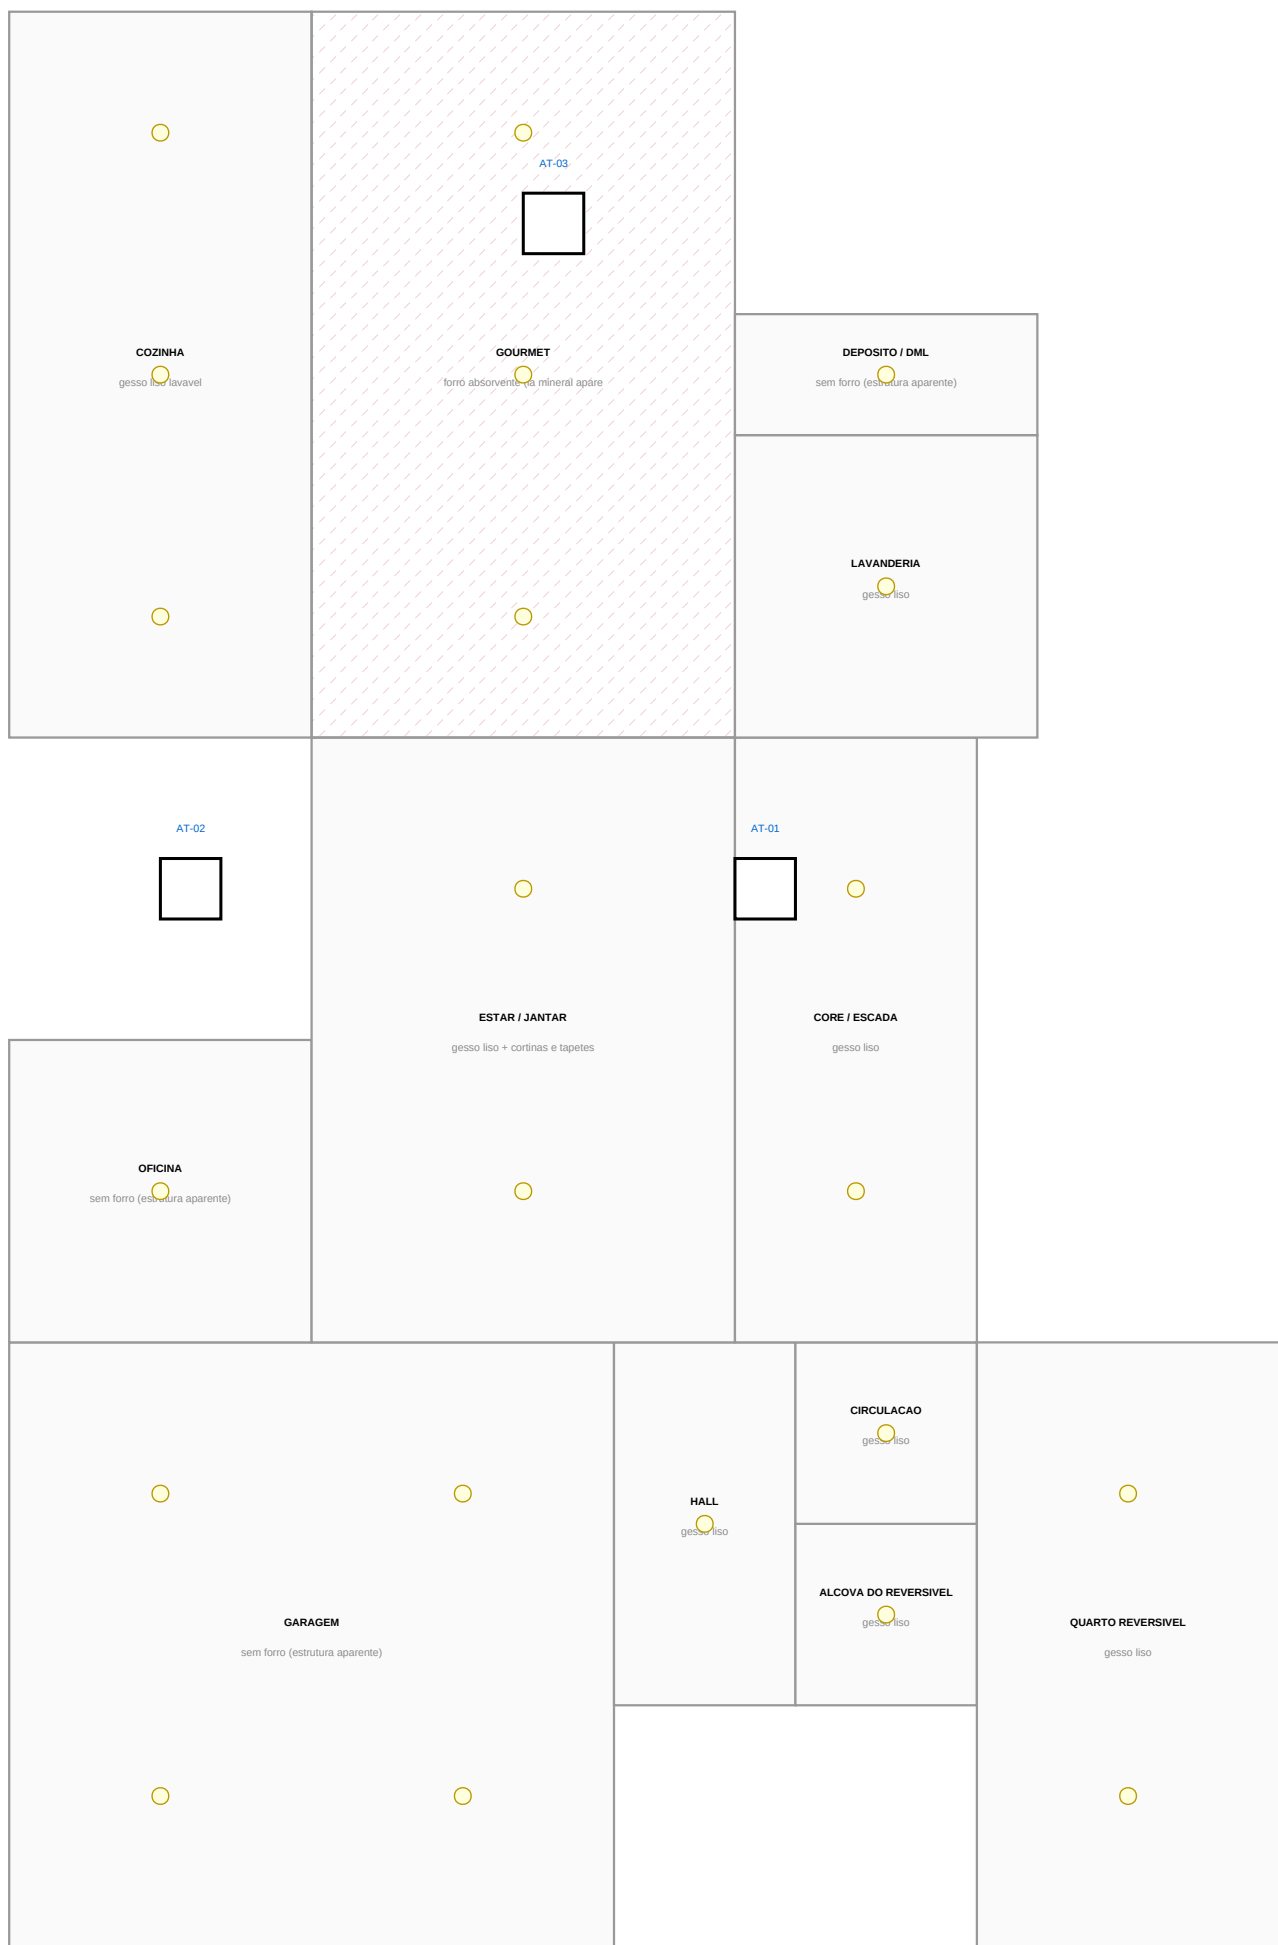

1 FORRO REFLETIDO — TERREO
ESCALA 1:75

NOTAS

- * Planta refletida: vista do forro projetada no plano horizontal.
- * Forro absorvente apenas no gourmet — único ponto com necessidade crítica.
- * Alcapso técnico de 600 x 600 mm, passando de cobertura de 600 mm.
- * Luminária geral 3.000 K, IRC máximo 90.

PROJETO PORTO REAL

RESIDÊNCIA UNIFAMILIAR (MANSÃO - AM) | SOBR TATIANA-PS

PROJETO ARQUITETÔNICO

PLANTA DE FORRO E ILUMINAÇÃO

BASE GEOMÉTRICA Linha Consolidada ISO 8529 (previável) UNIDADE: METROS - MM	ESCALA 1:75 FORMATO A1 MILIMETROS (500/500/500)	EMISSÃO ESTUDO PRELIMINAR RSB LADO LIBERADO PARA DRENAÇÃO SEM ART / RNT	PROVA 16 DE 48 REVISTAS
--	---	--	--------------------------------------