


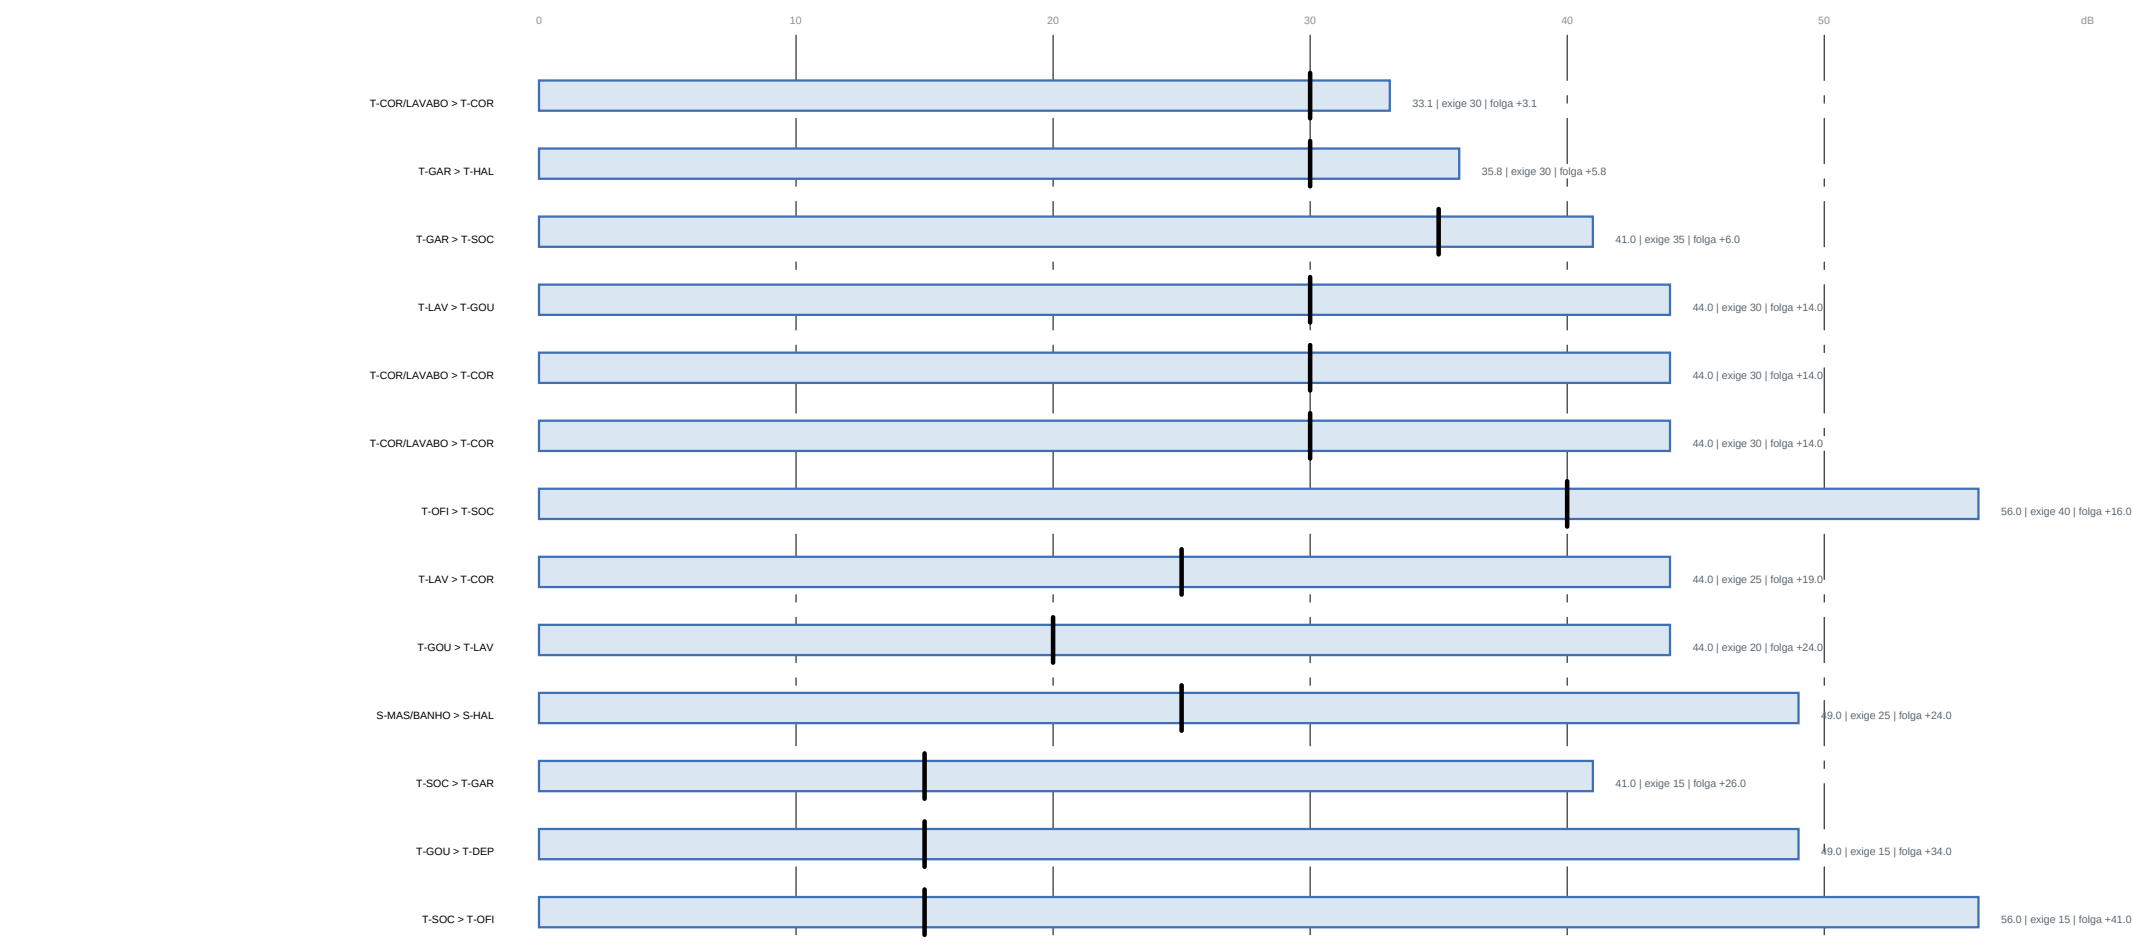

Barra = isolamento obtido; traço vertical = exigência (valor da fonte menos nível do receptor, NBR 15552)

O QUE MUDOU EM R52

ONDE	ANTES	DEPOIS	POR QUE
Banho compartilhado > hall de entrada	porta de correr (Rw 25) — conjunto de 20,2 dB	parede CEGSA, 44 dB	o acesso de volta passou para a circulação
Banho compartilhado > quarto eventual	porta com (Rw 25) — conjunto de 25,5 dB, exigia 25	parede CEGSA, 44 dB	era a por passagem da casa, e não era a saída
Hall > garagem	porta com — 36,9 dB, exigia 30	PDS lajea vedada — 50,9 dB	porta entre garagem e casa tem lajea lajea para ser mudeca
Banho compartilhado > circulação	não havia porta	PDS lajea vedada — 35,7 dB, exigia 25	único acesso do banho, e abria para fora
Bloco do chuveiro	encostado na parede do hall	canto arredondado, toldo e janela alta	consequência da porta nova, a regra dos 900 cm de bloco reaproveita a primeira lavatória

TABELAS ADOTADAS

ITEM	VALOR	FONTE
Fonte: caixa sanitária	75 dB(A)	prática corrente de acústica
Fonte: bloco do chuveiro	70 dB(A)	prática corrente de acústica
Fonte: cozinha e gourmet	70 dB(A)	prática corrente de acústica
Fonte: sala e jantar	70 dB(A)	prática corrente de acústica
Fonte: garagem	70 dB(A)	prática corrente de acústica
Fonte: máquina de lavar e secar	70 dB(A)	prática corrente de acústica
Fonte: oficina	60 dB(A)	prática corrente de acústica
Límite: banho	45 dB(A)	NBR 15552:2017 (circulação e entrada adiabática)
Límite: circulação	45 dB(A)	NBR 15552:2017 (circulação e entrada adiabática)
Límite: cozinha	45 dB(A)	NBR 15552:2017 (circulação e entrada adiabática)
Límite: depósito	55 dB(A)	NBR 15552:2017 (circulação e entrada adiabática)
Límite: dormitório	35 dB(A)	NBR 15552:2017 (circulação e entrada adiabática)
Límite: entrada	45 dB(A)	NBR 15552:2017 (circulação e entrada adiabática)
Límite: estar	45 dB(A)	NBR 15552:2017 (circulação e entrada adiabática)
Límite: garagem	55 dB(A)	NBR 15552:2017 (circulação e entrada adiabática)
Límite: office	45 dB(A)	NBR 15552:2017 (circulação e entrada adiabática)
Límite: oficina	55 dB(A)	NBR 15552:2017 (circulação e entrada adiabática)
Límite: serviço	50 dB(A)	NBR 15552:2017 (circulação e entrada adiabática)
Fonte: acústica	Pin 25 dB	Nota de mercado declarada
Fonte: cozinha	Pin 25 dB	Nota de mercado declarada
Fonte: sala	Pin 25 dB	Nota de mercado declarada
Fonte: depósito	Pin 25 dB	Nota de mercado declarada
Fonte: lajea vedada	Pin 30 dB	Nota de mercado declarada

NOTAS

1 Esta planilha está para o proprietário perguntar o que 100 verificações não sabem responder: quem entra na casa ouve o chuveiro do banheiro da entrada?

2 Ouça. A parede era bloco (Pin 1, Pin 44) e a porta era de correr (Rw 25), o conjunto entregava 20 dB. Em acústica o bloco DOMINA — não se faz média aritmética do isolamento, se soma energia que passa.

3 Isolamento se se exige ENTRE portas. Dentro da file social o ruído não é definido, é o programa.

4 O aditivo igual ao R52 (parâmetros declarados) não é pre-verificação de projeto, não entra no campo da NBR 15575-3.

PROJETO PORTO REAL

RESIDENCIA UNIFAMILIAR (MANSÃO - AM) | SOBR TATIANA-PS

PROJETO ARQUITETONICO

DESEMPENHO ACUSTICO ENTRE AMBIENTES

BASE GEOMETRICA	ESCALA	EMISSAO	PROVA
Lista Consolidada	s/ escala	ESTUDIO PRELIMINAR R52	
Pin R52 (previsão)	FORMATO A1	NAO LIBERADO PARA OBRA	39
UNIDADE MESTRE: AM	MALHA 605000000	SEM ART / RNT	06-48 REVIEW