


VERIFICACAO NBR 9050

ITEM	EXISTIDO	PROJETO	
Vel. livre de porta	800 mm	940 mm (altura de 900)	OK
Circulo de giro 360 graus	1.500 mm	hall, banheiro e quarto	OK
Desnivel sem rampas	até 5 mm	terminos nivelados	OK
Largura de circulação	900 mm	1.800 mm no hall	OK
Barras de apoio	relevo no piso	instaladas no P1 e P10.1	OK
Barras de acesso	altura livre 750 mm	sem barreiras sob a calha	OK
Corrimão e interruptor	600 a 1.000 mm	a definir no detalhe	pendente



FLUXOS — SEPARACAO DE CIRCUITOS

CIRCUITO	PERCURSO	CIRCULO SOCIAL?
Servico	garagem -> oficina -> lavanderia -> cozinha -> despensa	NAO
Social	entrada -> hall -> estar -> gourmet -> alameda -> piscina	—
Intimo Intim	hall -> banheiro compartilhado -> quarto compartilh	NAO
Intimo Superior	hall -> cora -> hall superior -> suíte	NAO
Uso e carga	cozinha -> despensa -> reserv. sal	NAO

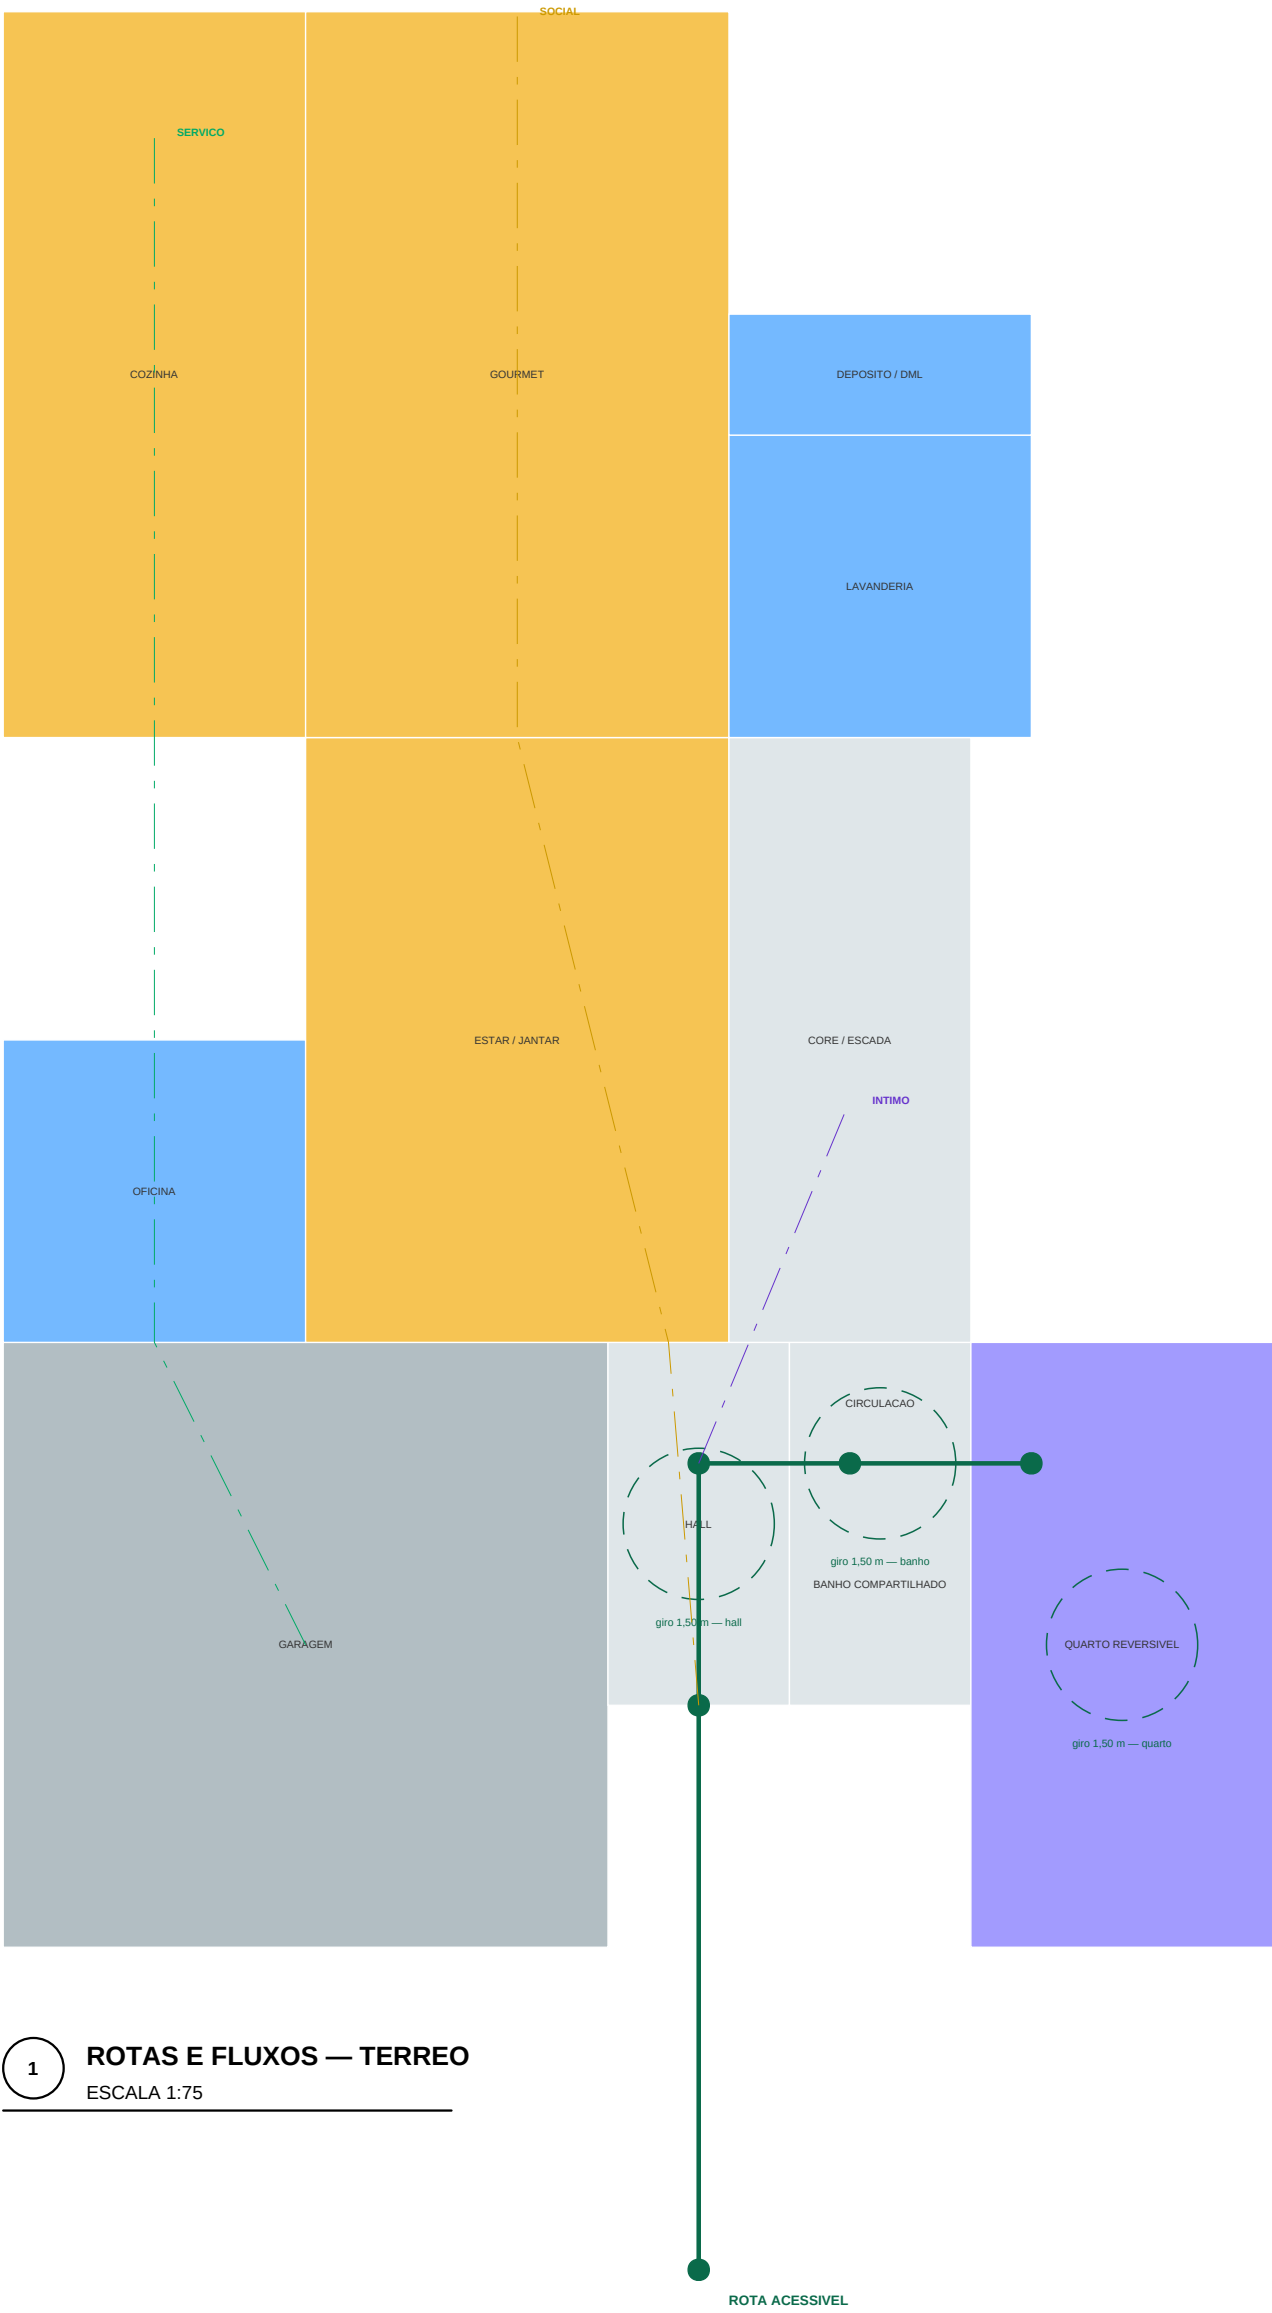

1 ROTAS E FLUXOS — TERREO
ESCALA 1:75

- NOTAS
- * Rota acessível do passeio ao quarto reservado e ao banheiro compartilhado.
 - * Circulo de giro de 1.500 mm verificado nos pontos de manobra.
 - * Porta de correr de 900 mm no banheiro libera a área de manobra.
 - * Reforço para barras de apoio instaladas antes do fechamento das placas.

PROJETO PORTO REAL

RESIDENCIA UNIFAMILIAR (MANAUS - AM) | SOUZA TATIANA-PS

PROJETO ARQUITETONICO

ACESSIBILIDADE E FLUXOS

BASE GEOMETRICA	ESCALA	EMISSAO	PROJETO
União Consolidada	1:75	ESTUDO PRELIMINAR R32	
ps-R32 (previsível)	FORMATO A1	NAO LIBERADO PARA OBRA	
UNIDADE MESTRE: 040	MAQUETA 600/900/300	SEM ART / PRINT	17
			06-25 REV R32