


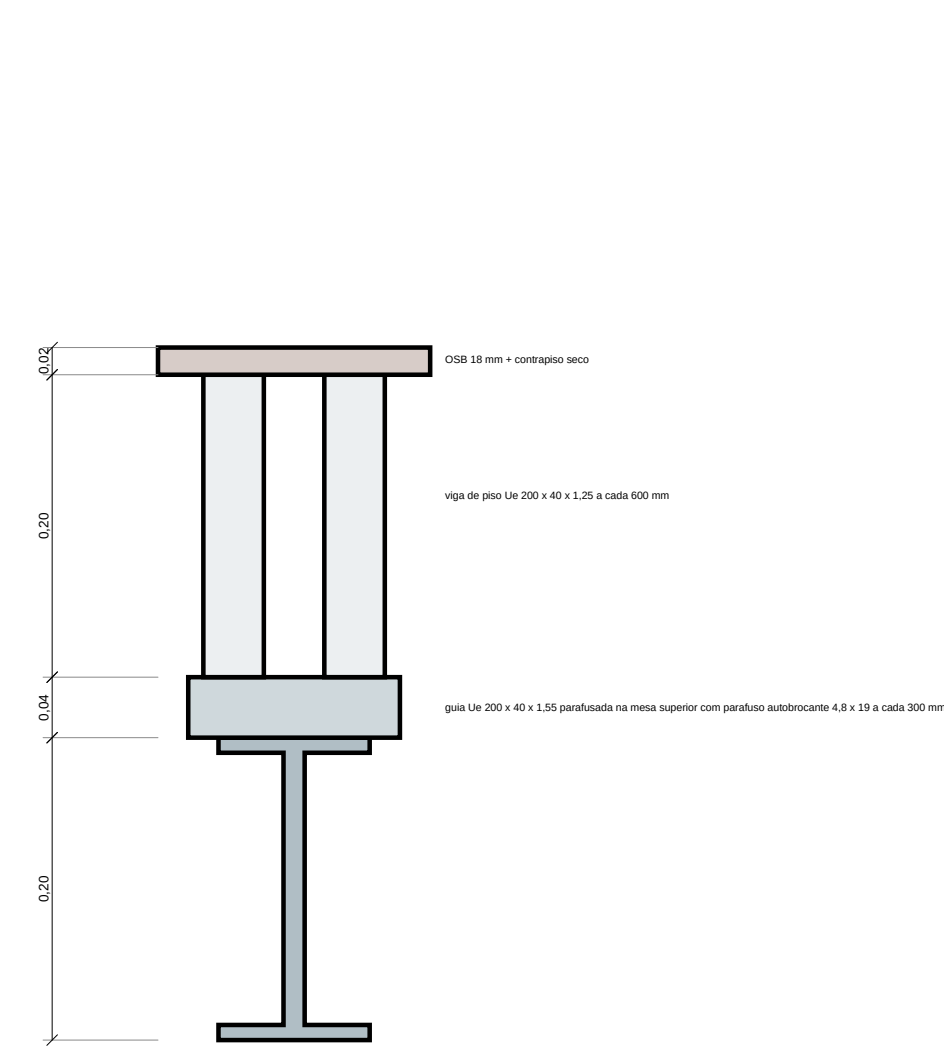

1 APOIO DO VIGAMENTO LSF SOBRE VIGA LAMINADA
ESCALA 1:5


A mesa da viga e ponto nerva e acotada - 0

banda mediana de 5 mm sob a guia corta os dois

da parede, que o montador chama de megalpa

na chapa de apoio, fixação horizontal no topo

Sem esta junta, a flecha da viga deixa de ser

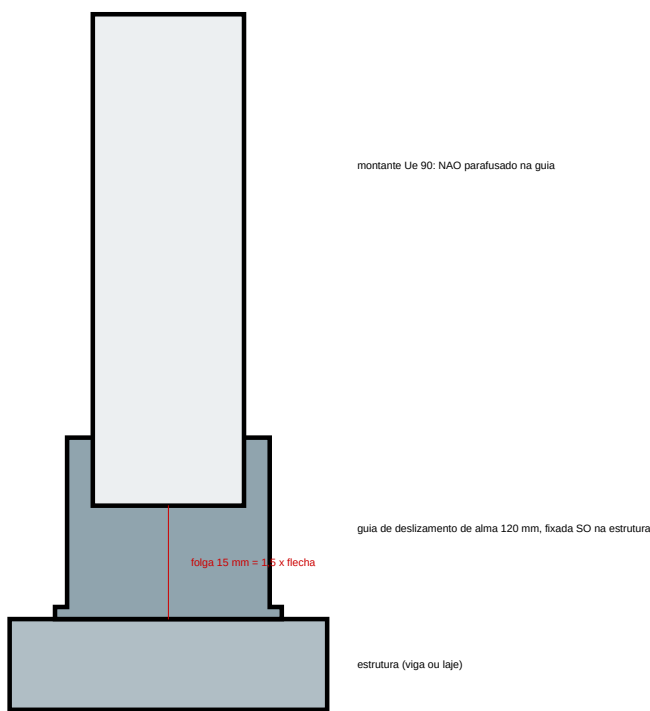

2 JUNTA DE DESLIZAMENTO NO TOPO DA PAREDE
ESCALA 1:5


relevo e ponto nerva de (presta ordem)

perfil e marca de la de flecha no corte do aço

para 200 mm, com montantes duplos horizontalmente

Cada dois acortam, a parede engrossa localmente

O pilar de 300 mm NAO cabe na parede de 250 mm

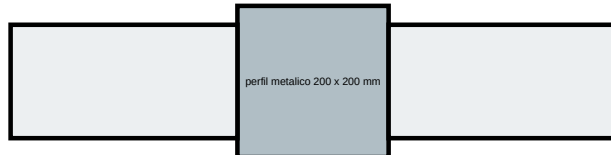

3 PILAR METALICO EMBUTIDO EM PAREDE LSF
ESCALA 1:10

perfil LSF 100 mm

DIMENSIONAMENTO DAS VIGAS — GOVERNADO PELA FLECHA, NAO PELA RESISTENCIA

VIGA	SOBRE	VAO (mm)	T88 (mm)	u (mm)	LIMITE	PERFIL	N (mm)	FLECHA	ADM (mm)	TENSÃO (MPa)	SLF (mm)
V-01	T-001	3000	2700	0,08	L-001	W050x15,0	1305	3,47	6,00	104 (65 %)	10
V-02	T-001	3000	2700	0,08	L-001	W050x15,0	1305	7,94	10,43	70 (31 %)	—
V-03	T-001	3000	2700	0,08	L-001	W050x15,0	1305	11,64	17,14	87 (28 %)	—
V-04	T-001	3000	1500	0,04	L-001	W050x15,0	685	3,77	6,00	83 (27 %)	10
V-05	T-001	3000	3000	0,40	L-001	W050x15,0	1305	3,80	6,00	113 (50 %)	10
V-06	T-001	3000	3000	0,40	L-001	W050x15,0	1305	3,80	6,00	113 (50 %)	10
V-07	T-001	3000	1800	7,06	L-001	W050x15,0	685	4,38	8,57	139 (61 %)	—
V-08	T-001	3000	900	0,78	L-001	W050x15,0	685	3,14	8,57	89 (38 %)	—
V-09	T-001	3000	900	0,78	L-001	W050x15,0	685	3,14	8,57	89 (38 %)	—
V-10	T-001	7200	3000	3,00	L-001	W050x15,0	4340	7,25	10,38	57 (25 %)	10
V-11	T-001	8000	1500	0,72	L-001	W050x15,0	685	5,74	8,57	93 (23 %)	—

POR QUE A FLECHA GOVERNA

GRANDEZA	FAIXA NO PROJETO	LIMITAÇÃO
Uso da resistência à flexão	23 a 61 %	abaixo resistência: o perfil não está no limite em nenhuma viga
Flecha / flecha admissível	37 a 73 %	e aqui que o perfil se aproxima do limite — e é o que define a seção
Consequência de erro a resistência	calagem	evento raro, verificado por cálculo e ART
Consequência de erro a flecha	falha localizada no apoio	evento raro, falha de ordem 1 que se concentra para sempre
Custo de substituir um perfil	2 a 5 kg/m de aço	risco de que uma única reparação da parede falhada

CAIXA D'ÁGUA — CARGA CONCENTRADA

ITEM	VALOR	DECISÃO
Válculo / carga	2000 L / 2000 kg	21 m em 7,20 m2
Posição	abaixo da caixa 150x150x150	abaixo da parede do próprio ambiente, sem plataforma sobre o solo
Base	5000 mm	abaixo do topo do superior
Coluna no terreno	0,5 mca	gratuitamente, fixado
Coluna no superior	0,5 mca	analisando: TC-14 ou 0,5 m no topo superior
Apoio	2 perfis sob a base	dois perfis sob a base, transferindo para as paredes do com. a carga

NOTAS

- O perfil laminado flex, a chapa de apoio sobre a base. As duas medidas são independentes e ambas obrigatórias.
- Flecha limitada a L/200 onde a viga sustenta vedação fixa, contra L/200 de uso geral.
- Junta de deslocamento com flecha de 1,5 x flecha calculada, por viga.
- Pro-dimensionamento por flecha — cálculo estrutural e ART (permite com pendência).

PROJETO PORTO REAL

RESIDENCIA UNIFAMILIAR (MANSÃO - AM) | SOBR TATIANA-PS

PROJETO ARQUITETONICO

INTERFACE LIGHT STEEL FRAME X PERFIL LAMINADO

BASE GEOMETRICA	ESCALA	EMISSÃO	PROJETO
União Consolidada	indicada	ESTUDO PRELIMINAR R32	
em R32 (previsão)		NAO LIBERADO PARA OBRA	
UNIDADE: METRO: MM	FORMATO: A1	SEM ART / RNT	
	VALOR: 605/500/500		

20

06-25 REV R32