



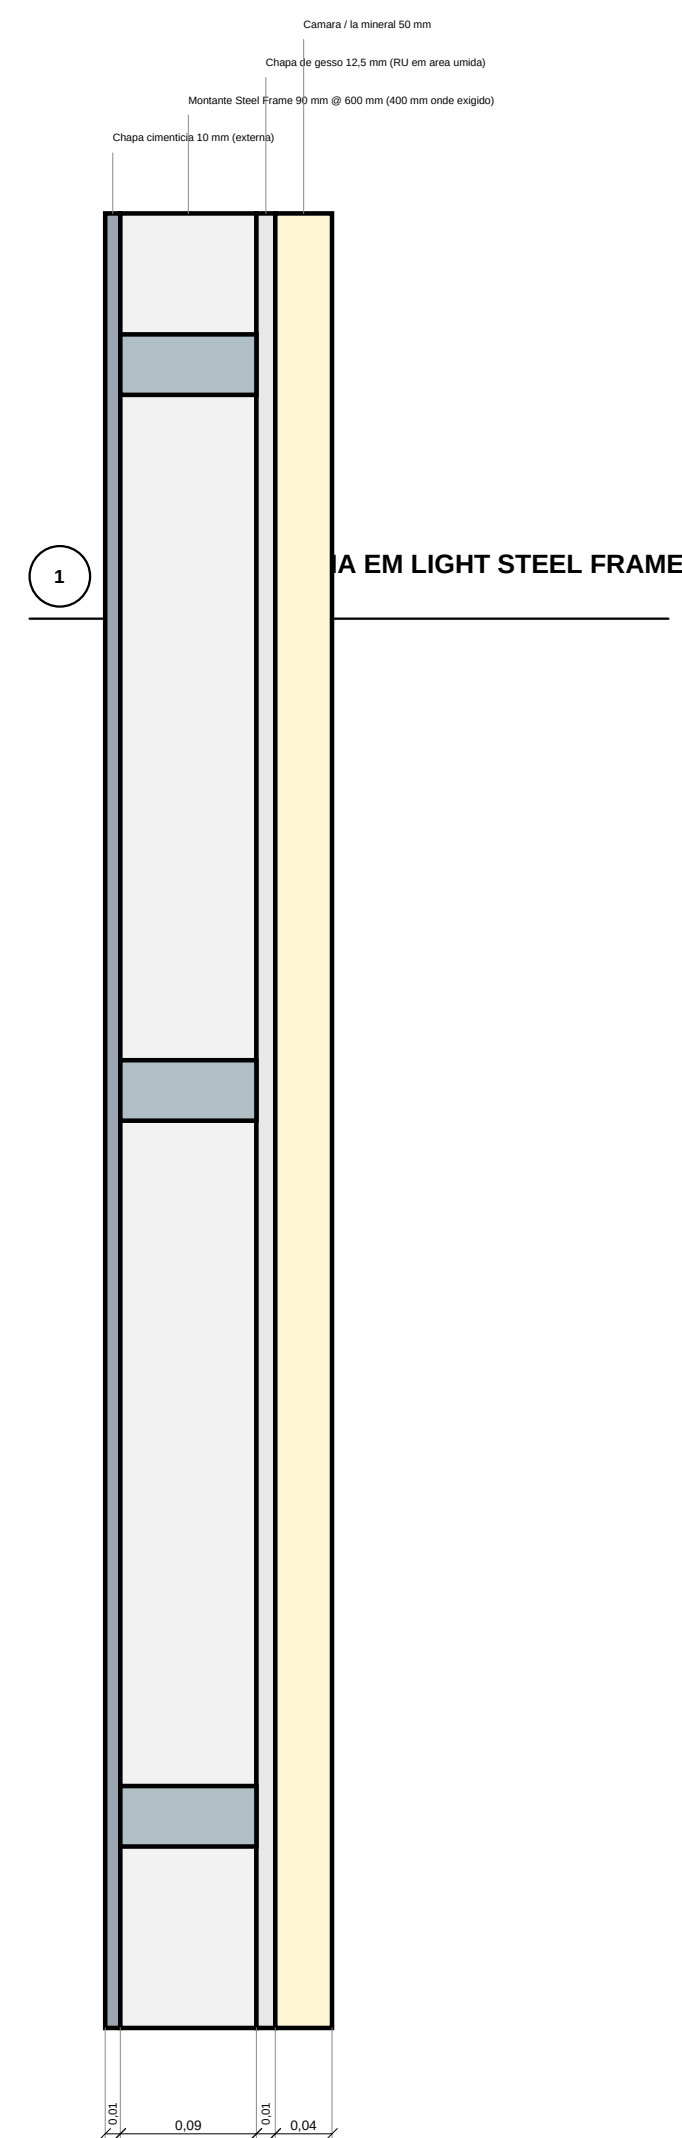


A EM LIGHT STEEL FRAME

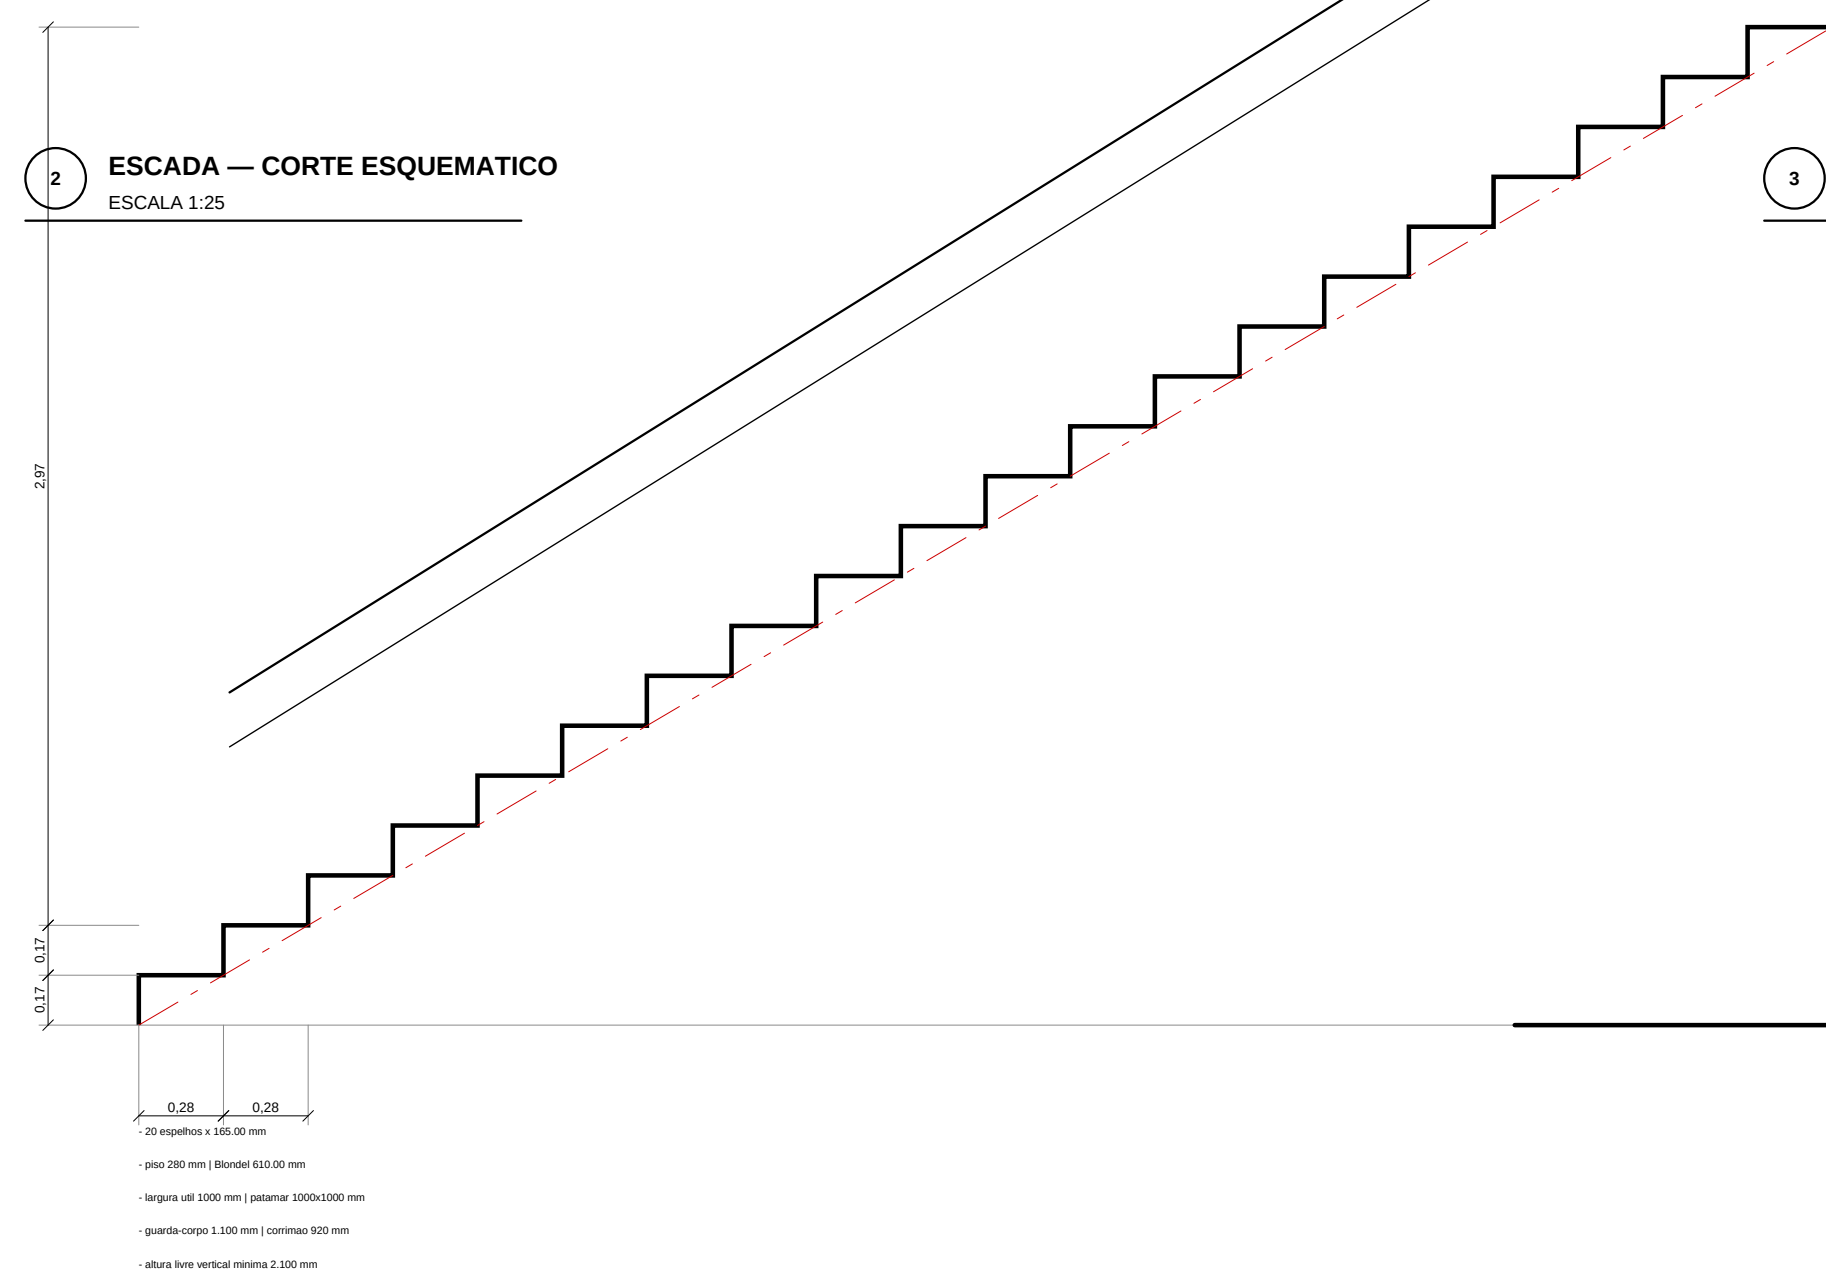

2 ESCADA — CORTE ESQUEMATICO
ESCALA 1:25



3 PISCINA — CORTE
ESCALA 1:25

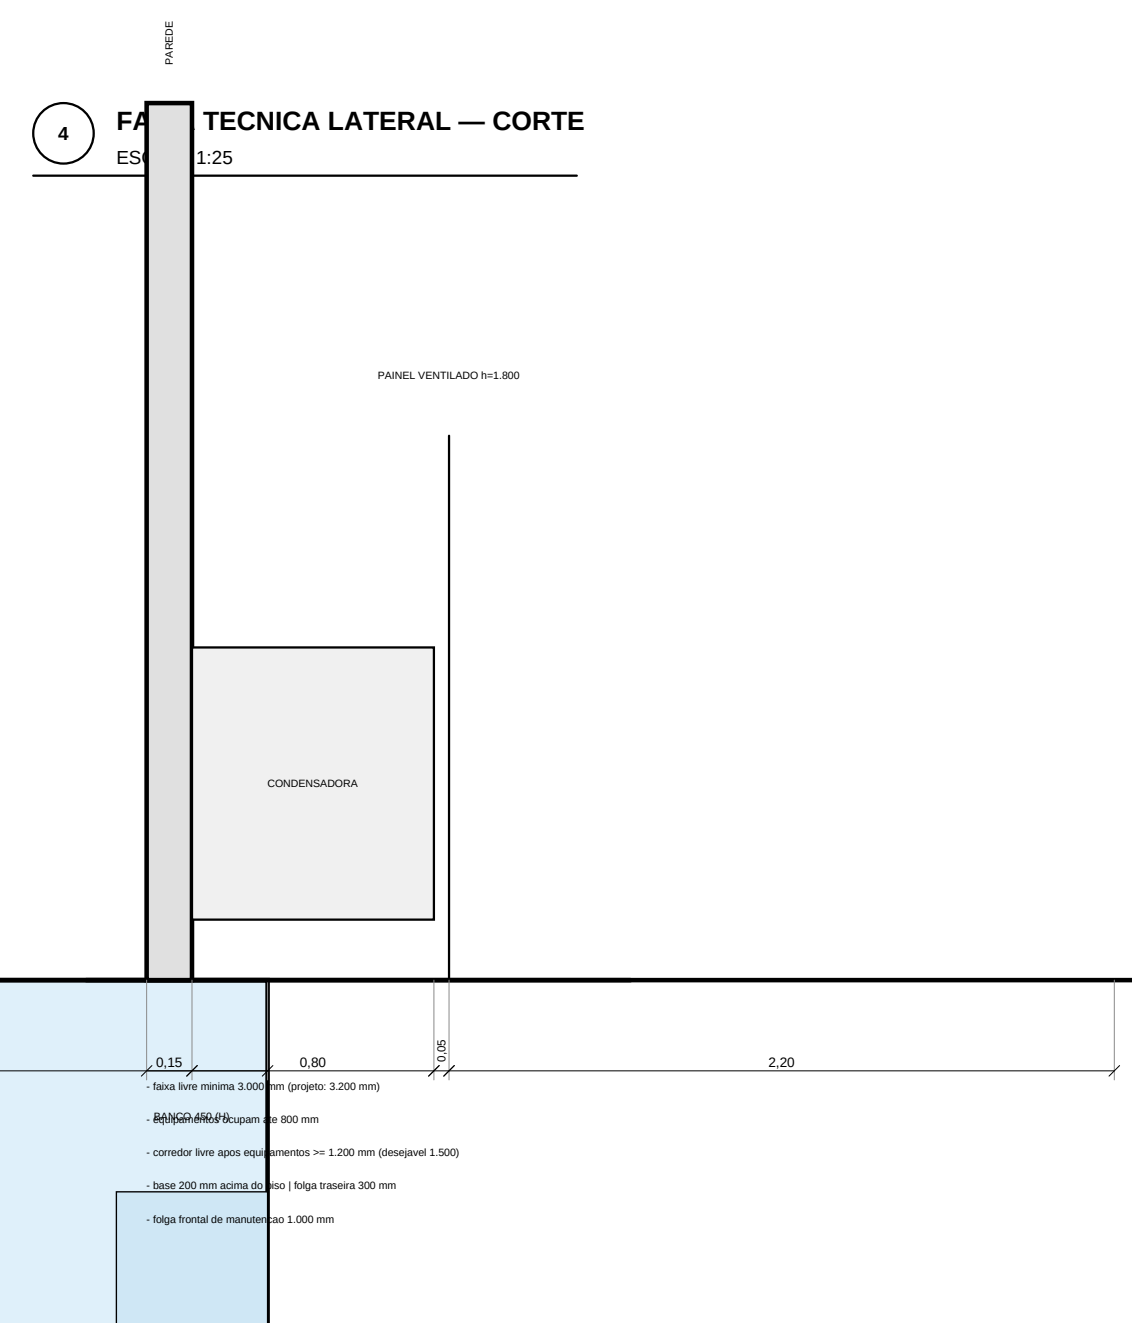

4 FA [redacted] TECNICA LATERAL — CORTE
ES [redacted] 1:25

esp. total 150 mm

NOTAS

- Detalhes de estudo — não liberados para fabricação ou corte (sem nesting codificado).
- Parede externa consolidada em 150 mm; divisória interna em 100 mm (Hf).
- Escada reconciliar com estrutura, guarda-corpo e espessura de acabamento antes de definitiva.

PROJETO PORTO REAL			
RESIDENCIA UNIFAMILIAR MARAUS - AM 500 TATIANA-PS			
PROJETO ARQUITETONICO			
DETALHES CONSTRUTIVOS AMPLIADOS			
BASE GEOMETRICA	ESCALA	MISSAO	PRIMEIRA
Lista Consolidada por-Lista (previstos)	indicada FORMATO A3 MATERIAL: 600/900/350	ESTUDO PRELIMINAR R08 NAO LIBERACAO PARA OBRA SEM ART. 1987	10 04 DE FEV R08