


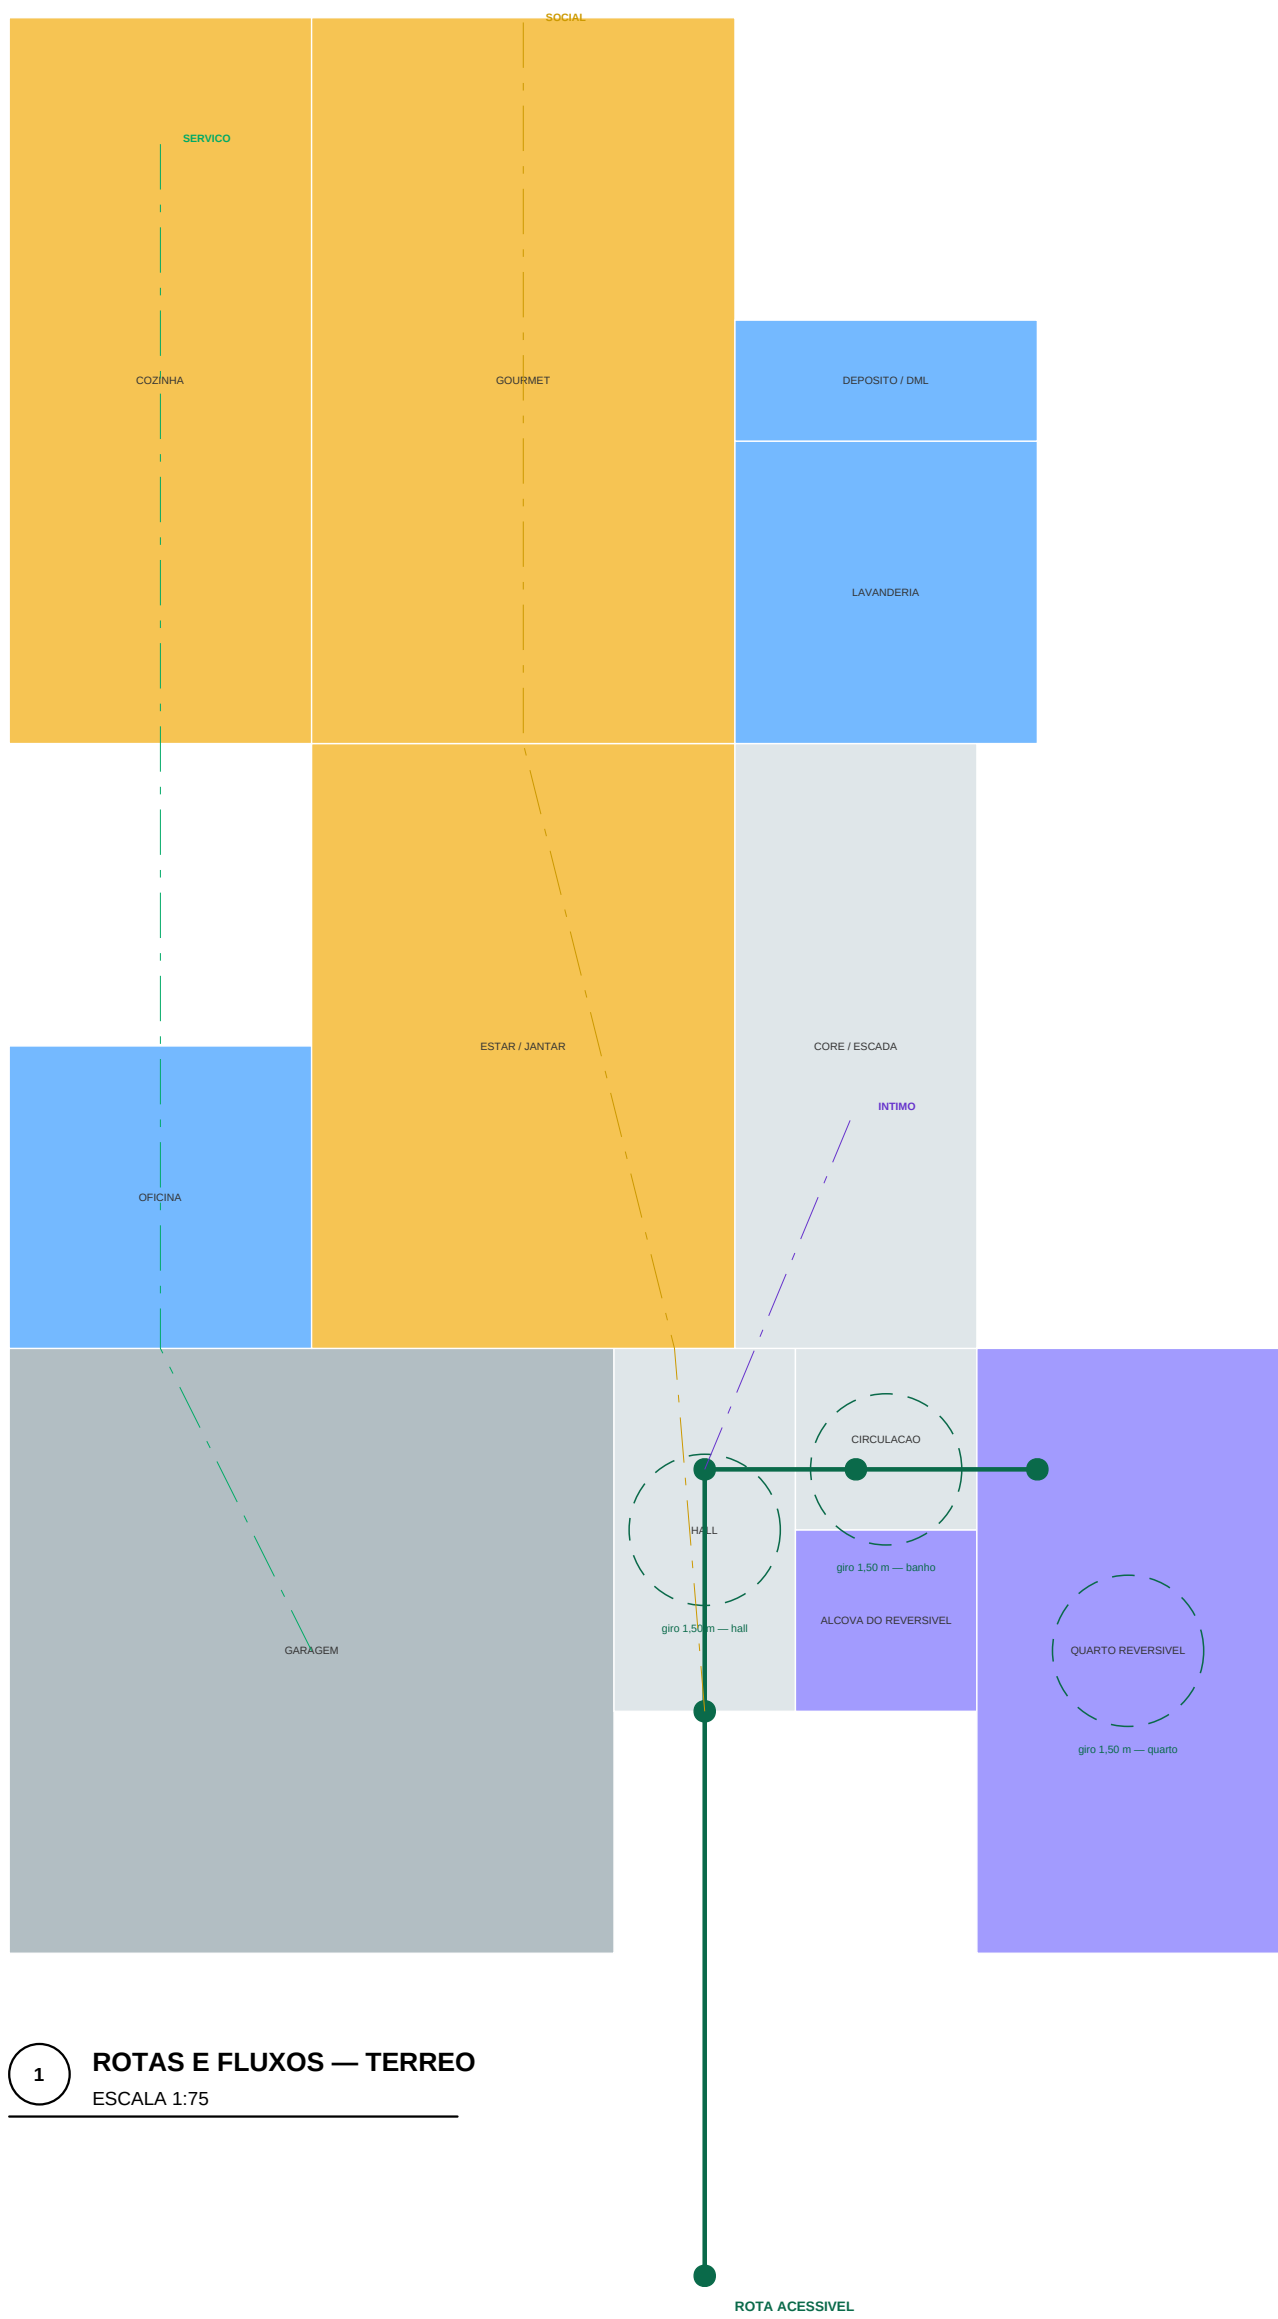


1 ROTAS E FLUXOS — TERREO
ESCALA 1:75

VERIFICACAO NBR 9050

ITEM	EXISTENTE	PROPOSTO	
Visão livre de porta	800 mm	940 mm (altura de 900)	OK
Circuito de giro 360 graus	1.500 mm	hall, banheiro e quarto	OK
Deslocar sem rampas	até 5 mm	soluções elevadas	OK
Largura de circulação	900 mm	1.800 mm no hall	OK
Barras de apoio	relívios prévios	instaladas no PTE 1 e PTE 2	OK
Barras de acesso	altura livre 750 mm	sem barreiras até a altura	OK
Corrimão e interruptor	600 a 1.000 mm	a definir no detalhe	pendente

FLUXOS — SEPARACAO DE CIRCUITOS

CIRCUITO	PERCURSO	CRUZAR O SOCIAL?
Serviço	garagem → oficina → lavanderia → cozinha → despensa	NÃO
Social	entrada → hall → estar → gourmet → alameda → piscina	—
Área de serviço	hall → circulação → banheiro social (quarto reversível) (se não for projeto)	NÃO
Área superior	hall → core → hall superior → suíte	NÃO
Área de carga	cozinha → despensa → reserv. hall	NÃO

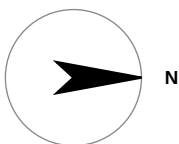

- NOTAS
- * Rota acessível do passeio ao quarto reversível e ao banheiro social.
 - * Circuito de giro de 1.500 mm verificado nos pontos de manobra.
 - * Porta de correr de 900 mm no banheiro social e área de varanda.
 - * Reforço para barras de apoio instaladas antes do fechamento das placas.

PROJETO PORTO REAL

RESIDENCIA UNIFAMILIAR (MANSÃO - AM) | SOUS TATIANA-PS

PROJETO ARQUITETONICO

ACESSIBILIDADE E FLUXOS

BASE GEOMETRICA	ESCALA	EMISSAO	PROVA
Lista Consolidada	1:75	ESTUDO PRELIMINAR RIB	17
ISO-PT2 (previsão)	FORMATO A1	NÃO LIBERADO PARA OBRA	SEM ART / RNT
UNIDADE MESTRE: AM	MALHA 600/600/300	SEM ART / RNT	06.47 REV 008