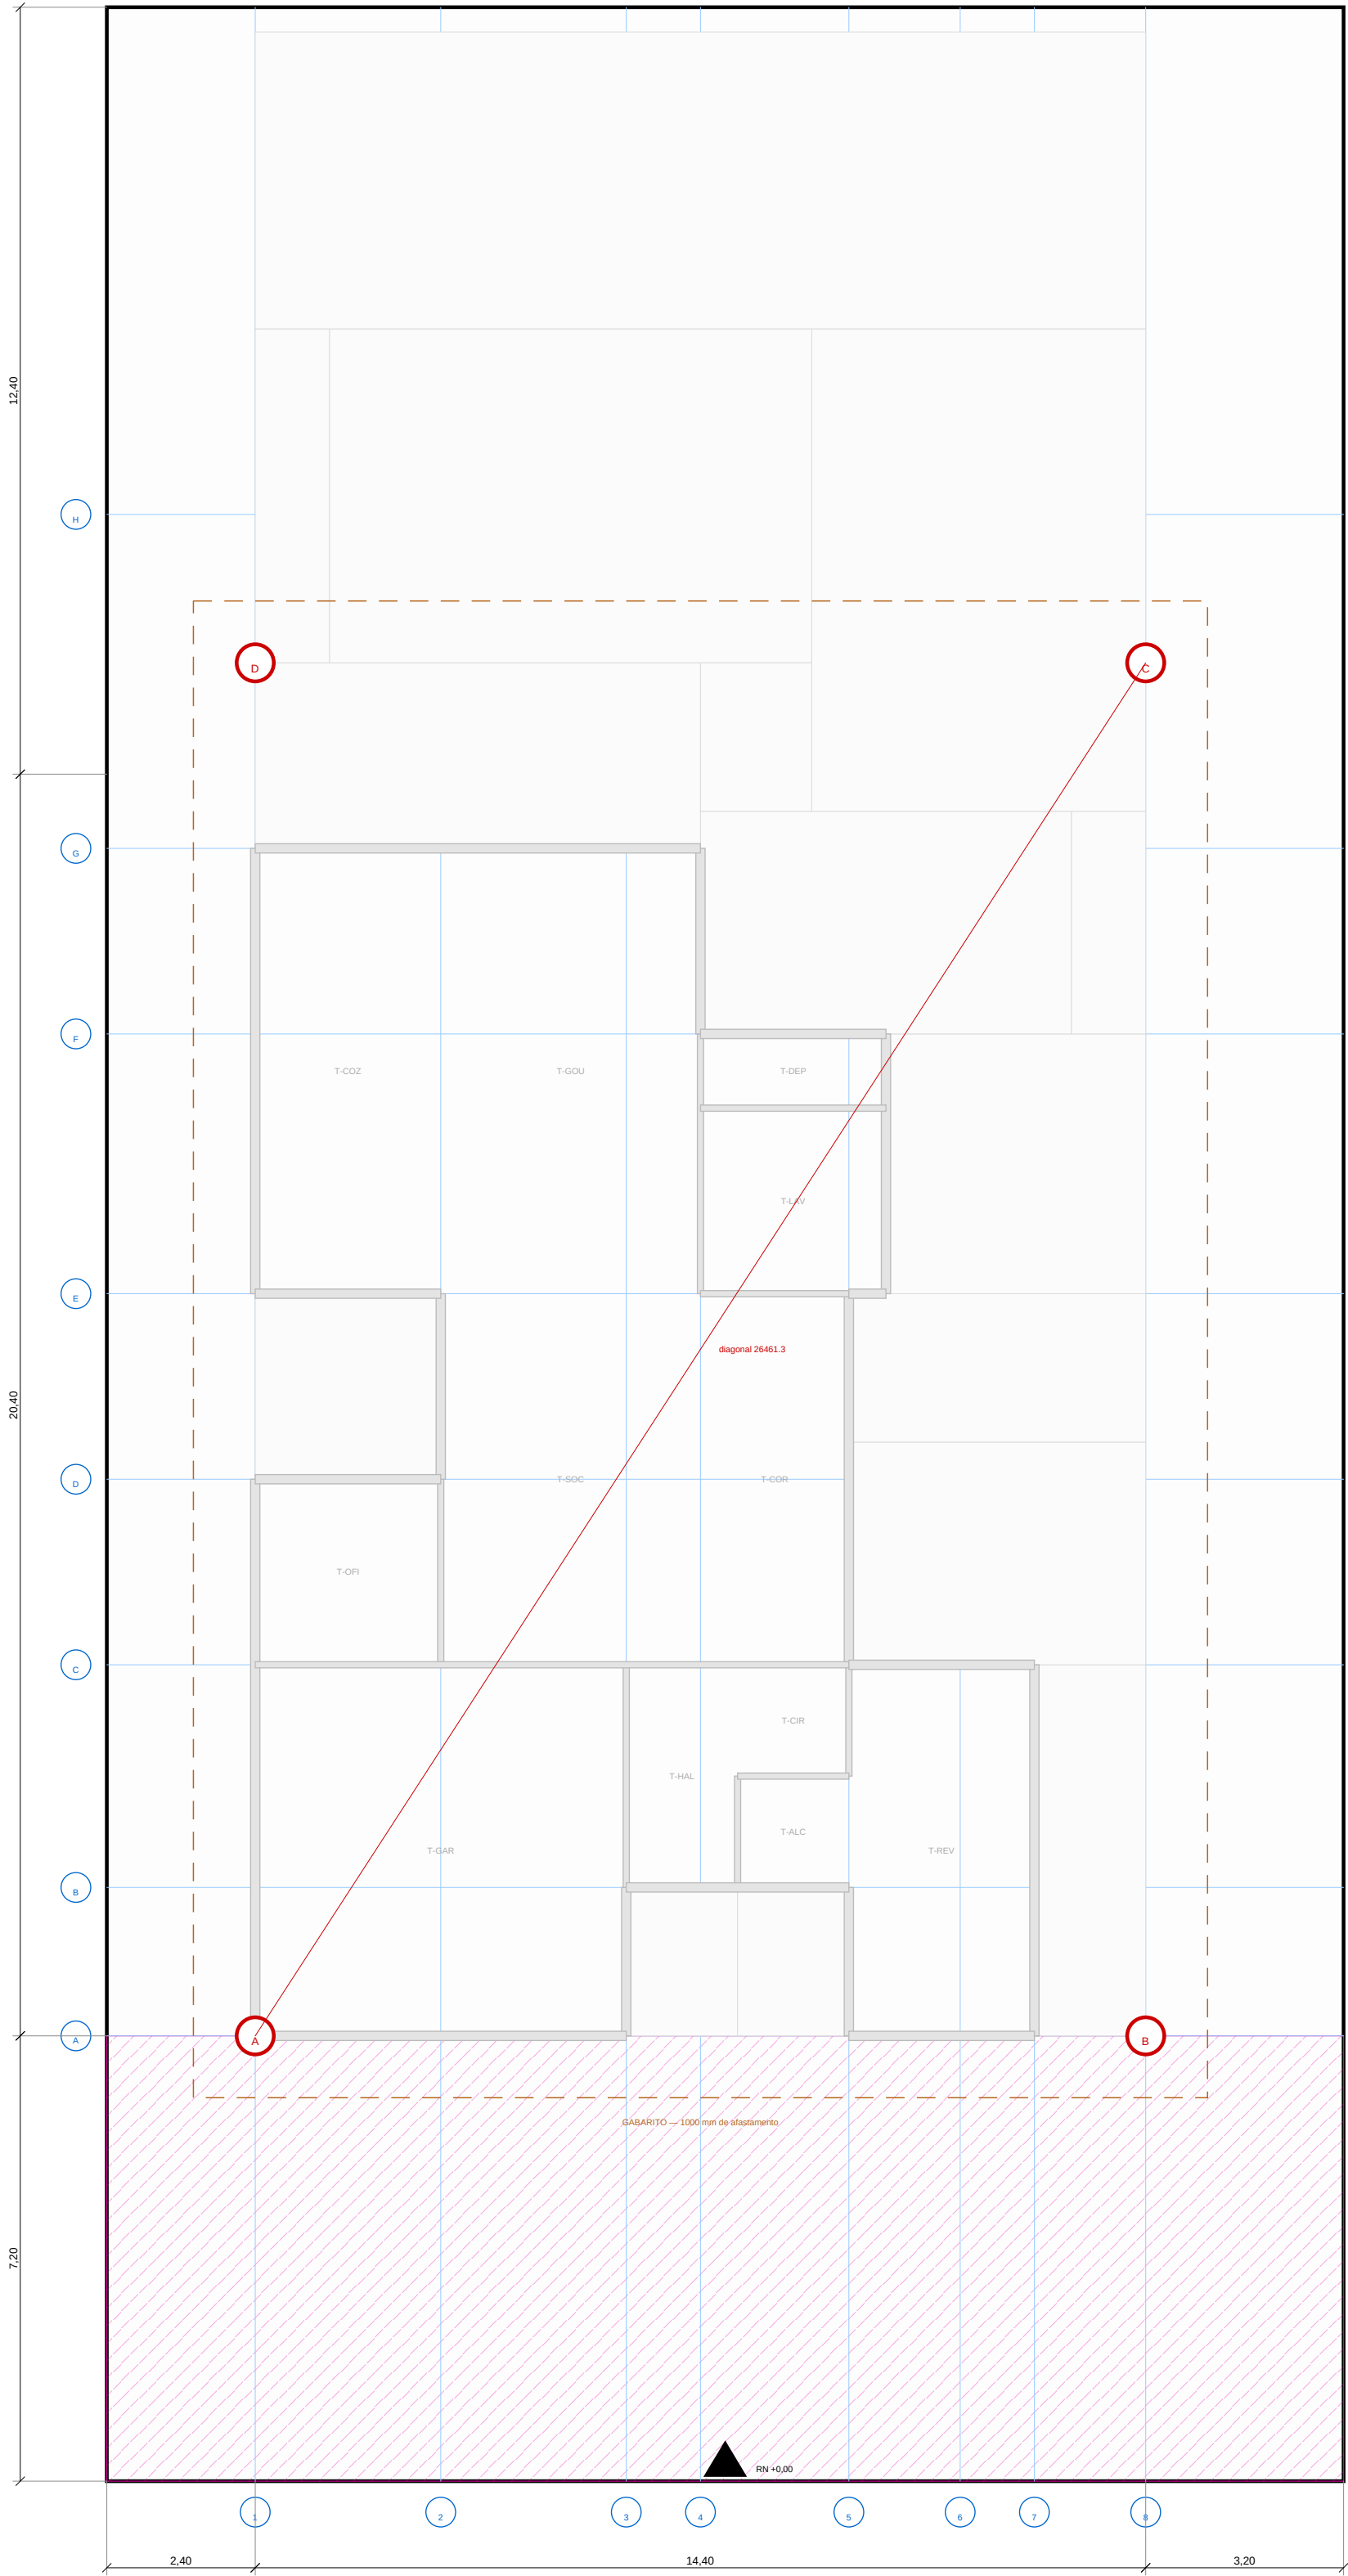


COORDENADAS DOS CANTOS (mm)

CANTO	X	Y	DIVISA SUL	DIVISA NORTE	TESTADA	QUIBO	DIAGONAL
A	2400	7200	2400	17600	7200	32800	26461,3
B	18800	7200	18800	3200	7200	32800	26461,3
C	18800	28400	18800	3200	28400	19600	26461,3
D	2400	28400	2400	17600	28400	19600	26461,3

PROCEDIMENTO DE LOCACAO

#	PASSO	CRITERIO DE ACEITE
1	Conferir as divisas com o material de base	divergencia maxima de 50 mm interromper a locacao
2	Instalar o PNM sobre o concreto 200 x 200 x 100 mm, fora da area de obra	fora da area de obra
3	Montar o gabarito a 1000 mm do canteiro	perguntas 75 x 75 e tubos 20 x 100
4	Marcar os eixos X, Y e Z a 10 mm no gabarito	linha coordenada maxima de 200 mm
5	Colar sobre o canteiro das divisas de obra	verificar em cada eixo, erro de cada eixo
6	Conferir a diagonal A-C	26461,3 mm com tolerancia de 20 mm
7	Conferir o espaçamento por 3-6 mm em cada canto	antes de qualquer concretagem
8	Registrar em ata com foto e modelo	gabarito continuo nos dois lados da obra, conferencia

EIXOS MODULARES

DIRECAO	MODULO (mm)
X (L x R)	2400 5400 8400 9600 12600 13800 15000 16800
Y (A x H)	7200 9600 13200 14200 15000 28400 29400 32800
Matriz	principal 600 mm - diagonal 300 mm
Origem	canto frontal esquerdo da base
Unidade	milímetros

NOTAS

- Locacao e o unico documento em que o erro nao tem impacto direto a obra, pois o erro e corrigido.
- Cada canto e cotado das divisas de obra, nunca em cada eixo acumulado — erro de cada eixo, erro de referencia independente nos.
- Conferencia obrigatoria para diagonal 26461,3 mm entre A e C antes de concretar o canteiro.
- Ata no ato de locacao, assinada por todos os envolvidos (TC-OB, cliente, cliente) e pelo arquiteto do projeto.

PROJETO PORTO REAL

RESIDENCIA UNIFAMILIAR (MANSO) - AM | 2024 (TARMA-PS)

PROJETO ARQUITETONICO

LOCACAO DE OBRA E GABARITO

BASE GEOMETRICA Linha Consolidada Projeto (previsão) Unidade: milímetros (mm)	ESCALA 1:100 Formato A1 Módulo: 600/300 (mm)	EXIBICAO ESTUDO PRELIMINAR RBB Linha Consolidada PARA OBRA SEM ART / RNT	PROJETO 31 06.47 REVISE
--	--	---	--------------------------------------