




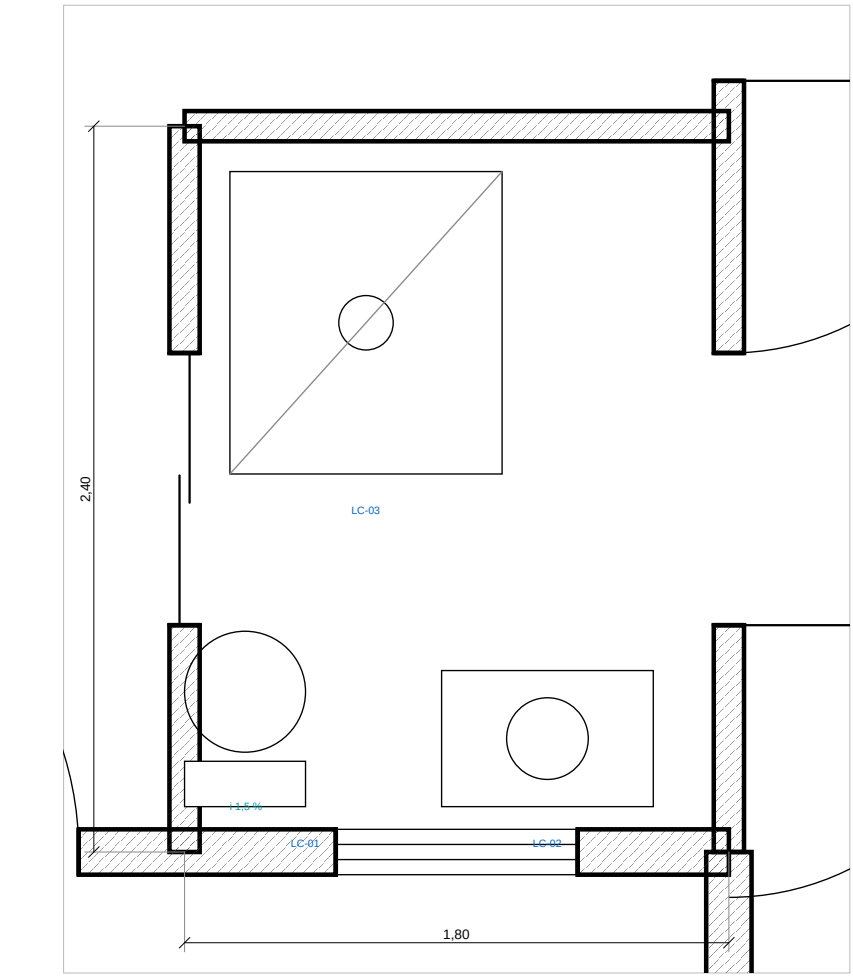


1 BANHO SOCIAL
ESCALA 1:25

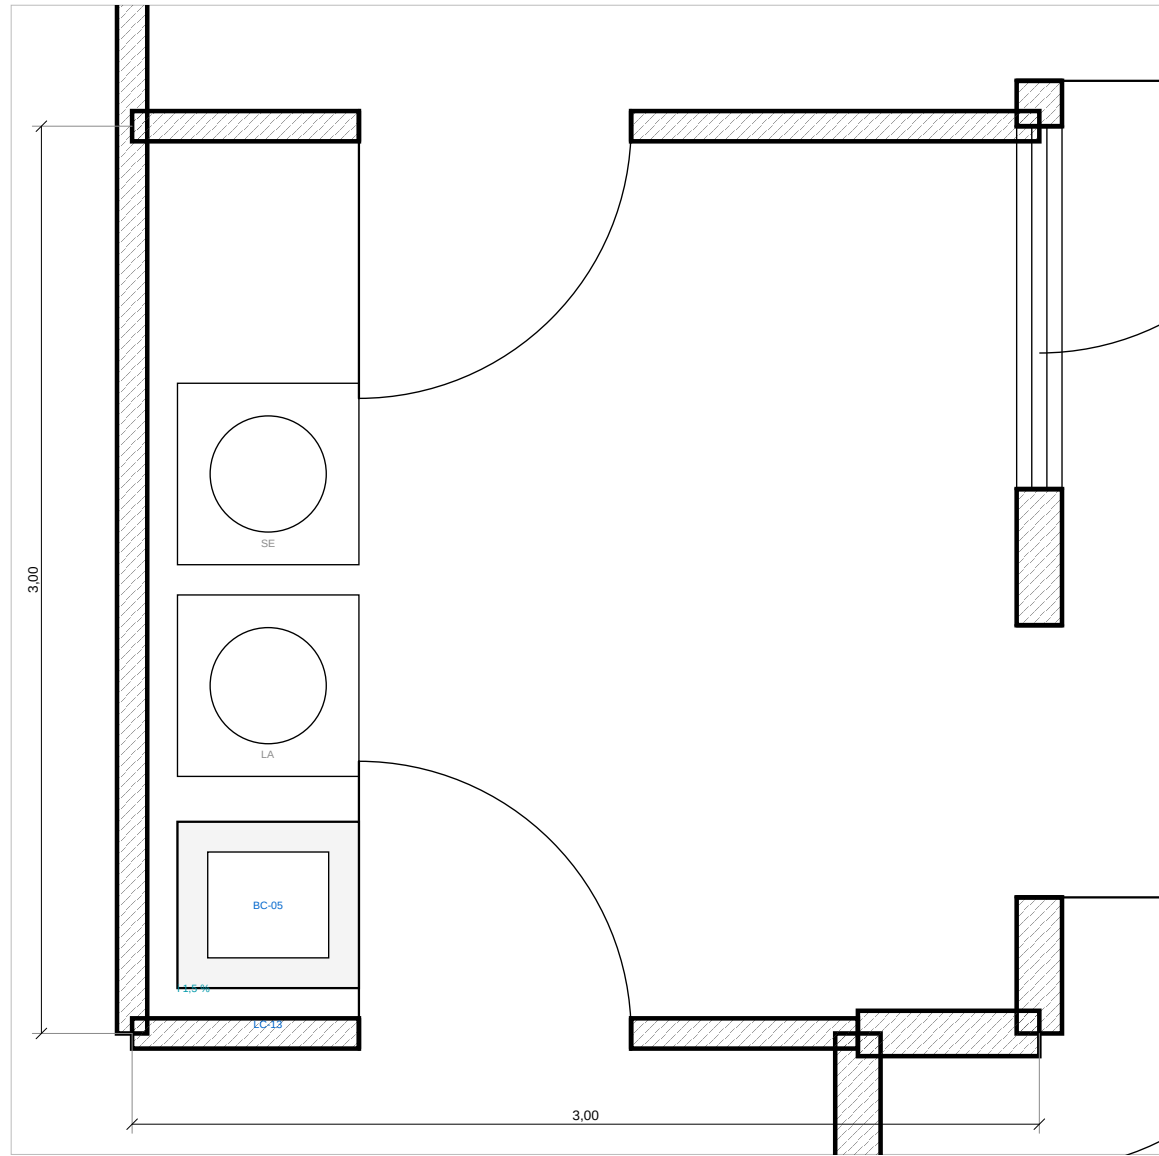

2 LAVANDERIA
ESCALA 1:25

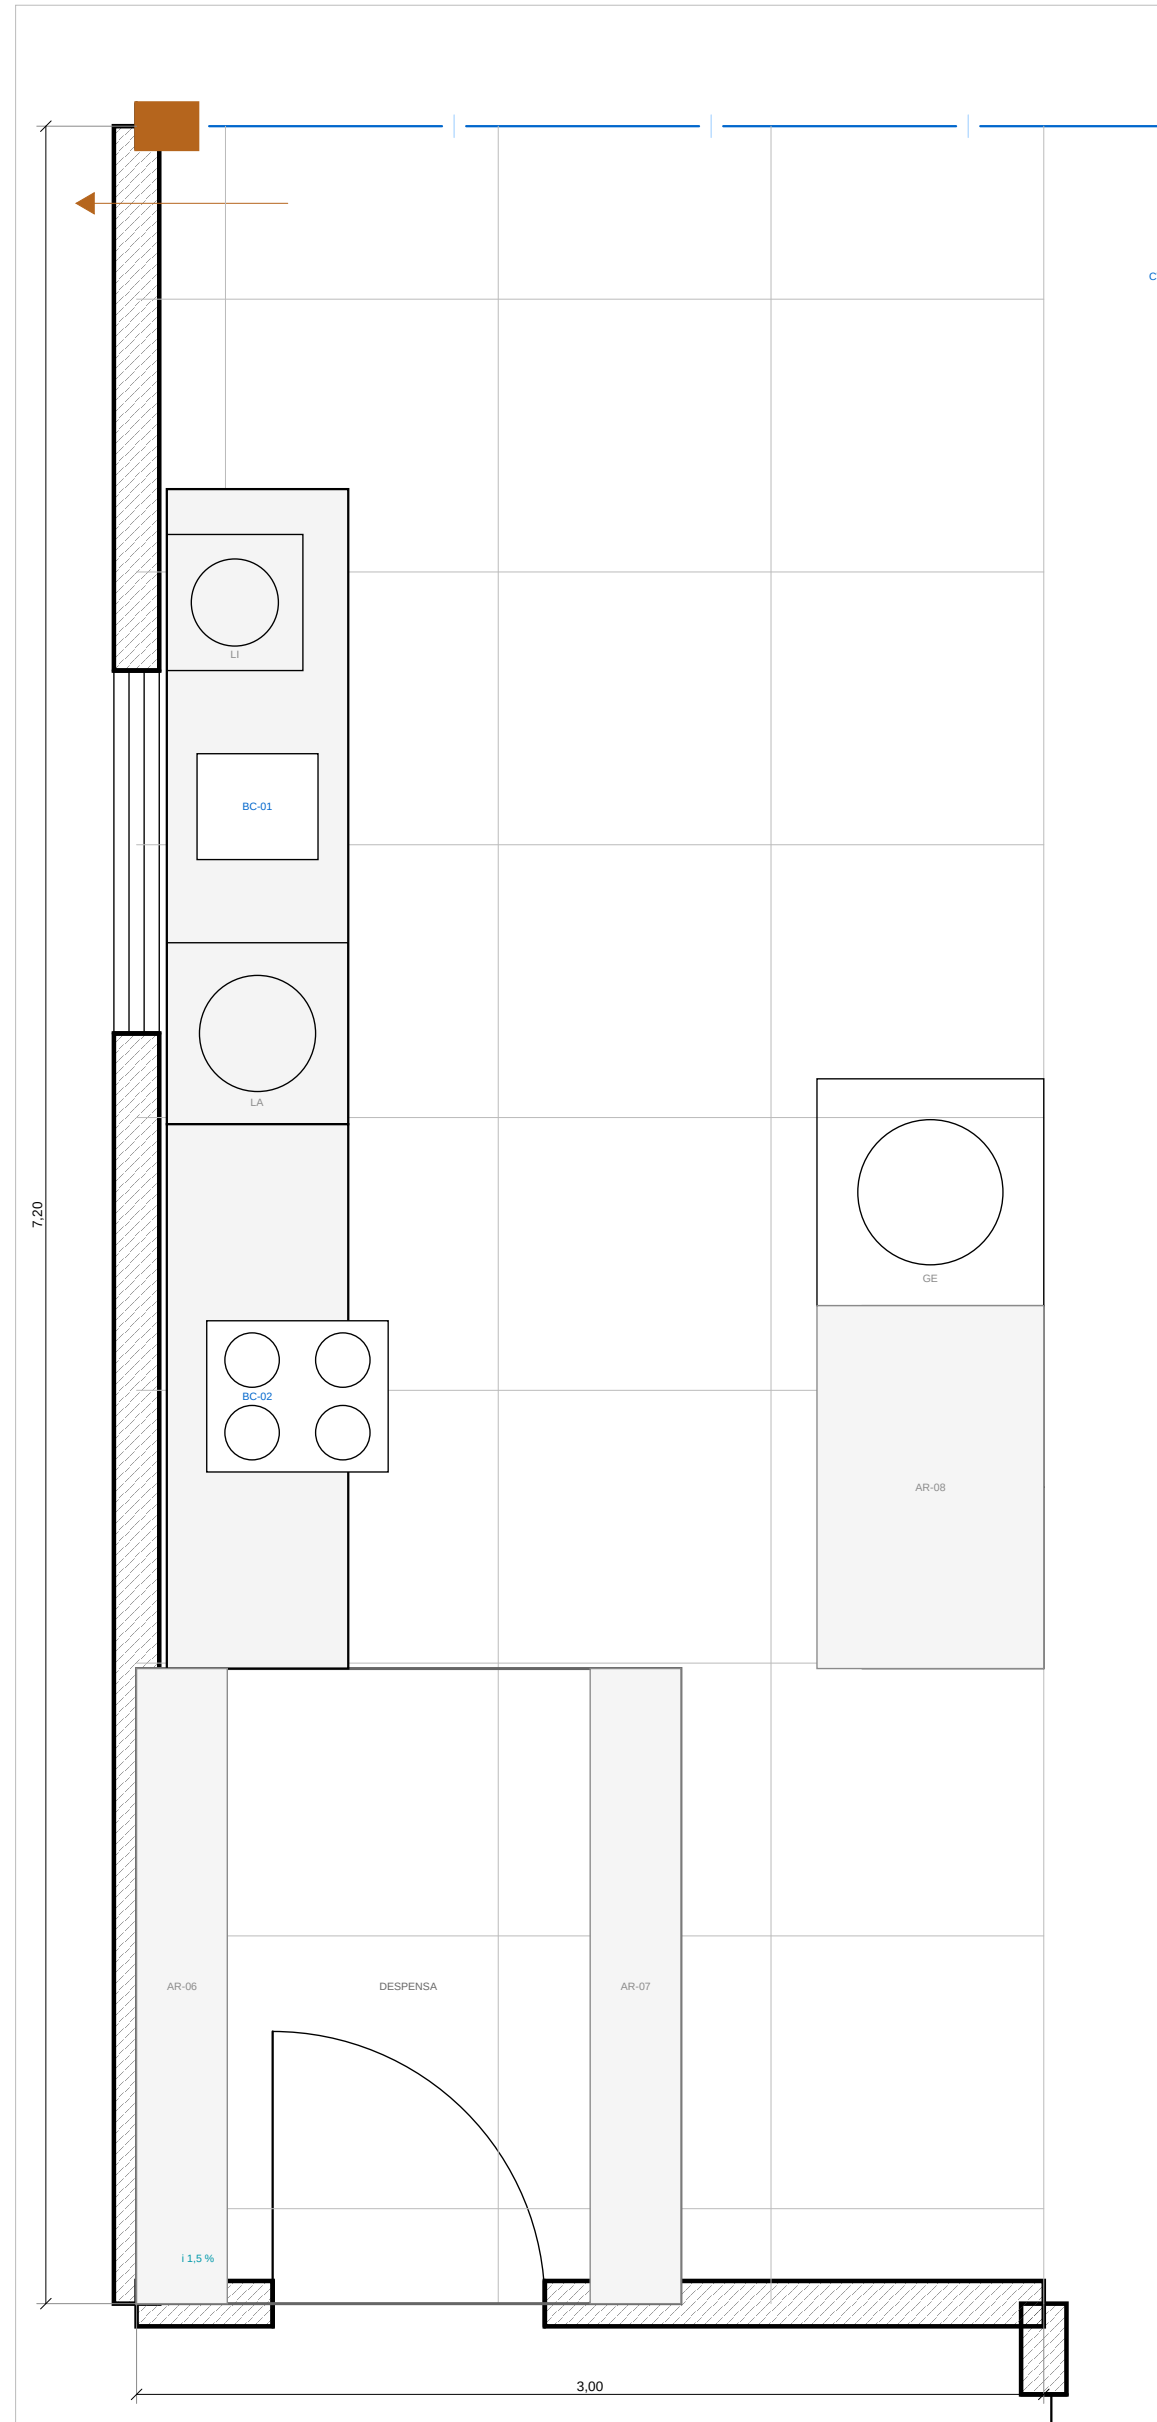

3 COZINHA
ESCALA 1:25

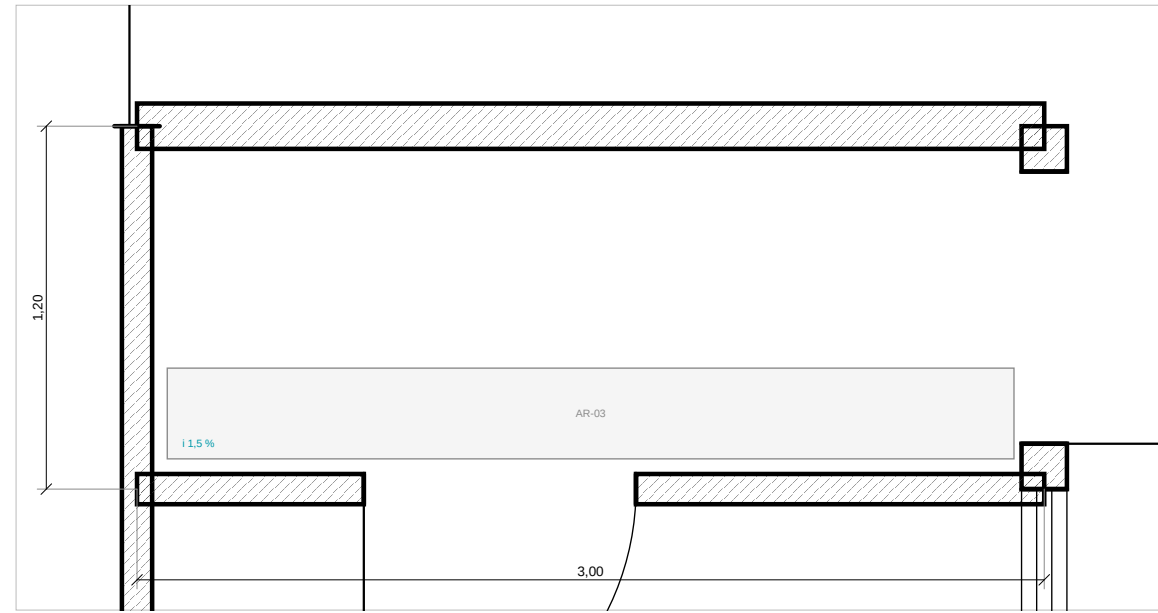

4 DEPOSITO / DML
ESCALA 1:25

PAGINACAO VERIFICADA — PECAS INTEIRAS + RECORTE EM CADA PONTA

AMB	AMBIENTE	ZONA	PEÇA	ESQD X	ESQD Y	ALTURA (mm)
T-BWC	BANHO SOCIAL	ZP-4	parede	0 + 0200	0 + 0000	2400 (2 Ruas + 100)
T-LAV	LAVANDERIA	ZP-5	parede	0 + 0200	4 + 0500	1800 (2 Ruas + 100)
T-COZ	COZINHA	ZP-1	pis	0 + 0000	7 + 11000	—
T-DEP	DEPOSITO / DML	ZP-5	parede	0 + 0200	1 + 0500	1800 (2 Ruas + 100)

- NOTAS
- * Pignoneiros de piso em linha fina, a malha vem da ZONA de pignoneiros, não do canto do ambiente.
 - * Peca de piso porcelanado retificado 300 x 300, parede ceramico retificado 300 x 600, junta 2 mm.
 - * Camaroto de 1,5 % para o piso em toda area molhada, solteira elevada 15 mm nos bicos.
 - * Representação: marra lquida em 2 dimensoes, subido 300 mm na parede e 1.800 mm nos bicos.

PROJETO PORTO REAL

RESIDENCIA UNIFAMILIAR (MANAUS - AM) | SOUZA TARTAGLIA-PS

PROJETO ARQUITETONICO

AMPLIACOES DE AREA MOLHADA — TERREO

BASE GEOMETRICA Linha Consolidada Projeto (previsão) UNIDADE: METRO (m)	ESCALA 1:25 FORMATO: A1 MATERIAL: 600/600/300	EXIBICAO ESTUDIO PRELIMINAR R43 Linha Consolidada PARA OBRAS SEM ART / RNT	PROJETO 22 06-25 REV R43
--	--	---	--------------------------------