


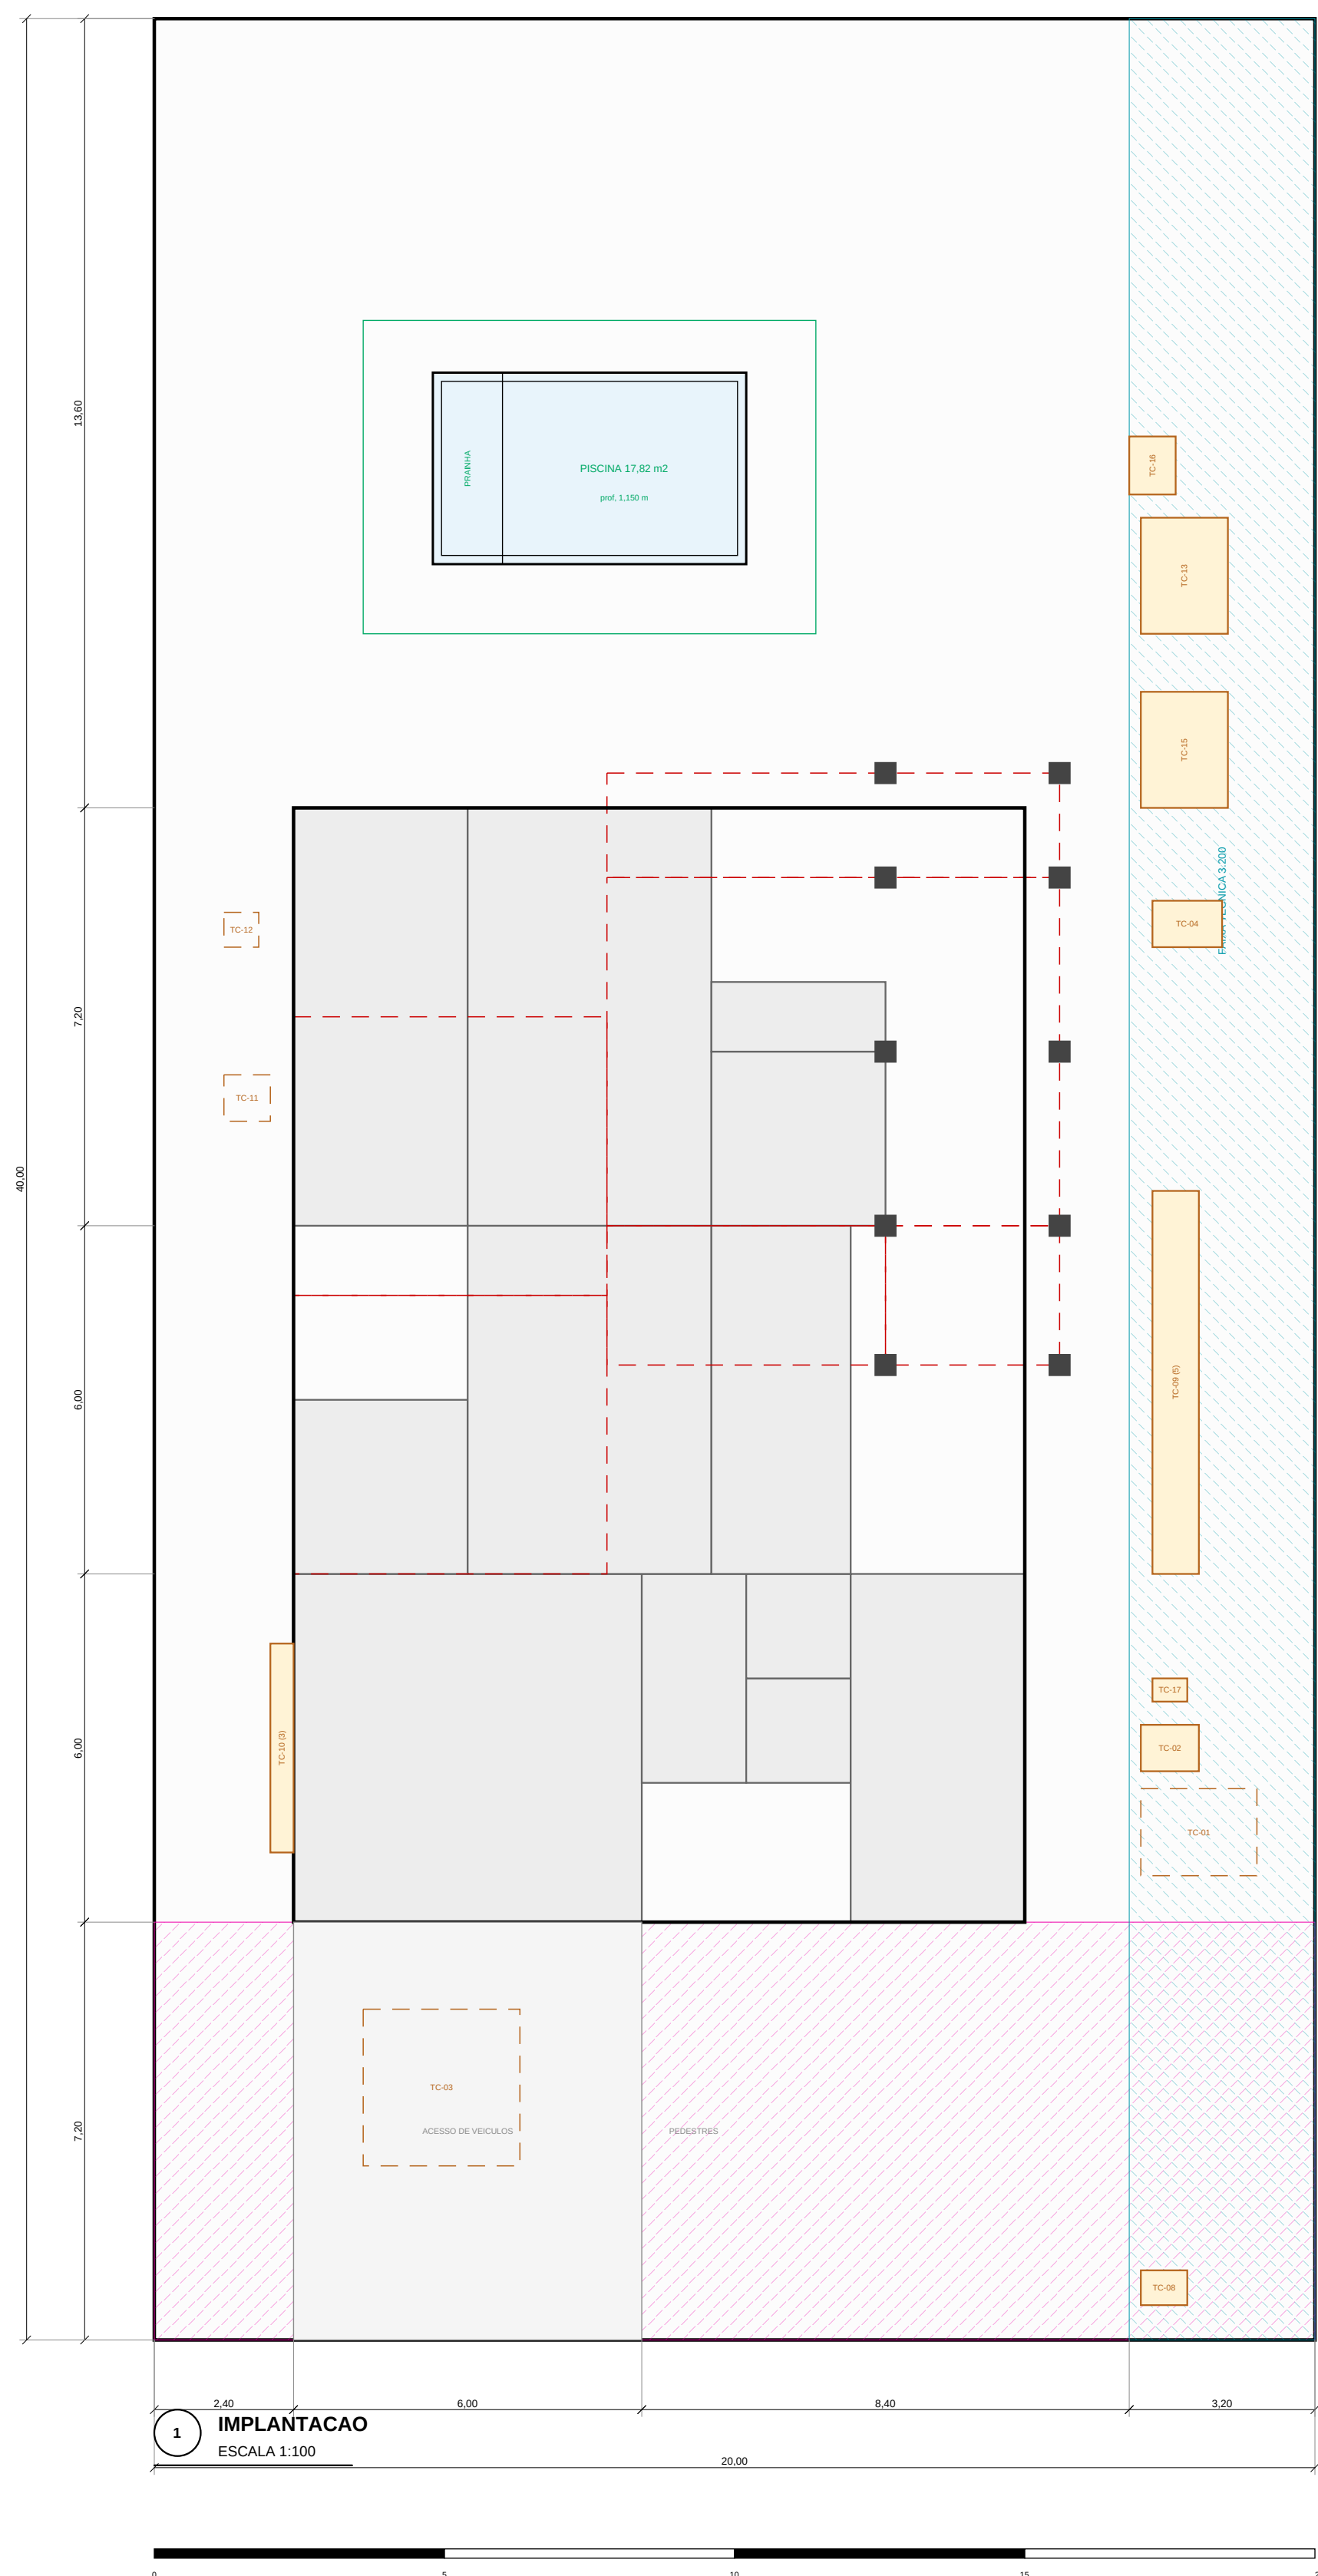

PARAMETRO	PROJETO	LIMITES	
Taxa de ocupação	33,21 %	max 30 %	OK
Coeff. de aproveitamento	0,272	max 1,00	OK
Cobertura	2 pavimentos	max 4,00	OK
Recuo frontal	7500 mm	conforme S/Cd p/6	OK
Recuo lateral eq.	2400 mm	sem parâmetro definido	OK
Faixa técnica de	3200 mm	rec. 3000 mm	OK
Recuo de fundo	13600 mm	rec. 5000 mm	OK

NOTAS

- Lote 20.000 x 40.000 mm = 800.00 m2.
- Recuos: frontal 7,200 / lateral esq. 2,400 / faixa tecnica dir. 3,200 / fundo 13,600 mm.
- Parametros do SU/05 Tarumã/Tarumã-Açu sao hipoteses (H) — pendente certidao de uso do solo.
- Sem muro frontal, muros laterais e de fundo h = 2,200 mm.

PROJETO PORTO REAL

RESIDÊNCIA UNIFAMILIAR | MANAUS - AM | 5016 TARUMA 7

PROJETO ARQUITETONICO

IMPLANTACAO E SITUACAO

BASE GEOMÉTRICA	ESCALA	EMISSÃO	PRANCHA
Lista Consolidada	1:100	ESTUDO PRELIMINAR R79	01
pos-R32 (previsto)	FORMATO A1	NÃO LIBERADO PARA OBRA	
UNIDADE MEDIDA: m/m	MALHA: 600/300/350	SEM ART. INT.	OK-72 REV R79