




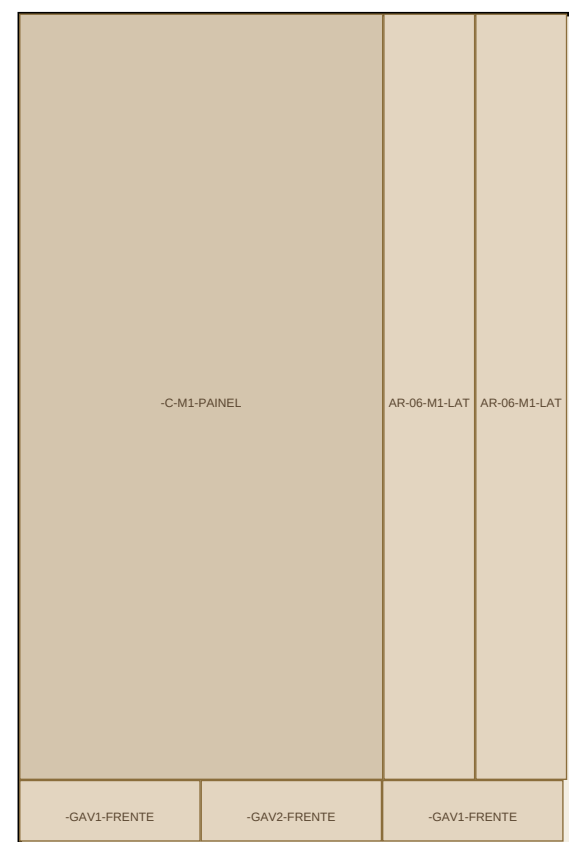


C-1001 — 6 peças, 63 %

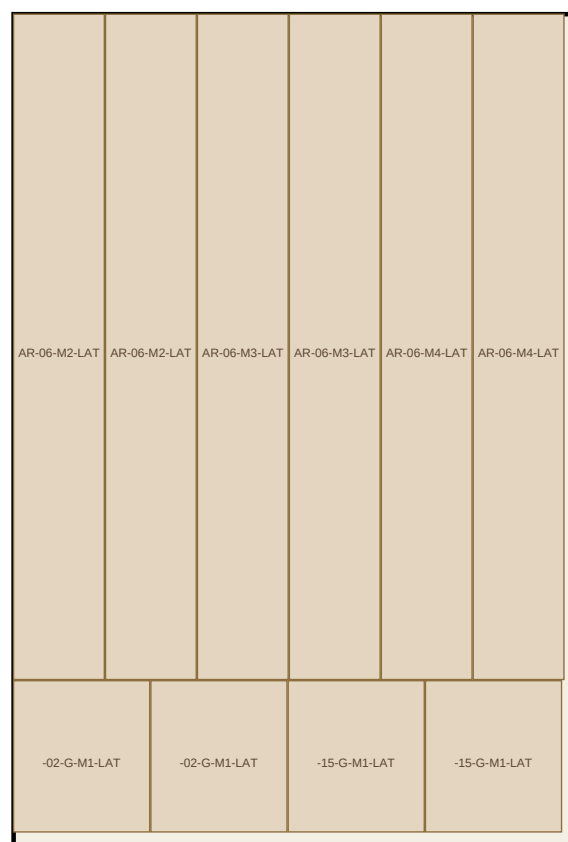


CH002 — 10 peças, 66 %

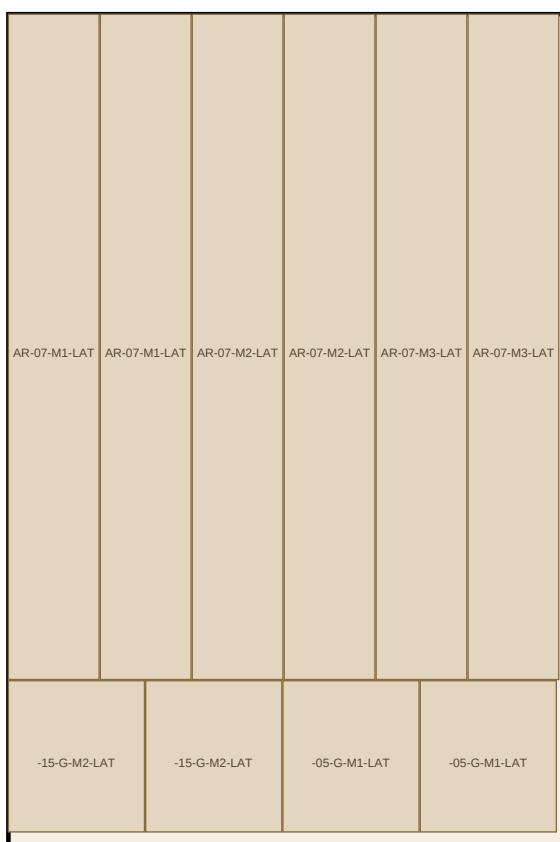


C-003 — 10 peças, 96 %

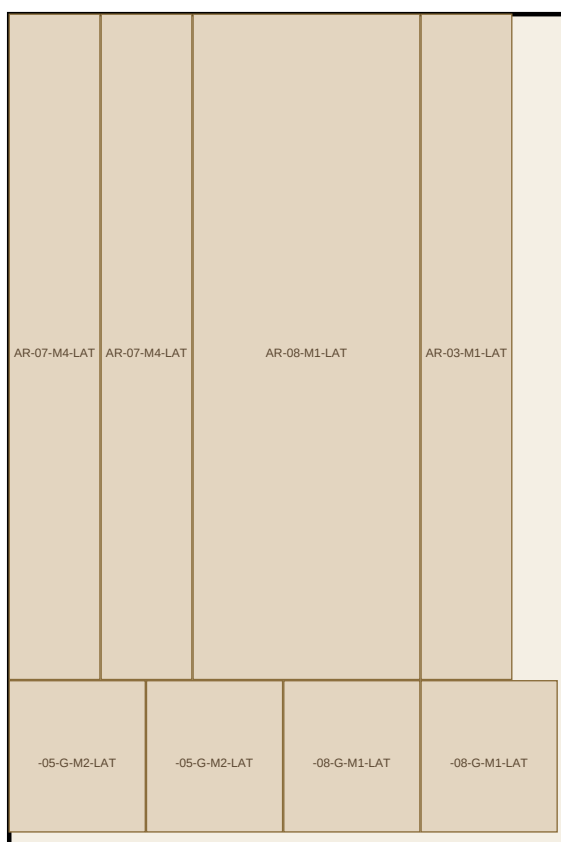


CH004 — 8 pecas, 89 %

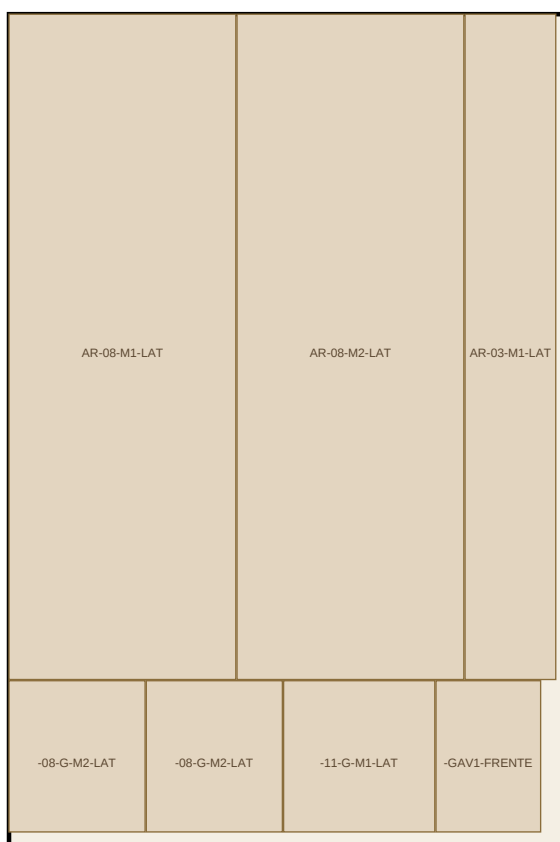


CH005 — 7 peças, 96 %

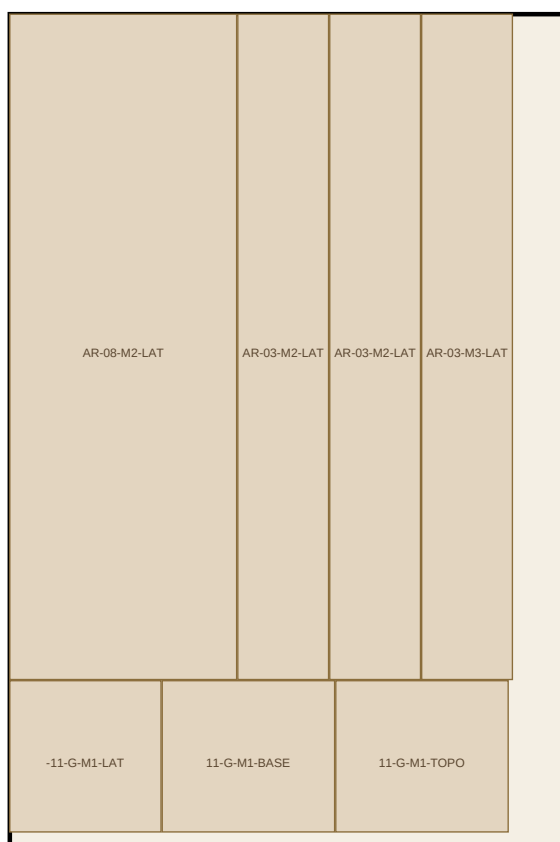

CH006 — 7 peças, 87 %

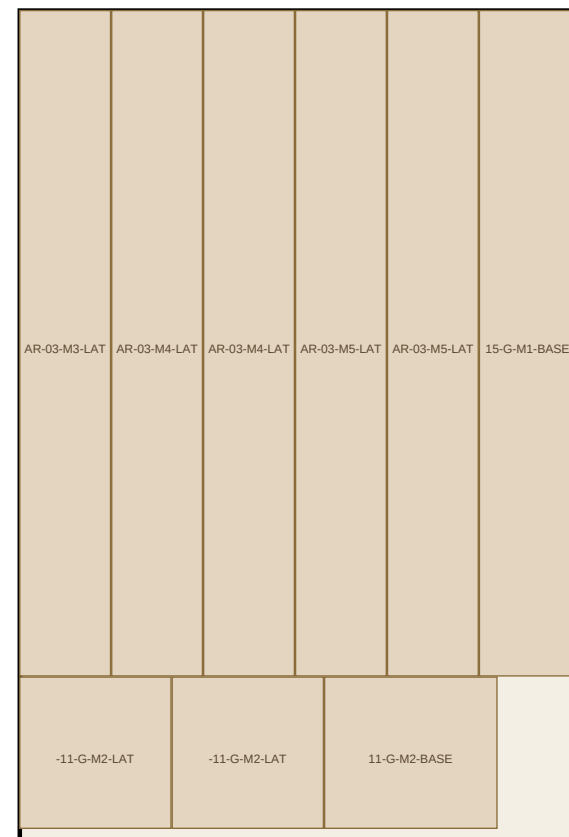

CH007 — 9 peças, 83 %

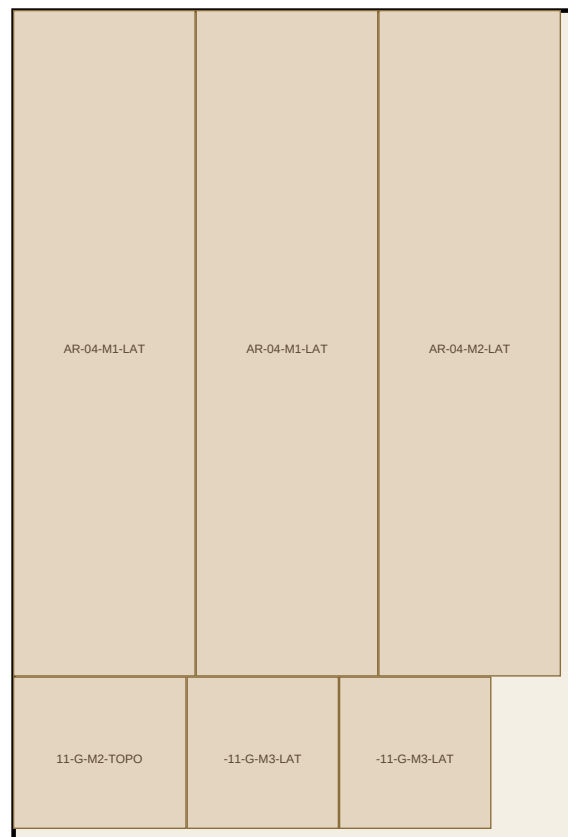


CH008 — 6 pages, 93 %



CH079 — 8 pags, 95 %



CH023 — 8 peças, 94 %

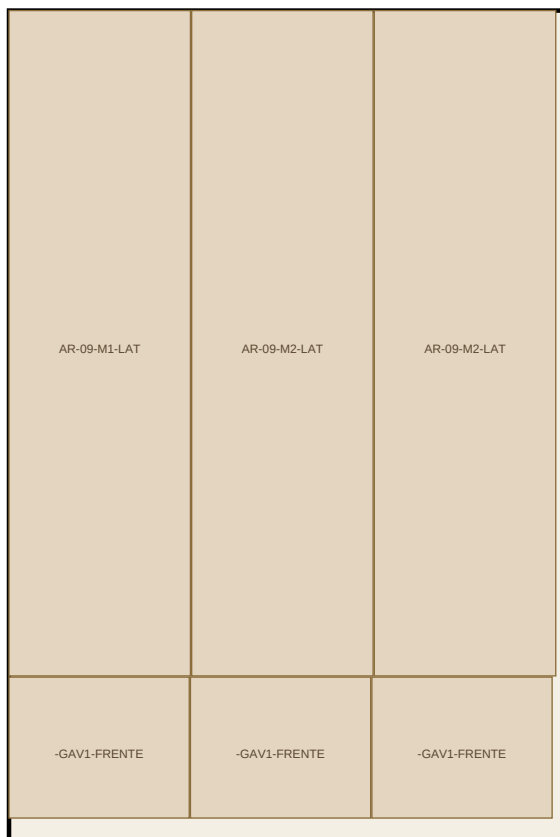

CH011 — 6 peças, 94 %



CH012 — 7 peças, 94 %


CHAPAS DE 15 mm — 68 CHAPAS

CHAP	PECS	APPROV
CH001	5	55%
CH002	33	56%
CH003	20	56%
CH004	8	59%
CH005	7	59%
CH006	7	61%
CH007	5	63%
CH008	6	63%
CH009	6	65%
CH010	5	64%
CH011	6	64%
CH012	7	64%
CH013	8	62%
CH014	6	63%
CH015	5	64%
CH016	7	55%
CH017	7	55%
CH018	7	55%
CH019	7	52%
CH020	8	52%
CH021	6	52%
CH022	6	53%
CH023	6	53%
CH024	6	52%
CH025	5	52%
CH026	7	53%
CH027	10	56%
CH028	9	53%
CH029	9	53%
CH030	9	53%
CH031	9	53%
CH032	9	54%
CH033	9	54%
CH034	9	54%
CH035	9	54%
CH036	10	54%
CH037	9	52%
CH038	10	54%
CH039	6	56%
CH040	4	56%

CMAP	PEAS	APPROV.
CM041	9	15%
CM042	12	22%
CM043	12	27%
CM044	12	27%
CM045	12	30%
CM046	12	31%
CM047	12	36%
CM048	15	30%
CM049	12	30%
CM050	15	39%
CM051	15	39%
CM052	15	39%
CM053	14	43%
CM054	13	37%
CM055	15	36%
CM056	15	36%
CM057	15	36%
CM058	15	36%
CM059	15	36%
CM060	15	36%
CM061	15	36%
CM062	15	36%
CM063	17	42%
CM064	18	54%
CM065	18	52%
CM066	30	77%
CM067	40	80%
CM068	48	96%
CM069	12	20%

CHAPAS DE 6 mm — 20

DMAPA	PECAS	APPROV.
CH002	7	82 %
CH003	7	85 %
CH003	5	85 %
CH004	5	89 %
CH005	5	87 %
CH006	6	92 %
CH007	5	92 %
CH008	7	93 %
CH009	7	94 %
CH011	7	93 %
CH011	7	93 %
CH012	6	92 %
CH012	6	92 %
CH013	6	92 %
CH013	5	92 %
CH018	6	88 %
CH017	11	78 %
CH018	13	92 %
CH019	13	77 %
CH020	8	79 %

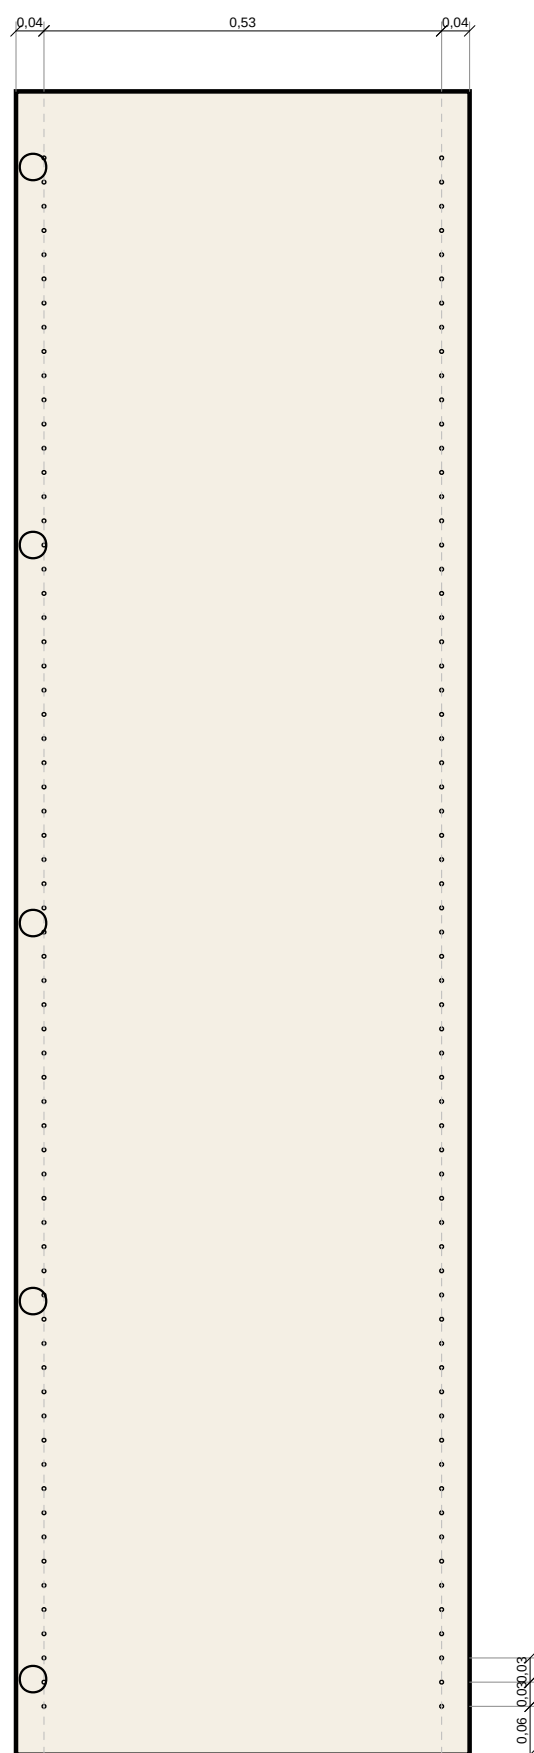

A LATERAL TIPICA 600 x 2.200 — FURCAO SISTEMA 32 E CANECOS
ESCALA 1:10

FURACAO POR PECA — 127 LINHAS (as primeiras)

[illegible]

NOTAS

- Chapa MDF 2750 x 1850 mm, sem 4 mm, com guilhotinado em faixas pelo mesmo neling das placas de fechamento (nucleopieling)

- 15 mm: 731 peças em 68 chapas, 89 % de aproveitamento. 6 mm (fundos): 347 peças em 20 chapas, 85 %.

* As primeiras 12 chapas de 15 mm estão desenhadas; as demais seguem a mesma lista (engenharia.jon e a lista de peças da PR-59).

- Sistema 32: fileiras a 37 mm das bordas, furos de 5 mm x 13 a cada 22 mm; caneco de 35 mm a 22,5 mm da borda

PROJETO PORTO REAL

RESIDÊNCIA UNIFAMILIAR | MANAUS - AM | SU16 TARUMA (H)

PROJETO ARQUITETÔNICO

MARCENARIA — PLANO DE CORTE DE CHAPAS E FURCAO SISTEMA 32

BASE GEOMETRICA Lista Consolidada per R32 (univertel) UNIVERSIDADE FEDERAL DO RIO DE JANEIRO	ESCALA 1:25 · 1:10 FORMATO A1 MALHA 900/900/350	EMISSAO ESTUDO PRELIMINAR R79 RAO LIBERATO PARA ODBA SEM ART / RNT	PRONCHIA 58 de 72 REV R79
---	--	---	---