


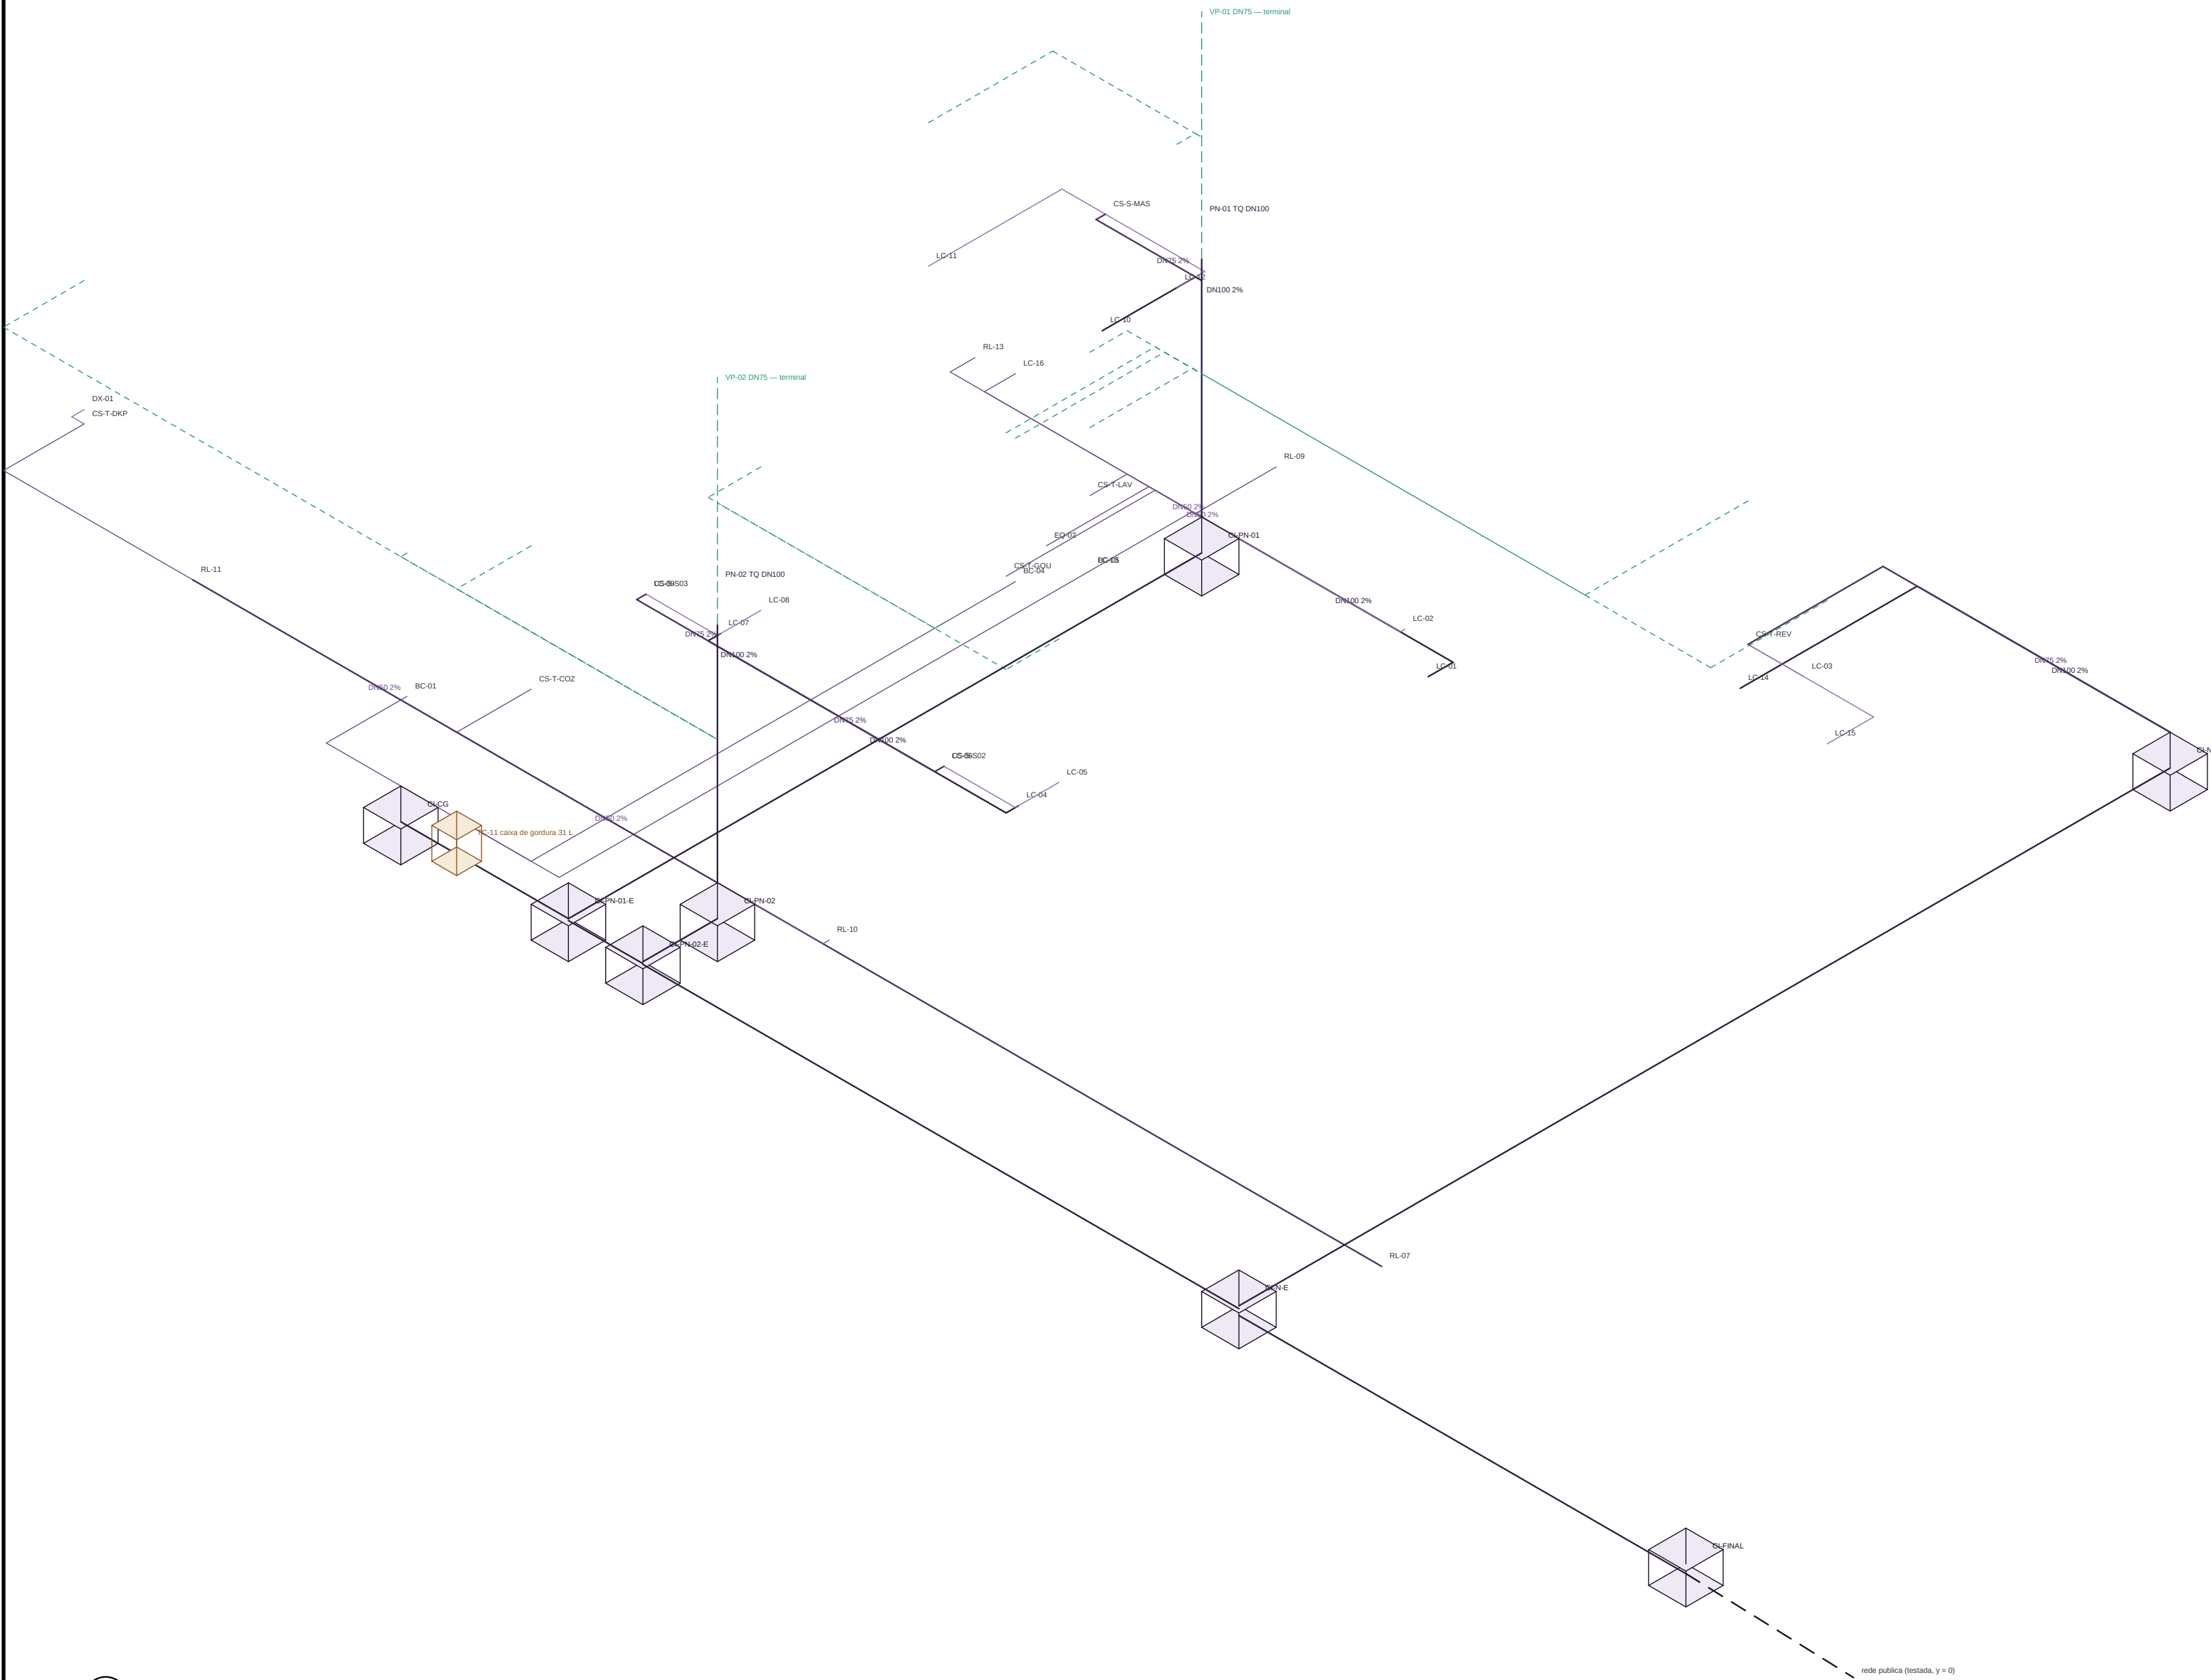


1 ISOMETRICO DE ESGOTO E VENTILACAO
ESCALA 1:75

2 PLANTA DE CAIXAS DE INSPECAO E COLETOR
ESCALA 1:150

COLETOR — COTA DE FUNDO (mm, RN = piso do terreno)

DE	PARA	DN	L/m	1	FUNDO MONT.	FUNDO AIS.	PROF. AIS.
CI-PAV01	CI-PAV02 E	DN100	18,2	2%	—	—	—
CI-PAV02	CI-PAV02 E	DN100	1,2	2%	—	—	—
CIN	CIN E	DN100	18,0	2%	—	—	—
CI-CO	CI-PAV01 E	DN100	2,7	1%	000	027	000
CI-PAV01 E	CI-PAV02 E	DN100	2,2	1%	007	000	007
CI-PAV02 E	CIN E	DN100	9,0	1%	008	000	008
CIN E	CI-FINAL	DN100	7,2	1%	008	007	008

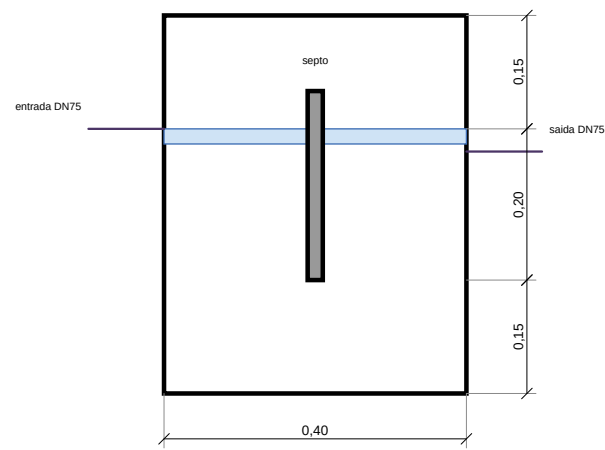

3 CAIXA DE GORDURA 31 L — hermetica, inspecionavel
ESCALA 1:10

PEÇA	AMB	TIPO	DN	UMC	1	L/m	DESTINO	VENT.
LC-01	T-01P	vento	DN100	6	2%	6,3	CI-PAV01	sem
LC-02	T-02P	ventoso	DN65	1	2%	3,9	CI-PAV01	sem
LC-03	T-REV	box	DN65	2	2%	1,1	CS-T-REV	sem
LC-14	T-REV	vento	DN100	6	2%	6,3	CIN	sem
LC-15	T-REV	ventoso	DN65	1	2%	3,3	CS-T-REV	sem
LC-04	S-REV	vento	DN100	6	2%	6,3	PAV02	sem
LC-05	S-REV	ventoso	DN65	1	2%	2,2	CS-S-REV	sem
LC-06	S-REV	box	DN65	2	2%	0,9	CS-S-REV	sem
LC-07	S-REV	vento	DN100	6	2%	6,4	PAV02	sem
LC-08	S-REV	ventoso	DN65	1	2%	2,2	CS-S-REV	sem
LC-09	S-REV	box	DN65	2	2%	0,9	CS-S-REV	sem
LC-10	S-MAV	vento	DN100	6	2%	3,9	PAV01	sem
LC-11	S-MAV	ventoso	DN65	1	2%	3,4	CS-S-MAV	sem
LC-12	S-MAV	box	DN65	2	2%	2,5	CS-S-MAV	sem
LC-13	T-LAV	sanita	DN65	3	2%	2,2	CI-PAV01	sem
LC-16	T-01P	sanita	DN65	3	2%	4,4	CI-PAV01	sem
BC-01	T-02P	sem	DN65	3	2%	4,1	TC-11	sem
BC-04	T-02P	sem	DN65	3	2%	10,8	TC-11	sem
BC-05	T-LAV	sem	DN65	3	2%	12,2	TC-11	sem
EQ-02	T-LAV	sanita	DN65	3	2%	3,0	CI-PAV01	sem
DN-01	T-01P	sanita	DN65	2	2%	0,9	CS-T-01P	sem
CS-T-REV	T-REV	caixa 31L	DN75	4	2%	8,2	CIN	sem
CS-S-REV	S-REV	caixa 31L	DN75	4	2%	4,4	PAV02	sem
CS-S-REV	S-REV	caixa 31L	DN75	4	2%	1,7	PAV02	sem
CS-S-MAV	S-MAV	caixa 31L	DN75	4	2%	2,2	PAV01	sem
CS-T-LAV	T-LAV	caixa 31L	DN65	1	2%	2,2	CI-PAV01	sem
CS-T-COZ	T-COZ	caixa 31L	DN65	1	2%	6,5	CI-PAV02	sem
CS-T-01P	T-01P	caixa 31L	DN65	3	2%	10,4	CI-PAV02	sem
CS-T-02P	T-02P	caixa 31L	DN65	1	2%	3,6	CI-PAV01	sem
RL-13	T-01P	sem	DN65	1	2%	6,3	CI-PAV01	sem
RL-07	T-01P	sem	DN75	1	2%	22,8	CI-PAV02	sem
RL-11	T-LAV	sem	DN75	1	2%	10,1	CI-PAV02	sem
RL-09	T-VRL	sem	DN65	1	2%	1,7	CI-PAV01	sem
RL-10	T-LAV	sem	DN65	1	2%	2,3	CI-PAV02	sem

- NOTAS
- * Retalho de descarga por peça com DN da NBR 5200; comprimento 2% em toda a rede predial (a norma permite 1% em DN100) — a decisão "sem nos entupir" — coleta enterrado a 1%.
 - * Lavatório, box e vaso de cada banheiro capem em caixa 31L (300 x 150 x 150 mm), vaso direto ao tubo de queda ou a caixa de inspeção. 14 ramais de ventilação DN65 onde a altura fica além da distância da tabela 5.
 - * O campo de inspeção 800 x 600 por de cada tubo de queda, terço, encontro e esgoto (de 35 m) fundo final a 600 mm na totalidade, no sentido em que o tubo desce (PDE), a profundidade nos eixos.
 - * Caixa de gordura CGR — caixa de gordura sempre de 31 L a partir de dois pontos, tubos de queda DN100 com terminal de ventilação 300 mm acima da cobertura.

PROJETO PORTO REAL

RESIDENCIA UNIFAMILIAR (MANAUS - AM) | SOUZA TATIANA-PS

PROJETO ARQUITETONICO

ESGOTO SANITARIO E VENTILACAO — ISOMETRICO, CAIXAS E COLETOR

BASE GEOMETRICA	ESCALA	DESCRIÇÃO	PROJETO
União Consolidada	1:75 • 1:150 • 1:10	ESTUDO PRELIMINAR R79	
Projeto (previsão)	FORMATO A1	NAO LIBERADO PARA OBRA	
UNIDADE MESTRE: AM	MAIUS 60505050	SEM ART / INT	62

6/12 REV79