


VERIFICACAO URBANISTICA (H)

| PARAMETRO               | PROJETO      | LIMITE             |    |
|-------------------------|--------------|--------------------|----|
| Taxa de ocupação        | 33,21 %      | até 50 %           | OK |
| Coef. de aproveitamento | 0,372        | até 1,00           | OK |
| Galvao                  | 2 pavimentos | até 4              | OK |
| Recuo frontal           | 7200 mm      | conforme 50/00 (H) | OK |
| Recuo lateral esq.      | 2400 mm      | sem limite no lado | OK |
| Recuo lateral dir.      | 3000 mm      | até 3000 mm        | OK |
| Recuo de fundo          | 13800 mm     | até 5000 mm        | OK |

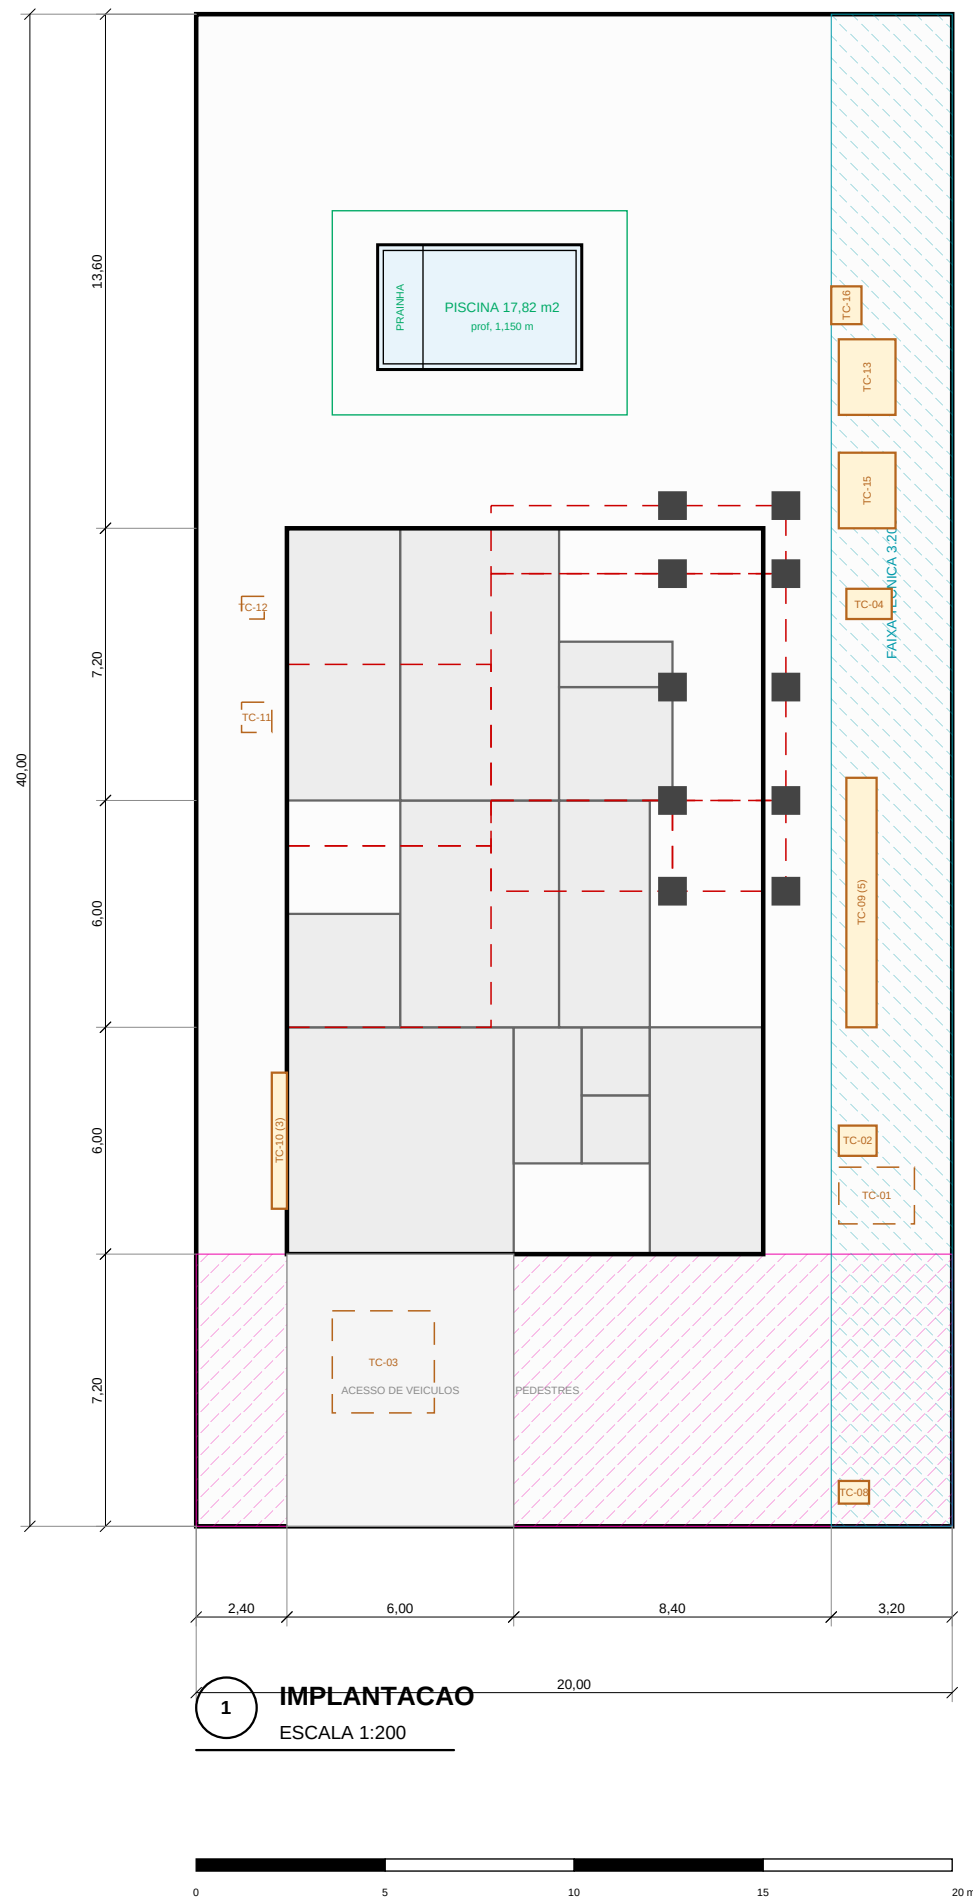

- NOTAS
- \* Lote 25.000 x 40.000 mts = 800.00 m2.
  - \* Recuo frontal 7.200 / lateral esq. 2.400 / lateral dir. 3.000 / fundo 13.800 mts.
  - \* Parametros do SUD Tatuá/Tatuá-Açu aos Registros (H) - pendentes controle de uso do solo.
  - \* Sem muro frontal, mural lateral e de fundo 9 x 2.200 mts.

PROJETO PORTO REAL

RESIDENCIA UNIFAMILIAR (MANSÃO - AM) | SOUS TATUÁ-PA

PROJETO ARQUITETONICO

IMPLANTACAO E SITUACAO

|                      |                       |                         |               |
|----------------------|-----------------------|-------------------------|---------------|
| BASE GEOMETRICA      | ESCALA                | EMISSAO                 | PROJECIA      |
| Unia Consolidada     | 1:200                 | ESTUDIO PRELIMINAR R59  | 01            |
| em R52 (previsão)    | FORMATO A1            | IMAO LIBERADO PARA OBRA |               |
| UNIDADE: METROS - MM | MILIMETROS (50/00/00) | SEM ART / RNT           | 06-48 REV 003 |