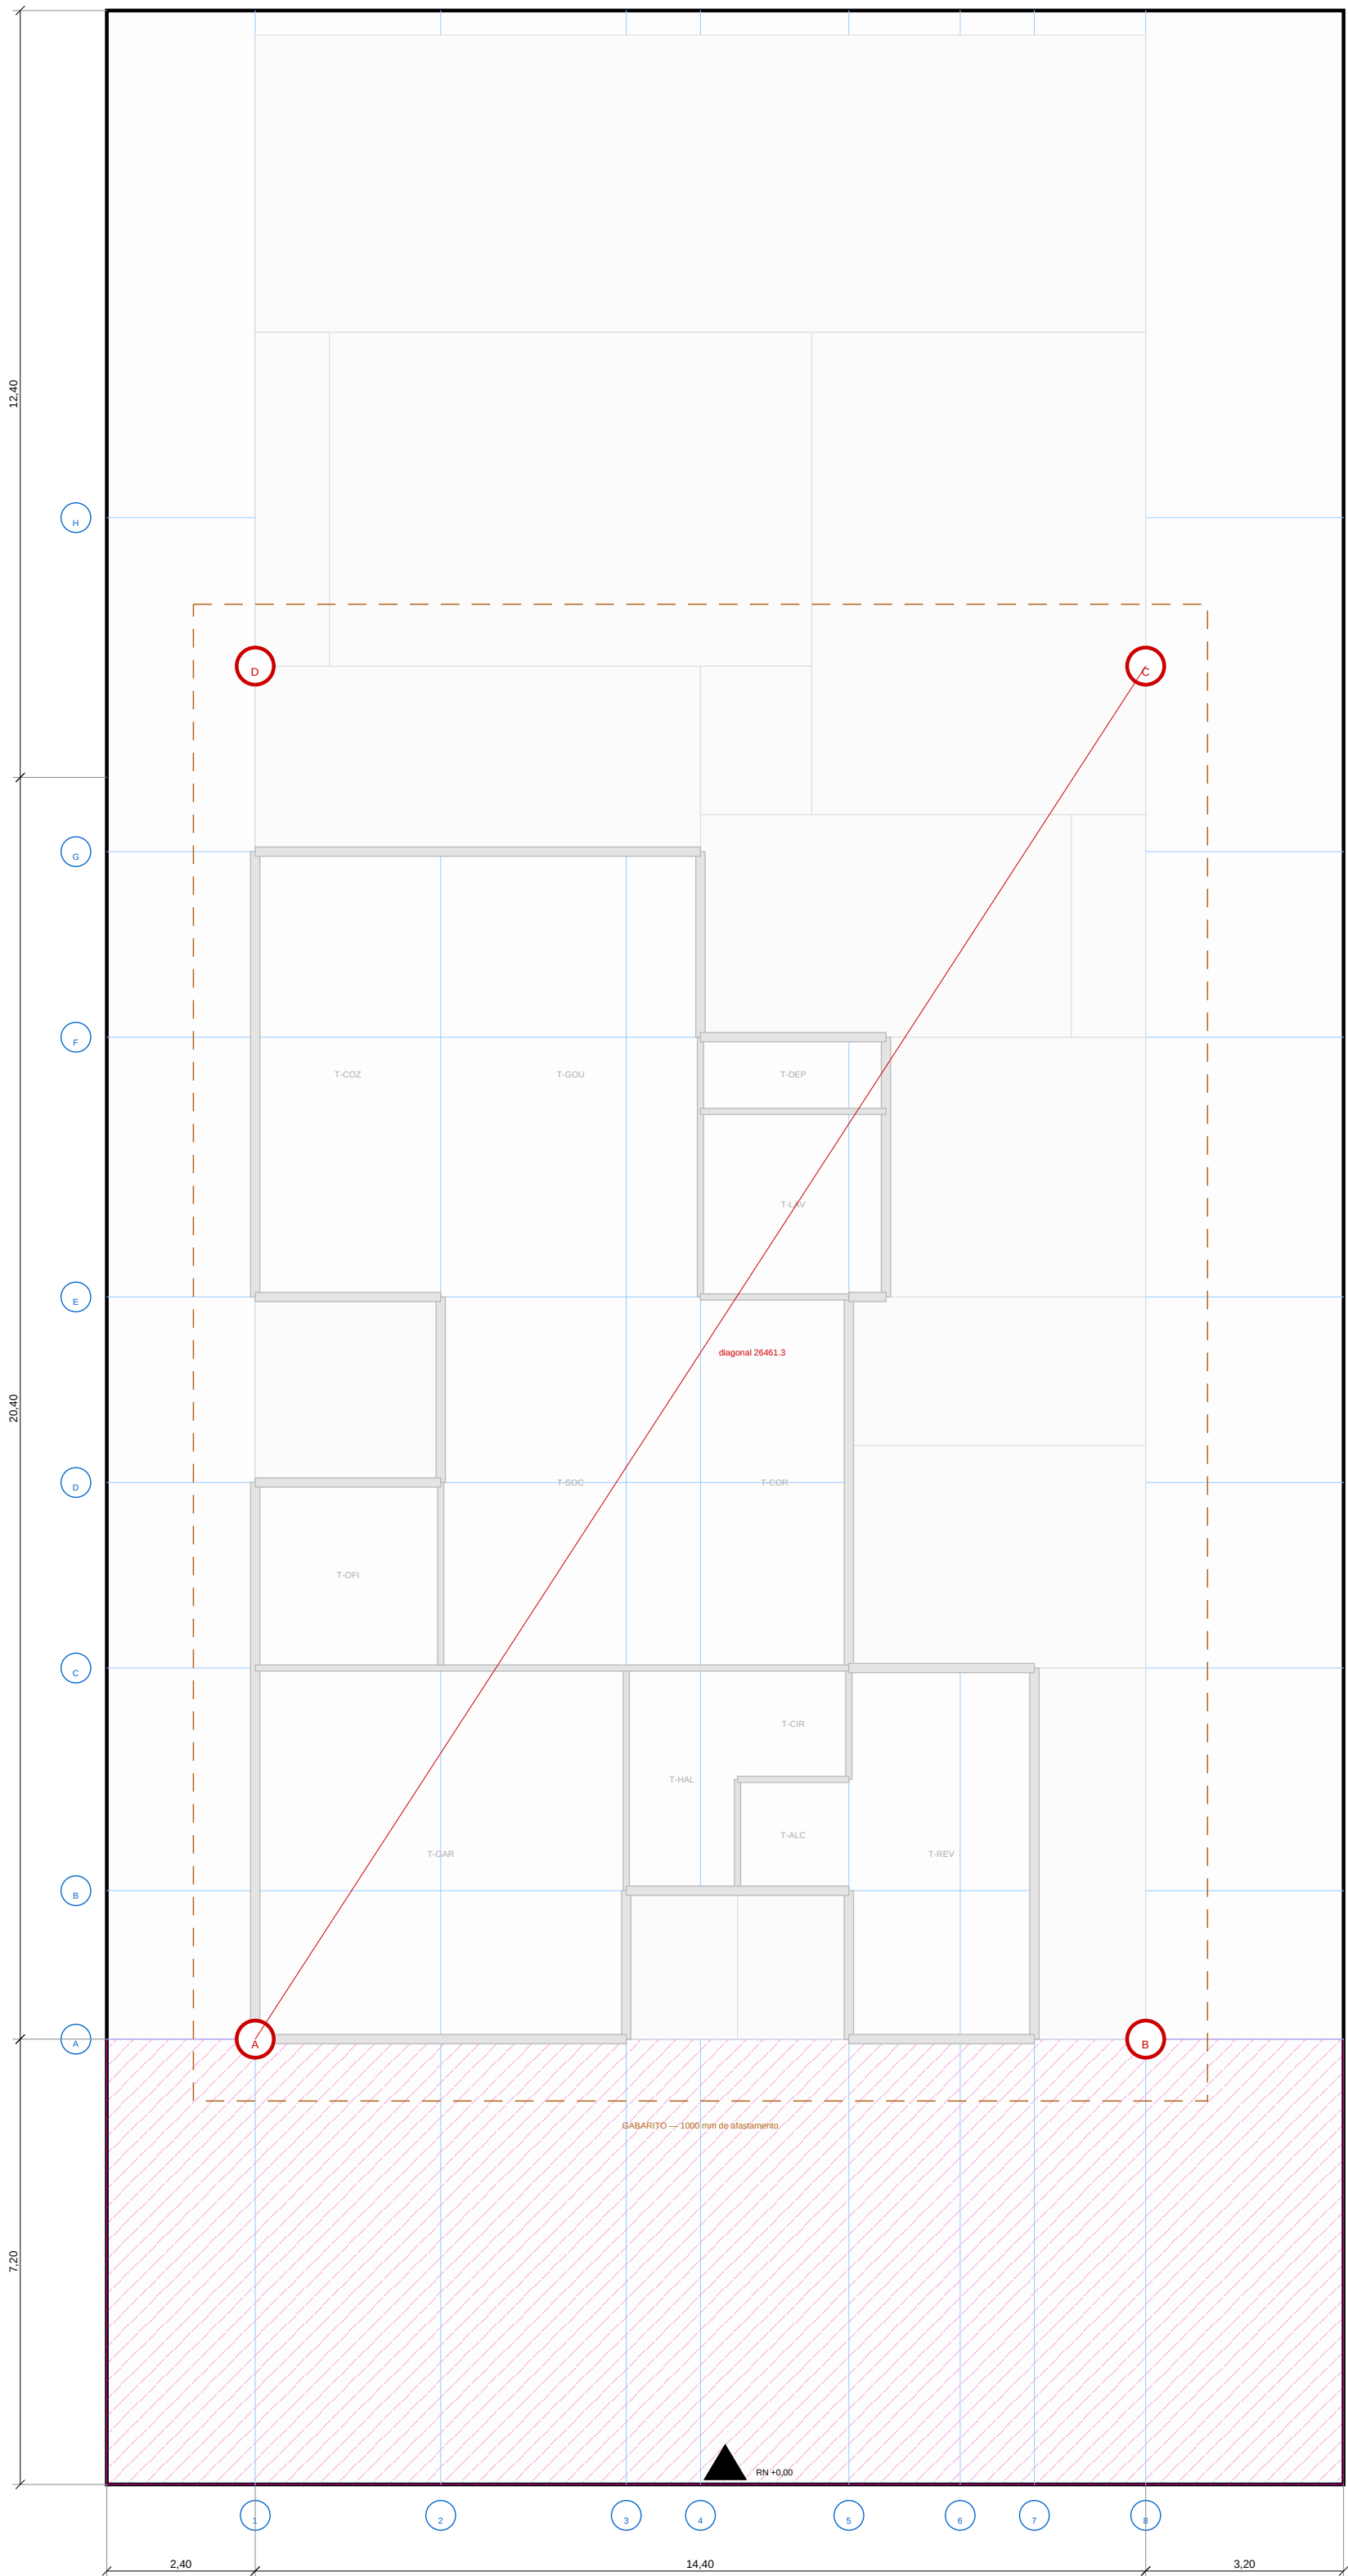


COORDENADAS DOS CANTOS (mm)

CANTO	X	Y	DIVISA SUL	DIVISA NORTE	TESTADA	QUILÔMETRO	DIAGONAL
A	2400	7200	2400	17600	7200	32800	26461,3
B	18800	7200	18800	3200	7200	32800	26461,3
C	18800	28400	18800	3200	28400	18800	26461,3
D	2400	28400	2400	17600	28400	18800	26461,3

PROCEDIMENTO DE LOCACAO

#	PASSO	CRITERIO DE ACABO
1	Conferir as divisas com o material de base	divergencia maxima de 10 mm interromper a locacao
2	Instalar o RMC marca de concreto 200 x 200 x 100 mm, fora da area de obra	fora da area de obra
3	Montar o gabarito a 1000 mm do canteiro	perguntas 75 x 75 e tubos 20 x 100
4	Marcar os eixos X (1) a (10) e Y (1) a (10) no gabarito	linha coordenada maxima de 200 mm
5	Cotar cada canto das QUAS dividas	verificar em cada canto, erro de cada lado
6	Conferir a diagonal A-C	26461,3 mm com tolerancia de 10 mm
7	Conferir o quadrado por 3-4-5 em cada canto	antes de qualquer concretagem
8	Registrar em ata com foto e modelo	gabarito continuo nos dois lados da obra, conferencia

EIXOS MODULARES

DIRECAO	PROJECAO (mm)
X (1) a (10)	2400 5400 8400 9600 12600 13800 15000 16200
Y (1) a (10)	7200 9600 12000 14400 16800 19200 21600 24000 26400 28800
Módulo	principal 600 mm - submódulo 300 mm
Origem	canto frontal esquerdo da base
Unidade	módulo

NOTAS

- Locação e o único documento em que o erro não tem contagem baseada a casa mil do lugar.
- Cada canto e cotado das QUAS dividas, nunca em cotagem acumulada — erro de cada soma, erro de referencia independente não.
- Conferencia obrigatória pela diagonal 26461,3 mm entre A e C antes de concretar o radier.
- Ata no ato de locação, assinada por todos os envolvidos (TC-OB, caso não seja) e pelo responsável da obra.

PROJETO PORTO REAL

RESIDENCIA UNIFAMILIAR (MANSÃO) - AM | SOBR TATIANA-PS

PROJETO ARQUITETONICO

LOCACAO DE OBRA E GABARITO

BASE GEOMETRICA Linha Consolidada Projeto (previsão) Unidade: metro, milímetro	ESCALA 1:100 FORMATO A1 Módulo: 600/300/150	EXIBICAO ESTUDO PRELIMINAR R59 Linha Libertada para Obra SEM ART / RNT	PROJECÇÃO 31 06-48 REV 003
---	--	---	----------------------------------