


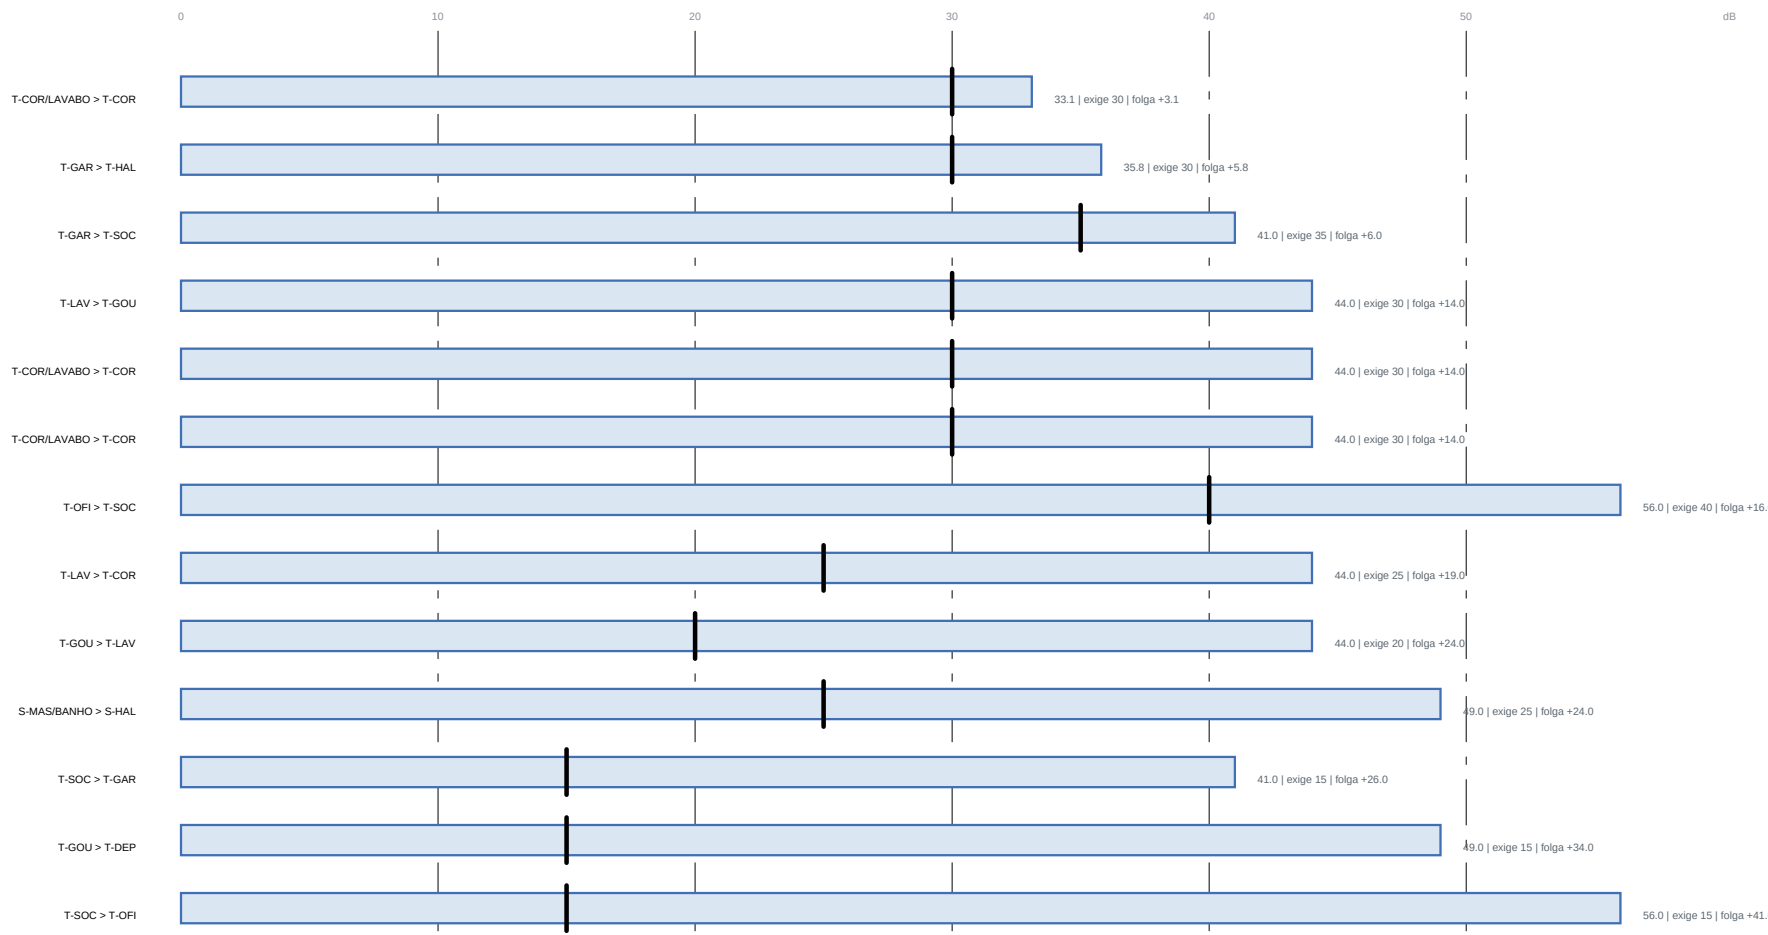

Barra = isolamento obtido; traço vertical = exigência (valor da fonte menos nível do receptor, NBR 15102)

O QUE MUDOU EM R52

ONDE	ANTES	DEPOIS	POR QUE
Banho compartilhado + hall de entrada	porta de correr (Rw 25) — conjunto de 20,2 dB	parede CEGSA, 44 dB	o acrílico de vidro passou para o circulation
Banho compartilhado + quarto eventual	porta com (Rw 25) — conjunto de 25,5 dB, exigia 25	parede CEGSA, 44 dB	era a por passagem da casa, e não era a vidro
Hall + garagem	porta com — 36,9 dB, exigia 30	PDS lãminas vitadas — 36,9 dB	porta entre garagem e casa tem lãminas isolantes para ser mágica
Banho compartilhado + circulation	não havia porta	PDS lãminas vitadas — 35,7 dB, exigia 25	único acesso do banho, e abria para fora
Bloco do chuveiro	encostado na parede do hall	canto arredondado, toldo e janela alta	consequência da porta nova, a regra dos 900 mm de bloco respondeu a primeira tentativa

TABELAS ADOTADAS

ITEM	VALOR	FONTE
Fonte: caixa sanitária	75 dB(A)	prática corrente de acústica
Fonte: bloco do chuveiro	70 dB(A)	prática corrente de acústica
Fonte: cozinha e gourmet	70 dB(A)	prática corrente de acústica
Fonte: sala e jantar	70 dB(A)	prática corrente de acústica
Fonte: garagem	70 dB(A)	prática corrente de acústica
Fonte: máquina de lavar e secar	70 dB(A)	prática corrente de acústica
Fonte: oficina	60 dB(A)	prática corrente de acústica
Limite: banho	45 dB(A)	NBR 15102:2017 (circulação e entrada adjacente)
Limite: circulation	45 dB(A)	NBR 15102:2017 (circulação e entrada adjacente)
Limite: cozinha	45 dB(A)	NBR 15102:2017 (circulação e entrada adjacente)
Limite: dormitório	55 dB(A)	NBR 15102:2017 (circulação e entrada adjacente)
Limite: escritório	55 dB(A)	NBR 15102:2017 (circulação e entrada adjacente)
Limite: entrada	45 dB(A)	NBR 15102:2017 (circulação e entrada adjacente)
Limite: estar	45 dB(A)	NBR 15102:2017 (circulação e entrada adjacente)
Limite: sala	45 dB(A)	NBR 15102:2017 (circulação e entrada adjacente)
Limite: oficina	55 dB(A)	NBR 15102:2017 (circulação e entrada adjacente)
Limite: serviço	55 dB(A)	NBR 15102:2017 (circulação e entrada adjacente)
Fonte: academia	Pin 25 dB	Nota de mercado declarada
Fonte: cinema	Pin 25 dB	Nota de mercado declarada
Fonte: sala	Pin 25 dB	Nota de mercado declarada
Fonte: sala de estar	Pin 25 dB	Nota de mercado declarada
Fonte: sala de jantar	Pin 25 dB	Nota de mercado declarada
Fonte: sala de estar	Pin 25 dB	Nota de mercado declarada

NOTAS

1 Esta planilha serve para o proprietário perguntar o que 100 verificações não sabem responder: quem entra na casa ouve o chuveiro do banheiro da entrada?

2 Ouviu. A parede era bloco (Rw 1), Pin 44 e a porta era de correr (Rw 25), o conjunto entregava 20 dB. Em acústica o bloco DOMINA — não se faz média aritmética do isolamento, se soma energia que passa.

3 Isolamento no seu nível ENTRE zonas. Dentro da file social o nível não é definido, é o programa.

4 O aditivo igual ao R52 (previsão declarada), não é pre-verificação de projeto, não entra no campo da NBR 15102-3.

PROJETO PORTO REAL

RESIDENCIA UNIFAMILIAR (MAGALHÃS - AM) | 100% TATIANA-PS

PROJETO ARQUITETÔNICO

DESEMPENHO ACUSTICO ENTRE AMBIENTES

BASE GEOMÉTRICA	ESCALA	EMISSÃO	PROVA
Lista Consolidada	s/ escala	ESTUDO PRELIMINAR R59	
Pin R52 (previsão)	FORMATO A1	IMÓVEL LIBERADO PARA OBRA	39
UNIDADE MÉTRICA: mm	MILHAR 600/500/300	SEM ART / RNT	06.48 REV 003