



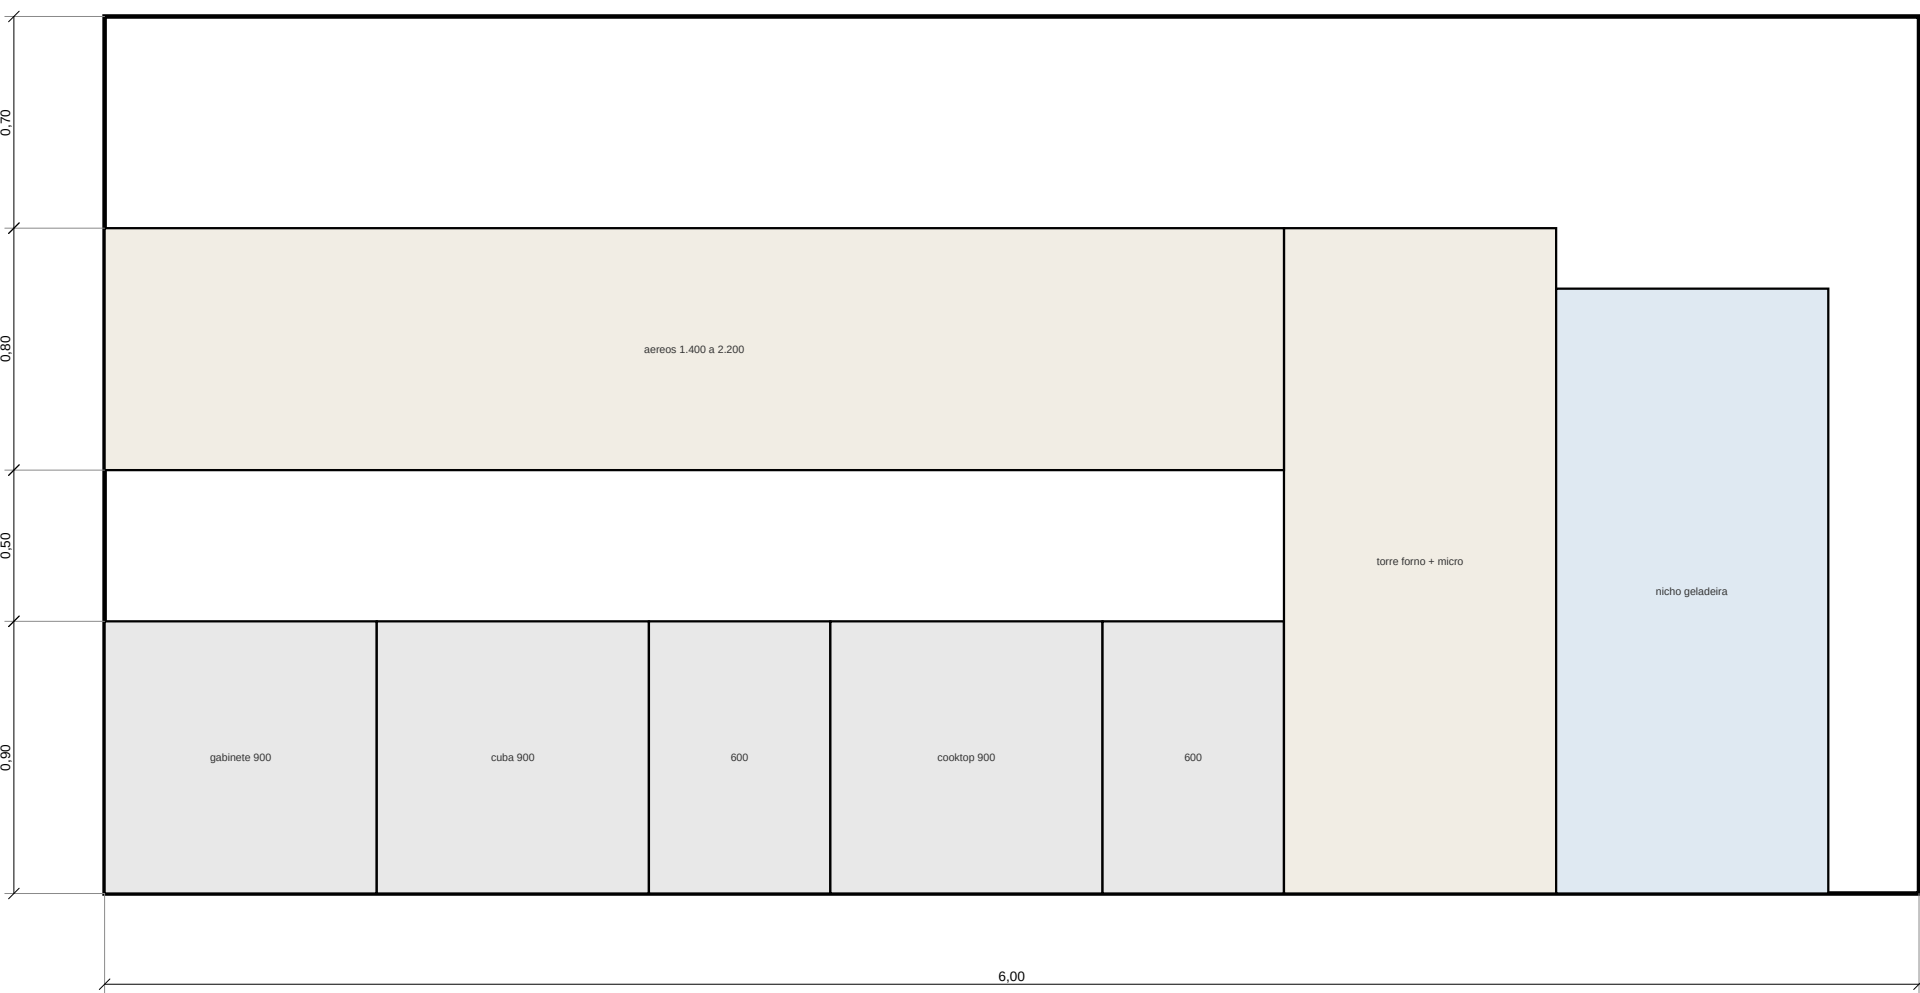


COZINHA — PAREDE SUL (BANCADA PRINCIPAL)

- bancada em granito, 600 mm de profundidade
- circulação livre mínima de 1.000 mm (despejada 1.100)
- 6 unidades de bancada a 1.500 mm

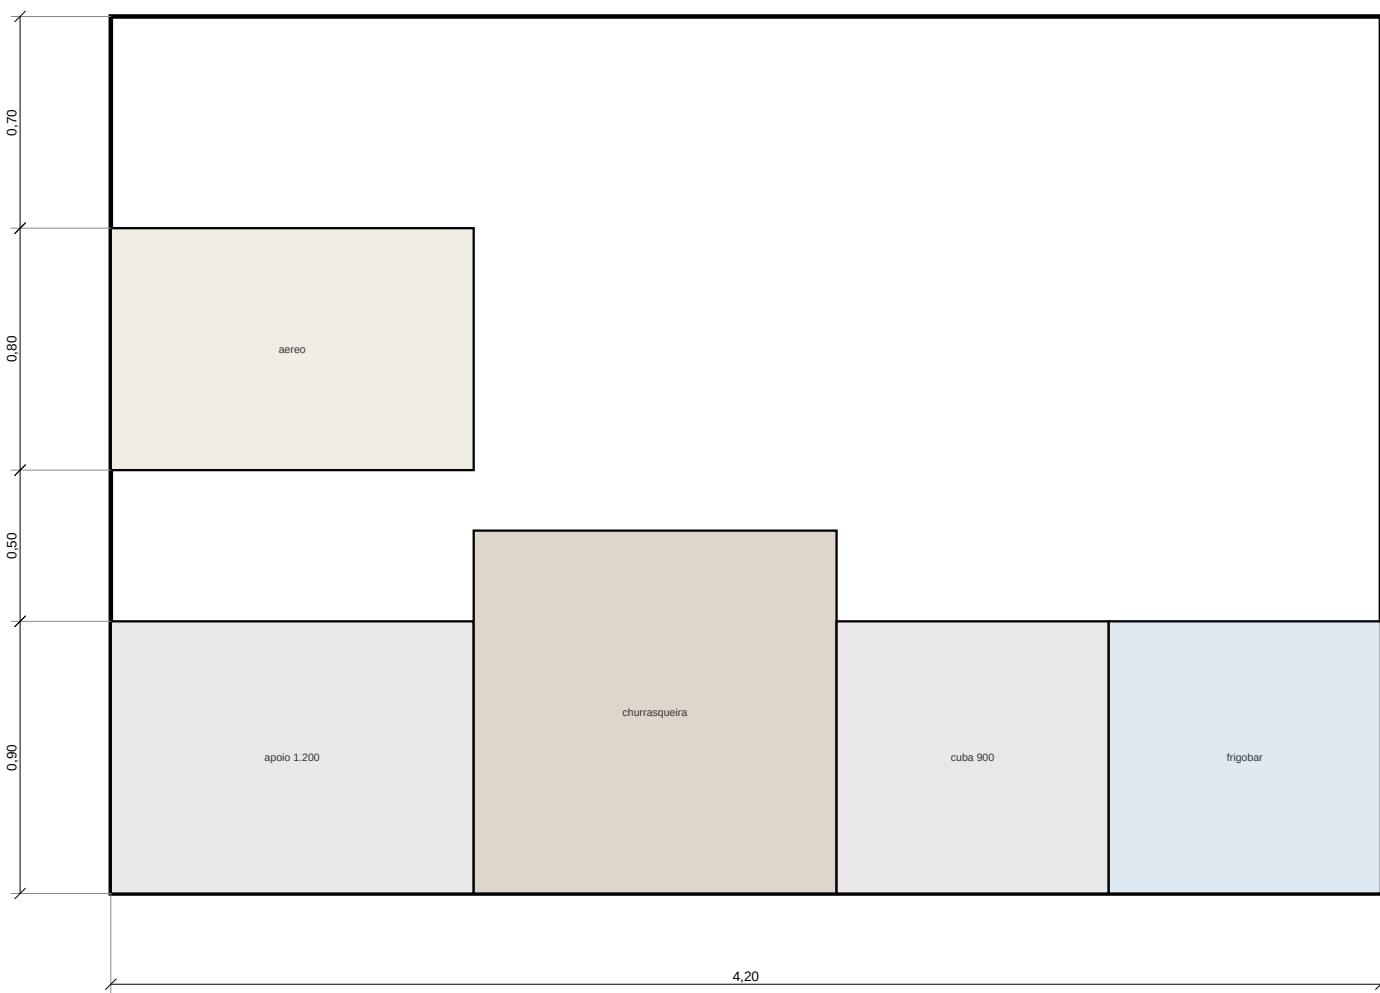

GOURMET — BANCADA E CHURRASQUEIRA

- ilha com vazão mínima de 20 litros por hora de volume
- bancada integrada e cozinha pelo lado norte

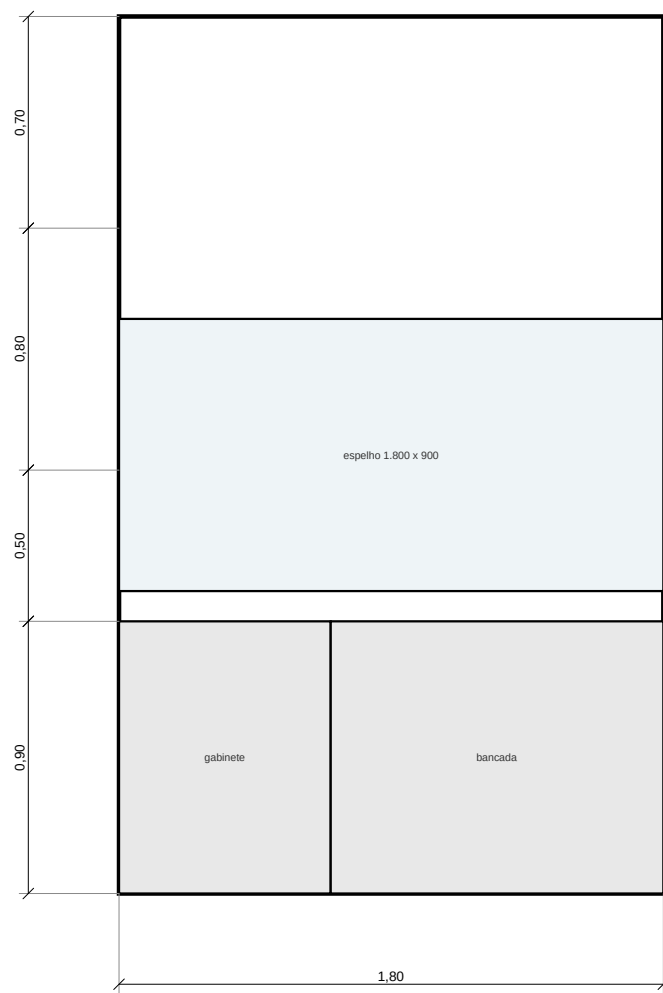


LAVABO SOB A ESCADA — PAREDE DA BANCADA

- reforço embutido para barra de apoio da NBR 9050
- porta de correr de 900 mm barra e círculo de giro




SUITE MASTER — BANHO

- revestimento cerâmico até o teto na área molhada

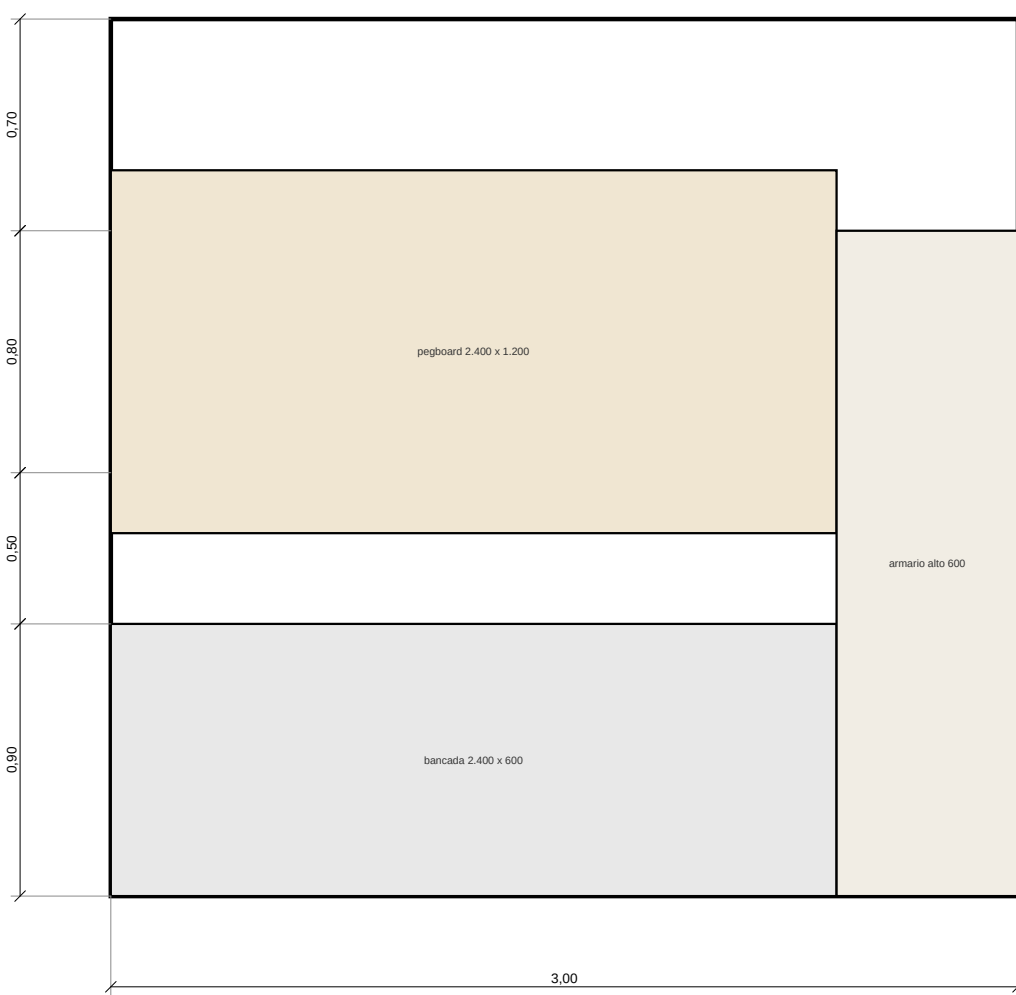

OFICINA — BANCADA DE TRABALHO

- 4 unidades de bancada, círculo comum 20 A e reserva 32 A (p)
- iluminação geral 500 lux e 800 lux sobre a bancada, 4.000 K
- área central livre de 1.200 x 1.800 mm

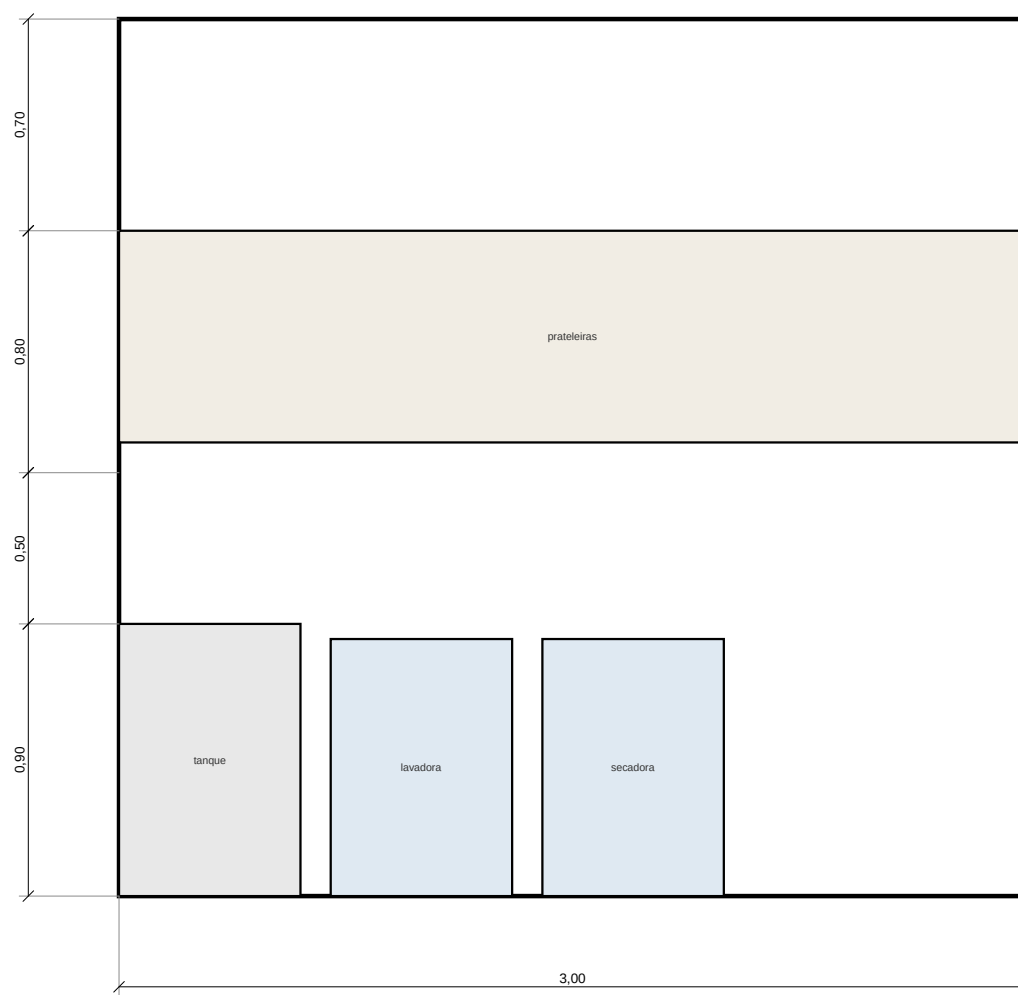

LAVANDERIA — TANQUE E MÁQUINAS

- base antiderrapante sob as máquinas, tudo elevado
- grimaltes na parede de apoio, longe da oficina

- NOTAS
- Visão de parede, base para marcenaria, revestimento e pontos elétricos.
 - Modulo de marcenaria em 300 / 450 / 600 / 900 mm, conforme o briefing.
 - Bancadas a 900 mm, altura superior de 1.400 a 2.200 mm.
 - Altura de bancada integrada a central sobre o próprio eletro.

PROJETO PORTO REAL

RESIDENCIA UNIFAMILIAR (MANSÃO - AM) | SOBR TATIANA-PS

PROJETO ARQUITETONICO

ELEVACOES INTERNAS

BASE GEOMETRICA
Linha Consolidada
Projeto (preliminar)
UNIDADE: METRO: mm

ESCALA
1:25
FORMATO A1
MILHA 455/555/555

EXATIDAO
ESTUDO PRELIMINAR RTO
TWO LIBERADO PARA DESA
SEM ART / RNT

PROVA
15
de 54 REVIZO