

- downlight embudo
- ⊕


plafon de sobrepor (forno perfurado / aparente)
- pendente (je-direito duplo)
- linear do tafeia (bancado, closet, mesa)
- arandela de espelho
- balizador de escada
- 2700 K
- 3000 K
- 4000 K
- forno absorvente perfurado (afa 0.70)
- sem forno (panel PPR aparente)

LUMINOTECNICA POR AMBIENTE — METODO DOS LUMENS

AMB	USO	m2	altura	dimens	LUMINOSIDA	kw	W
T-CORR	apoi	35.5	75	108	4 x Plafon LED de sobrepor 24 W	4000 K	96
T-AL	circulacao	6.5	100	151	2 x Downlight LED embudo 18 W	3000 K	36
T-ALC	recep	3.2	100	151	1 x Downlight LED embudo 18 W	2700 K	18
T-CORR	circulacao	3.1	100	151	1 x Downlight LED embudo 18 W	3000 K	18
T-DEV	recep	12.7	100	200	5 x Downlight LED embudo 18 W	2700 K	90
T-CORR	abaco	9.9	500	151	4 x Downlight LED embudo 18 W	4000 K	144
T-SOC	soci	25.2	200	242	8 x Downlight LED embudo 24 W	3000 K	144
T-CORR	escada	12.2	100	188	2 x Pendente LED de je-direito dup	3000 K	90
T-CORR	cocina	17.8	300	353	7 x Downlight LED embudo 24 W	4000 K	168
T-CORR	soci	30.2	200	208	6 x Plafon LED de sobrepor 24 W	3000 K	144
T-LAV	soci	9.0	200	245	4 x Downlight LED embudo 18 W	4000 K	72
T-DEP	soci	3.5	200	272	2 x Downlight LED embudo 18 W	4000 K	36
S-SOC	recep	21.6	100	182	5 x Downlight LED embudo 18 W	2700 K	90
S-SOC	recep	21.6	100	182	5 x Downlight LED embudo 18 W	2700 K	90
S-AL	circulacao	11.5	100	120	2 x Downlight LED embudo 24 W	3000 K	40
S-LOU	soci	7.2	200	350	4 x Downlight LED embudo 24 W	3000 K	96
S-MAS	recep	21.6	100	182	6 x Downlight LED embudo 18 W	2700 K	90
S-SOC-BANHO	banho	4.3	200	233	2 x Downlight LED embudo 18 W	3000 K	36
S-SOC-BANHO	banho	4.3	200	233	2 x Downlight LED embudo 18 W	3000 K	36
T-CORR-DEPENSA	soci	9.9	200	398	2 x Downlight LED embudo 24 W	4000 K	48
T-RECEBAMANO	banho	4.1	200	233	2 x Downlight LED embudo 18 W	3000 K	36
T-CORR-LAVAMANO	banho	2.1	200	227	1 x Downlight LED embudo 18 W	3000 K	18
S-MAS-BANHO	banho	10.8	200	251	4 x Downlight LED embudo 18 W	3000 K	72
S-MAS-CLOSET	closet	9.0	200	245	4 x Downlight LED embudo 18 W	3000 K	72
S-MAS-OFFICE	office	5.4	300	112	4 x Downlight LED embudo 24 W	4000 K	96

LUZ DE TAREFA

CD	ON	TIPO	QTD	kw
L1-BC-01	bancada BC-01 (T-CORR)	linear	2.1 m	4000 K
L1-BC-02	bancada BC-02 (T-CORR)	linear	1.8 m	4000 K
L1-BC-03	bancada BC-03 (T-CORR)	linear	1.5 m	4000 K
L1-BC-04	bancada BC-04 (T-CORR)	linear	3.0 m	4000 K
L1-BC-05	bancada BC-05 (T-CORR)	linear	2.4 m	4000 K
L1-LC-01	espelho do banheiro LC-01 (T-CORR)	arandela	1	4000 K
L1-LC-02	espelho do banheiro LC-02 (T-REV)	arandela	1	4000 K
L1-LC-03	espelho do banheiro LC-03 (S-SOC)	arandela	1	4000 K
L1-LC-04	espelho do banheiro LC-04 (S-SOC)	arandela	1	4000 K
L1-LC-05	espelho do banheiro LC-05 (S-MAS)	arandela	2	4000 K
L1-S-MAS-CLOSET	closet do S-MAS	linear	3.0 m	3000 K
L1-S-MAS-OFFICE	mesa do office do S-MAS	linear	1.2 m	4000 K
L1-RECEBAMANO	escada (Recebamano)	balizadora	6	3000 K

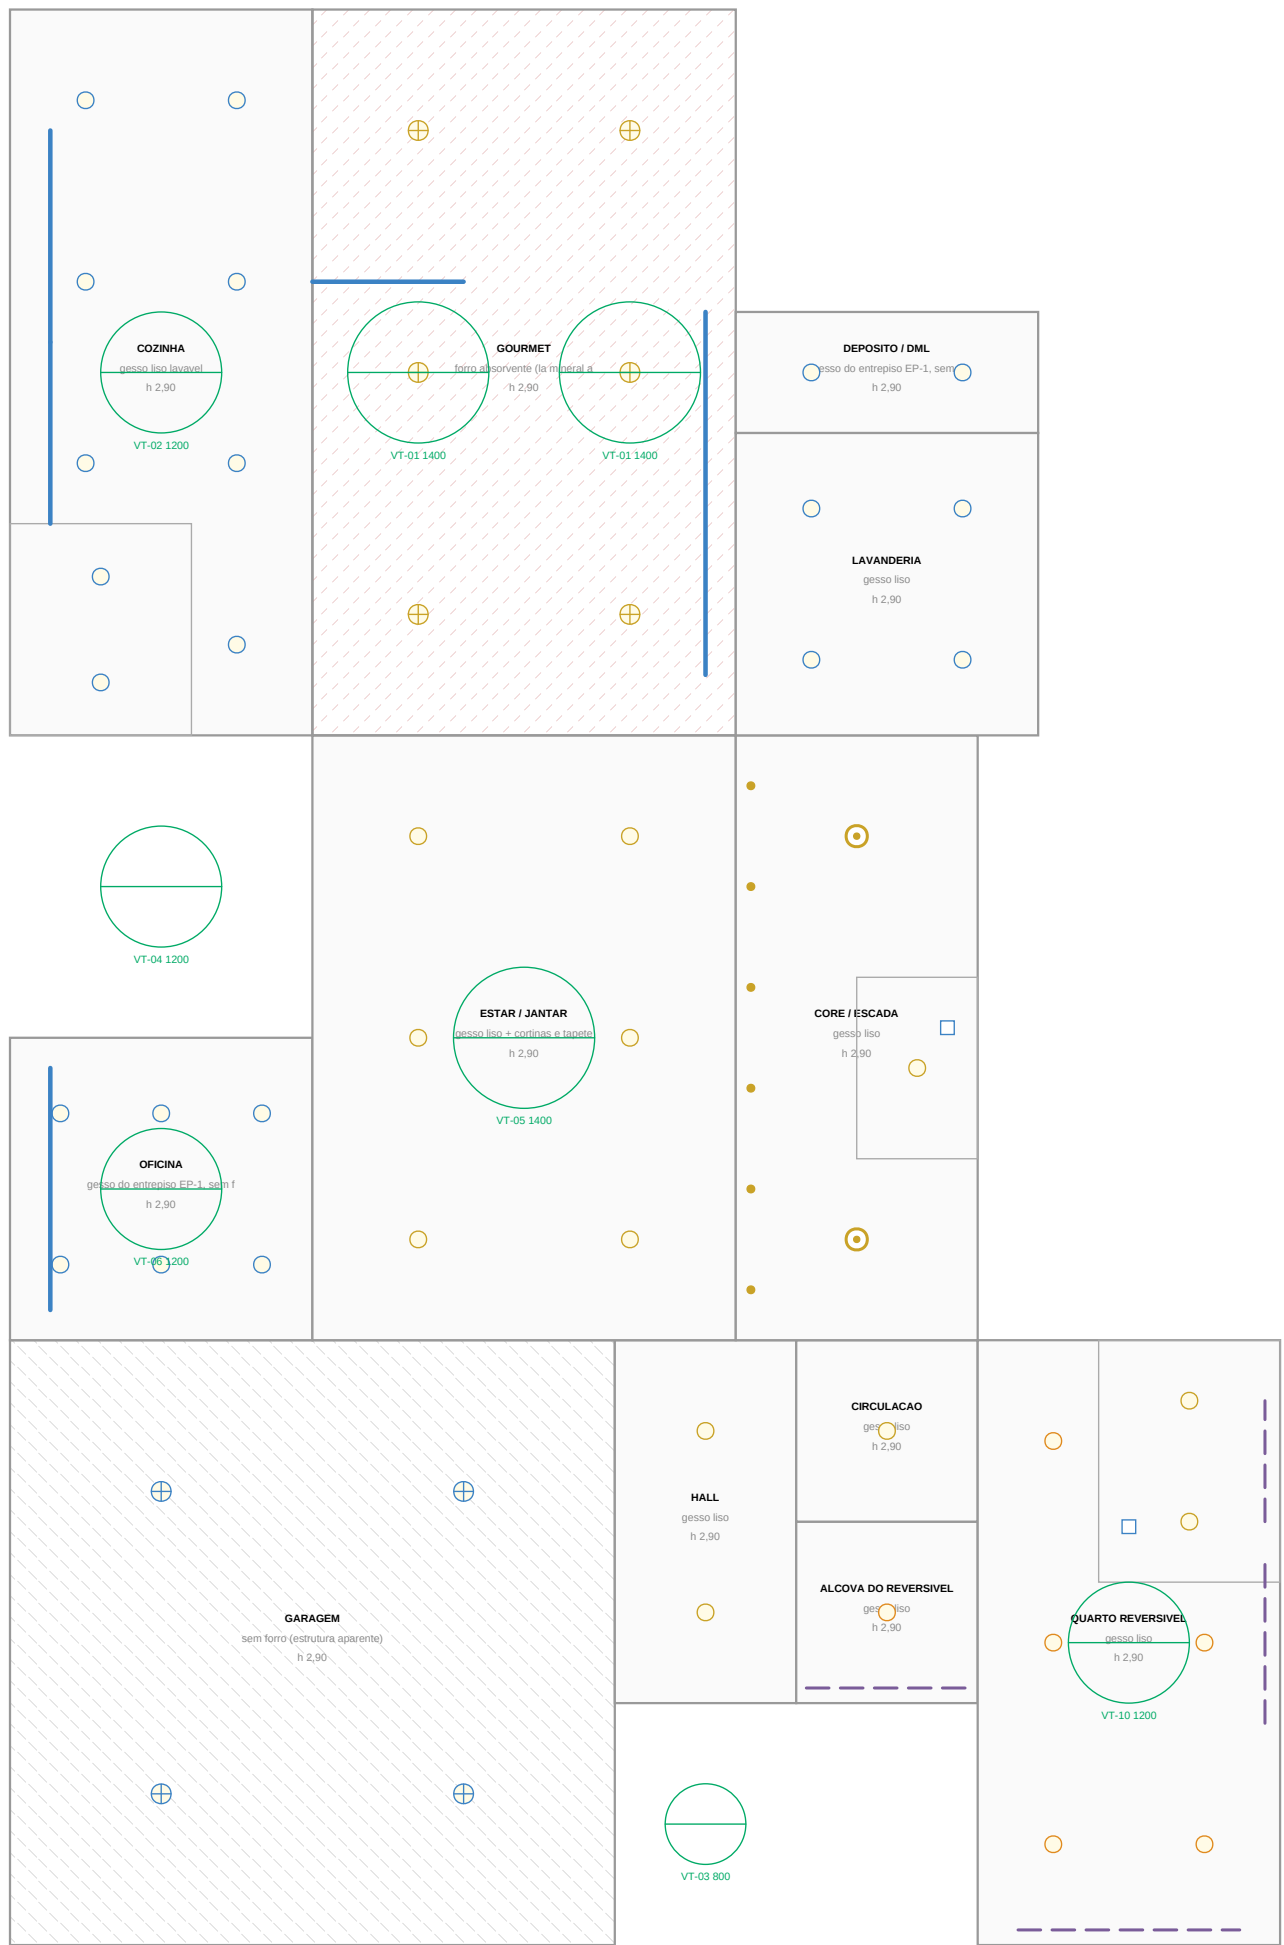

1 FORRO REFLETIDO — TERREO
ESCALA 1:75



2 FORRO REFLETIDO — SUPERIOR
ESCALA 1:75

- NOTAS
- Planta refletida: vista do forno projetada no plano horizontal, terreno e superior.
 - Luminarias pelo METODO DOS LUMENS por ambiente (NBR 9050:2020 / NBR 5413), medida de uniformidade SHU 1.2.
 - 18 pontos gerais, 12 pontos de tarefa, 3074 W (3.3 kWh).
 - Cor: 2.700 K interno, 3.000 K social e circulacao, 4.000 K cocina, banho e hall.
 - 11 embelezamento de teto (pontos), diametro em mm.
 - Curtina (placado inox) instalada de 150 mm ao longo da janela de todo ambiente interno.

PROJETO PORTO REAL

RESIDENCIA UNIFAMILIAR (MANSO - AM) | 5000 TUBARAO-AM

PROJETO ARQUITETONICO

PLANTA DE FORRO E ILUMINACAO

BASE GEOMETRICA União Consolidada Projeto (preliminar) Unidade (preliminar)	ESCALA 1:75 FORMATO A1 MILIMETROS (1:75)	EMISSAO ESTUDO PRELIMINAR RTO Linha (preliminar) SEM ART / RNT	PROJETO 16 04/24 REV 02
--	---	---	-------------------------------