



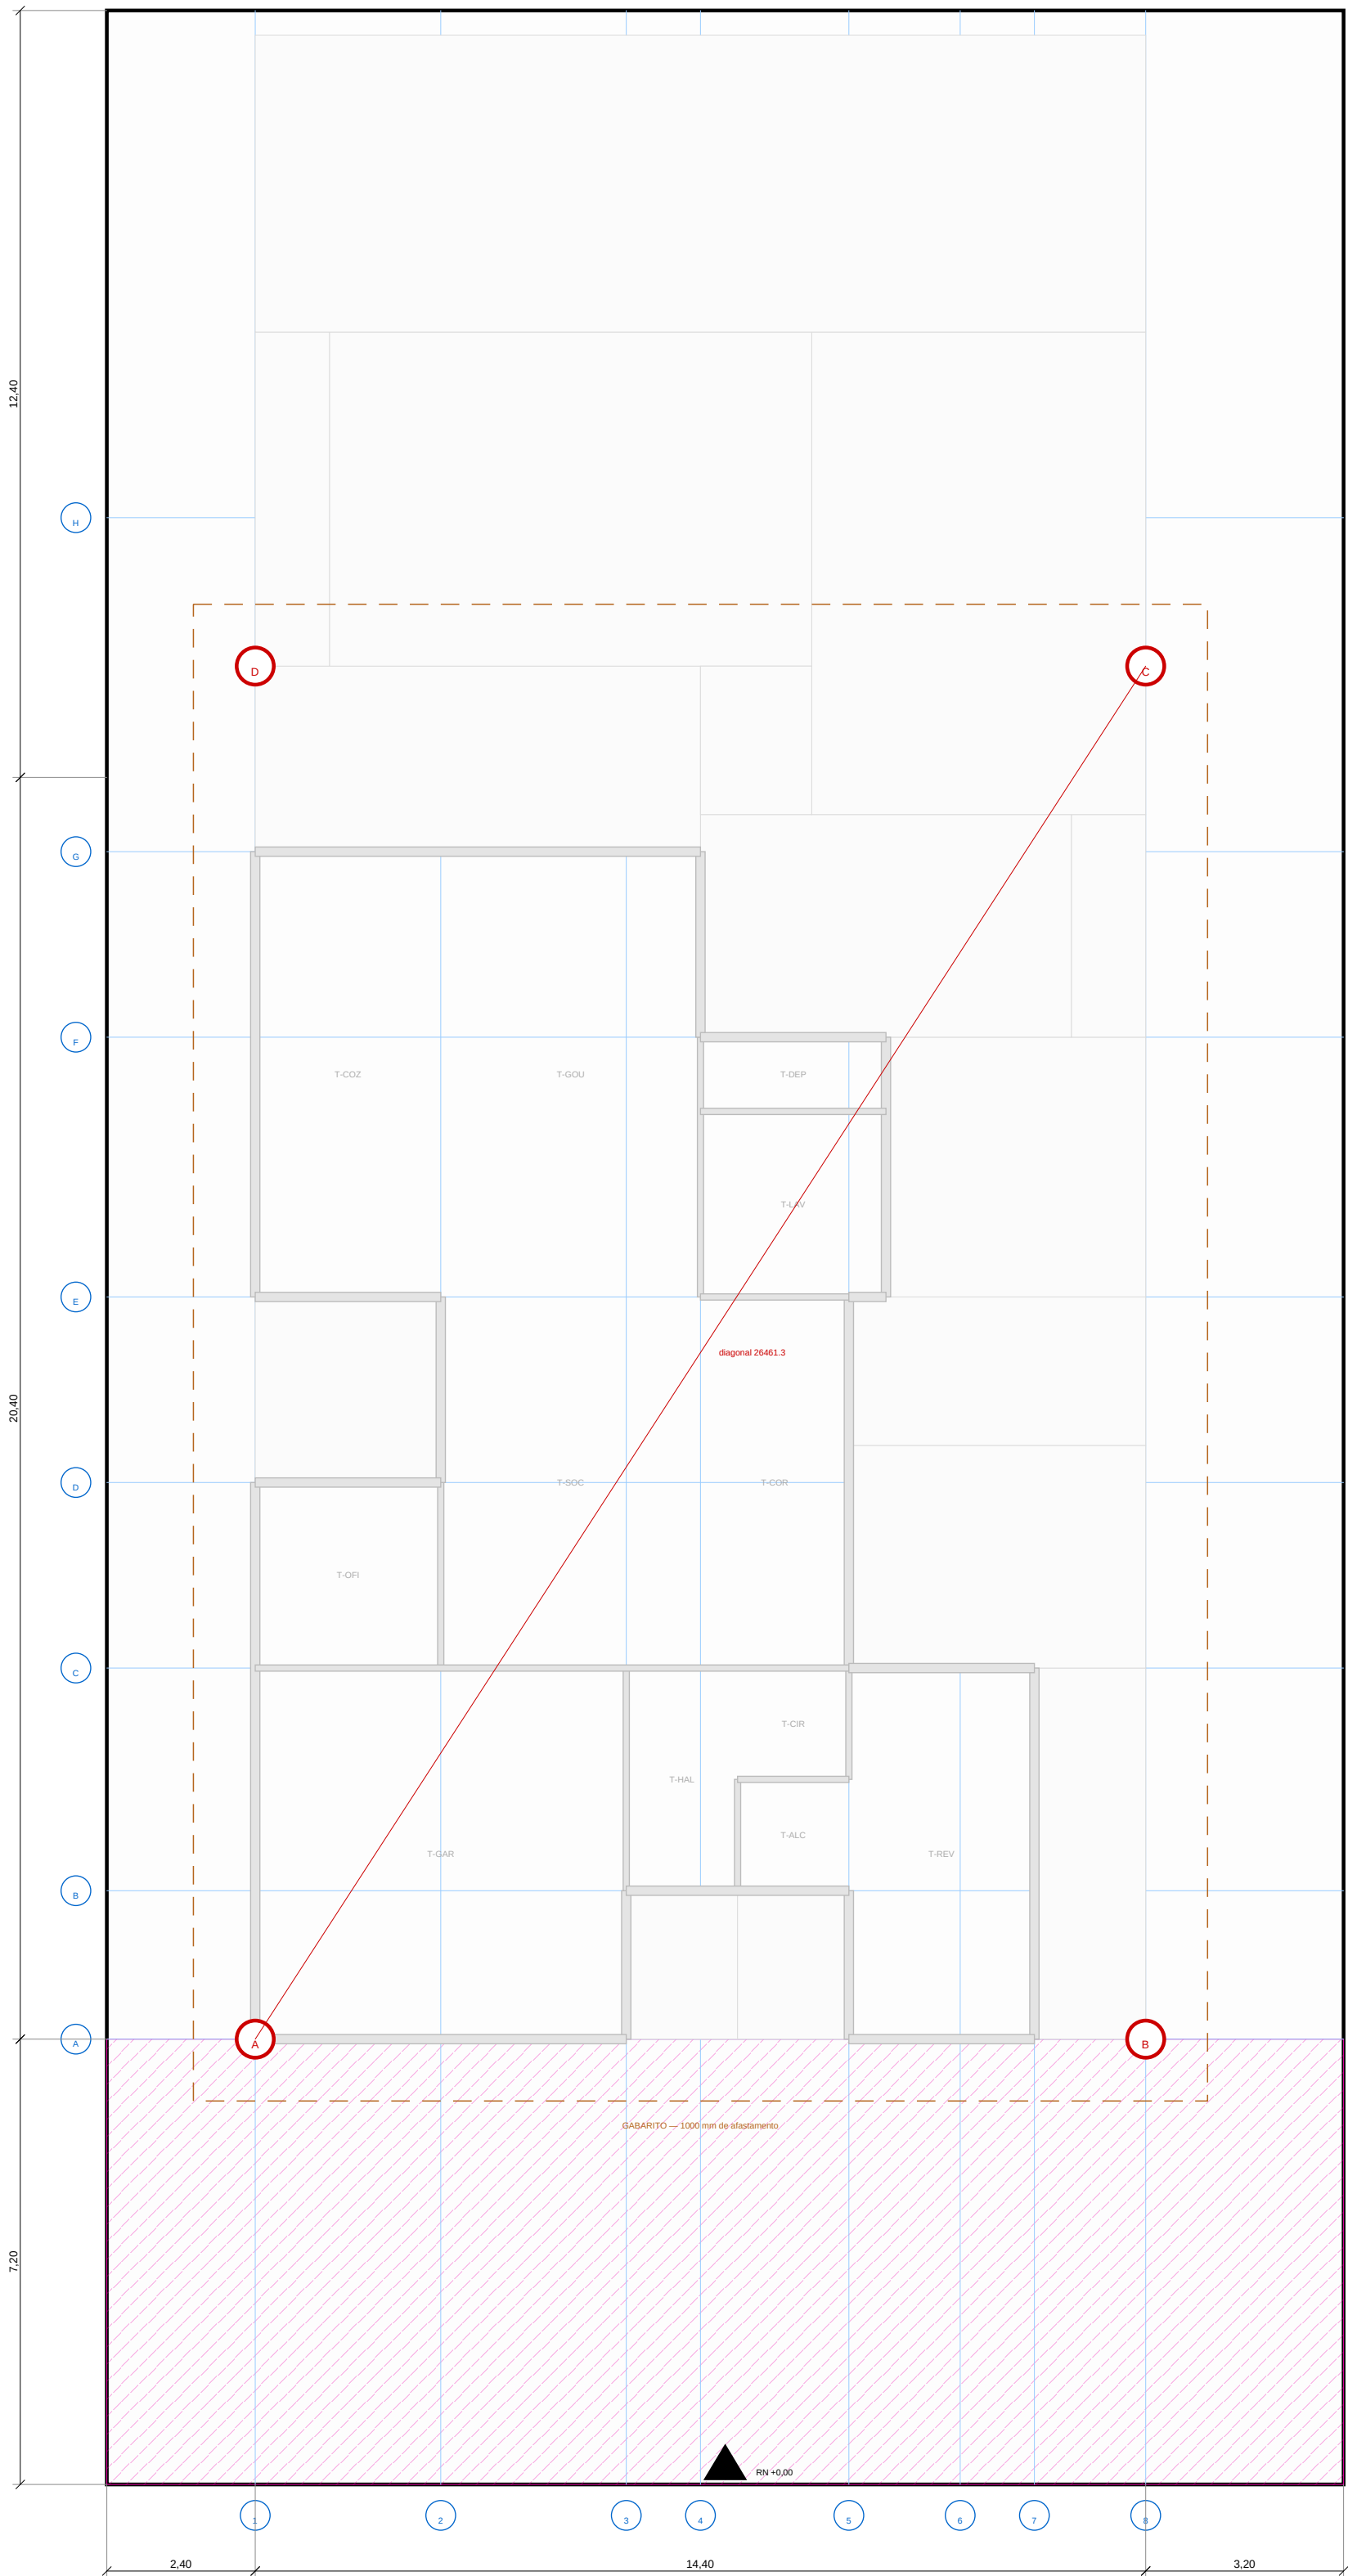

1. LOCACAO — EIXOS E COORDENADAS
ESCALA 1:100

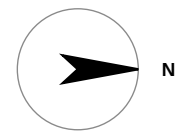

COORDENADAS DOS CANTOS (mm)

CANTO	X	Y	DIVISA SUL	DIVISA NORTE	TESTADA	QUIBO	DIAGONAL
A	2400	7200	2400	17600	7200	32800	26461,3
B	16800	7200	16800	3200	7200	32800	26461,3
C	16800	29400	16800	3200	29400	19600	26461,3
D	2400	29400	2400	17600	29400	19600	26461,3

PROCEDIMENTO DE LOCACAO

#	PASSO	CRITERIO DE ACEITE
1	Conferir as divisas com o material de base	divergencia maxima de 10 mm interrompa a locacao
2	Instalar o RMC marca de concreto 200 x 200 x 100 mm, fora da area de obra	fora da area de obra
3	Montar o gabarito a 1000 mm do cantoneiro	perpendicular 75 x 75 a tolancia 20 x 100
4	Marcar os eixos X, Y e Z a 10 x 10 no gabarito	tolancia coordenada maxima de 200 mm
5	Cortar cabos com ois OARS diretos	verificar em cabos: erro de cabos soma
6	Conferir a diagonal A-C	26461,3 mm com tolerancia de 10 mm
7	Conferir o quadrado por 3-4-5 em cada canto	antes de qualquer concretagem
8	Registrar em ata com foto e modelo	gabarito continuo nos dois lados da obra, conferencia

EIXOS MODULARES

DIRECAO	PROJECAO (mm)
X (L x R)	2400 5400 8400 9600 12600 13800 15000 16800
Y (A x H)	7200 9600 13200 14200 15000 29400 32800
Matriz	principal 800 mm - subgrid 300 mm
Origem	canto frontal esquerdo da base
Unidade	milímetros

NOTAS

- Locacao e o unico desvio em que o erro nao tem impacto direto a casa de lugar.
- Cada canto e o eixo dos OARS diretos, nunca em cabos acumulados — erro de cabos soma, erro de referencia independente nao.
- Conferencia obrigatoria para diagonal 26461,3 mm entre A e C antes de concretar o radier.
- Ris no eixo de baseado, alinhado ao eixo 10-00, com 0,00 + 1 para alinhado do terreno.

PROJETO PORTO REAL

RESIDENCIA UNIFAMILIAR (MANSO) - AM | 100% TUBERIA-PS

PROJETO ARQUITETONICO

LOCACAO DE OBRA E GABARITO

BASE GEOMETRICA Linha Consolidada Projeto (previsão) UNIDADE: METRO (m)	ESCALA 1:100 FORMATO: A1 MATERIAL: 60x90x300	EXIBICAO ESTUDIO PRELIMINAR RTO Linha Consolidada PARA OBRA SEM ART / RNT	PROJECOA 31 60x90x300
--	---	--	-----------------------------