


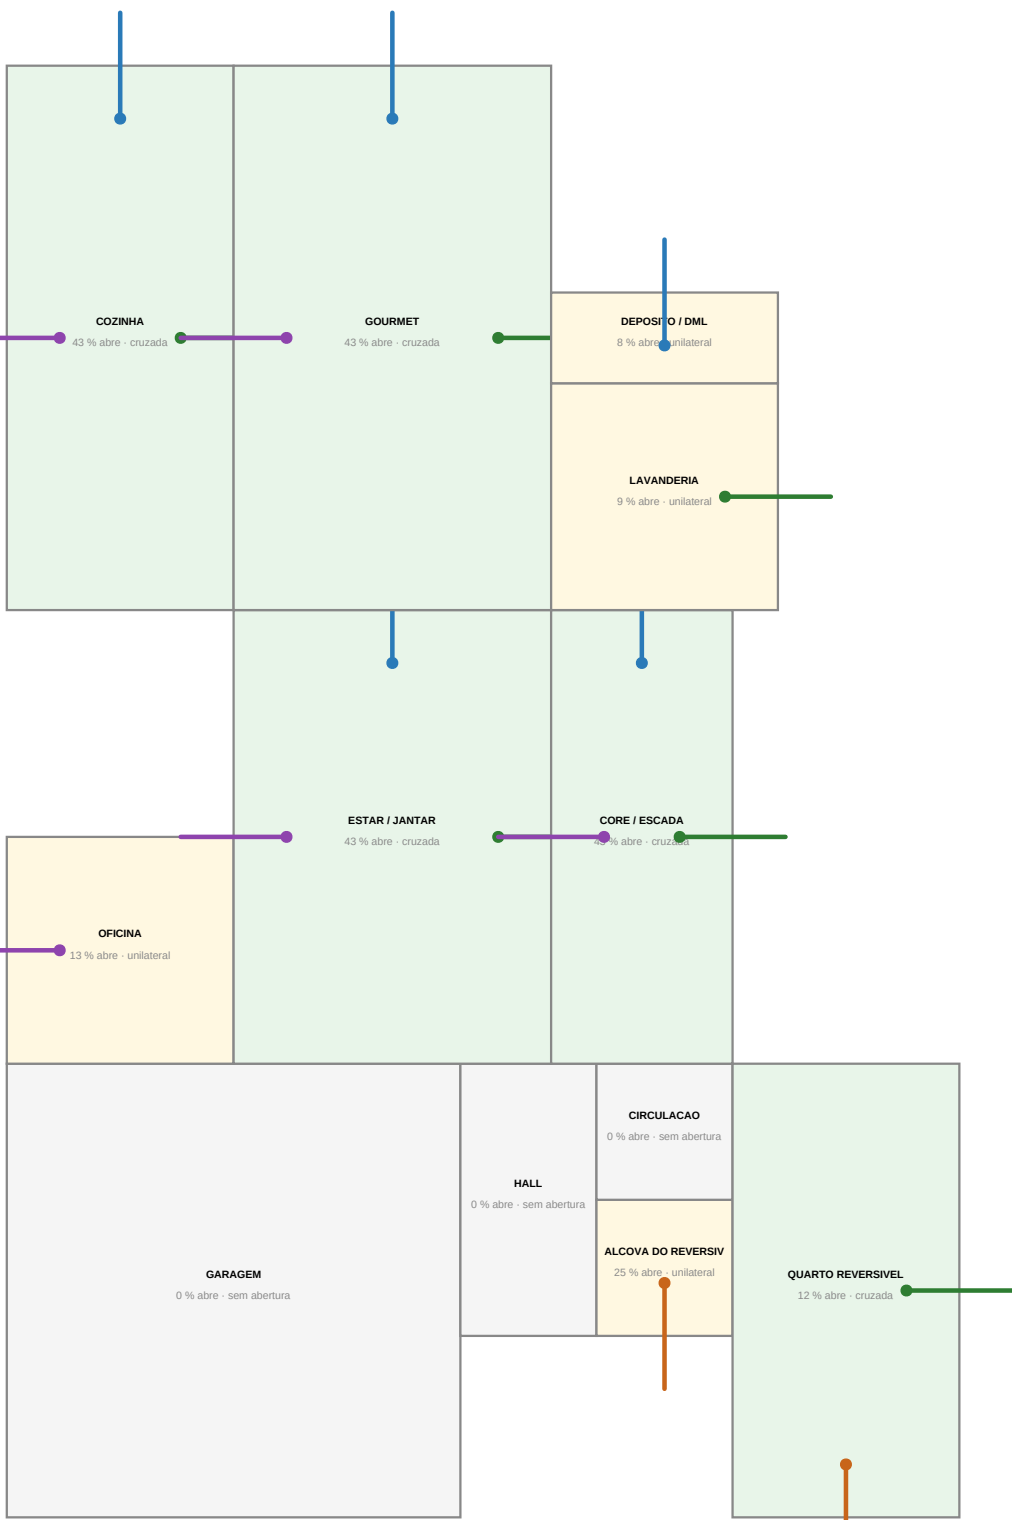


1 TERREO — faces que abrem
ESCALA 1:100

COB	AMBIENTE	CAT.	PROJE	ABREJE	PERÍMETRO	FACIES	TIPO	NOTA
T-GAR	Garagem	externo	34,5	0,00	0%	—	—	ver
T-HALL	HALL	circulatório	9,0	0,00	0%	—	—	ver
T-ALC	ALCOVA DO REVERSÍVEL	interno	2,9	0,72	25%	L	unilateral	OK
T-COR	CIRCULAÇÃO	circulatório	2,9	0,00	0%	—	—	ver
T-REV	QUARTO REVERSÍVEL	interno	26,7	2,04	22%	L, N	cruzada	OK
T-OFI	OFICINA	aberta	4,3	1,08	23%	S	unilateral	ver
T-BOC	ESTAR/JANTAR	aberto	86,7	36,86	43%	N, D, S	cruzada	OK
T-COR	CORR. E ESCADA	circulatório	86,7	36,86	43%	N, D, S	cruzada	ver
T-COZ	COZINHA	aberto	86,7	36,86	43%	N, D, S	cruzada	OK
T-GOU	GOURMET	aberto	86,7	36,86	43%	N, D, S	cruzada	OK
T-LAV	LAVANDERIA	serviço	6,0	0,72	9%	N	unilateral	ver
T-DEP	DEPÓSITO DmL	serviço	3,1	0,24	8%	O	unilateral	ver
S-S02	SUITE 02	interno	26,5	2,04	8%	L, S	cruzada	OK
S-S03	SUITE 03	interno	26,7	2,04	8%	O, S	cruzada	OK
S-HALL	HALL E REPOUSAR	circulatório	10,8	0,00	0%	—	—	ver
S-LOU	MINI LOUNGE / TV	aberto	6,5	0,72	11%	N	unilateral	OK
S-MAST	SUITE MASTER	interno	45,1	7,80	17%	N, D, S	cruzada	OK

PRIVACIDADE — CADA JANELA CONTRA A DIVISA QUE OLHA (art. 1.301 CC)

VIAJ	AMB	FACIES	DET. m	AMB. m	PERÍMETRO	BRIS	LEITURA	
004	T-REV	N	0,00	1,00	1000	—	distante	OK
002	T-COR	N	0,00	1,00	1000	—	distante	OK
005	T-REV	L	7,20	—	1100	BR-L	rua	OK
001	T-REV	N	0,00	1,00	1100	—	distante	OK
001	T-ALC	L	0,60	—	1100	—	rua	OK
003	T-COR	S	3,40	1,00	1100	—	exposta ao vento	OK
001	T-COZ	S	3,40	1,00	1100	—	exposta ao vento	OK
001	T-LAV	N	7,40	1,00	1100	—	distante	OK
004	T-DEP	O	36,90	1,00	1000	—	distante	OK
PR02	T-COR	N	8,00	1,00	9	—	distante	OK
PR02	T-GOU	N	10,40	1,00	9	—	distante	OK
CR05	T-GOU	O	13,00	1,00	9	BR-O	protetida por terra	OK
PR02	T-BOC	S	9,40	1,00	9	—	distante	OK
001	S-LOU	N	4,40	1,00	1100	—	distante	OK
005	S-S02	S	3,40	1,00	1100	—	exposta ao vento	OK
001	S-S02	L	13,20	—	1100	BR-L	rua	OK
004	S-S02	L	13,20	—	1000	BR-L	rua	OK
005	S-S03	S	3,40	1,00	1100	—	exposta ao vento	OK
001	S-S03	O	17,20	1,00	1100	—	distante	OK
004	S-S03	S	2,40	1,00	1000	—	exposta ao vento	OK
005	S-MAST	S	7,80	1,00	1100	—	distante	OK
PR02	S-MAST	O	14,80	1,00	9	—	distante	OK
004	S-MAST	N	4,40	1,00	1000	—	distante	OK
001	S-MAST	N	4,40	1,00	1100	—	distante	OK

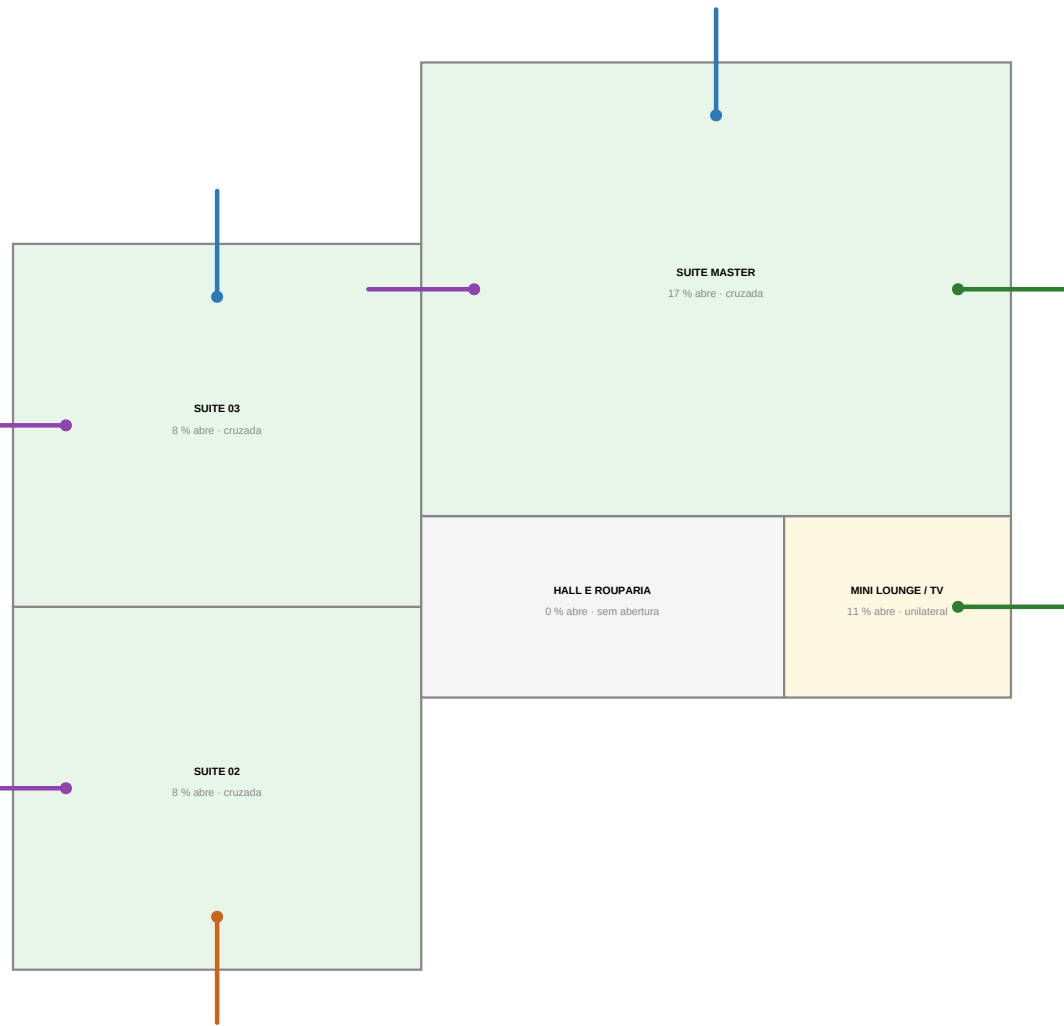

2 SUPERIOR — faces que abrem
ESCALA 1:100

NOTAS

* Área que ABRE por ambiente contra a área do piso. NBR 15275-4 exige 8% na região Norte. NBR 15275-3 recomenda 40% na ZSB (abertura grande).

* Facies que abre por fachada (FC) contra a porta-balcão 200%, janela de correio 50%, basculante 33%, porta-óptica 0%.

* Privacidade pelo art. 1.301 do Código Civil: janela que olha a divisa a menos de 2,50 m e protreta. O brisa que protege esta norma.

* Seta em cada face com abertura, duas ou mais faces = ventilação cruzada.

PROJETO PORTO REAL

RESIDÊNCIA UNIFAMILIAR | MARAULIS - AM | 500m² TÁTUAS-PI

PROJETO ARQUITETÔNICO

VENTILAÇÃO NATURAL, CRUZADA E PRIVACIDADE

BASE GEOMÉTRICA União Consolidada Projeto (preliminar) UNIDADE: MESTRE: AM	ESCALA 1:100 FORMATO: A1 MATERIAL: 605/505/505	EMISSÃO ESTUDO PRELIMINAR RTO Linha Libertada PARA OBRAS SEM ART / RNT	PRIVACIDADE 49 6054 REV 02
---	---	---	----------------------------------