

- downlight embudo

plafon de sobrepor (forno perfurado / aparente)

pendente (je-direito duplo)

linear do tafeia (bancado, closet, mesa)

arandela de espelho

balizador de escada
- 2700 K

3000 K

4000 K
- forno absorvente perfurado (afa 0.70)


sem forno (painel PPR aparente)

LUMINOTECNICA POR AMBIENTE — METODO DOS LUMENS

AMB	USO	mx	mx/ta	abnta	LUMINARIA	kw	W
T-GAR	apoi	30.0	75	108	4 x Plafon LED de sobrepor 24 W	4000 K	96
T-AL	circulacao	6.5	100	151	2 x Downlight LED embudo 18 W	3000 K	36
T-ALC	recep	3.0	100	151	1 x Downlight LED embudo 18 W	2700 K	18
T-CM	circulacao	3.0	100	151	1 x Downlight LED embudo 18 W	3000 K	18
T-DEV	recep	12.7	100	200	5 x Downlight LED embudo 18 W	2700 K	90
T-CM	abito	9.0	100	151	4 x Downlight LED embudo 18 W	4000 K	144
T-SOC	social	25.2	200	242	8 x Downlight LED embudo 24 W	3000 K	144
T-COR	escada	12.2	100	188	2 x Pendente LED de je-direito dup	3000 K	90
T-COE	cacheca	17.8	300	393	7 x Downlight LED embudo 24 W	4000 K	168
T-GOU	social	30.2	200	208	6 x Plafon LED de sobrepor 24 W	3000 K	144
T-LAV	banho	9.0	200	245	4 x Downlight LED embudo 18 W	4000 K	72
T-DEP	banho	3.0	200	272	2 x Downlight LED embudo 18 W	4000 K	36
S-SO1	recep	21.6	100	182	5 x Downlight LED embudo 18 W	2700 K	90
S-SO2	recep	21.6	100	182	5 x Downlight LED embudo 18 W	2700 K	90
S-AL	circulacao	11.5	100	120	2 x Downlight LED embudo 24 W	3000 K	48
S-LOU	social	7.2	200	390	4 x Downlight LED embudo 24 W	3000 K	96
S-MAS	recep	21.6	100	182	6 x Downlight LED embudo 18 W	2700 K	90
S-SO3BANHO	banho	4.0	200	230	2 x Downlight LED embudo 18 W	3000 K	36
S-SO3BANHO	banho	4.0	200	230	2 x Downlight LED embudo 18 W	3000 K	36
T-CLOSET-ESPENSA	banho	3.0	200	390	2 x Downlight LED embudo 24 W	4000 K	48
T-BEUSBANHO	banho	4.0	200	230	2 x Downlight LED embudo 18 W	3000 K	36
T-COM-LAVABO	banho	2.0	200	227	1 x Downlight LED embudo 18 W	3000 K	18
S-MASBANHO	banho	10.8	200	251	4 x Downlight LED embudo 18 W	3000 K	72
S-MAS-CLOSET	closet	9.0	200	245	4 x Downlight LED embudo 18 W	3000 K	72
S-MAS-OFFICE	office	9.4	300	512	4 x Downlight LED embudo 24 W	4000 K	96

LUZ DE TAREFA

COD	ONDE	TIPO	QTD	kw
L7-BC-01	bancada BC-01 (T-CO2)	linear	2.1 m	4000 K
L7-BC-02	bancada BC-02 (T-CO2)	linear	1.8 m	4000 K
L7-BC-03	bancada BC-03 (T-CO3)	linear	1.5 m	4000 K
L7-BC-04	bancada BC-04 (T-CO3)	linear	3.0 m	4000 K
L7-BC-05	bancada BC-05 (T-CO3)	linear	2.4 m	4000 K
L7-LC-02	espelho do banheiro LC-02 (T-CO3)	arandela	1	4000 K
L7-LC-03	espelho do banheiro LC-03 (T-REV)	arandela	1	4000 K
L7-LC-05	espelho do banheiro LC-05 (S-SO2)	arandela	1	4000 K
L7-LC-06	espelho do banheiro LC-06 (S-SO2)	arandela	1	4000 K
L7-LC-11	espelho do banheiro LC-11 (S-MAS)	arandela	2	4000 K
L7-S-MAS-CLOSET	closet do S-MAS	linear	3.0 m	3000 K
L7-S-MAS-OFFICE	mesa do office do S-MAS	linear	1.2 m	4000 K
L7-ENGADIA	escada (balizadora)	balizadora	6	3000 K

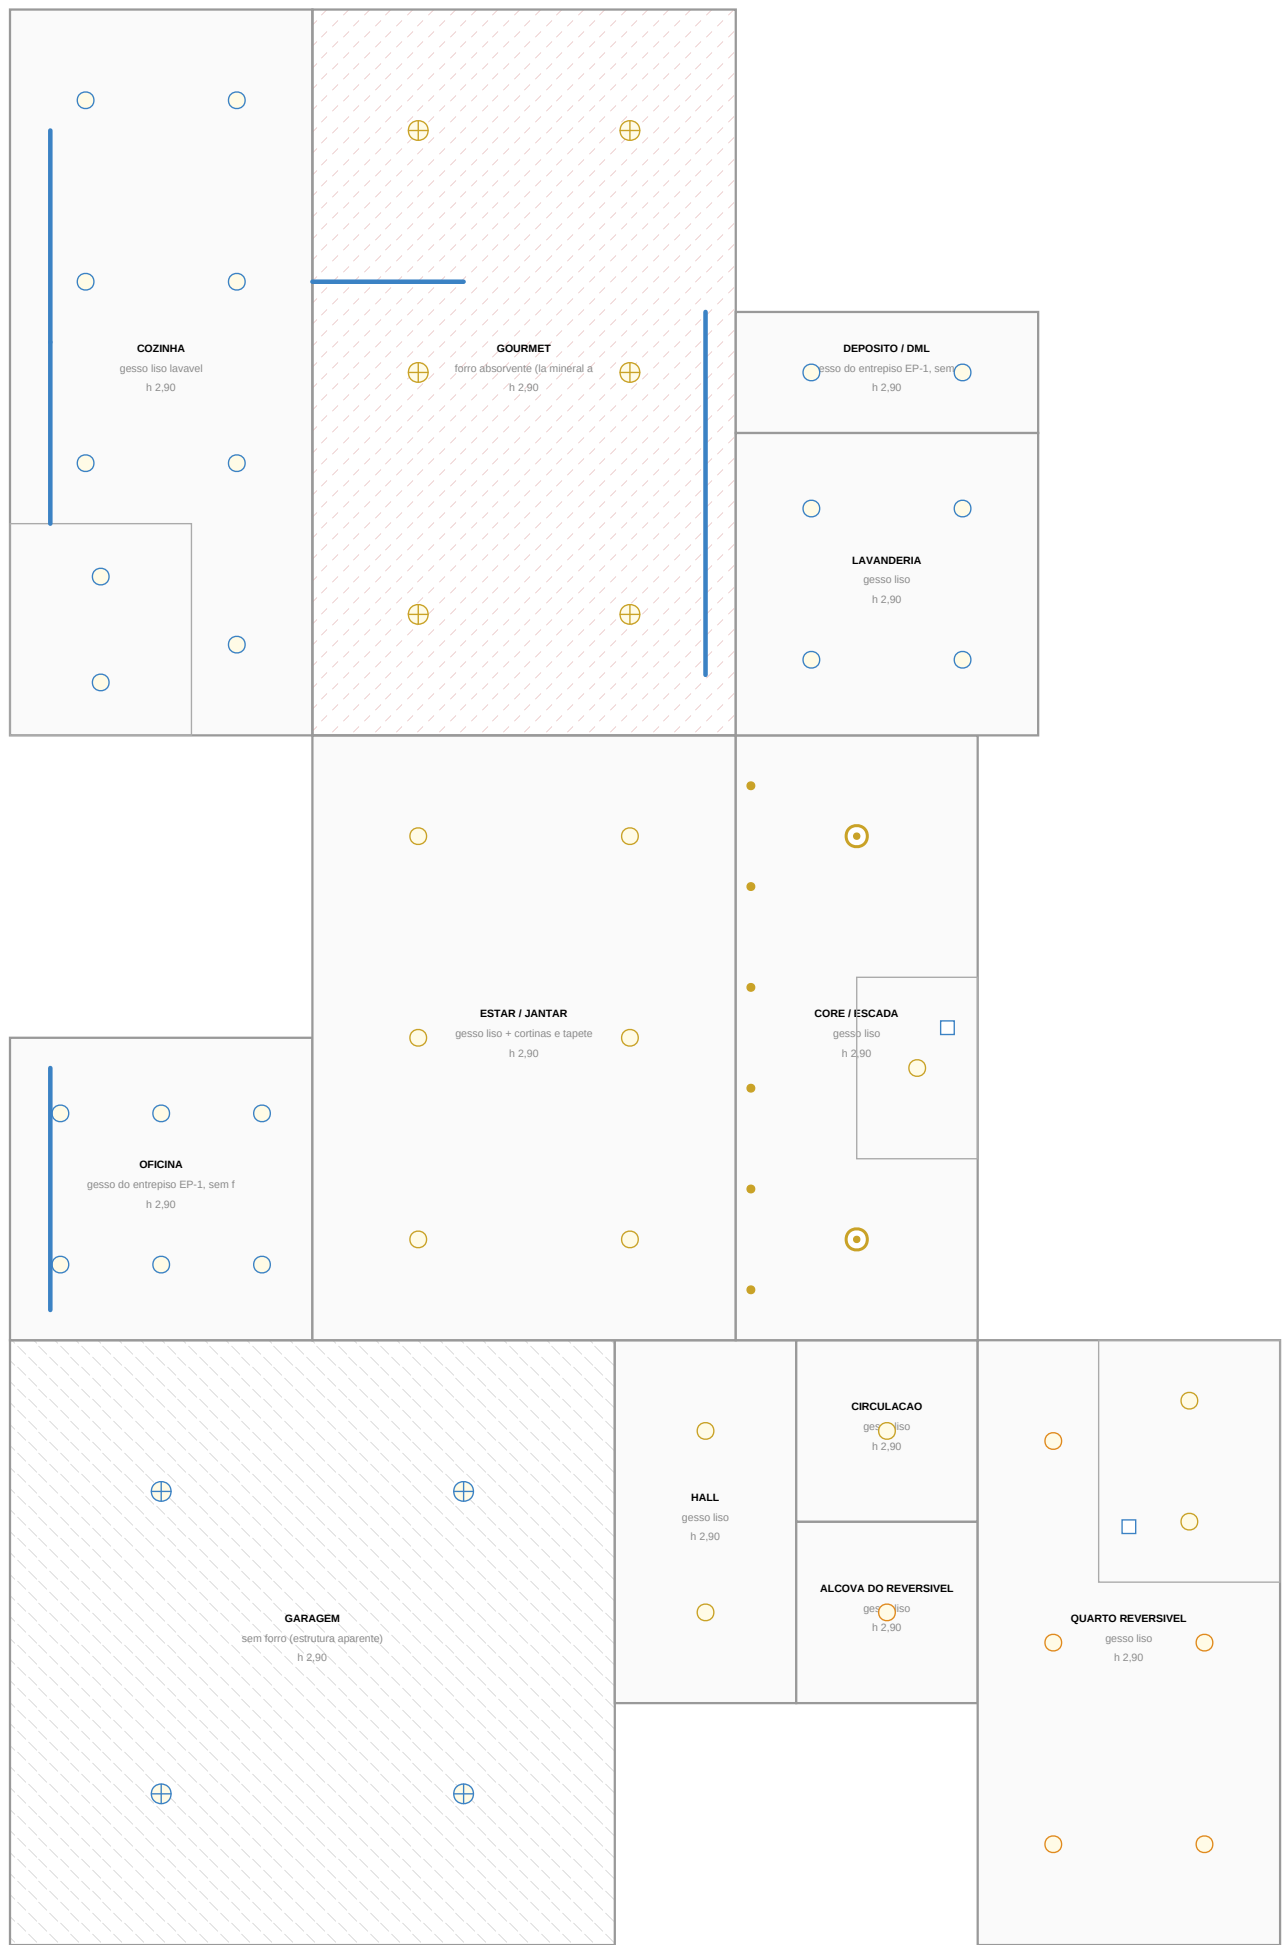

1 FORRO REFLETIDO — TERREO
ESCALA 1:75



2 FORRO REFLETIDO — SUPERIOR
ESCALA 1:75

- NOTAS
- Planta refletida: vista do forno projetada no plano horizontal, terreno e superior.
 - Luminarias pelo METODO DOS LUMENS por ambiente (NBR 9070:2015 / NBR 5413), malha de uniformidade 50% 1.2.
 - 10 pontos por metro, 12 pontos de parede, 30% W (3.2 W/m²).
 - Cor: 2.700 K interior - 3.000 K social e circulação - 4.000 K cozinha, banheiro e trabalho.

PROJETO PORTO REAL

RESIDENCIA UNIFAMILIAR (MANSÃO - AM) | SOBR TATIANA-PS

PROJETO ARQUITETONICO

PLANTA DE FORRO E ILUMINACAO

BASE GEOMETRICA União Consolidada Projeto (previsível) UNIDADE: METRO: mm	ESCALA 1:75 FORMATO A1 MILHA: 600/500/300	EMISSAO ESTUDIO PRELIMINAR RES LIMITE LIBERADO PARA OBRA SEM ART / RNT	PROJETO 16 06-43 REV 02
--	---	---	--------------------------------------