


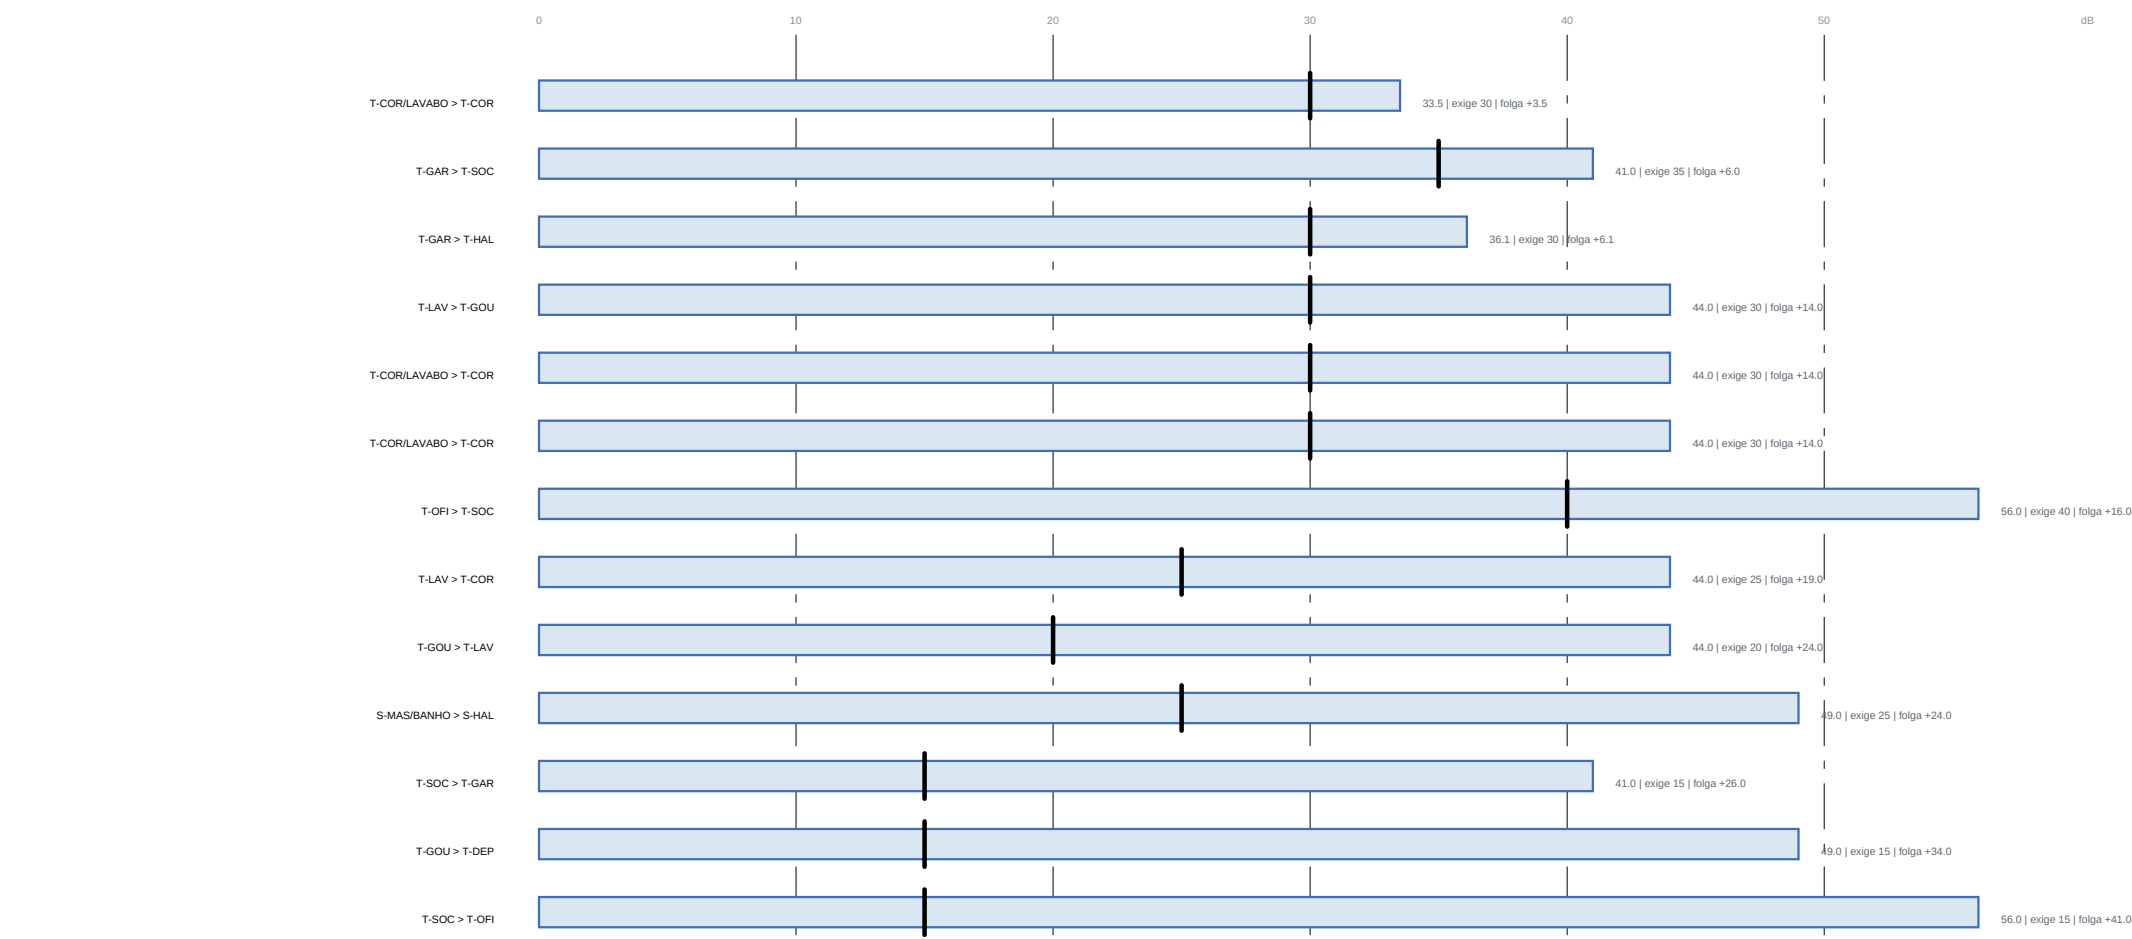

Barra = isolamento edificado; traço vertical = exigência (valor da fonte menos limite do receptor, NBR 15102)

O QUE MUDOU EM R52

ONDE	ANTES	DEPOIS	POR QUE
Banho compartilhado + hall de entrada	porta de correr (Rw 25) — conjunto de 20,2 dB	parede CEGSA, 44 dB	o acesso de volta passou para a circulação
Banho compartilhado + quarto eventual	porta com (Rw 25) — conjunto de 25,5 dB, exigia 25	parede CEGSA, 44 dB	era a pior passagem da casa, e não era a única
Hall + garagem	porta seca — 36,9 dB, exigia 35	PDS isolada vedada — 36,9 dB	porta entre garagem e casa tem dupla função para ser móbica
Banho compartilhado + circulação	não havia porta	PDS isolada vedada — 35,7 dB, exigia 25	único acesso do banho, e abria para fora
Bloco do chuveiro	encostado na parede do hall	canto arredondado, toldo e janela alta	consequência da porta nova, a regra dos 900 cm de box obrigou a primeira tentativa

TABELAS ADOTADAS

ITEM	VALOR	FONTE
Fonte: caixa sanitária	75 dB(A)	prática corrente de acústica
Fonte: bloco do chuveiro	75 dB(A)	prática corrente de acústica
Fonte: cozinha e gourmet	75 dB(A)	prática corrente de acústica
Fonte: sala e jantar	75 dB(A)	prática corrente de acústica
Fonte: garagem	75 dB(A)	prática corrente de acústica
Fonte: máquina de lavar e secar	75 dB(A)	prática corrente de acústica
Fonte: oficina	80 dB(A)	prática corrente de acústica
Limite: banho	45 dB(A)	NBR 15102:2017 (circulação e entrada adjacente)
Limite: circulação	45 dB(A)	NBR 15102:2017 (circulação e entrada adjacente)
Limite: cozinha	45 dB(A)	NBR 15102:2017 (circulação e entrada adjacente)
Limite: dormitório	55 dB(A)	NBR 15102:2017 (circulação e entrada adjacente)
Limite: escritório	55 dB(A)	NBR 15102:2017 (circulação e entrada adjacente)
Limite: entrada	45 dB(A)	NBR 15102:2017 (circulação e entrada adjacente)
Limite: estar	45 dB(A)	NBR 15102:2017 (circulação e entrada adjacente)
Limite: sala	45 dB(A)	NBR 15102:2017 (circulação e entrada adjacente)
Limite: oficina	55 dB(A)	NBR 15102:2017 (circulação e entrada adjacente)
Limite: serviço	55 dB(A)	NBR 15102:2017 (circulação e entrada adjacente)
Fonte: acústica	Flw 25 dB	Nota de mercado declarada
Fonte: sonar	Flw 25 dB	Nota de mercado declarada
Fonte: sala	Flw 25 dB	Nota de mercado declarada
Fonte: sala de	Flw 25 dB	Nota de mercado declarada
Fonte: sala de visita	Flw 30 dB	Nota de mercado declarada

NOTAS

1 Esta planilha existe porque o proprietário perguntou o que 100 verificações não sabem responder: quem entra na casa ouve o chuveiro do banho da entrada?

2 Ouviu. A parede era boa (Rw 44), mas ali é a porta era do corredor (Rw 25), o conjunto entregava 20 dB. Em acústica o eixo físico DOMINA — não se faz média aritmética do isolamento, se soma energia que passa.

3 Isolamento ao ar exige EXTRE cuidado. Dentro da file social o ruído não é definido, é o programa.

4 O adotado igual ao R52 compõe (semplificação declarada). Não é pré-verificação de projeto, mas ensaio de campo da NBR 15107-3.

PROJETO PORTO REAL

RESIDENCIA UNIFAMILIAR (MANSÃO - AM) | SOBR TATIANA-PR

PROJETO ARQUITETÔNICO

DESEMPENHO ACUSTICO ENTRE AMBIENTES

BASE GEOMÉTRICA	ESCALA	EMISSÃO	PROVA
Lista Consolidada	s/ escala	ESTUDO PRELIMINAR R52	
ISO R52 (previsão)	FORMATO A1	ISO LIBERADO PARA OBRA	39
UNIDADE MÉTRICA: mm	MILÍMETROS (50/100/200)	SEM ART / RNT	06-43 REV R52