



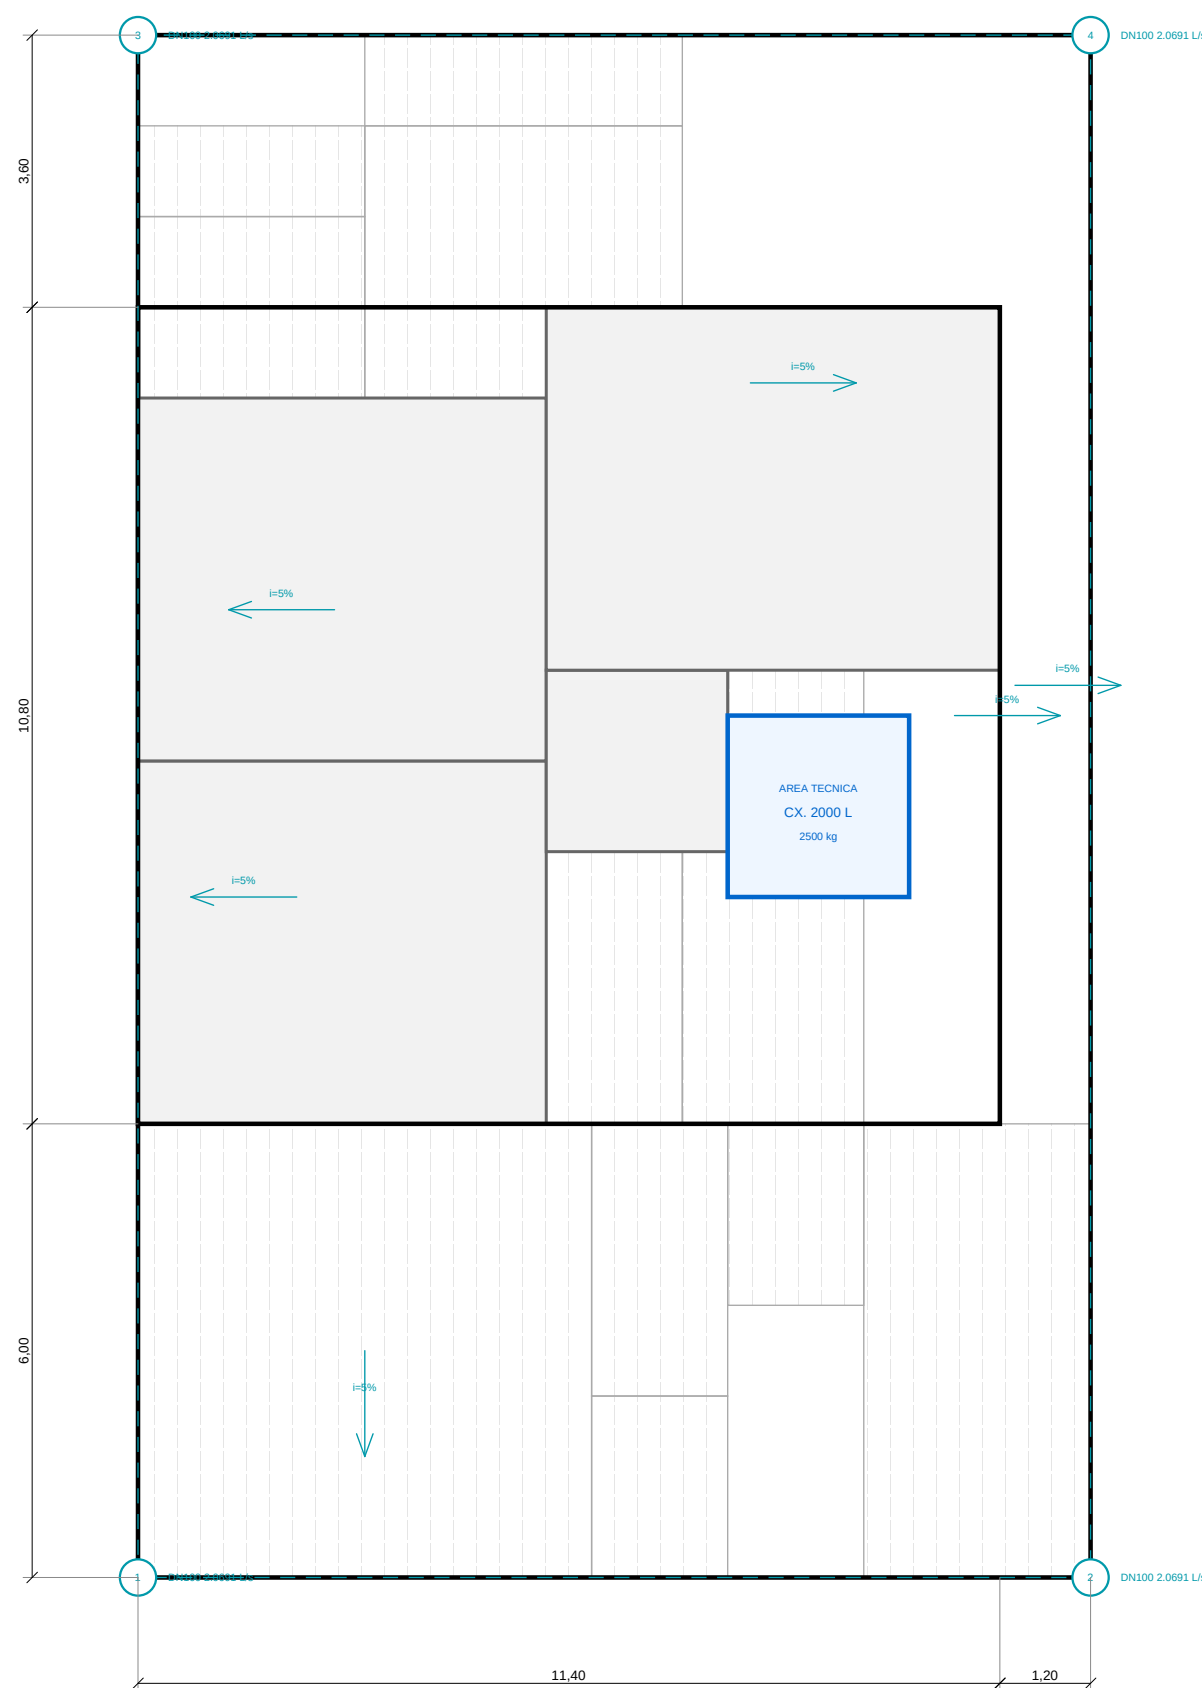

1 COBERTURA
ESCALA 1:100

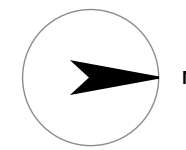

- NOTAS
- Plafond sandbach PPR 75 mm, inclinação 5 %.
 - Calha externa 120x120 mm, 4 bocanetas Ø100.
 - Contribuição 174.24 m² (+ 100 m²) C = 0.35 = Q = 8.2764 L/s.
 - Reservatório de retenção pluvial 2.000 L, -- orgânicos e lixíngios, sem ligação a rede pública.

PROJETO PORTO REAL

RESIDÊNCIA UNIFAMILIAR (MANSÃO - AM) | SOUS TATIANA-PS

PROJETO ARQUITETÔNICO

PLANTA DE COBERTURA

BASE GEOMÉTRICA	ESCALA	EMISSÃO	PROVA
Unidade Consolidada	1:100	ESTUDO PRELIMINAR	05
Projeto (previsão)	FORMATO A1	NOVO LIBERADO PARA OBRAS	
UNIDADE MESTRE: AM	MALHA 600/600/300	SEM ART / RNT	05.13