


VERIFICACAO NBR 9050

ITEM	EXISTENTE	PROJETO	
Visão livre de porta	800 mm	940 mm (altura de 900)	OK
Circuito de giro 360 graus	1.500 mm	hall, banheiro e quarto	OK
Deslocar sem rampas	até 5 mm	soluções elevadas	OK
Largura de circulação	900 mm	1.800 mm no hall	OK
Barra de apoio	relevo próprio	ambulador no PTE 1 e PTE 2	OK
Barreira acústica	altura livre 730 mm	sem barreiras sob a calha	OK
Contraste e interruptor	600 a 1.000 mm	a definir no relatório	pendente



FLUXOS — SEPARACAO DE CIRCUITOS

CIRCUITO	PERCURSO	CIRCULO O SOCIAL?
Serviço	garagem -> oficina -> lavanderia -> cozinha -> despensa	NAO
Social	entrada -> hall -> estar -> gourmet -> alameda -> piscina	—
Área de serviço	hall -> circulação -> banheiro social (quarto reservado) (se não for projeto)	NAO
Área superior	hall -> core -> hall superior -> suíte	NAO
Área de carga	cozinha -> despensa -> reservado	NAO

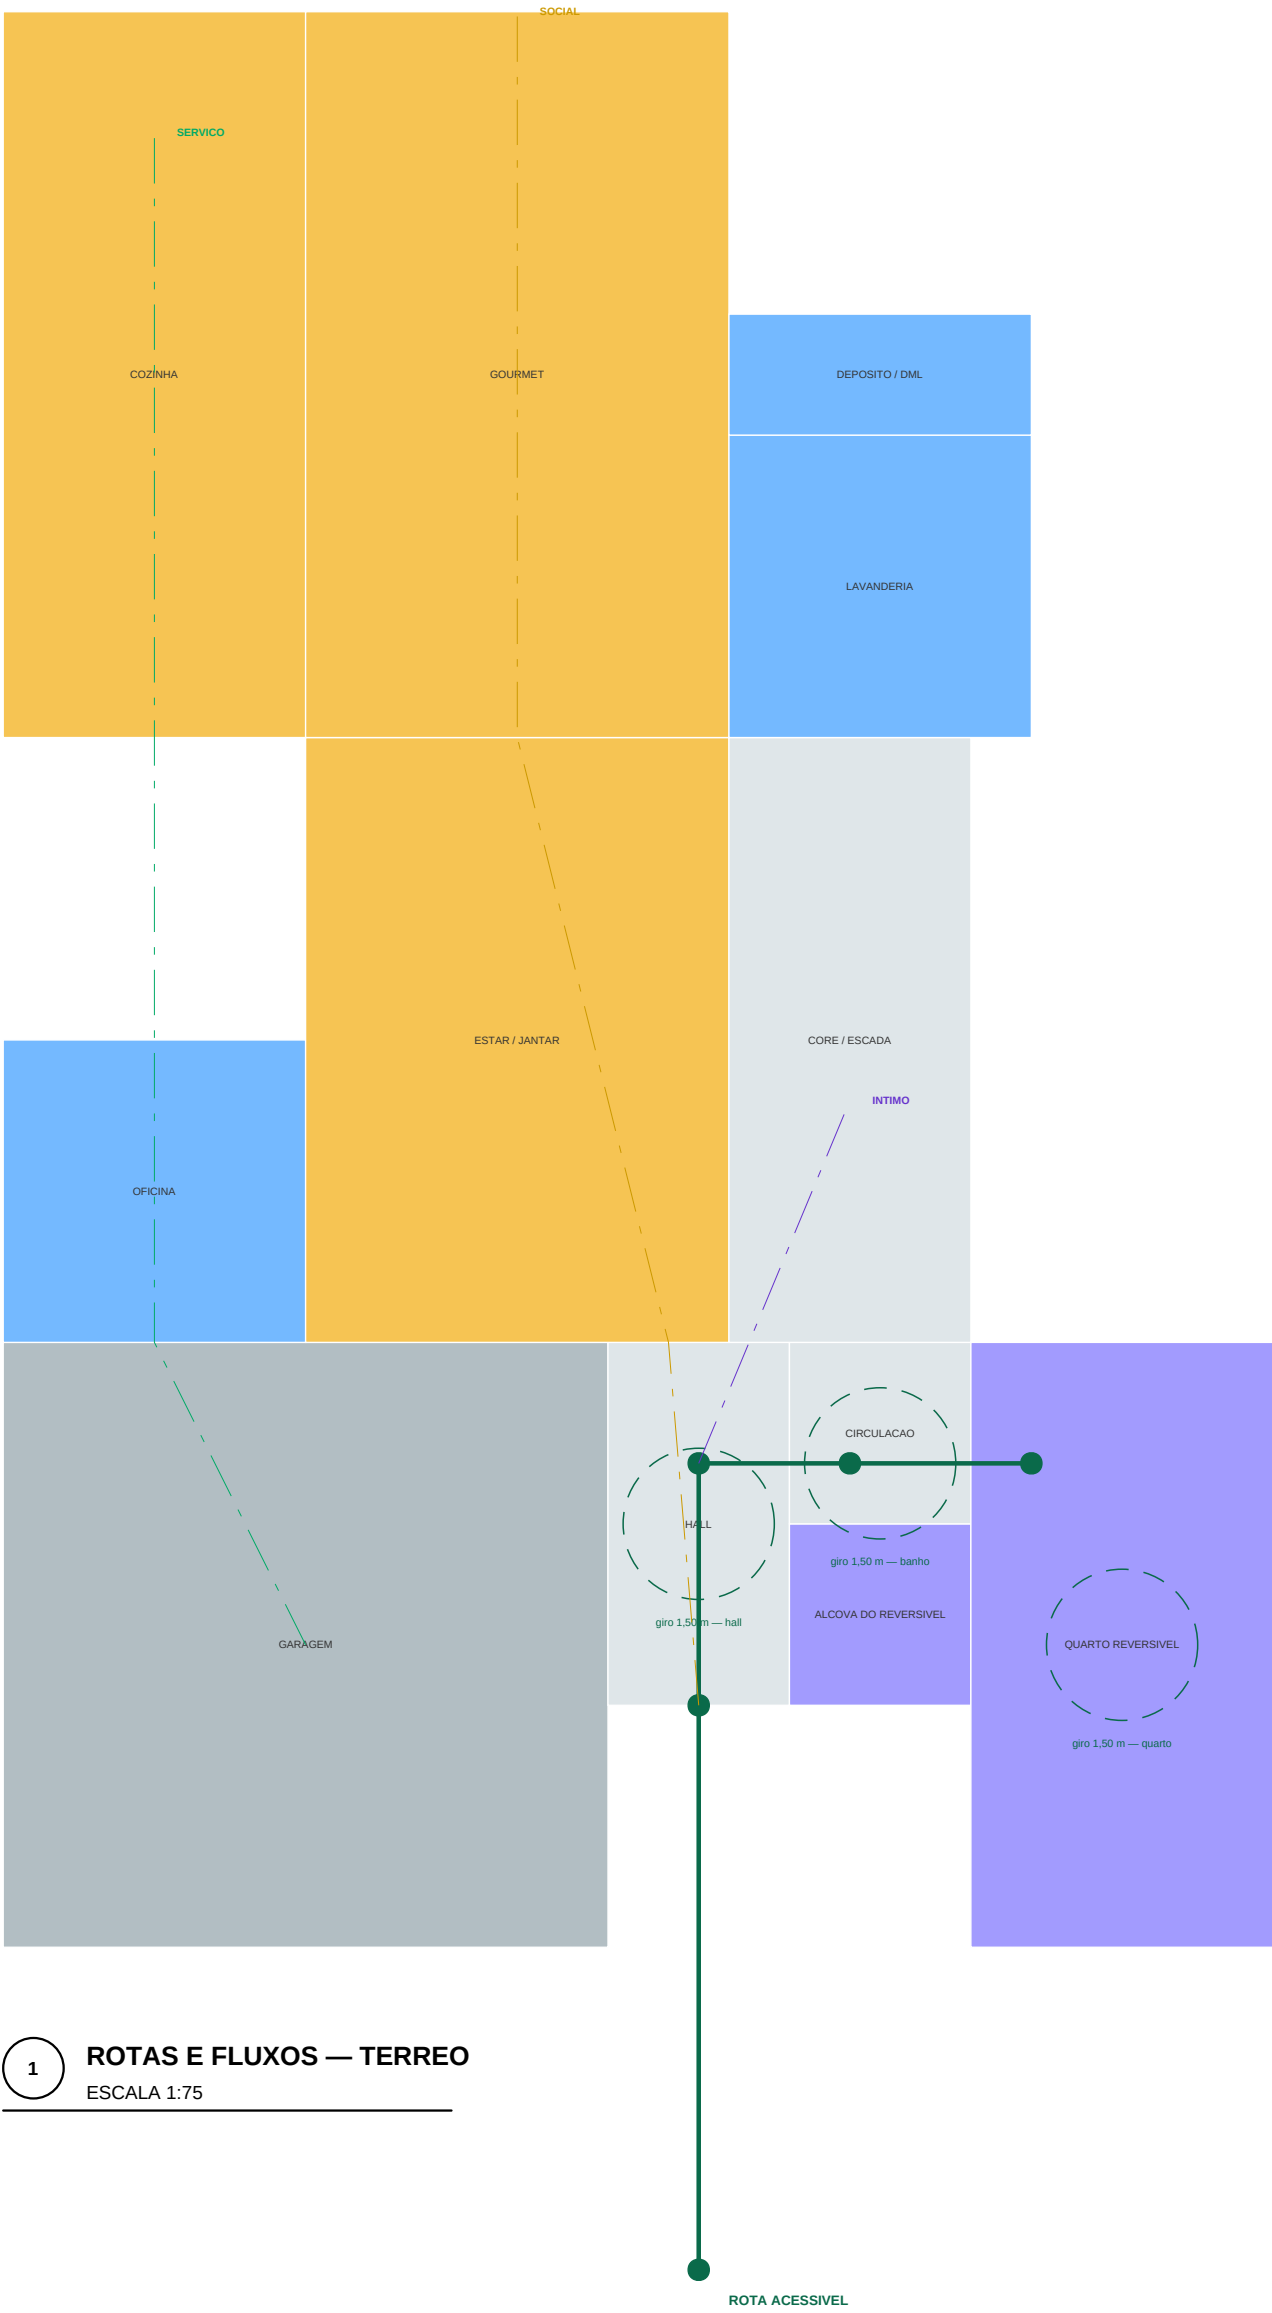

1 ROTAS E FLUXOS — TERREO
ESCALA 1:75

- NOTAS
- * Rota acessível do passeio ao quarto reservado e ao banheiro social.
 - * Circuito de giro de 1.500 mm verificado nos pontos de manobra.
 - * Porta de correr de 900 mm no banheiro social e área de manobra.
 - * Reforço para barra de apoio embutida antes do fechamento das placas.

PROJETO PORTO REAL

RESIDENCIA UNIFAMILIAR (MANSÃO - AM) | SOBR TATIANA-PS

PROJETO ARQUITETONICO

ACESSIBILIDADE E FLUXOS

BASE GEOMETRICA	ESCALA	EMISSAO	PROJECION
União Consolidada	1:75	ESTUDO PRELIMINAR RES	17
ISO-PTD (previsão)	FORMATO A1	NAO LIBERADO PARA OBRA	SEM ART / RNT
UNIDADE MESTRE: AM	MAI/24 05/05/2025		04-78 REV 02