
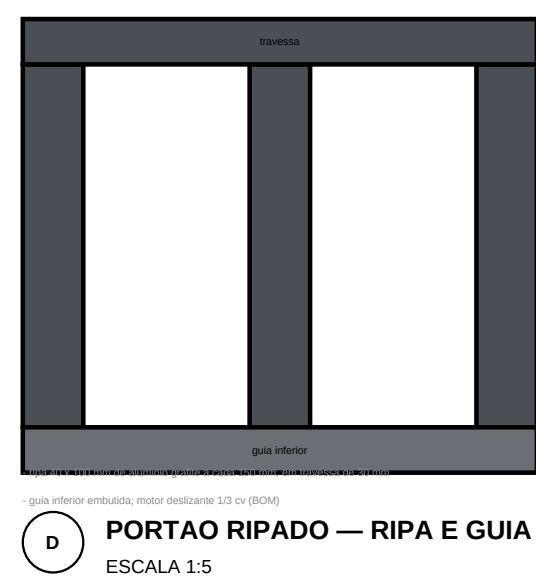


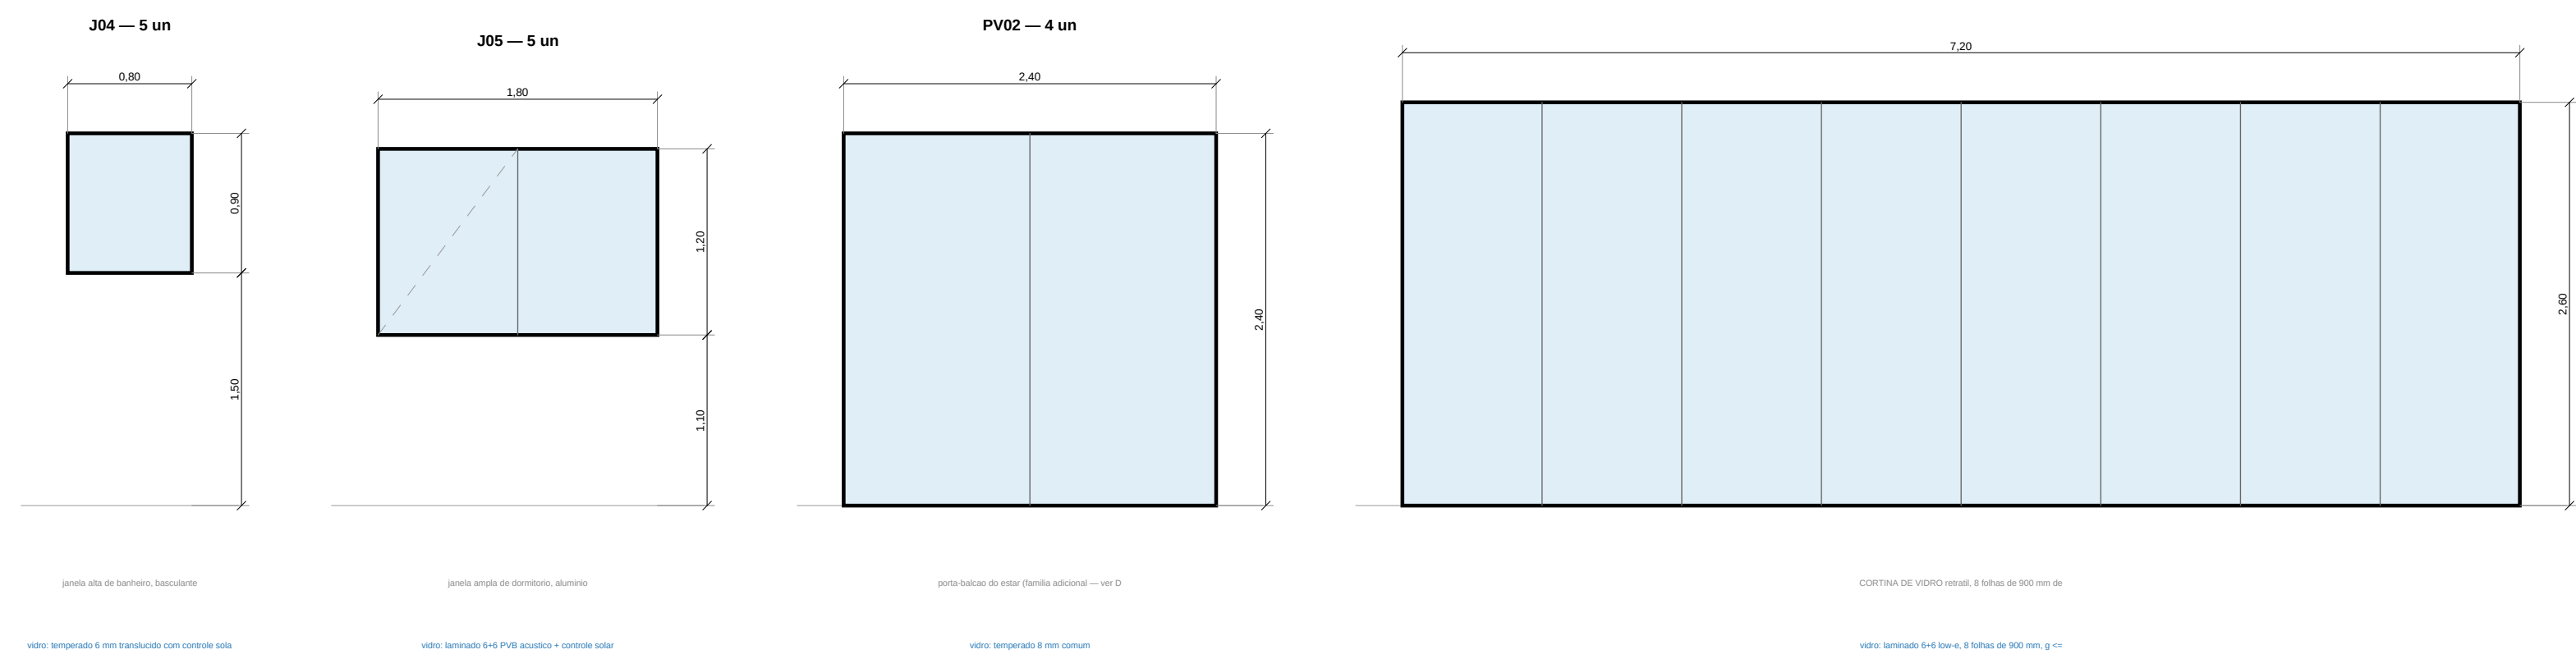

PROJETO PORTO REAL			
RESIDENCIA UNIFAMILIAR (MANAUS) - IM (1500 TAPAJOS - PA)			
PROJETO ARQUITETONICO			
ESQUADRIAS — TIPOS, QUANTIDADES E DETALHES			
BASE GEOMETRICA Lista Concordada pro-022 (previões) UNIDADE MESTRE (m²)	ESCALA 1:40 • 1:5 FORMATO A1 SALHA 900/600/300	EMISSAO ESTUDO PRELIMINAR R01 NÃO LIERACAO PARA OBRA SEM IMT / IMPT	PRECISAO 52 de 75 REV 02