



1 BC-01 GABINETE SOB GRANITO
ESCALA 1:40

4 mod. - 0 portas - 0 gav. - 24 peças - perfil gôto de alumínio graf

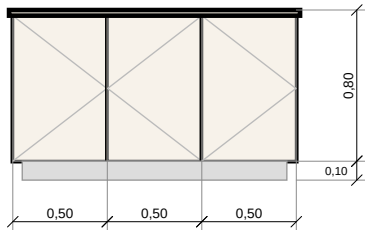


4 BC-03 GABINETE SOB GRANITO
ESCALA 1:40

3 mod. - 3 portas - 0 gav. - 18 peças - perfil gôto de alumínio graf

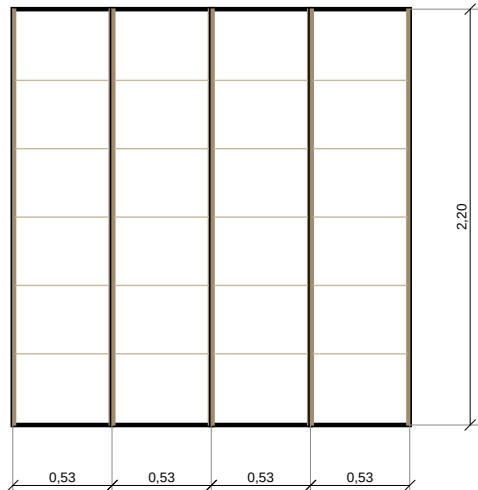


7 AR-06 PRATELEIRAS
ESCALA 1:40

4 mod. - 0 portas - 0 gav. - 40 peças - perfil gôto de alumínio graf

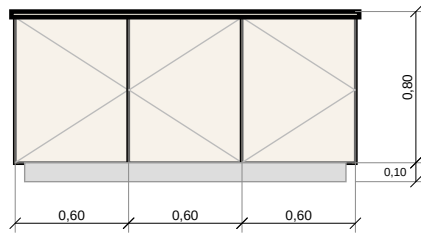


2 BC-02 GABINETE SOB GRANITO
ESCALA 1:40

3 mod. - 3 portas - 0 gav. - 18 peças - perfil gôto de alumínio graf

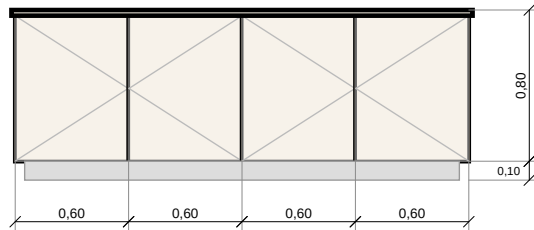


5 BC-06 GABINETE SOB GRANITO
ESCALA 1:40

4 mod. - 4 portas - 0 gav. - 24 peças - perfil gôto de alumínio graf

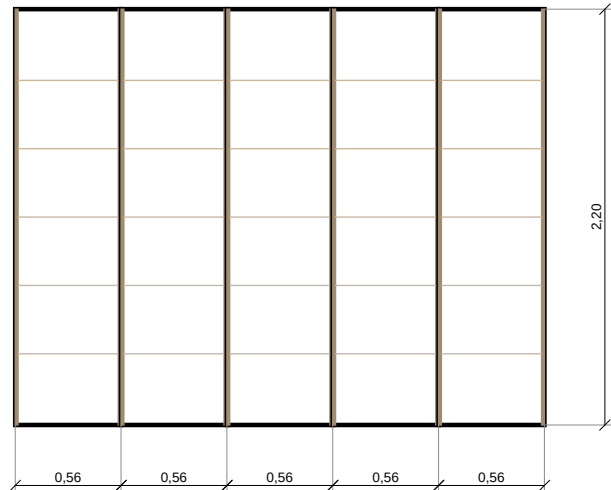


8 AR-03 PRATELEIRAS
ESCALA 1:40

5 mod. - 0 portas - 0 gav. - 40 peças - perfil gôto de alumínio graf

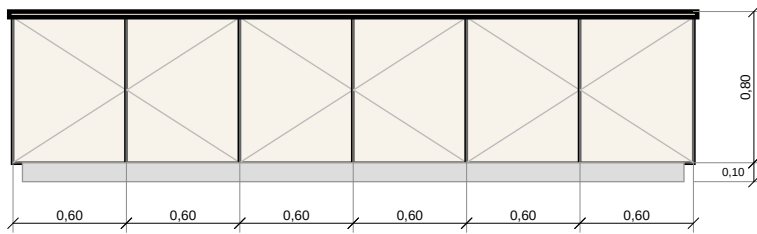


3 BC-04 GABINETE SOB GRANITO
ESCALA 1:40

6 mod. - 6 portas - 0 gav. - 36 peças - perfil gôto de alumínio graf

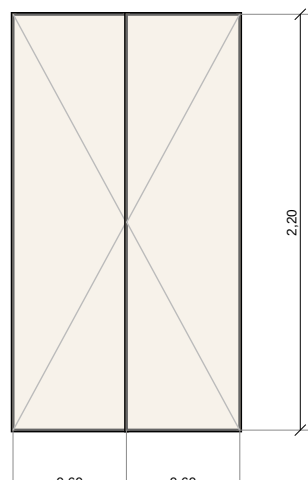


6 AR-08 ARMARIO ALTO
ESCALA 1:40

2 mod. - 2 portas - 0 gav. - 20 peças - perfil gôto de alumínio graf

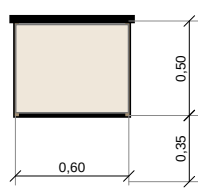


9 LC-02 GAB. LAVATORIO
ESCALA 1:40

2 mod. - 0 portas - 2 gav. - 20 peças - canto voltado a 45 graus diam

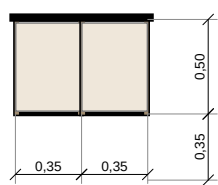


11 LC-05 GAB. LAVATORIO
ESCALA 1:40

2 mod. - 0 portas - 2 gav. - 20 peças - canto voltado a 45 graus diam

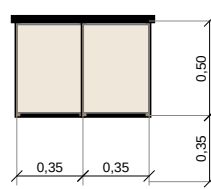


10 LC-15 GAB. LAVATORIO
ESCALA 1:40

2 mod. - 0 portas - 2 gav. - 20 peças - canto voltado a 45 graus diam

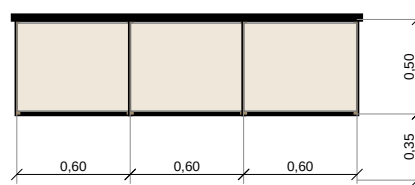

12 LC-11 GAB. LAVATORIO
ESCALA 1:40

3 mod. - 0 portas - 3 gav. - 20 peças - canto voltado a 45 graus diam

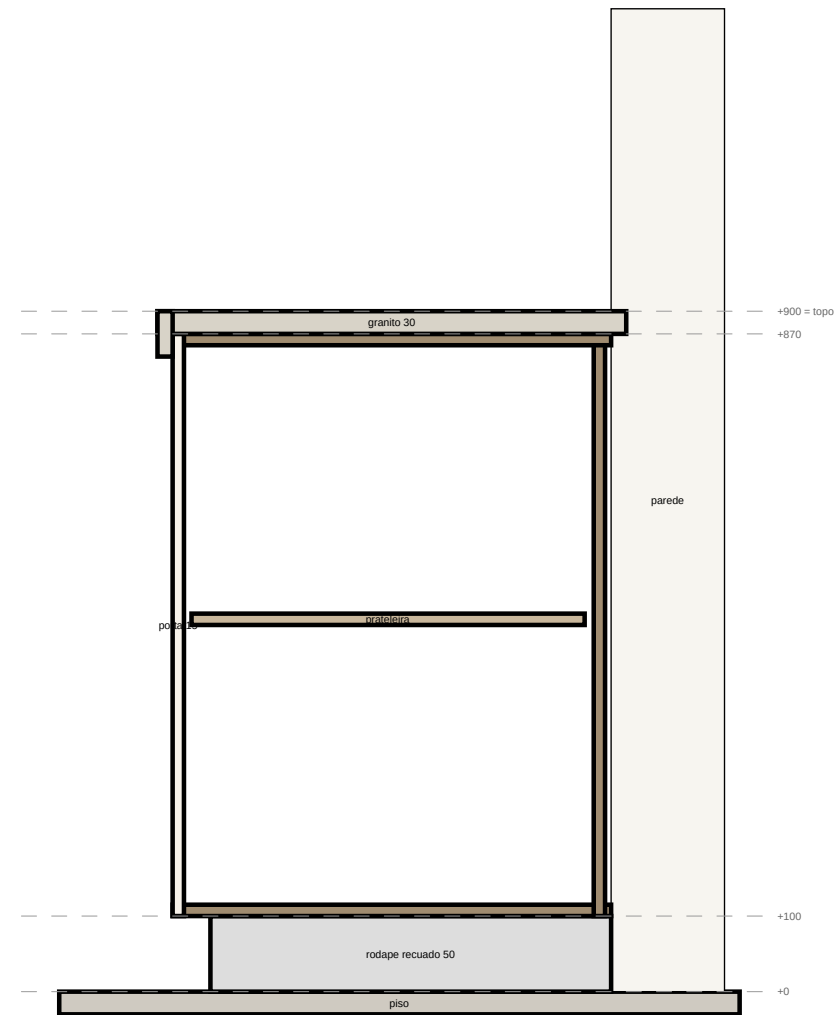

A SECAO DO GABINETE SOB GRANITO — APOIO E RODAPE
ESCALA 1:10

- NOTAS
- * Gabinete sob granito: cantos de MDF 15 mm sobre apoios, rodape recuado 50 mm, tempo a 900 mm. Módulo com todos sem prateleira, módulo de cooktop com uma.
 - * Gabinete de lavatório suspenso a 200 mm do piso, uma gaveta por módulo, cuba de apoio.
 - * Portas por módulos, abridoras pela altura (2 até 900, 3 até 2.500, 4 até 2.800, 5 acima).
 - * Prateleira trançada e arcos de porta. Puxador perfil gôto grafite nas portas sociais.

PROJETO PORTO REAL

RESIDENCIA UNIFAMILIAR | MARAULIS - AM | SOBR TATIANA-PS

PROJETO ARQUITETONICO

MARCENARIA I — GABINETES DE COZINHA, GOURMET, OFICINA E BANHOS

BASE GEOMETRICA	ESCALA	EMISSAO	PROJECION
União Consolidada	1:40 • 1:10	ESTUDIO PRELIMINAR RES	56
Projeto (preliminar)	FORMATO A1	NAO LIBERADO PARA OBRA	SEM ART / PRINT
UNIDADE METRICA: MM	MILIMETROS (MM)		IN-TE REVIEW