


LISTA DE MATERIAL — TOTAIS

ITEM	QTD	UN
Cabo 1,5 mm² PE	628,4	m
Cabo 1,5 mm² Isar	628,4	m
Cabo 1,5 mm² neutro	628,4	m
Cabo 2,5 mm² PE	198,6	m
Cabo 2,5 mm² Isar	86,4	m
Cabo 2,5 mm² neutro	55,7	m
Cabo 4 mm² PE	130,5	m
Cabo 4 mm² Isar	187,8	m
Cabo 4 mm² neutro	92,9	m
Cabo 6 mm² PE	22,7	m
Cabo 6 mm² Isar	45,5	m
Atrelados corrigidos OND	1271,4	m
Atrelados corrigidos OND	145,5	m
diâmetro 10 A 2P curva C	21	un
diâmetro 10 A 2P curva C	10	un
diâmetro 10 A 2P curva C	2	un
diâmetro 10 A 2P curva C	3	un
diâmetro 20 A 2P curva C	16	un
diâmetro 20 A 2P curva C	1	un
diâmetro 20 A 2P curva C	4	un
diâmetro 40 A 2P curva C	2	un
DPE 4P 40 A 30 mA	3	un
DPS classe II 100 mA, 3P+N	1	un
diâmetro geral 120 A repetidor	1	un
diâmetro 120 A repetidor (desmembrado de QDS)	1	un
Quadro geral de módulos — QDS	1	un
Quadro superior de módulos — QDS	1	un
Unidade 2P+1 10 A (10T V)	82	un
Unidade 2P+1 20 A (20T V, TUE)	26	un
Unidade 2P+N (20A)	39	un
Unidade 2P+N (20A)	58	un
Cabo 4 x 2	140	m

POR CIRCUITO — 59

CIRC	QD	mm2	CABO m	ELETRE	m	DISJ	TOM	INT	LUC
TUE-06	QDS	6	2,4	ON20	1,1	20 A 2P	1	0	0
TUE-22	QDS	6	51,5	ON25	20,5	40 A 2P	1	2	0
TUE-3	QDS	4	5,7	ON20	1,9	20 A 2P	1	0	0
TUE-2	QDS	4	28,0	ON25	13,0	20 A 2P	1	0	0
TUE-5	QDS	4	32,4	ON20	10,9	20 A 2P	1	0	0
TUE-4	QDS	4	28,7	ON20	10,2	20 A 2P	1	0	0
TUE-23	QDS	2,5	36,8	ON20	18,9	20 A 2P	1	0	0
TUE-1-GOU	QDS	4	19,8	ON20	26,5	20 A 1P	12	0	0
TUE-10	QDS	2,5	48,8	ON20	18,2	10 A 2P	1	0	0
TUE-1-CCZ	QDS	4	19,6	ON20	23,5	20 A 1P	10	0	0
TUE-1	QDS	2,5	28,5	ON20	12,8	20 A 2P	1	0	0
TUE-1-COR	QDS	2,5	46,0	ON20	15,3	20 A 1P	5	0	0
TUE-1-LAY	QDS	2,5	58,3	ON20	18,4	20 A 1P	4	0	0
TUE-1-DEP	QDS	2,5	61,2	ON20	20,4	20 A 1P	2	0	0
TUE-12	QDS	2,5	67,2	ON20	22,4	20 A 1P	1	0	0
TUE-14	QDS	2,5	50,9	ON20	17,9	20 A 1P	1	0	0
TUE-5	QDS	2,5	39,9	ON20	5,8	20 A 2P	1	0	0
TUE-7	QDS	2,5	41,3	ON20	13,8	20 A 2P	1	0	0
TUE-6	QDS	2,5	28,9	ON20	9,8	20 A 2P	1	0	0
TUE-8	QDS	2,5	34,7	ON20	11,6	20 A 2P	1	0	0
ELU-1-BAH	QDS	1,5	48,0	ON20	18,5	20 A 1P	0	4	0
TUE-15	QDS	2,5	35,4	ON20	16,9	20 A 1P	1	0	0
TUE-16	QDS	2,5	19,3	ON20	23,4	20 A 1P	1	0	0
ELU-1-GAR	QDS	1,5	42,2	ON20	14,1	20 A 1P	0	3	0
ELU-1-GOU	QDS	1,5	51,2	ON20	30,4	20 A 1P	0	3	0
TUE-20	QDS	2,5	26,5	ON20	8,8	20 A 1P	1	0	0
TUE-24	QDS	2,5	27,7	ON20	8,2	20 A 2P	1	0	0
TUE-17	QDS	2,5	115,2	ON20	36,4	20 A 2P	1	0	0
ELU-1-SOC	QDS	1,5	107,3	ON20	19,1	20 A 1P	0	3	0
ELU-1-ROZ	QDS	1,5	45,9	ON20	15,3	20 A 1P	0	3	0
ELU-1-ESP	QDS	1,5	44,1	ON20	14,7	20 A 1P	0	3	0
TUE-15-BAH	QDS	2,5	35,5	ON20	12,2	20 A 1P	0	0	0
TUE-1-GAR	QDS	2,5	33,8	ON20	11,2	20 A 1P	0	0	0
TUE-1-OPH	QDS	2,5	38,2	ON20	10,1	20 A 1P	0	0	0
TUE-1-SOC	QDS	2,5	31,9	ON20	10,6	20 A 1P	0	0	0
ELU-1-COR	QDS	1,5	40,2	ON20	21,8	20 A 1P	0	2	0
TUE-1-ROZ	QDS	2,5	38,1	ON20	12,7	20 A 1P	0	0	0
TUE-1-ROZ	QDS	2,5	23,7	ON20	7,9	20 A 1P	0	0	0
TUE-15	QDS	2,5	14,8	ON20	18,2	20 A 2P	1	0	0
TUE-16	QDS	2,5	27,6	ON20	9,2	20 A 2P	1	0	0
TUE-20	QDS	2,5	28,5	ON20	12,2	20 A 2P	1	0	0
TUE-19	QDS	2,5	61,5	ON20	27,0	20 A 1P	1	0	0
ELU-1-REV	QDS	1,5	41,7	ON20	13,9	20 A 1P	0	2	3
TUE-1-REV	QDS	2,5	32,8	ON20	10,9	20 A 1P	4	0	0
ELU-1-COR	QDS	1,5	60,4	ON20	20,1	20 A 1P	0	2	3
TUE-1-BAH	QDS	2,5	14,8	ON20	3,9	20 A 1P	0	0	0
ELU-1-BAH	QDS	1,5	33,5	ON20	6,5	20 A 1P	0	1	2
TUE-1-BAH	QDS	2,5	24,3	ON20	6,1	20 A 1P	0	0	0
TUE-1-GOU	QDS	2,5	24,0	ON20	6,6	20 A 1P	0	0	0
TUE-21	QDS	2,5	6,1	ON20	2,0	20 A 1P	1	0	0
ELU-1-BAH	QDS	1,5	28,9	ON20	7,5	20 A 1P	0	1	2
TUE-1-ALC	QDS	2,5	33,0	ON20	6,5	20 A 1P	0	0	0
TUE-1-COR	QDS	2,5	23,7	ON20	7,9	20 A 1P	2	0	0
ELU-1-OPH	QDS	1,5	41,4	ON20	13,9	20 A 1P	0	1	2
ELU-1-LAY	QDS	1,5	60,2	ON20	20,1	20 A 1P	0	1	2
ELU-1-GOU	QDS	1,5	28,0	ON20	9,5	20 A 1P	0	1	2
ELU-1-ALC	QDS	1,5	25,1	ON20	5,8	20 A 1P	0	1	1
ELU-1-COR	QDS	1,5	28,0	ON20	6,7	20 A 1P	0	1	1
ELU-1-DEP	QDS	1,5	63,3	ON20	21,1	20 A 1P	0	1	1

SISTEMA FOTOVOLTAICO — DIAGRAMA

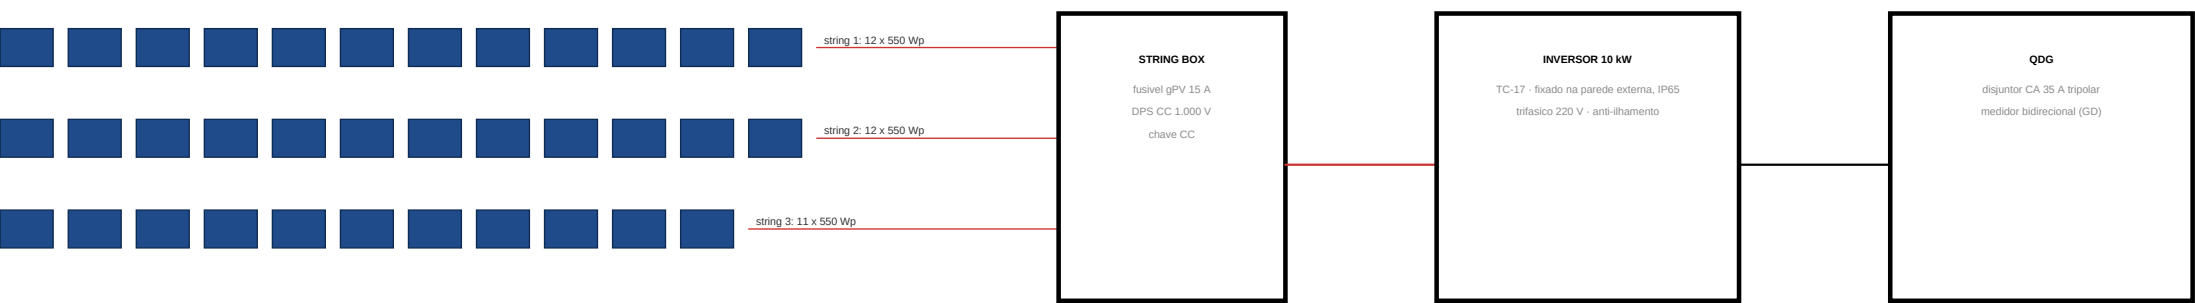

PASSAGEM DOS CABOS SOLARES

Colocação dos cabos (PVC, sem revestimento) e dos cabos (PVC, com revestimento) em eletrodutos PVC OND (apresenta proteção)
→ TC 17 x 1,500 mm de peso 10,8 m de parafusos e 2 conectores + PVC
instalação: 10 metros de cabo e 10 metros de parafusos e 2 conectores + PVC
apresentação dos dados de instalação (TC 17 x 1,500 mm)

NOTAS

- Cada linha de lista de material vem da soma dos circuitos de PE-00: cabo por seção e cor (base na cor da base, neutro azul, PE verde), eletroduto por diâmetro, diâmetro por concreto e poço.
- Complementos por parafusos: instalação do quadro de controle do ambiente e 1,2 (linha inferior de instalação, como em instalações) mais descida e subida.
- Fotovoltaico: 67,5 kWh/m² = 38,8 kWh = 38 módulos de 100 Wp em 3 strings, inversor 10 kW (TC 17) na linha técnica nota.
- Cabo de 1,5 mm² 1,8 m em eletroduto (preço da cobertura do inversor, string box com fusível, DPS CC e classe secundária, diâmetro CA no QDS).

PROJETO PORTO REAL

RESIDÊNCIA UNIFAMILIAR (MANSÃO - AM) | SOUS TATIANA-PS

PROJETO ARQUITETÔNICO

ELETRICA — MATERIAL POR CIRCUITO E SISTEMA FOTOVOLTAICO

BASE GEOMÉTRICA Lista Consolidada em PDF (previsão) UNIDADE: MESTRE - AM	ESCALA s/ escala FORMATO: A1 MATERIAL: 600/600/600	EMISSÃO ESTUDO PRELIMINAR RES TUDO LIBERADO PARA OBRA SEM ART / INT	PROVA 61 em 18 REV (RES)
---	---	--	--------------------------------