




1 CORTE LONGITUDINAL (SUL -> NORTE)
ESCALA 1:25

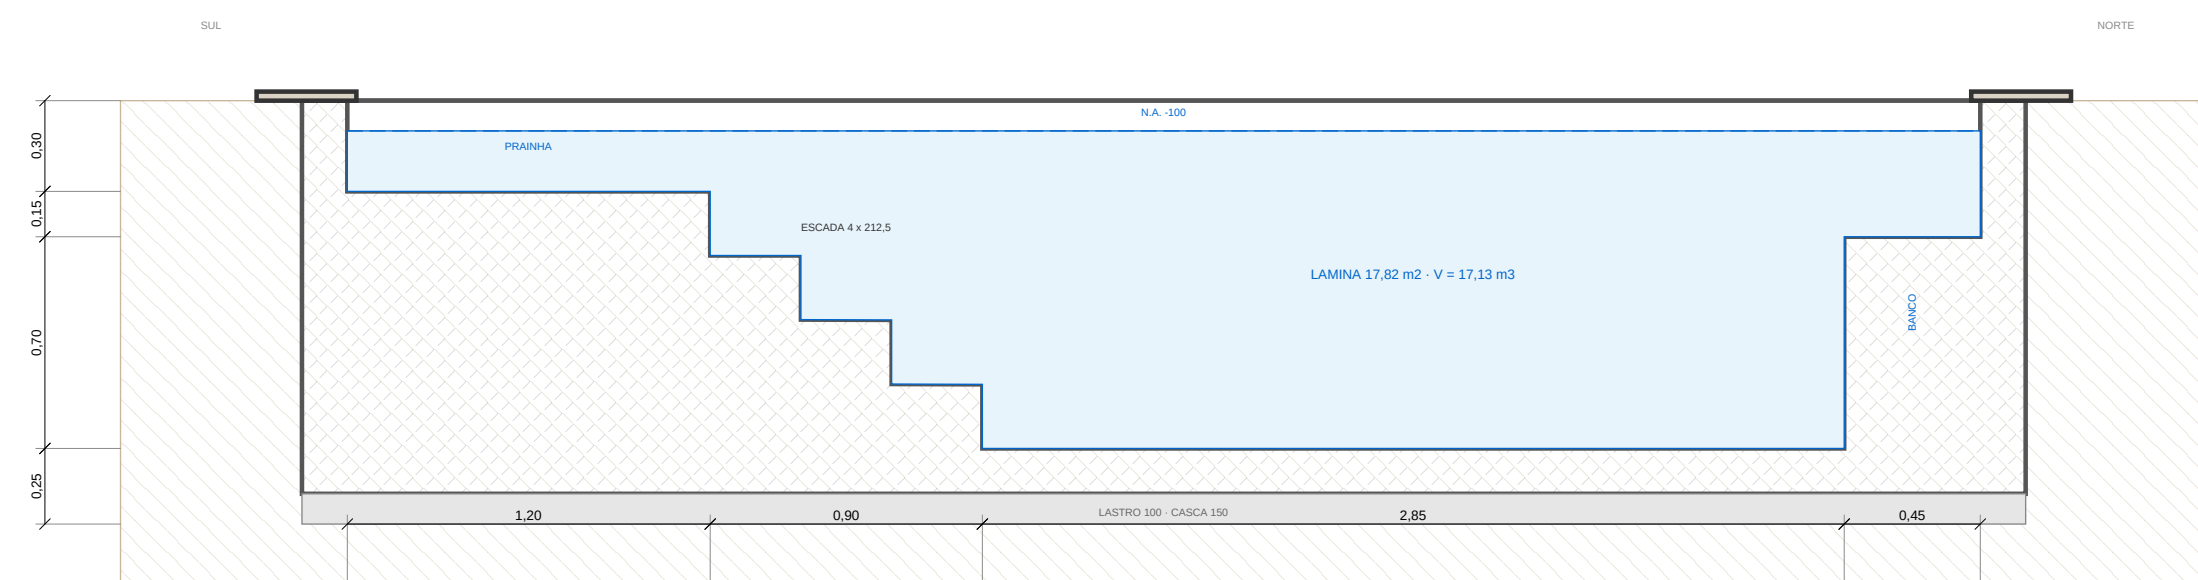


2 CORTE TRANSVERSAL PELO DRENO (LESTE -> OESTE)
ESCALA 1:25

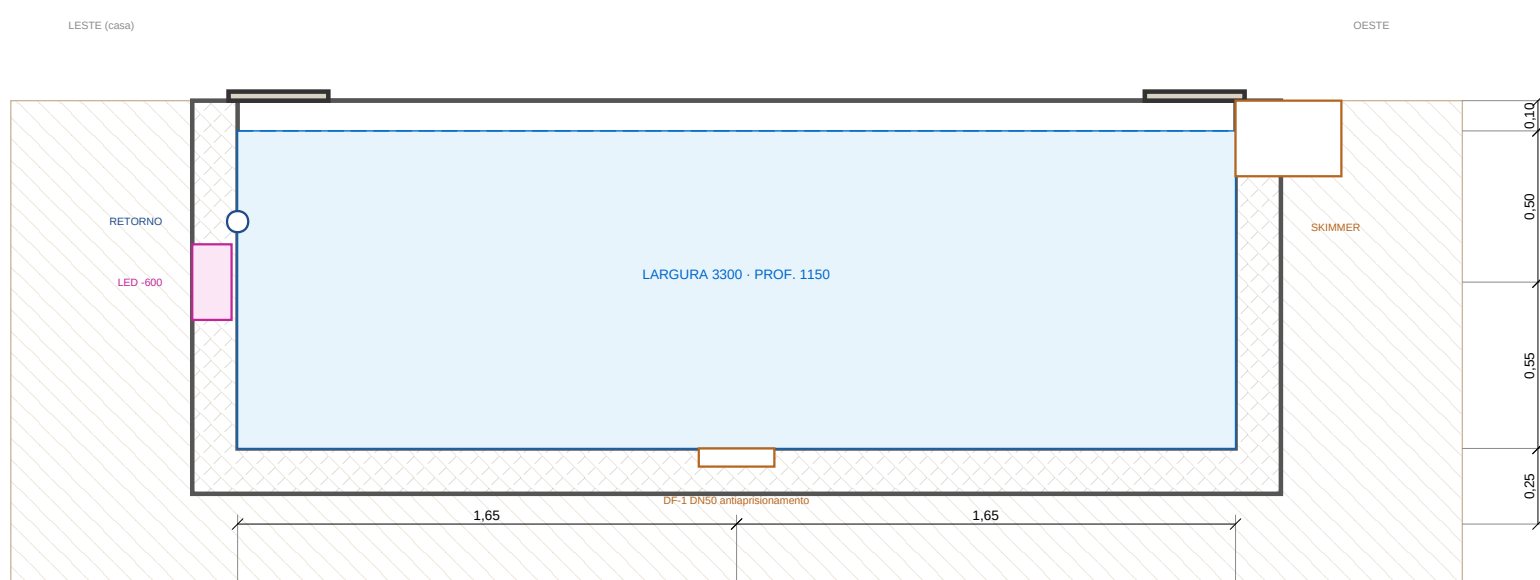


3 ESCADA DE PRAIA
ESCALA 1:10

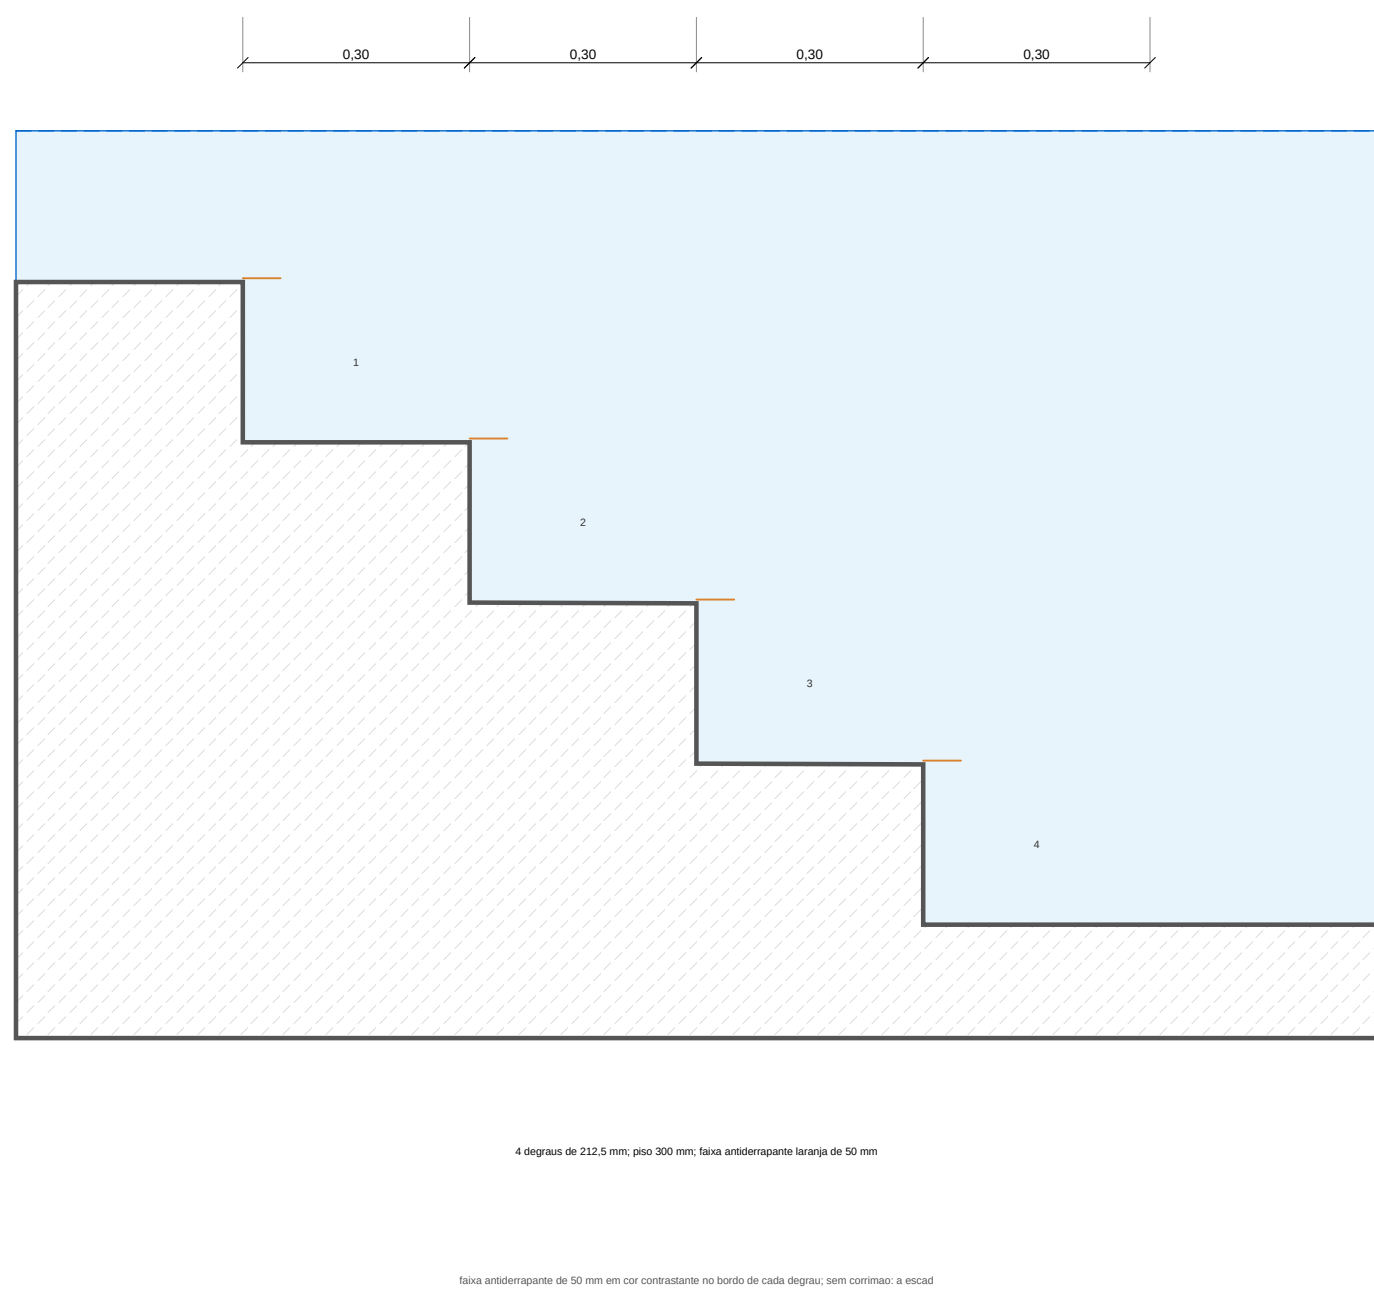


4 BORDA COM PINGADEIRA E FAIXA SECA
ESCALA 1:5

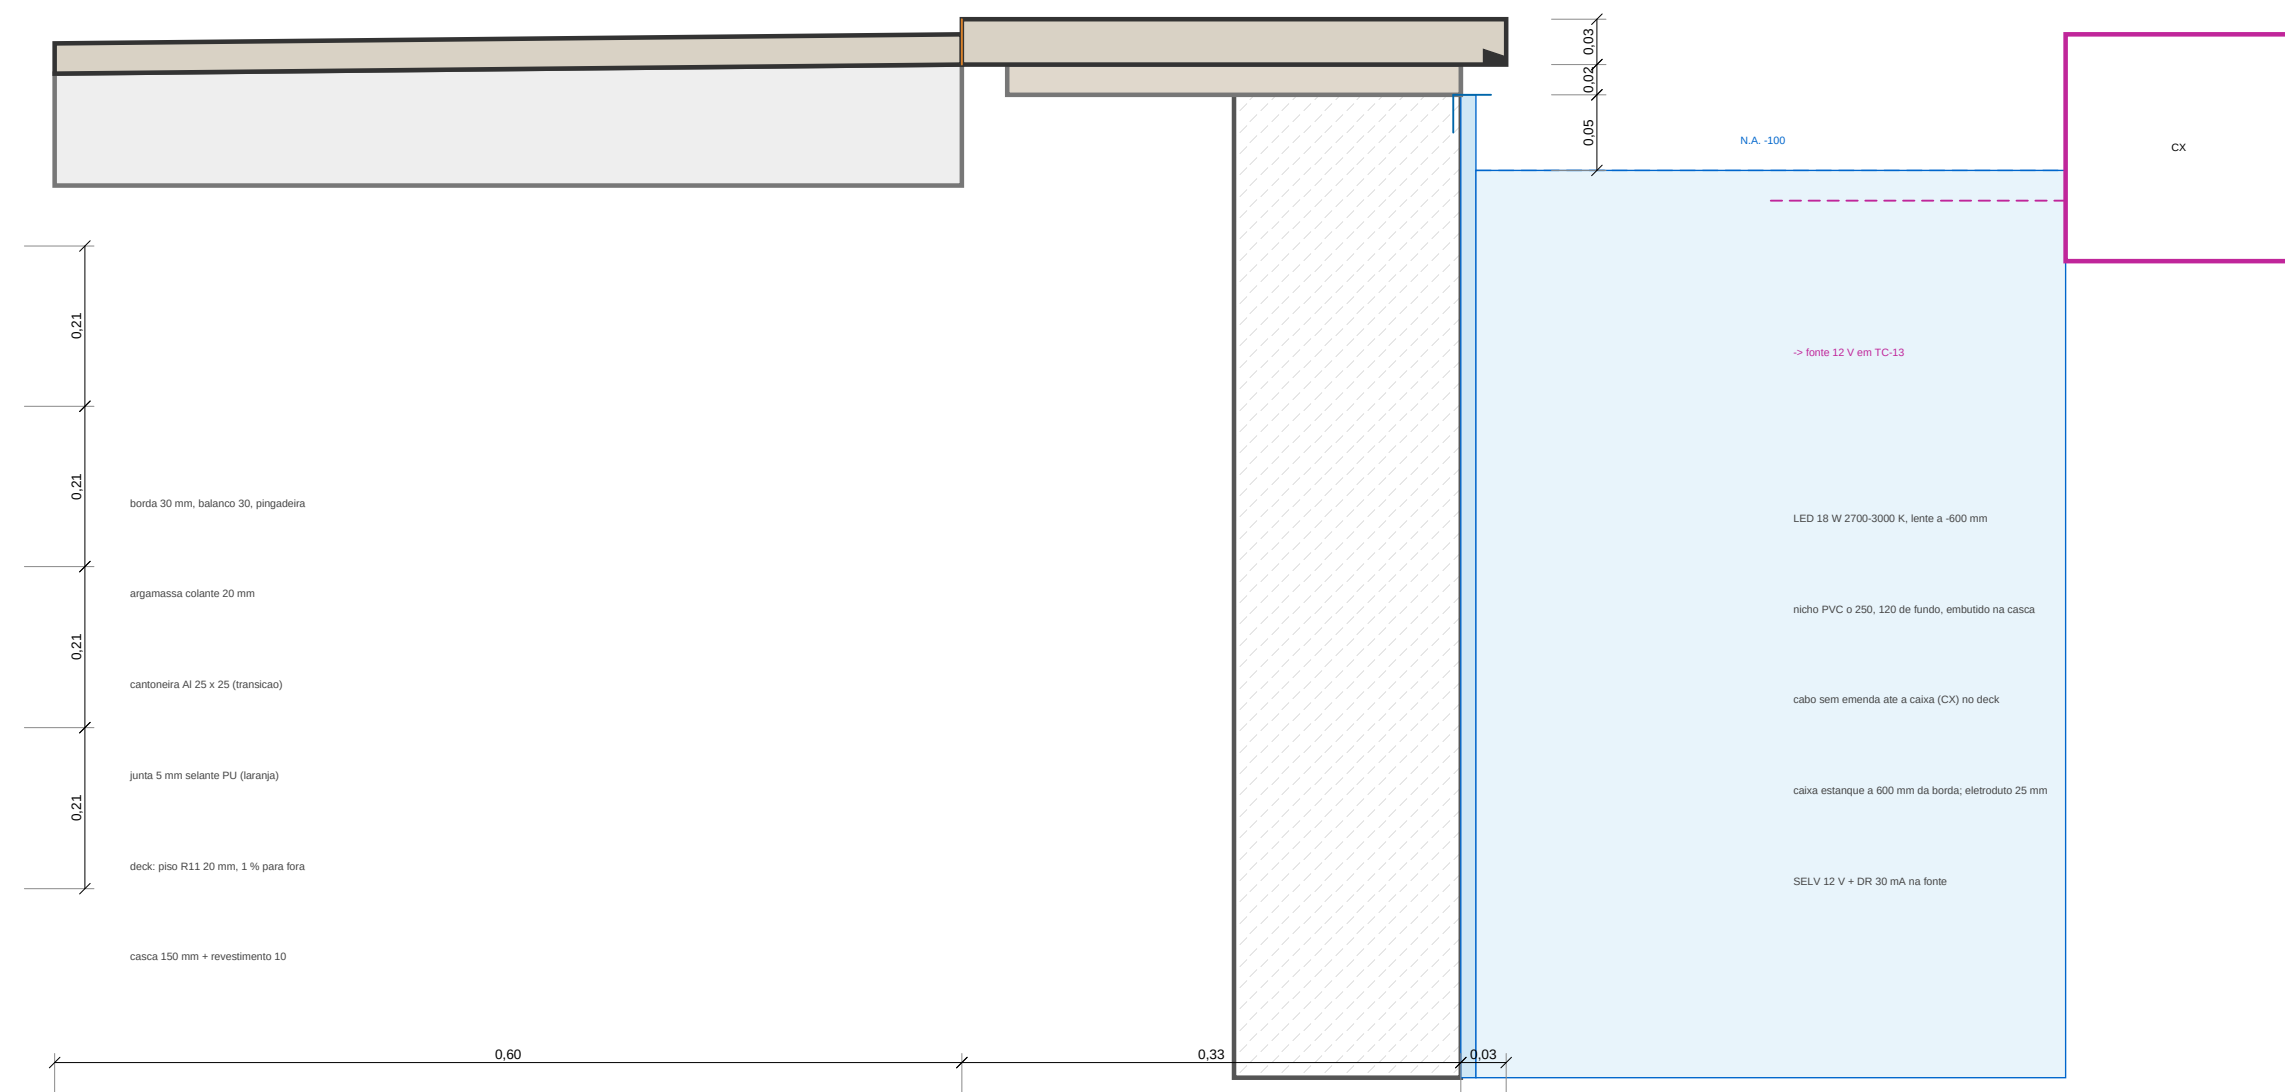

5 NICHOS DO LED E CAIXA DE PASSAGEM
ESCALA 1:5

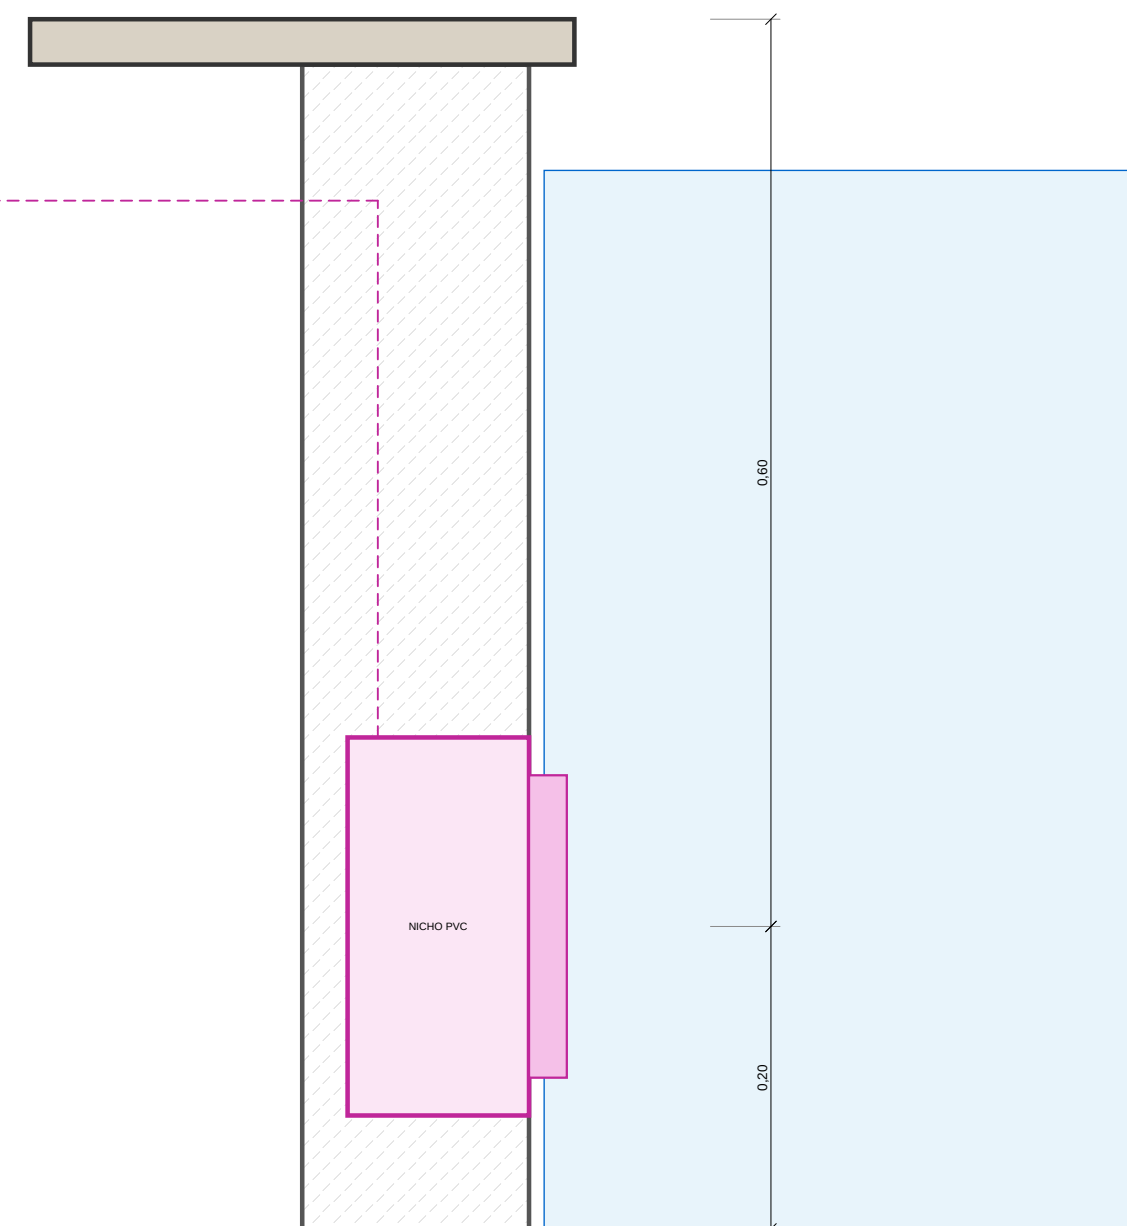

6 PLANTA DE ILUMINACAO SUBAQUATICA
ESCALA 1:50

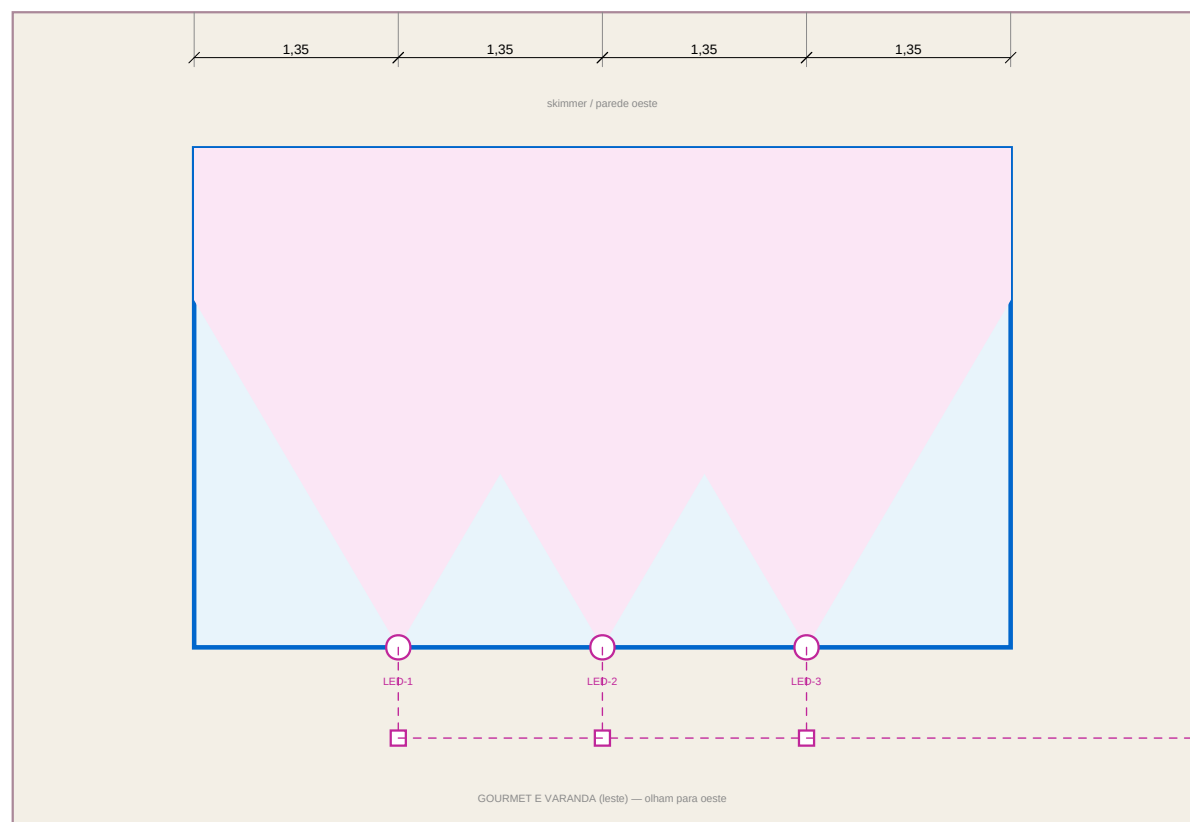

NOTAS

- Nível da água: 100 mm (plântero); Planta 30 mm; espada de grão 45 graus (222,5 x 100 mm) na largura mínima; Turbido 1150 mm; barco com assento a 450 mm.

- Calçados: concreto armado 30 cm SPA, cota de 150 mm, via água 0 m ± 12 (11), laje 100 mm; fundo de escavacao a - 1400 mm; Impermeabilizacao: cristalinizante no concreto fresco + argamassa polimerica biocomponente em 2 demãos (p); teste de estanqueidade de 72 h antes do revestimento.

- Borda: 600 x 200 x 20 mm, parafusado 1/2" da lava sobre, bordo bicoado e parguado, de 40 a 100 cm ± 10 para fora da piscina, furação: 3 L200 X200 X4 a 500 mm, SELV 12 V, 3,00 W/Hz.

- Numero marcação (p): sap liq/tenes de praga ltradas da MBR 10339 a praca de piscina númerada.

PROJETO PORTO REAL

RESIDÊNCIA UNIFAMILIAR | MANAUS - AM | SU16 TARUMA 9

PROJETO ARQUITETÔNICO

PISCINA: CORTES, ESCADA, BORDA E ILUMINACAO

BASE GEOMETRICA	ESCOLA	EMISSAO	FRANCIA
Lista Consolidada	indicada	ESTUDIO PHILIMINAR REI	70
por R32 (previsão)	FORMATO A1	NÃO LIBERADO PARA OBRA	de 75 REV 75
UNIDADE MEDIDA: m2	MALHA 400/200/100	NEW ART / 1987	