


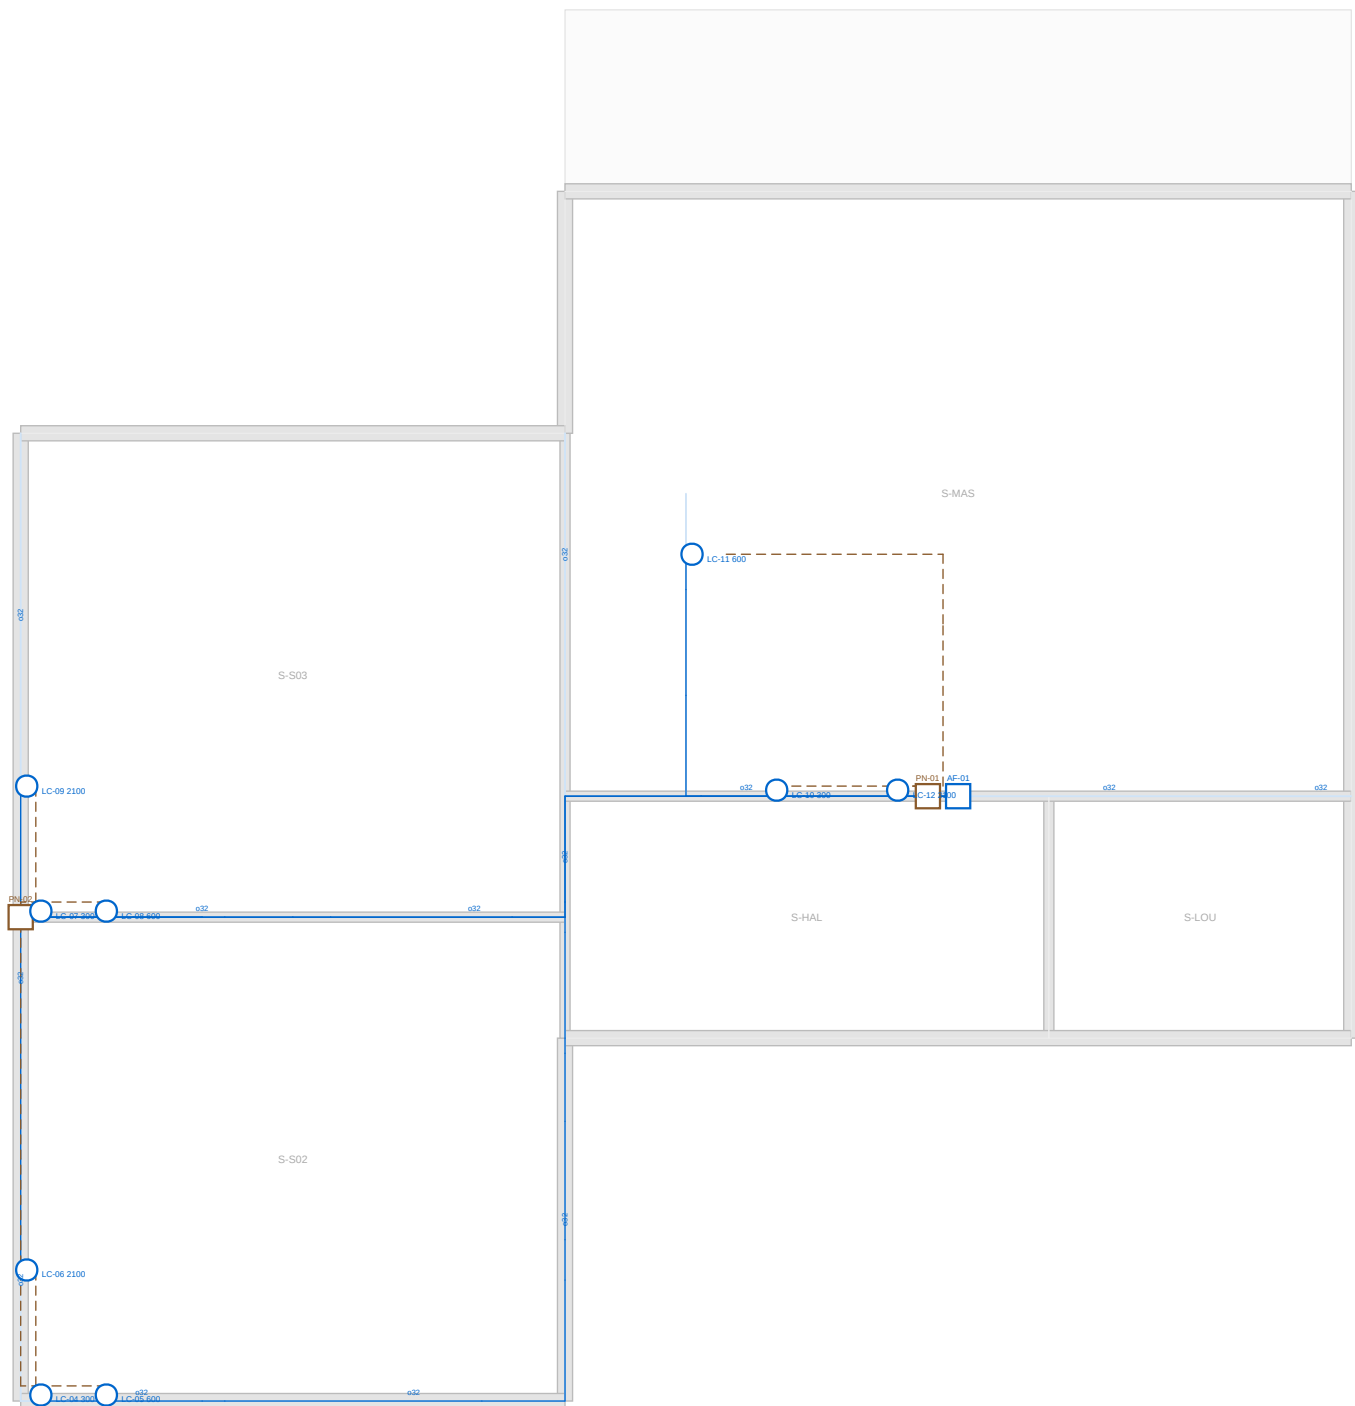

2 AGUA (azul, a 400 mm) E ESGOTO (marrom, sob o piso) — SUPERIOR  
ESCALA 1:75

| CDM        | DMR                              | TIPO                                           |
|------------|----------------------------------|------------------------------------------------|
| RG-GERAL   | saída do manufatureiro (Zanties) | registro de gerente + validade de retenção DCM |
| RG-COL-5   | saída do colante                 | registro de gerente DCM                        |
| RG-COL-7   | saída do lenço                   | registro de gerente DCM                        |
| RG-T-COR   | entrada do corral do T-COR       | registro de gerente DCM                        |
| RG-T-REV   | entrada do corral do T-REV       | registro de gerente DCM                        |
| RG-S-302   | entrada do corral do S-302       | registro de gerente DCM                        |
| RG-S-303   | entrada do corral do S-303       | registro de gerente DCM                        |
| RG-S-MAS   | entrada do corral do S-MAS       | registro de gerente DCM                        |
| RG-T-LAV   | entrada do corral do T-LAV       | registro de gerente DCM                        |
| RG-T-DEP   | entrada do corral do T-DEP       | registro de gerente DCM                        |
| RG-T-COE   | entrada do corral do T-COE       | registro de gerente DCM                        |
| RG-T-COL-1 | entrada do corral do T-COL-1     | registro de gerente DCM                        |
| RG-T-DEP   | entrada do corral do T-DEP       | registro de gerente DCM                        |
| RP-LOC09   | box LC-09                        | registro de pressão DCM                        |
| RP-LOC06   | box LC-06                        | registro de pressão DCM                        |
| RP-LOC08   | box LC-08                        | registro de pressão DCM                        |
| RP-LOC12   | box LC-12                        | registro de pressão DCM                        |
| RP-DE05    | ducha externa DTA-01             | registro de pressão DCM                        |

| ITEM                                                           | QTD | UN |
|----------------------------------------------------------------|-----|----|
| Luva de proteção no tamanho de 32 cm (prestar atenção tamanho) | 300 | un |
| cap de PEX no tamanho (a cada 600 mm)                          | 275 | un |
| cap de PEX no tamanho (a cada 600 mm)                          | 36  | un |
| barra de fixação entre montantes + pedão de transição única    | 21  | un |
| anel de amarração de engates a tela do radier (a cada 1,5 m)   | 52  | un |
| abrazadeira isolante de engates no entalhe (a cada 1,5 m)      | 24  | un |

## NOTAS

- PEI C/NDZ da coluna AF-01 ate cada peça, DENTRO da parede a 400 mm por furo de 32 mm (que a fabricacao passa a abrir em 26 mm); sobre na parede ate a peça, 123,5 m em 30 montantes admissíveis.

- C/igoto NUNCA em montante (DN05 e mais e furo maior que meia alça). 69,2 m sob o piso — enfiado no radier, entre as vigas no entrego — ate o pramado ou a canal, so o pramado e vertical (F14-02).

- Mude de secção: 64 paredes levam electrica eixo agua. Pareda de obra, parafuso de placa a furo de montador furo das faldas 300-490 (agual) e 1.400-1.500 mm (diagonal); as verticais ficam juntas aos pontes.

- Flange (e/la) lava no rator, clip de PEIX a cada 600 mm, barra de fixacao entre montantes em cada peço, engoto amarrado a tela do radier a cada 1,5 m e em abstracções isoladas a cada 1,0 m no entrego.