


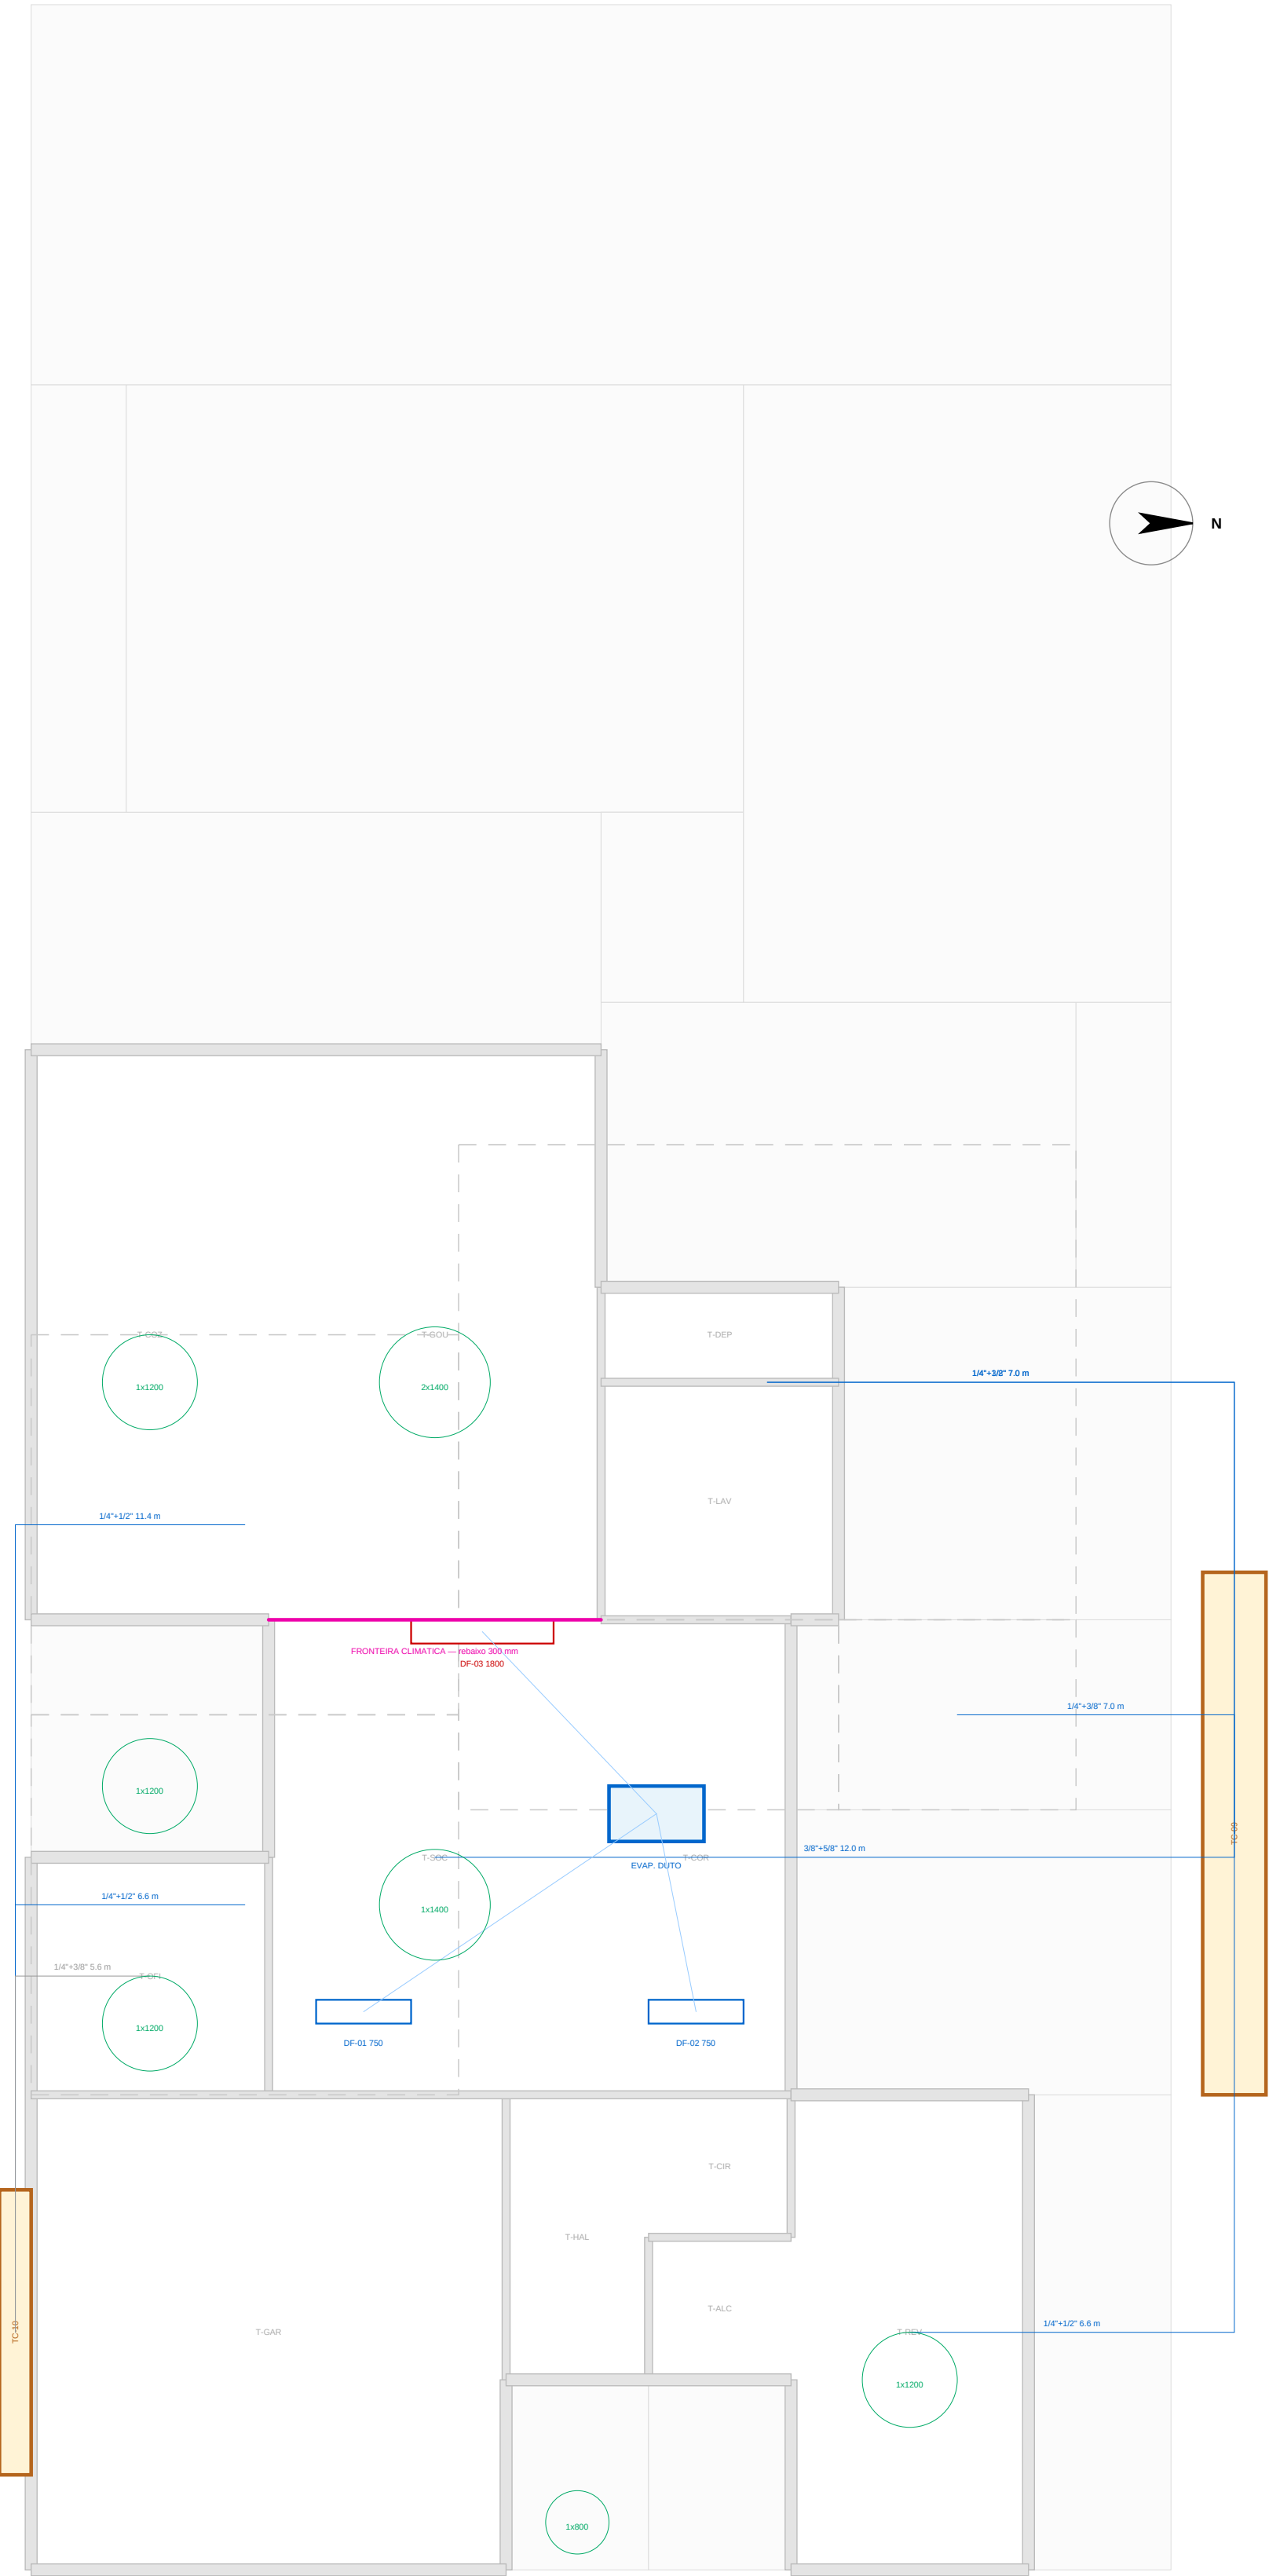

1 PERCURSO DAS LINHAS E DUTOS
ESCALA 1:75

LINHAS FRIGORÍGENAS — PERCURSO E BITOLA

LINHA	AMB	INCHO	BTUM	NOME (H)	BUBIDA (H)	TOTAL (H)	SUCCASOLU	DRENO	CARGA EXTRA	FASE
S-MA5	S-MA5	TC-09	18.000	1,6	3,9	7,0	14'7"12"	CH25	—	ABR
T-REV	T-REV	TC-09	18.000	2,2	2,9	6,6	14'7"12"	CH25	—	ABR
S-SE2	S-SE2	TC-10	18.000	1,2	3,9	6,8	14'7"12"	CH25	—	ABR
S-SE3	S-SE3	TC-10	18.000	6,0	3,9	11,4	14'7"12"	CH25	80 g	ABR
S-SDC	T-SDC	TC-08	20.000	1,6	2,9	11,0	38'7"08"	CH25	80 g	ABR
S-LDV	S-LDV	TC-09	9.000	1,6	3,9	7,0	14'7"38"	CH25	—	ABR
PFCE	S-MA5	TC-09	9.000	1,6	3,9	7,0	14'7"38"	CH25	—	ABR
T-OR	T-OR	TC-10	9.000	1,2	2,9	9,6	14'7"38"	CH25	—	ABR

DUTOS, DIFUSORES E EXAUSTÃO			
ELEMENTO	VIAJADA (mm)	DNOM	OBSERVAÇÃO
DF-01 — insulflex	750	T-SDC	junto parede contra do motor
DF-02 — insulflex	750	T-COR	com tubo o pouco de luz

(continuação)

ELEMENTO	VIAJADA (mm)	DNOM	OBSERVAÇÃO
DF-03 — insulflex	80	T-COR	CH25
DF-04 — insulflex	80	T-REV	CH25
DF-05 — insulflex	120	T-LDV	CH25, nota amplitude da instalação a 30.000
DF-06 — insulflex	120	S-MA5	CH25
DF-07 — insulflex	80	S-SE2	CH25, instalado contra do tubo vazio, com grampo de 6

- NOTAS
- Dots rictos de condensação. Linha mais longa 12.0 m, contra o limite de contorno de 15 m.
 - Dreno CH25 com diâmetro mínimo de 25% e altura antes da descarga, nunca ligado a engelo sem água.
 - Duto de insulflex no comprimento de 400 mm — nunca abreviar montado.
 - Isolamento contínuo na travessa de parede, com bucha de passagem, com de isolamento na parede condensa dentro da montante.

PROJETO PORTO REAL

RESIDENCIA UNIFAMILIAR (MANSÃO - AM) (SOLUÇÕES - PM)

PROJETO ARQUITETÓNICO

CLIMATIZAÇÃO — LINHAS FRIGORÍGENAS, DUTOS E DRENOS

BASE GEOMÉTRICA	ESCALA	EXAUSTÃO	PROVA
Linha Consolidada	1:75	ESTUDO PRELIMINAR RT2	28
PROJETO (previsão)	FORMATO A1	NOVO LIBERADO PARA OBRAS	SEM ART / INT
UNIDADE MÉTRICA (mm)	VALORES (mm/1000)	SEM ART / INT	64 REV RT2