


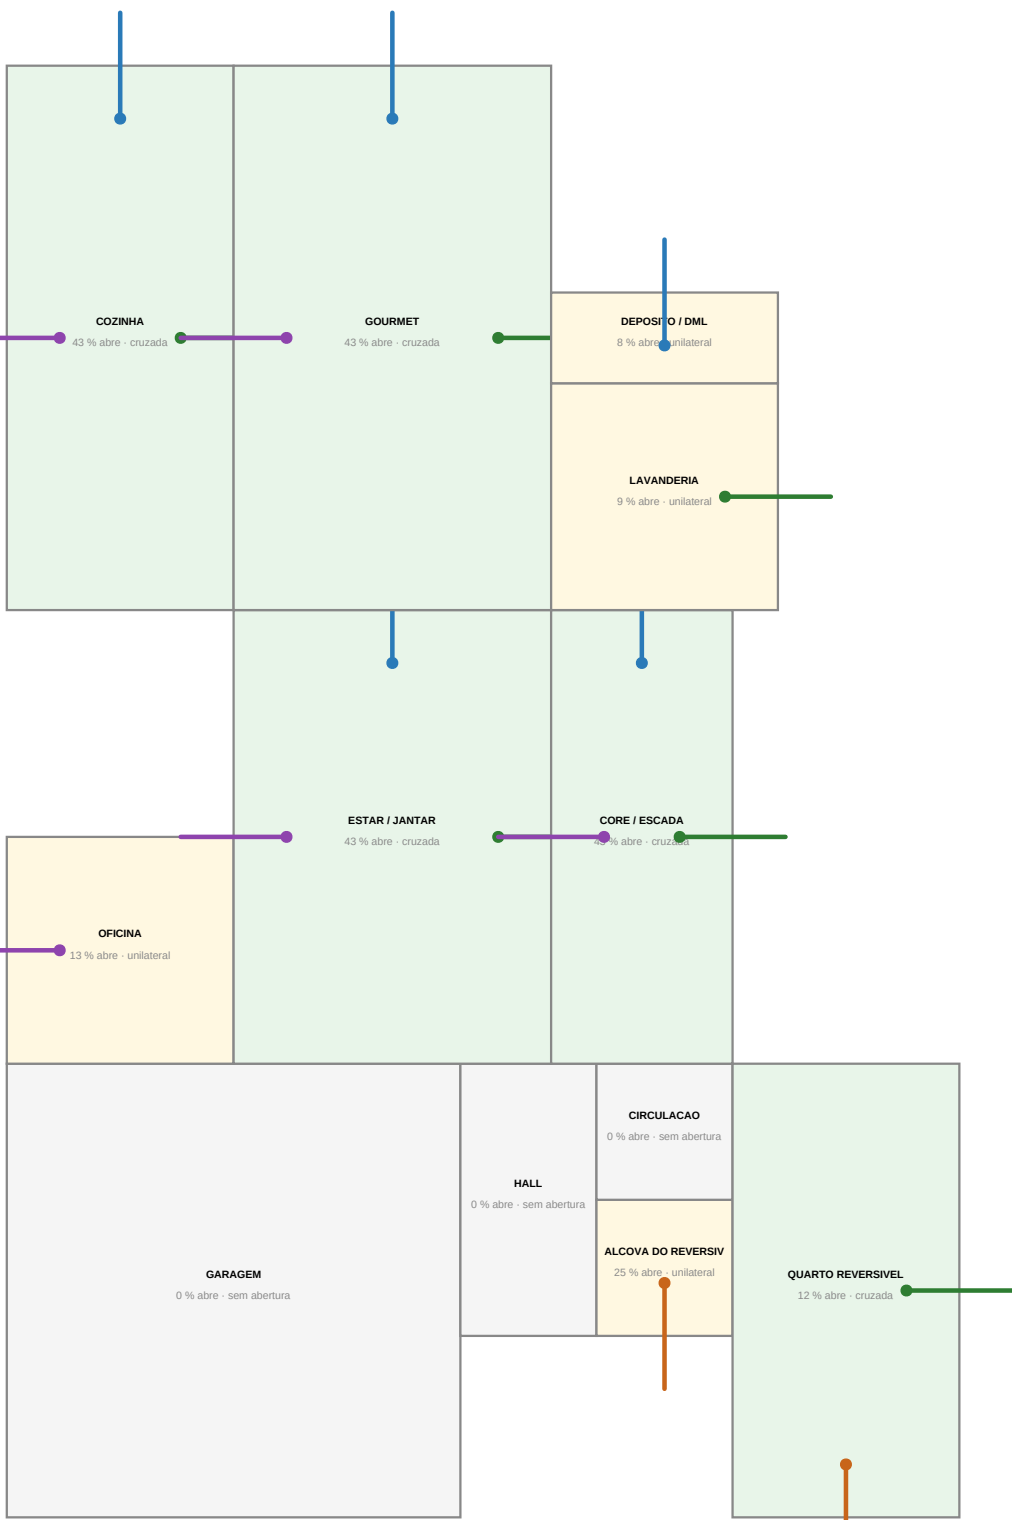


1 TERREO — faces que abrem
ESCALA 1:100

VENTILACAO POR AMBIENTE									
COD	AMBIENTE	CAT.	PRO.ME	ABRE.ME	PERIM.	FACIES	TIPO	ISOV	
T-GAR	GARAGEM	INTER	34,3	0,00	0%	—	—	YES	
T-HALL	HALL	INTERNO	9,9	0,00	0%	—	—	YES	
T-FALC	ALCOVA DO REVERSIVEL	INTERNO	2,9	0,72	25%	L	unidirecional	OK	
T-COR	CIRCULACAO	INTERNO	2,9	0,00	0%	—	—	YES	
T-REV	QUARTO REVERSIVEL	INTERNO	26,7	2,04	22%	L, N	cruzada	OK	
T-OFI	OFICINA	INTERNO	43	1,08	23%	S	unidirecional	YES	
T-BOC	ESTAR/JANTAR	INTERNO	86,7	36,86	43%	N, D, S	cruzada	OK	
T-COR	CORR. E ESCADA	INTERNO	86,7	36,86	43%	N, D, S	cruzada	YES	
T-COZ	COZINHA	INTERNO	86,7	36,86	43%	N, D, S	cruzada	OK	
T-GOU	GOURMET	INTERNO	86,7	36,86	43%	N, D, S	cruzada	OK	
T-LAV	LAVANDERIA	INTERNO	6	0,72	9%	N	unidirecional	YES	
T-DEP	DEPOSITO DmL	INTERNO	3,1	0,24	8%	O	unidirecional	YES	
S-S02	SUITE 02	INTERNO	26,5	2,04	8%	L, S	cruzada	OK	
S-S03	SUITE 03	INTERNO	26,7	2,04	8%	O, S	cruzada	OK	
S-HALL	HALL E REPOUSAR	INTERNO	10,8	0,00	0%	—	—	YES	
S-LOU	MINI LOUNGE / TV	INTERNO	6,5	0,72	11%	N	unidirecional	OK	
S-MAST	SUITE MASTER	INTERNO	45,1	7,80	17%	N, D, S	cruzada	OK	

PRIVACIDADE — CADA JANELA CONTRA A DIVISA QUE OLHA (art. 1.301 CC)

VIAJ	AMB	FACIE	ISOV.M	AMB.M	PROT.M	BRIS	LEITURA	
004	T-REV	N	0,00	1,00	1000	—	distante	OK
002	T-COR	N	0,00	1,00	1000	—	distante	OK
005	T-REV	L	2,20	—	1100	BR-L	nao	OK
001	T-REV	N	0,00	1,00	1100	—	distante	OK
001	T-FALC	L	0,60	—	1100	—	nao	OK
003	T-COR	S	3,40	1,00	1100	—	exposta ao vento	OK
001	T-COZ	S	3,40	1,00	1100	—	exposta ao vento	OK
001	T-LAV	N	7,40	1,00	1100	—	distante	OK
004	T-DEP	O	36,90	1,00	1000	—	distante	OK
PRO2	T-COR	N	8,00	1,00	9	—	distante	OK
PRO2	T-GOU	N	10,40	1,00	9	—	distante	OK
CRO5	T-GOU	O	13,00	1,00	9	BR-O	protetida por terra	OK
PRO2	T-BOC	S	9,40	1,00	9	—	distante	OK
001	S-LOU	N	4,40	1,00	1100	—	distante	OK
005	S-S02	S	3,40	1,00	1100	—	exposta ao vento	OK
001	S-S02	L	13,20	—	1100	BR-L	nao	OK
004	S-S02	L	13,20	—	1200	BR-L	nao	OK
005	S-S03	S	3,40	1,00	1100	—	exposta ao vento	OK
001	S-S03	O	17,20	1,00	1100	—	distante	OK
004	S-S03	S	2,40	1,00	1000	—	exposta ao vento	OK
005	S-MAST	S	7,80	1,00	1100	—	distante	OK
PRO2	S-MAST	O	14,80	1,00	9	—	distante	OK
004	S-MAST	N	4,40	1,00	1000	—	distante	OK
001	S-MAST	N	4,40	1,00	1100	—	distante	OK

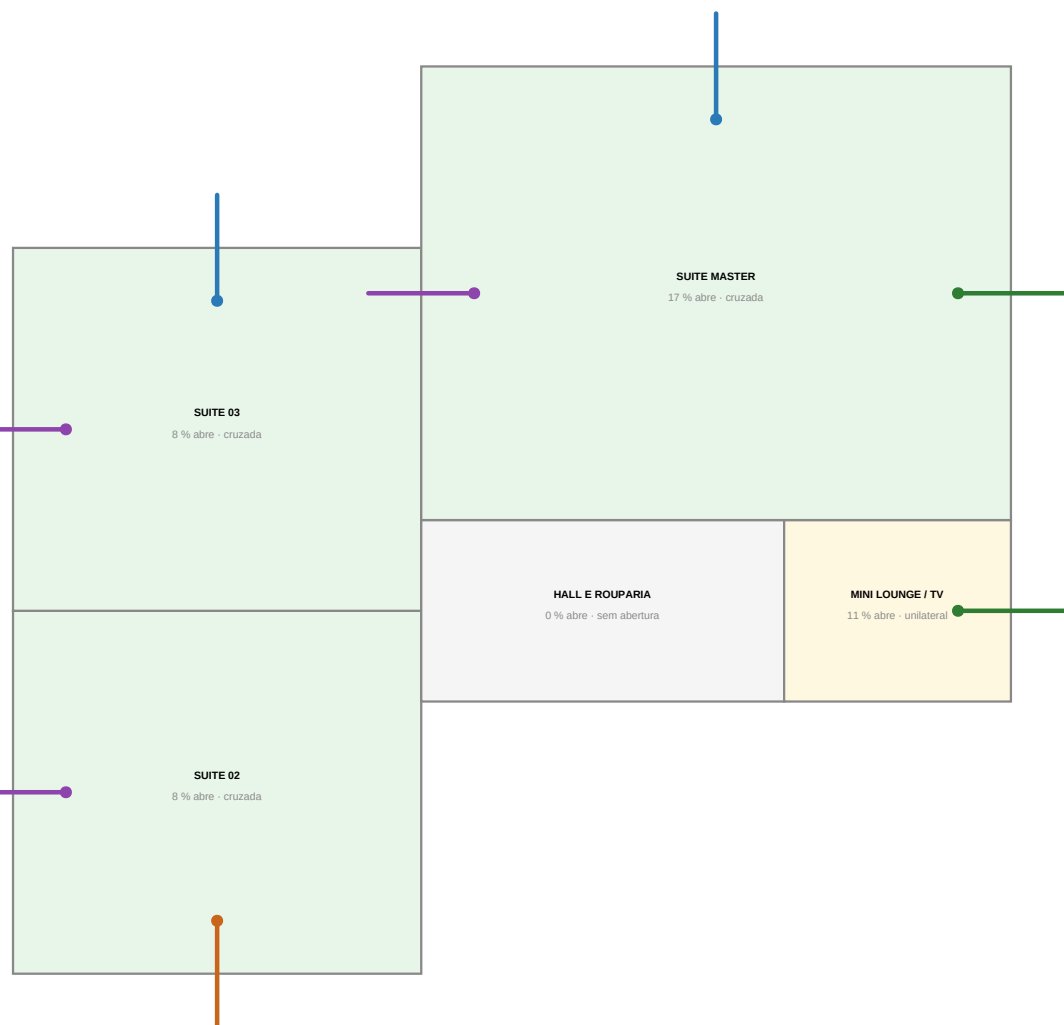

2 SUPERIOR — faces que abrem
ESCALA 1:100

NOTAS

¹ Área que ABRE por ambiente contra a área do piso. NBR 15275-4 exige 0% na região Norte. NBR 15220-3 recomenda 40% na ZSB (abertura grande).

² Facies que abre por fachada (FC) contra a porta-batente 200%, janela de correio 50%, basculante 33%, porta-óptica 0%.

³ Privacidade pelo art. 1.301 do Código Civil: janela que olha a divisa a menos de 2,50 m e proteta. O brisa que protege esta norma.

⁴ Seis em cada face com abertura, duas de mais faces = ventilação cruzada.

PROJETO PORTO REAL

RESIDENCIA UNIFAMILIAR (MANAUS - AM) | SUE TATIANA PI

PROJETO ARQUITETONICO

VENTILACAO NATURAL, CRUZADA E PRIVACIDADE

BASE GEOMETRICA	ESCALA	EMISSAO	PRIVACIA
Unia Consolidada	1:100	ESTUDIO PRELIMINAR R72	49
Proj R72 (previsão)	FORMATO A1	NAO LIBERADO PARA OBRA	
UNIDADE MESTRE: AM	MANAUS 66500000	SEM ART / RNT	06-64 REV R72