



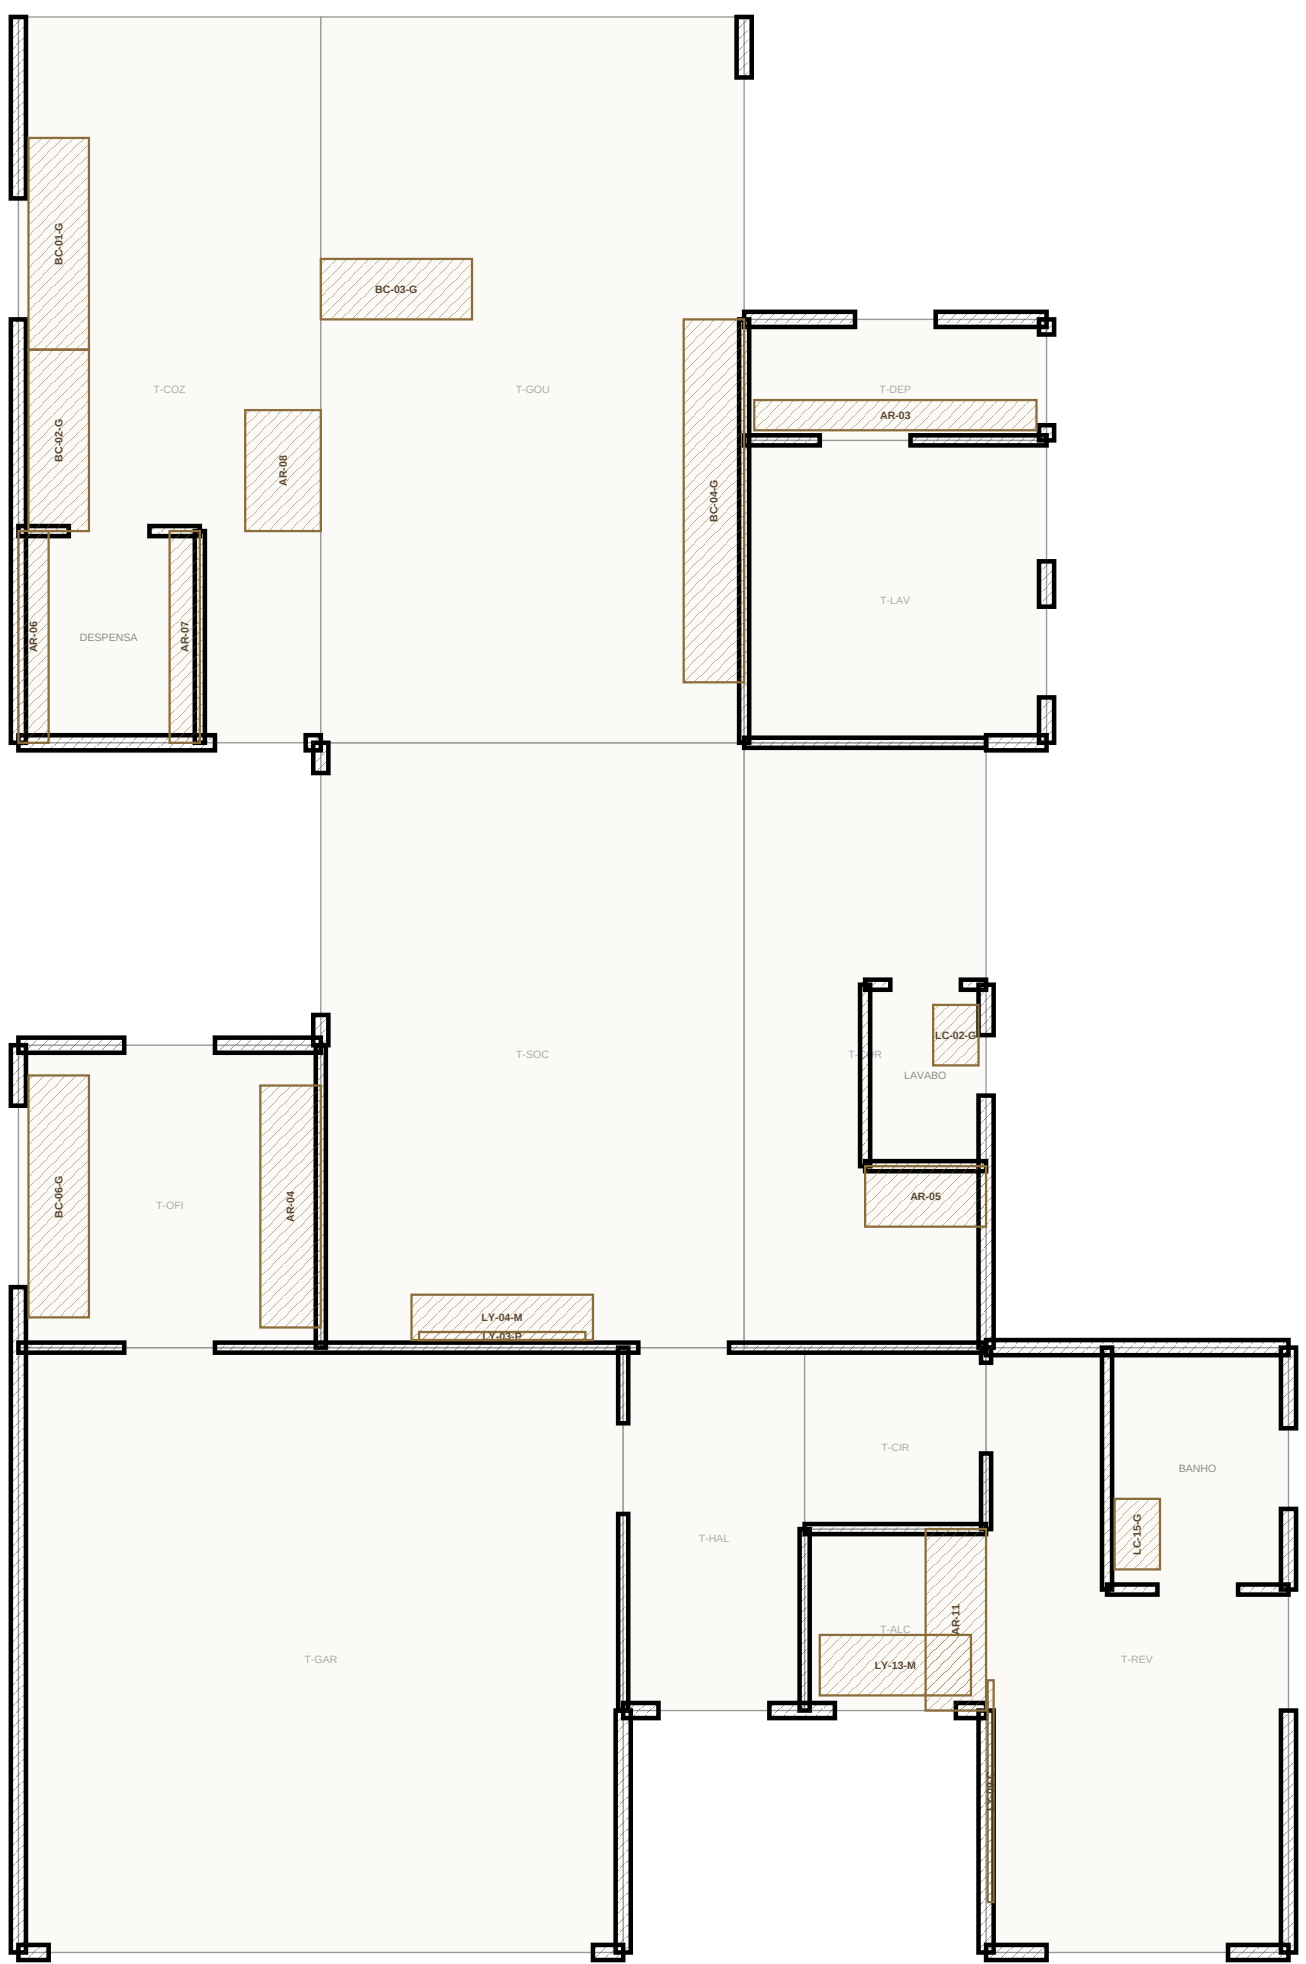

1 TERREO — MARCENARIA
ESCALA 1:75

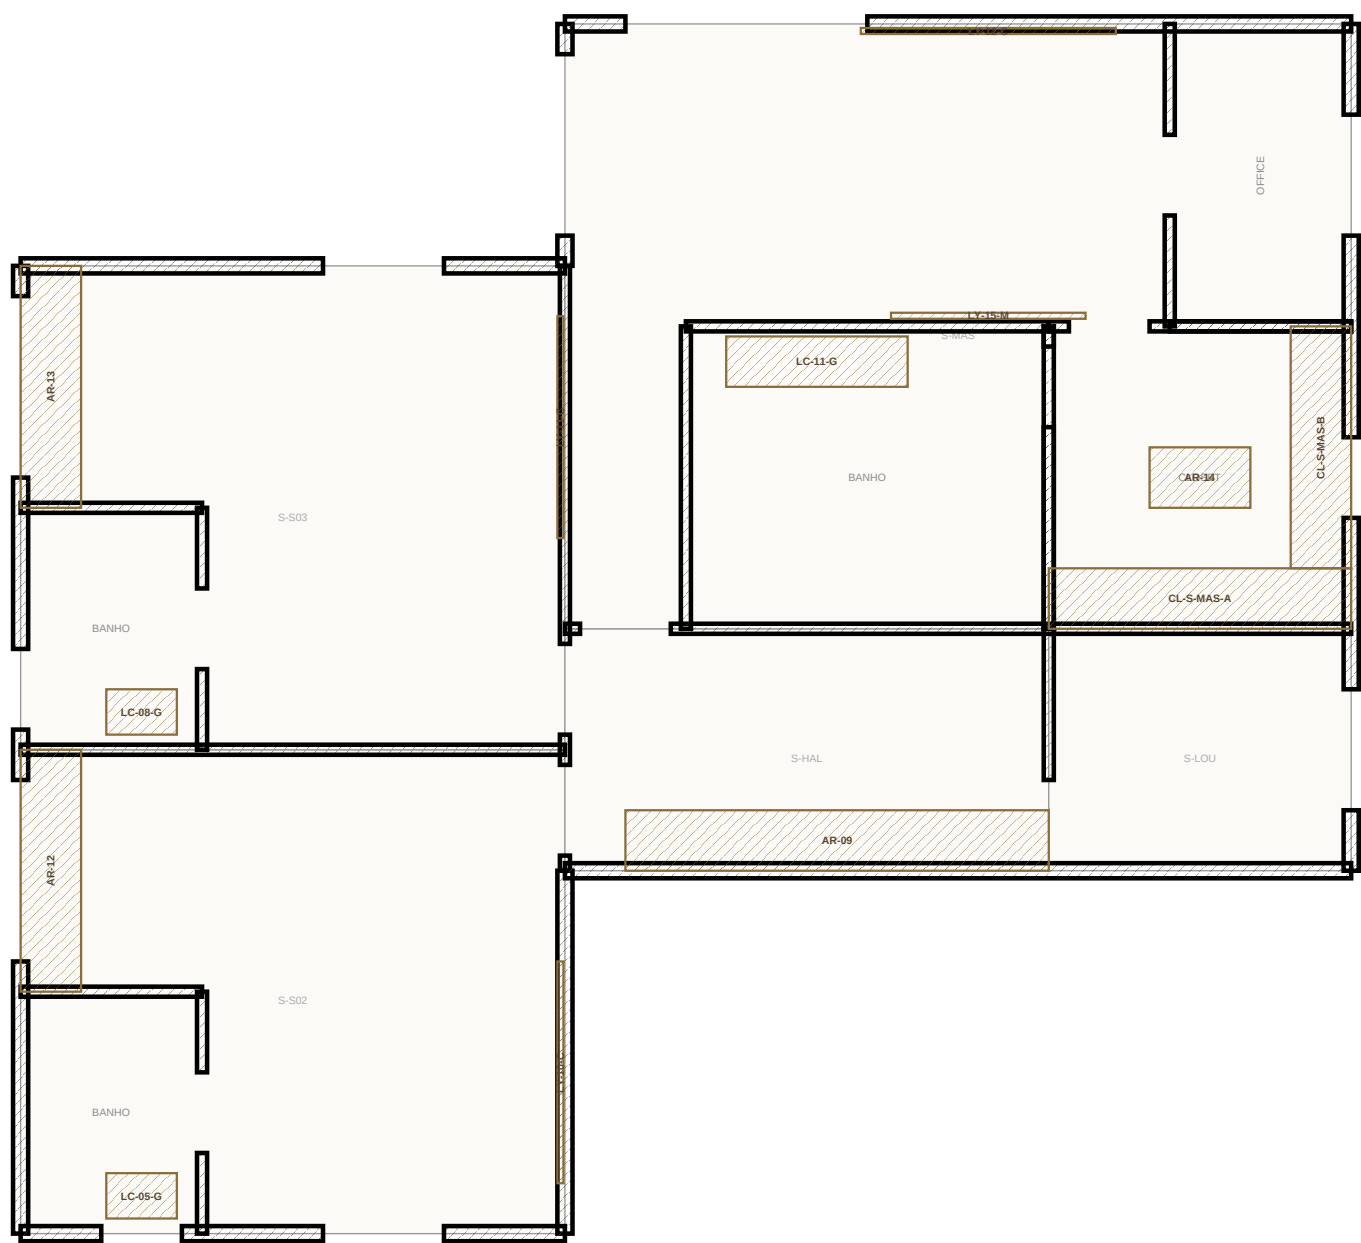

2 SUPERIOR — MARCENARIA
ESCALA 1:75

QUADRO DE MOVEIS — TUDO O QUE E MARCENARIA NA CASA

COD	AMB	FAMILIA	FRENTE	PROF	ALT	MOD	PORTAS	CAV	IND FR
AB-05	T-COR	prateleira	1.200	800	1.200	2	0	0	1.44
AB-06	T-COZ	prateleira	2.100	300	2.200	4	0	0	4.42
AB-07	T-COZ	prateleira	2.100	300	2.200	4	0	0	4.42
AB-08	T-COZ	armario alto	1.200	750	2.200	2	2	0	2.44
AB-09	T-DEP	prateleira	2.800	300	2.200	5	0	0	6.16
AB-04	T-GR	armario alto	2.400	600	2.200	4	4	0	5.28
AB-09	S-HAL	roupa	4.200	600	2.200	7	7	0	9.24
AB-11	T-ALC	guarda-roupa	1.800	600	2.200	3	3	8	3.96
AB-12	S-SO	guarda-roupa	2.400	600	2.200	4	4	8	5.28
AB-13	S-SO	guarda-roupa	2.400	600	2.200	4	4	8	5.28
AB-14	S-MAS	guarda-roupa	1.000	600	900	2	0	8	0.60
BC-01-G	T-COZ	patente	2.100	580	770	4	4	0	1.62
BC-02-G	T-COZ	patente	1.800	580	770	3	3	0	1.26
BC-03-G	T-COZ	patente	1.500	580	770	3	3	0	1.18
BC-04-G	T-COZ	patente	1.800	580	770	4	4	0	2.17
BC-05-G	T-GR	patente	2.400	580	770	4	4	0	1.65
LC-05-G	T-COR	patente banho	800	450	580	1	0	2	0.36
LC-06-G	T-REV	patente banho	700	450	580	2	0	2	0.36
LC-08-G	S-SO	patente banho	700	450	580	2	0	2	0.36
LC-09-G	S-SO	patente banho	700	450	580	2	0	2	0.36
LC-11-G	S-MAS	patente banho	1.800	580	760	3	0	2	0.66
LV-03-P	T-DEC	panela tv	1.800	55	1.800	1	0	5	3.24
LV-04-M	T-SOC	rack	1.800	450	450	3	0	3	0.81
LV-08-C	T-REV	cabineira	2.200	65	1.200	1	0	5	2.64
LV-12-M	T-ALC	mesa	1.500	600	750	1	0	3	1.12
LV-13-C	S-SO	cabineira	2.200	65	1.200	1	0	5	2.64
LV-14-C	S-SO	cabineira	2.200	65	1.200	1	0	5	2.64
LV-15-C	S-MAS	cabineira	2.200	65	1.200	1	0	5	3.04
LV-15-M	S-MAS	panela tv	1.800	55	1.800	1	0	5	3.47
CL-S-MAS-A	S-MAS	closet	3.000	600	2.200	5	0	10	6.60
CL-S-MAS-B	S-MAS	closet	2.400	600	2.200	4	0	8	5.28

TOTAIS

moveis	25
rodape	85
porta	584
porta / guarda	44 164
fronte total	91.34 m2
chapele 15.16 m2	66 1.20

NOTAS

- * Cada moveel vem de nucleos/marcenarias: ARMARIOS, gabinete de cada BANCADA de granito, gabinete suspenso de cada banheiro, rack, painel de TV e mesa de LAYOUT, cabineira de cada cama e as duas paredes do CLOSET.
- * Mobiliario maximo 500 mm (altura da porta), altura por familia (2).
- * Frente e a dimensao da largura da parede, profundidade e o outro. Elevacoes nas PR-05 e 07.
- * Posicao por categoria de ambiente: sala de estar/mesa/grupo nos areas sociais e de servico, cama e 60 gram nos dormitorios.

PROJETO PORTO REAL

RESIDENCIA UNIFAMILIAR (MANSO) - AM | 05/05/2024-05

PROJETO ARQUITETONICO

PLANTA DE MARCENARIA — TERREO E SUPERIOR

BASE GEOMETRICA Unidade Consolidada Projeto (preliminar) Unidade (preliminar)	ESCALA 1:75 FORMATO A1 MILHA 60/60/60/60	ENTRADA ESTUDO PRELIMINAR R72 LADO LIBERADO PARA OBRA SEM ART / RNT	PROJETO 55 05/04/REV072
--	---	--	-------------------------------