



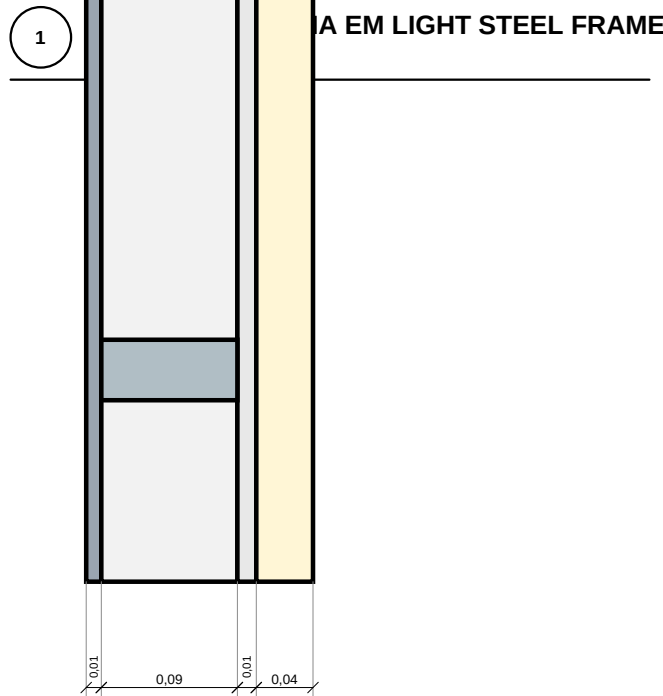


esp. total 150 mm


2 ESCADA — CORTE ESQUEMATICO
ESCALA 1:25

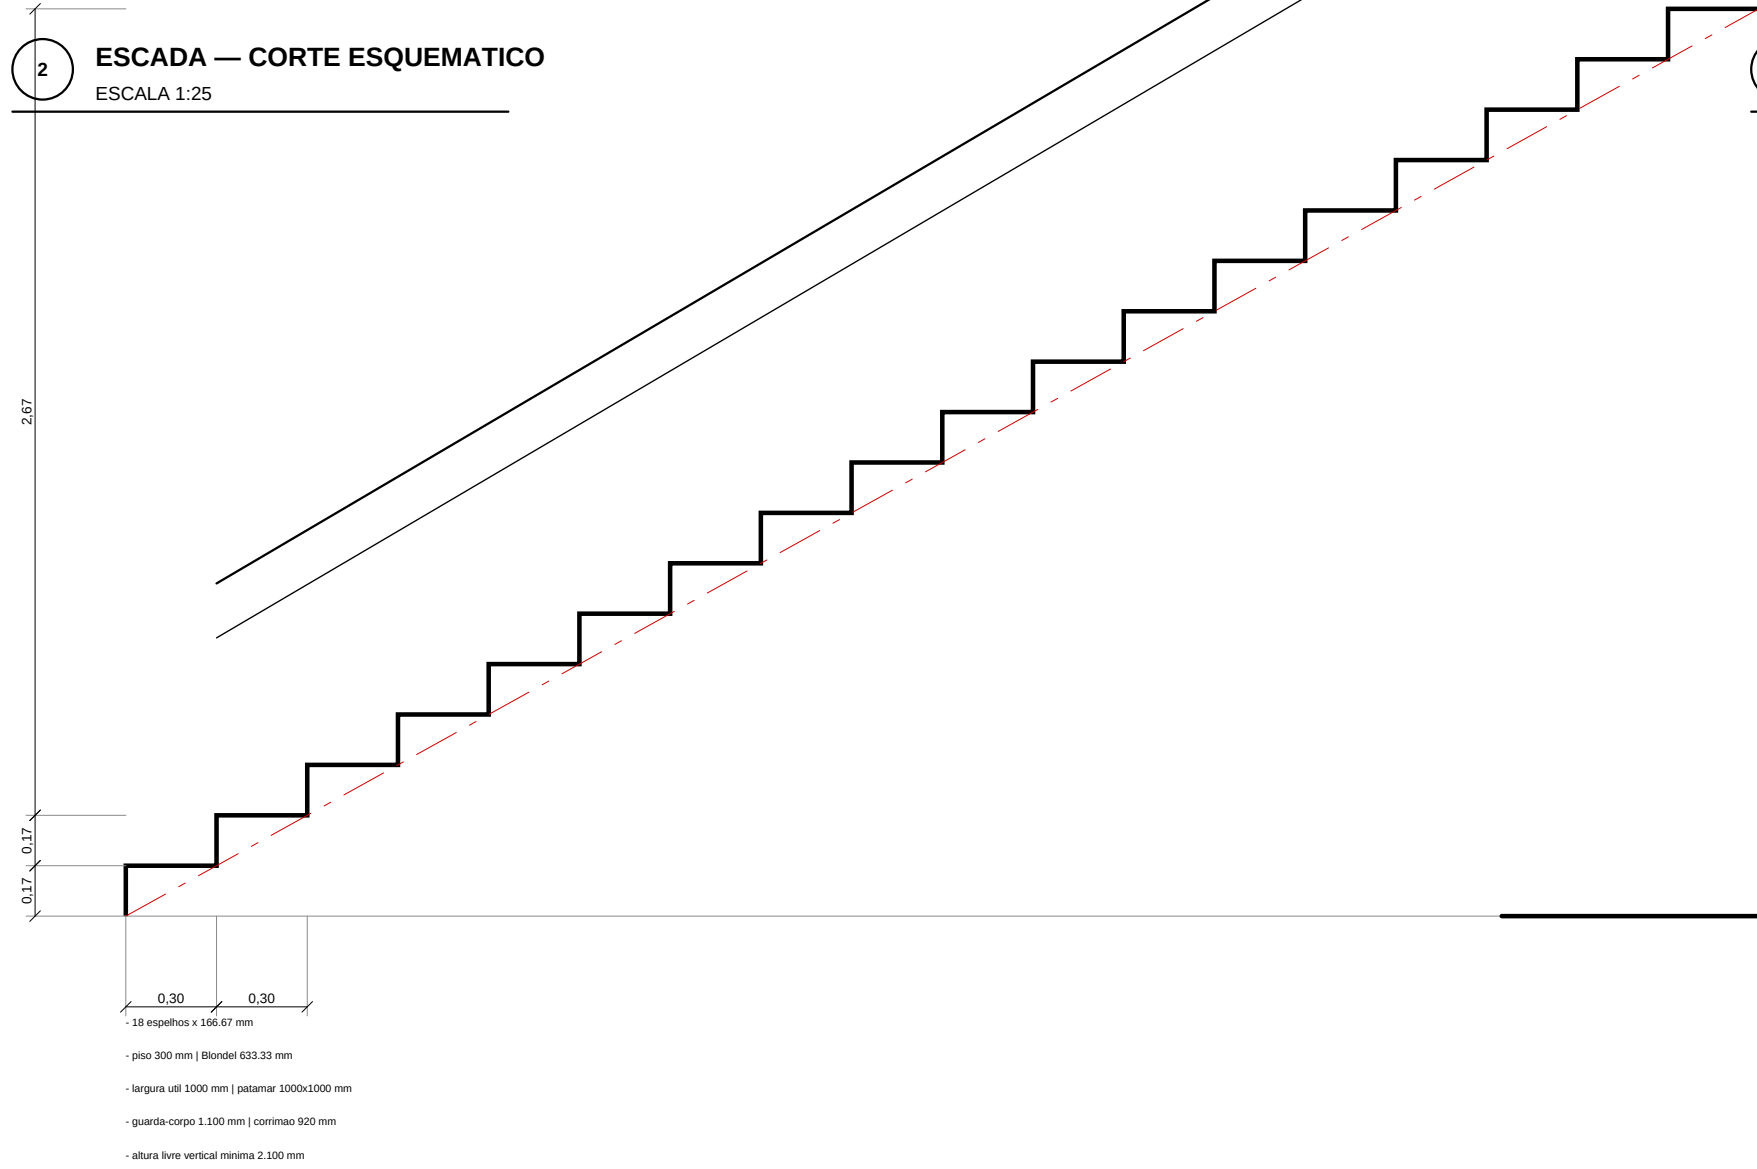

3 PISCINA — CORTE
ESCALA 1:25

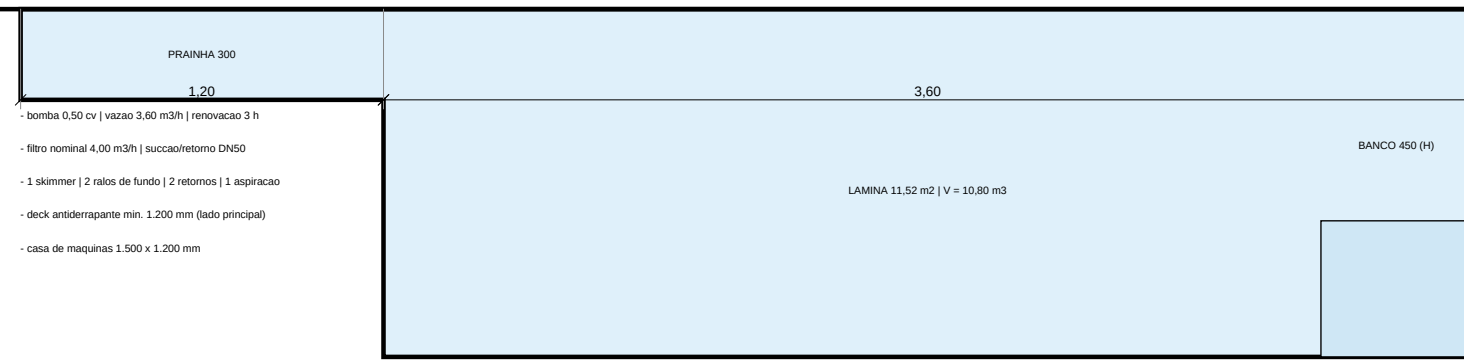

4 FAIXA TECNICA LATERAL — CORTE
ESCALA 1:25

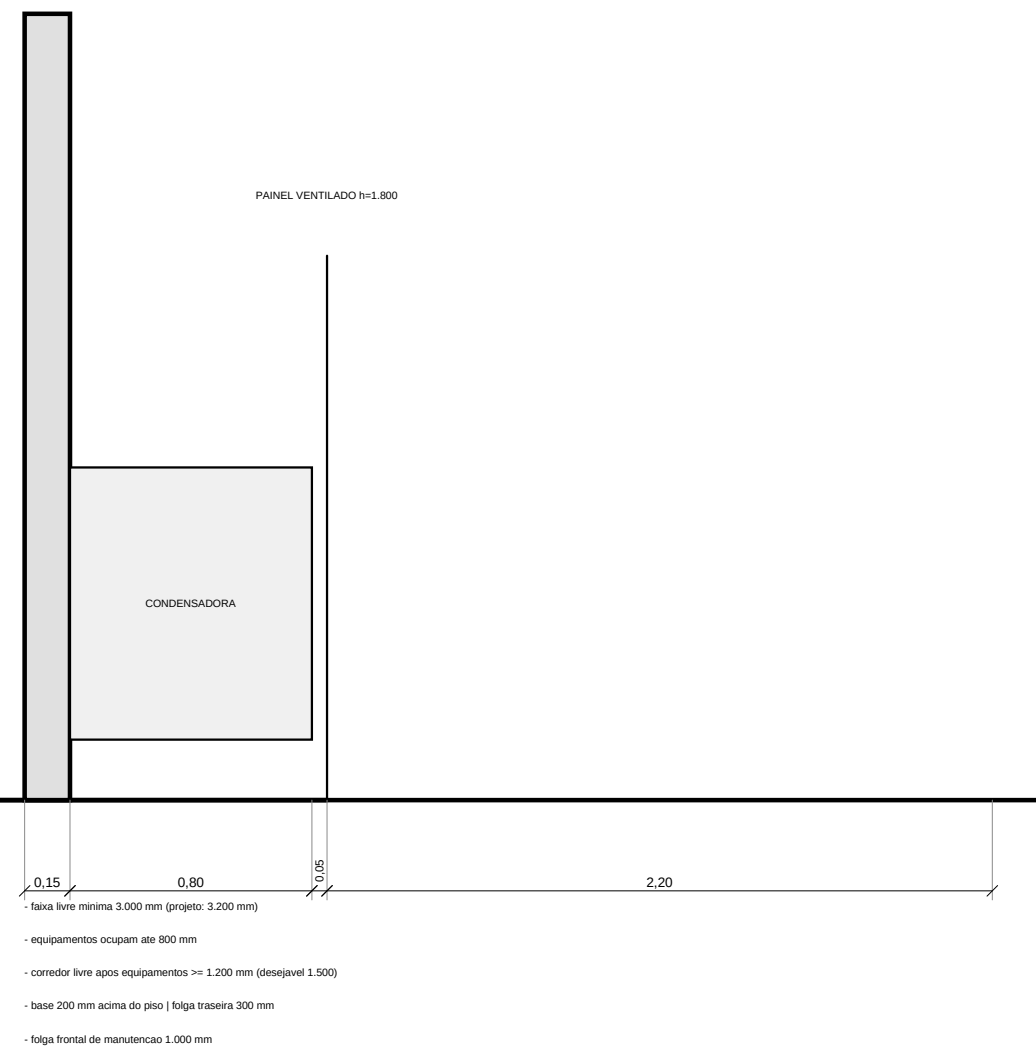

NOTAS

- Detalhes de estado — não liberados para fabricação ou corte (sem revisão confirmada).
- Parede externa consolidada em 120 mm, altura interna em 300 mm (95).
- Escada reconstruída com estrutura, guarda-corpo e espessura de acabamento antes da entrega.

PROJETO PORTO REAL

RESIDENCIA UNIFAMILIAR (MANSUETO - AM) (SOLUÇÕES-PS)

PROJETO ARQUITETONICO

DETALHES CONSTRUTIVOS AMPLIADOS

BASE GEOMETRICA	ESCALA	EMISSÃO	PROJETO
Unidade Consolidada	indicada	ESTUDO PRELIMINAR	10
PS-PS2 (previsão)	FORMATO A1	NO LIBERADO PARA OBRAS	
UNIDADE MENSURA: mm	MALHA 600/600/300	SEM ART / RNT	06.13