


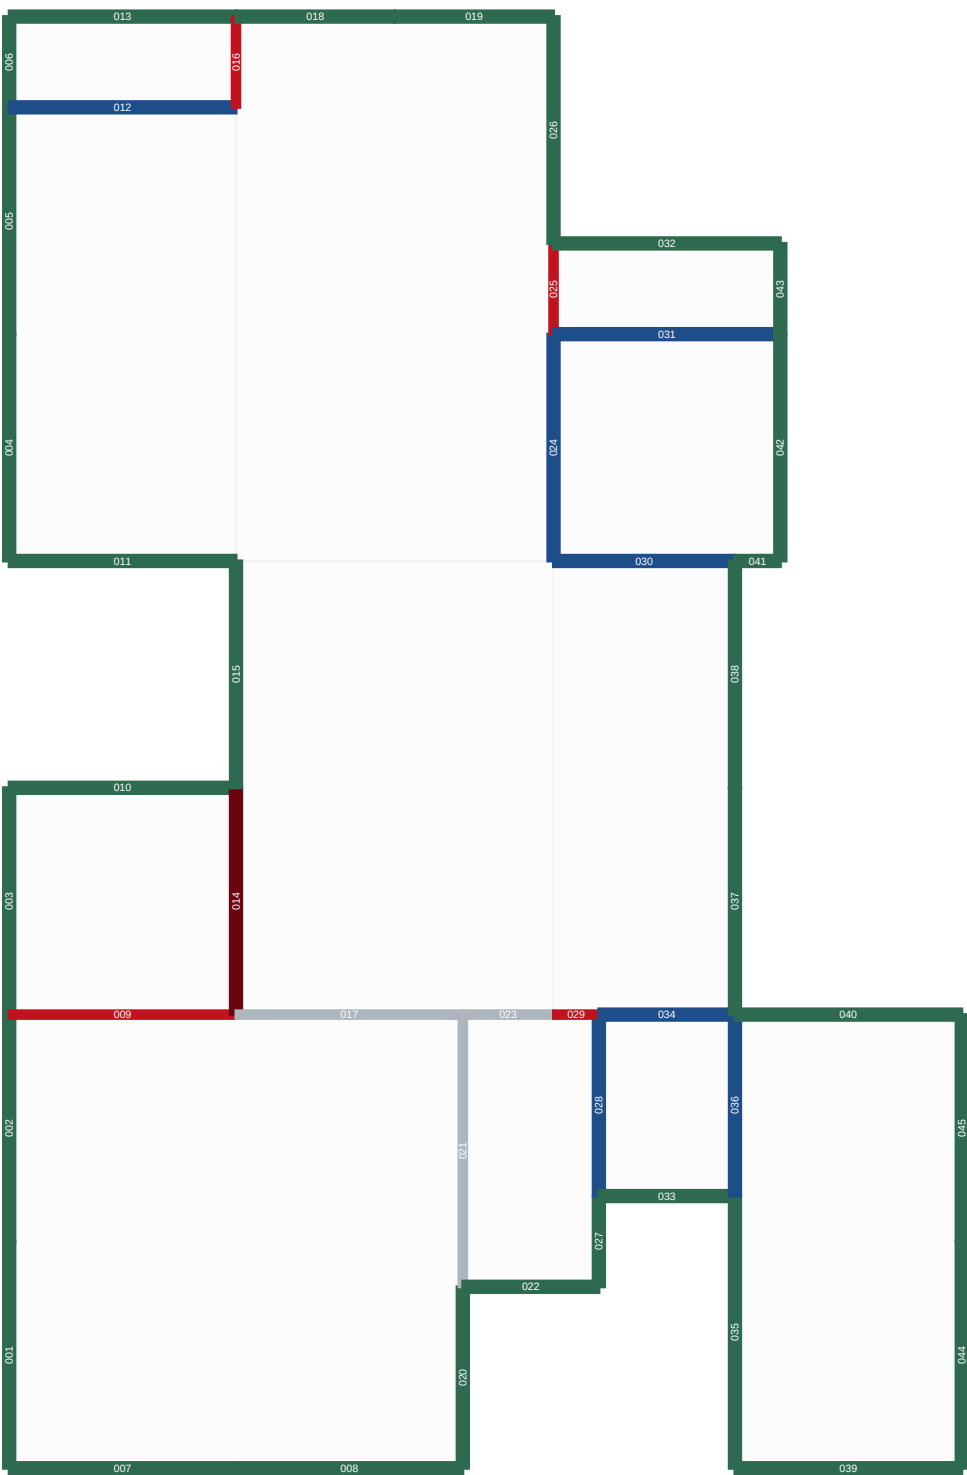

1 PAGINACAO — TERREO
ESCALA 1:100

QUANTITATIVO DE PAINES E MONTANTES

FAMILIA	PAINES	MONTANTES	PI de perfil	COMPOSICAO
PA-1	10	42	109,2	dupla chapa 12,5 + montante 48 x 16 x 40 + dupla chapa 12,5
PA-2	1	6	15,6	dupla chapa 12,5 + perfil oculto + montante 70 x 16 x 80
PE-1	47	248	644,8	laminação 32 x 80 x 50 (SDO enca) + montante 90 x 16 x 90 +
PA-3	7	37	98,2	perfil 60 x 12,5 + montante 90 x 16 x 90 + perfil 12,5 + rebordo
PA-1	3	18	41,8	perfil 12,5 + montante 70 x 16 x 90 + perfil 12,5
TOTAL	68	343	907,4	



EXTRATO DA LISTA DE PAINES (26 de 68)

CODIGO	FAMILIA	LARGO (mm)	ALT (mm)	MONT.	PROV.
PT-001	PE-1	3000	2000	6	T
PT-002	PE-1	3000	2000	6	T
PT-003	PE-1	3000	2000	6	T
PT-004	PE-1	3000	2000	6	T
PT-005	PE-1	3000	2000	6	T
PT-006	PE-1	1200	2000	3	T
PT-007	PE-1	3000	2000	6	T
PT-008	PE-1	3000	2000	6	T
PT-009	PA-1	3000	2000	6	T
PT-010	PE-1	3000	2000	6	T
PT-011	PE-1	3000	2000	6	T
PT-012	PA-1	3000	2000	6	T
PT-013	PE-1	3000	2000	6	T
PT-014	PA-2	3000	2000	6	T
PT-015	PE-1	3000	2000	6	T
PT-016	PA-1	1200	2000	3	T
PT-017	PA-1	3000	2000	6	T
PT-018	PE-1	2100	2000	4	T
PT-019	PE-1	2100	2000	4	T
PT-020	PE-1	2400	2000	5	T
PT-021	PA-1	3000	2000	7	T
PT-022	PE-1	1800	2000	4	T
PT-023	PA-1	1200	2000	3	T
PT-024	PA-1	3000	2000	6	T
PT-025	PA-1	1200	2000	3	T
PT-026	PE-1	3000	2000	6	T

- NOTAS
- * Painéis limitados a 3000 mm por manuseio e transporte.
 - * Montantes a cada 800 mm, 400 mm onde cabido no revestimento exigido.
 - * Não fixar a peça entre em perfil sem código, largura, altura, espessura, material e revest.
 - * Numeração por pavimento, a família define a composição interna do painel.

PROJETO PORTO REAL

RESIDENCIA UNIFAMILIAR (MANAUS - AM) | SOUZA TATIANA-PS

PROJETO ARQUITETONICO

PAGINACAO DE PAINES — LIGHT STEEL FRAME

BASE GEOMETRICA

Lista Consolidada

em PDF (previsão)

UNIDADE: METRO - MM

ESCALA

1:100

FORMATO A1

MAQUA: 600/900/300

EMISSAO

ESTUDIO PRELIMINAR

NAO LIBERADO PARA OBRA

SEM ART / RNT

PROJETO

18

06/18