


VERIFICACAO NBR 9050

ITEM	EXISTENTE	PROJETO	
Visão livre de porta	800 mm	940 mm (altura de 900)	OK
Circuito de giro 360 graus	1.500 mm	hall, banheiro e quarto	OK
Desnível sem rampas	até 5 mm	soluções niveladas	OK
Largura de circulação	900 mm	1.800 mm no hall	OK
Barra de apoio	relevo no piso	instalada na PTE 1 e PTE 2	OK
Barreira acústica	altura livre 750 mm	sem barreiras acústicas	OK
Contraste e interruptor	600 a 1.000 mm	a definir no detalhe	pendente



FLUXOS — SEPARACAO DE CIRCUITOS

CIRCUITO	PERCURSO	CIRCULO SOCIAL?
Serviço	garagem → oficina → lavanderia → cozinha → despensa	NAO
Social	entrada → hall → estar → gourmet → alameda → piscina	—
Área íntima	hall → circulação → banheiro social (quarto reservado) (quarto principal)	NAO
Área superior	hall → casa → hall superior → suíte	NAO
Área de carga	cozinha → despensa → reservado	NAO

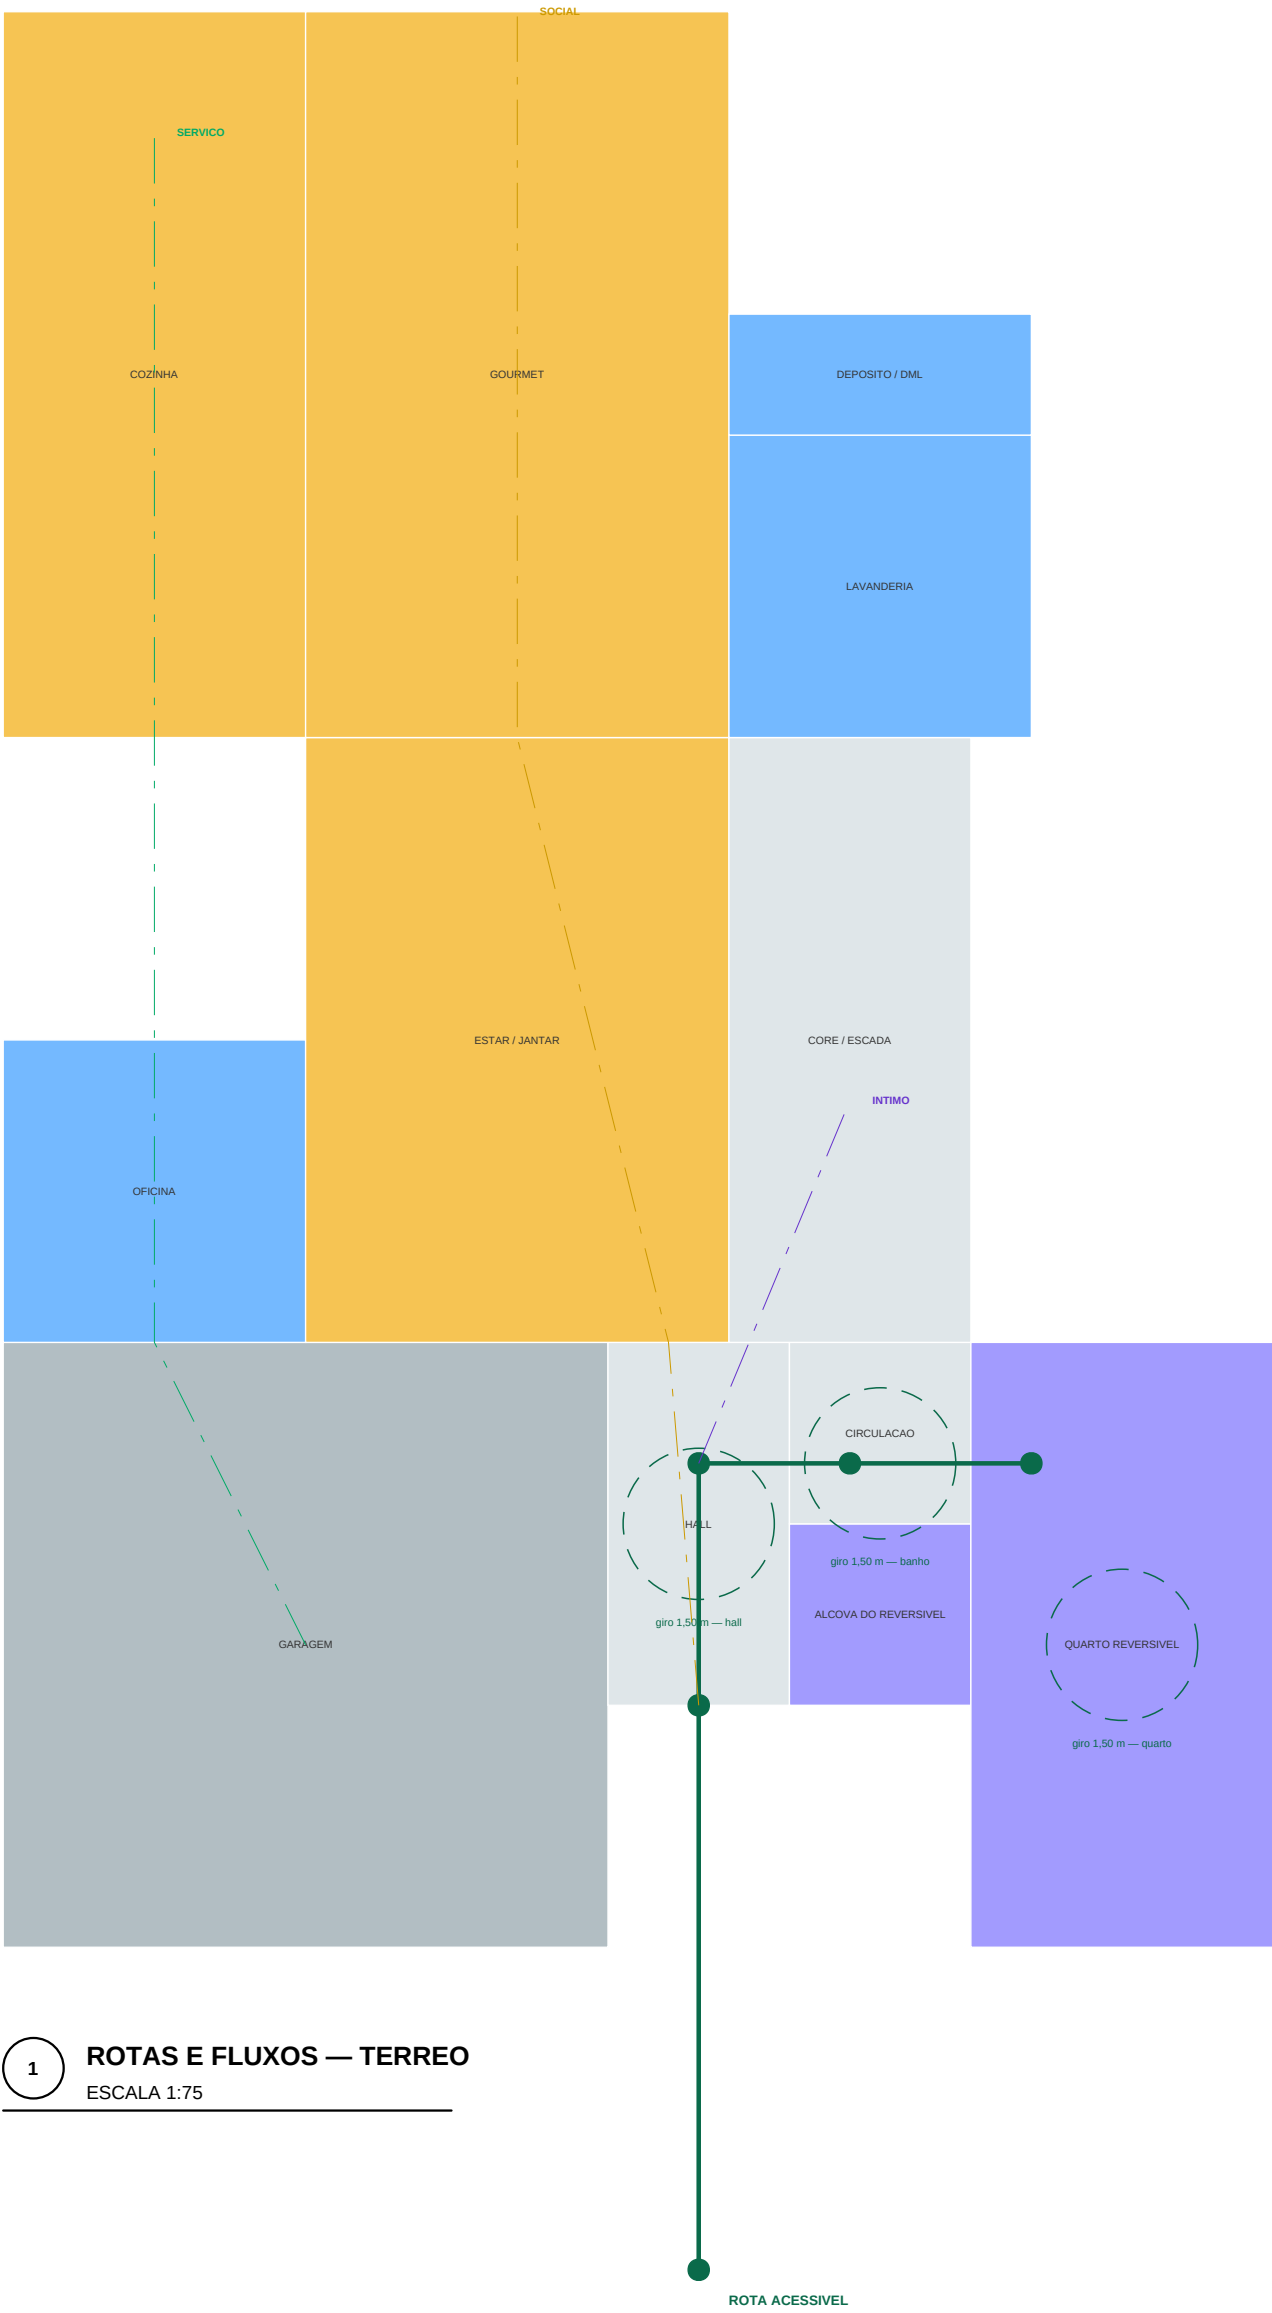

1 ROTAS E FLUXOS — TERREO
ESCALA 1:75

- NOTAS
- * Rota acessível do passeio ao quarto reservado e ao banheiro social.
 - * Circuito de giro de 1.500 mm verificado nos pontos de manobra.
 - * Porta de correr de 900 mm no banheiro social e área de varanda.
 - * Reforço para barra de apoio embutida antes do fechamento das placas.

PROJETO PORTO REAL

RESIDENCIA UNIFAMILIAR (MANSÃO - AM) | SOUZA TATIANA-PS

PROJETO ARQUITETONICO

ACESSIBILIDADE E FLUXOS

BASE GEOMETRICA	ESCALA	EMISSAO	PROJETO
União Consolidada	1:75	ESTUDO PRELIMINAR R12	
ISO-R12 (previsão)	FORMATO A1	NAO LIBERADO PARA OBRA	17
UNIDADE MESTRE: AM	MAI/24 05/05/2025	SEM ART / RNT	04-78 REV R12