


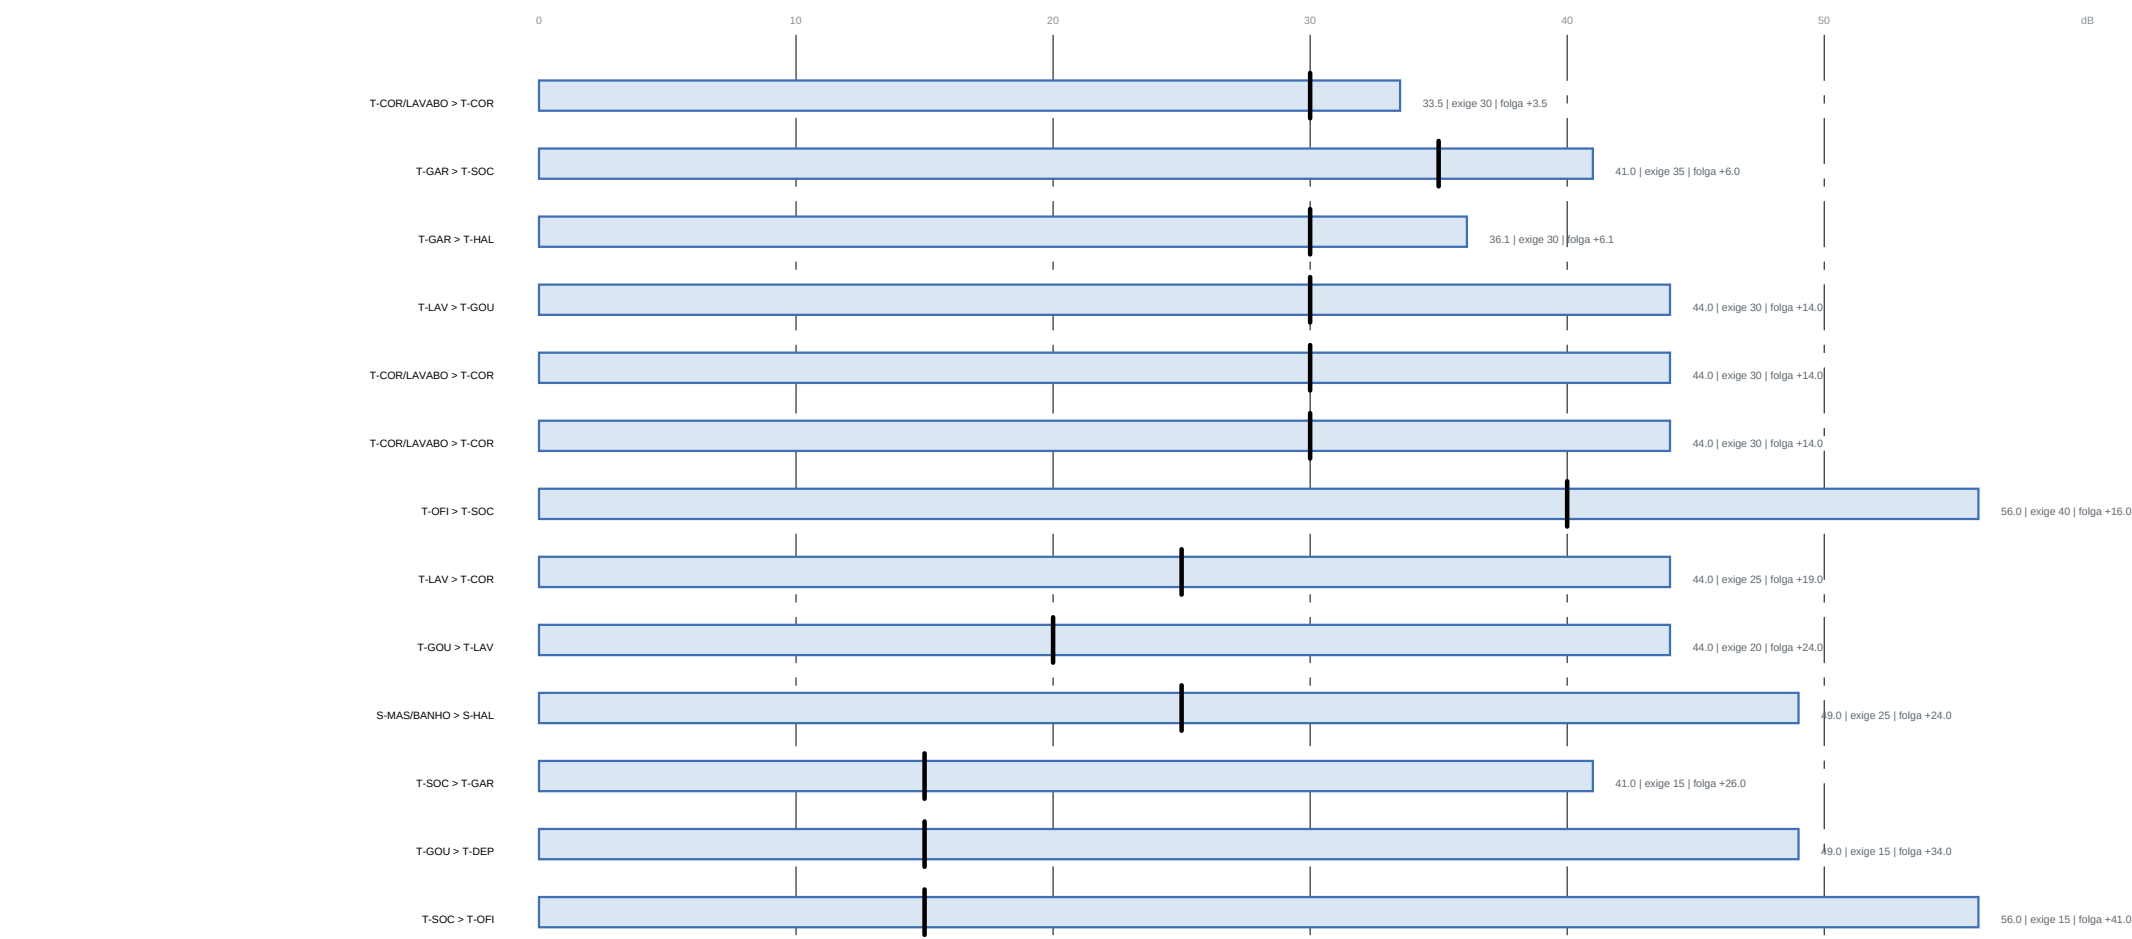

Barra = isolamento ôptico; traço vertical = energia (dB) da fonte menos nível do receptor. NBR 15102

O QUE MUDOU EM R52

ONDE	ANTES	DEPOIS	POR QUE
Banho compartilhado > hall de entrada	porta de correr (Rw 25) — conjunto de 20,2 dB	parede CEGSA, 44 dB	o acesso de volta passou para a circulação
Banho compartilhado > quarto eventual	porta com (Rw 25) — conjunto de 25,3 dB, energia 25	parede CEGSA, 44 dB	era a por passagem da casa, e não era a saída
Hall > garagem	porta seca — 36,9 dB, energia 30	PDS isolada vedada — 36,9 dB	porta entre garagem e casa tem dupla função para ser móbica
Banho compartilhado > circulação	não havia porta	PDS isolada vedada — 35,7 dB, energia 25	único acesso do banho, e abria para fora
Sala de chuveiro	encostado na parede do hall	canto arredondado, toldo e janela alta	consequência da porta nova, a regra dos 900 cm de box obrigou a primeira tentativa

TABELAS ADOTADAS

ITEM	VALOR	FONTE
Fonte: caixa sanitária	75 dB(A)	prática corrente de acústica
Fonte: box de chuveiro	70 dB(A)	prática corrente de acústica
Fonte: cozinha e gourmet	75 dB(A)	prática corrente de acústica
Fonte: sala e jantar	70 dB(A)	prática corrente de acústica
Fonte: garagem	75 dB(A)	prática corrente de acústica
Fonte: máquina de lavar e secar	75 dB(A)	prática corrente de acústica
Fonte: oficina	80 dB(A)	prática corrente de acústica
Límite: banho	45 dB(A)	NBR 15102:2017 (circulação e entrada adjacente)
Límite: circulação	45 dB(A)	NBR 15102:2017 (circulação e entrada adjacente)
Límite: cozinha	45 dB(A)	NBR 15102:2017 (circulação e entrada adjacente)
Límite: depósito	55 dB(A)	NBR 15102:2017 (circulação e entrada adjacente)
Límite: dormitório	35 dB(A)	NBR 15102:2017 (circulação e entrada adjacente)
Límite: entrada	45 dB(A)	NBR 15102:2017 (circulação e entrada adjacente)
Límite: estar	45 dB(A)	NBR 15102:2017 (circulação e entrada adjacente)
Límite: garagem	55 dB(A)	NBR 15102:2017 (circulação e entrada adjacente)
Límite: office	45 dB(A)	NBR 15102:2017 (circulação e entrada adjacente)
Límite: oficina	55 dB(A)	NBR 15102:2017 (circulação e entrada adjacente)
Límite: serviço	55 dB(A)	NBR 15102:2017 (circulação e entrada adjacente)
Fonte: academia	Pin 25 dB	Nota de mercado declarada
Fonte: cinema	Pin 25 dB	Nota de mercado declarada
Fonte: sala	Pin 20 dB	Nota de mercado declarada
Fonte: sala de	Pin 25 dB	Nota de mercado declarada
Fonte: sala de visita	Pin 30 dB	Nota de mercado declarada

NOTAS

1 Esta planilha existe porque o proprietário perguntou o que 100 verificações não sabem responder: quem entra na casa ouve o chuveiro do banho da entrada?

2 Ouviu. A parede era box (Pin 1, Pin 44) e a porta era de correr (Rw 25), o conjunto entregava 20 dB. Em acústica o eixo físico DOMINA — não se faz média aritmética do isolamento, se soma energia que passa.

3 Isolamento ou se ouve ENTRE portas. Dentro da file social o ruído não é definido, é o programa.

4 O adotado igual ao R52 (comprimento declarado), não o pre-verificação de projeto, não enviado de campo da NBR 15107-3.

PROJETO PORTO REAL

RESIDENCIA UNIFAMILIAR (MANSÃO - AM) | SOBR TATIANA-PS

PROJETO ARQUITETÔNICO

DESEMPENHO ACUSTICO ENTRE AMBIENTES

BASE GEOMÉTRICA	ESCALA	EMISSÃO	PROVA
Lista Consolidada	s/ escala	ESTUDO PRELIMINAR R52	
Pin R52 (previsão)	FORMATO A1	NAO LIBERADO PARA OBRA	39
UNIDADE MESTRE: mm	MILIMETROS (1:500000)	SEM ART / RNT	IN-TE REVIEW