



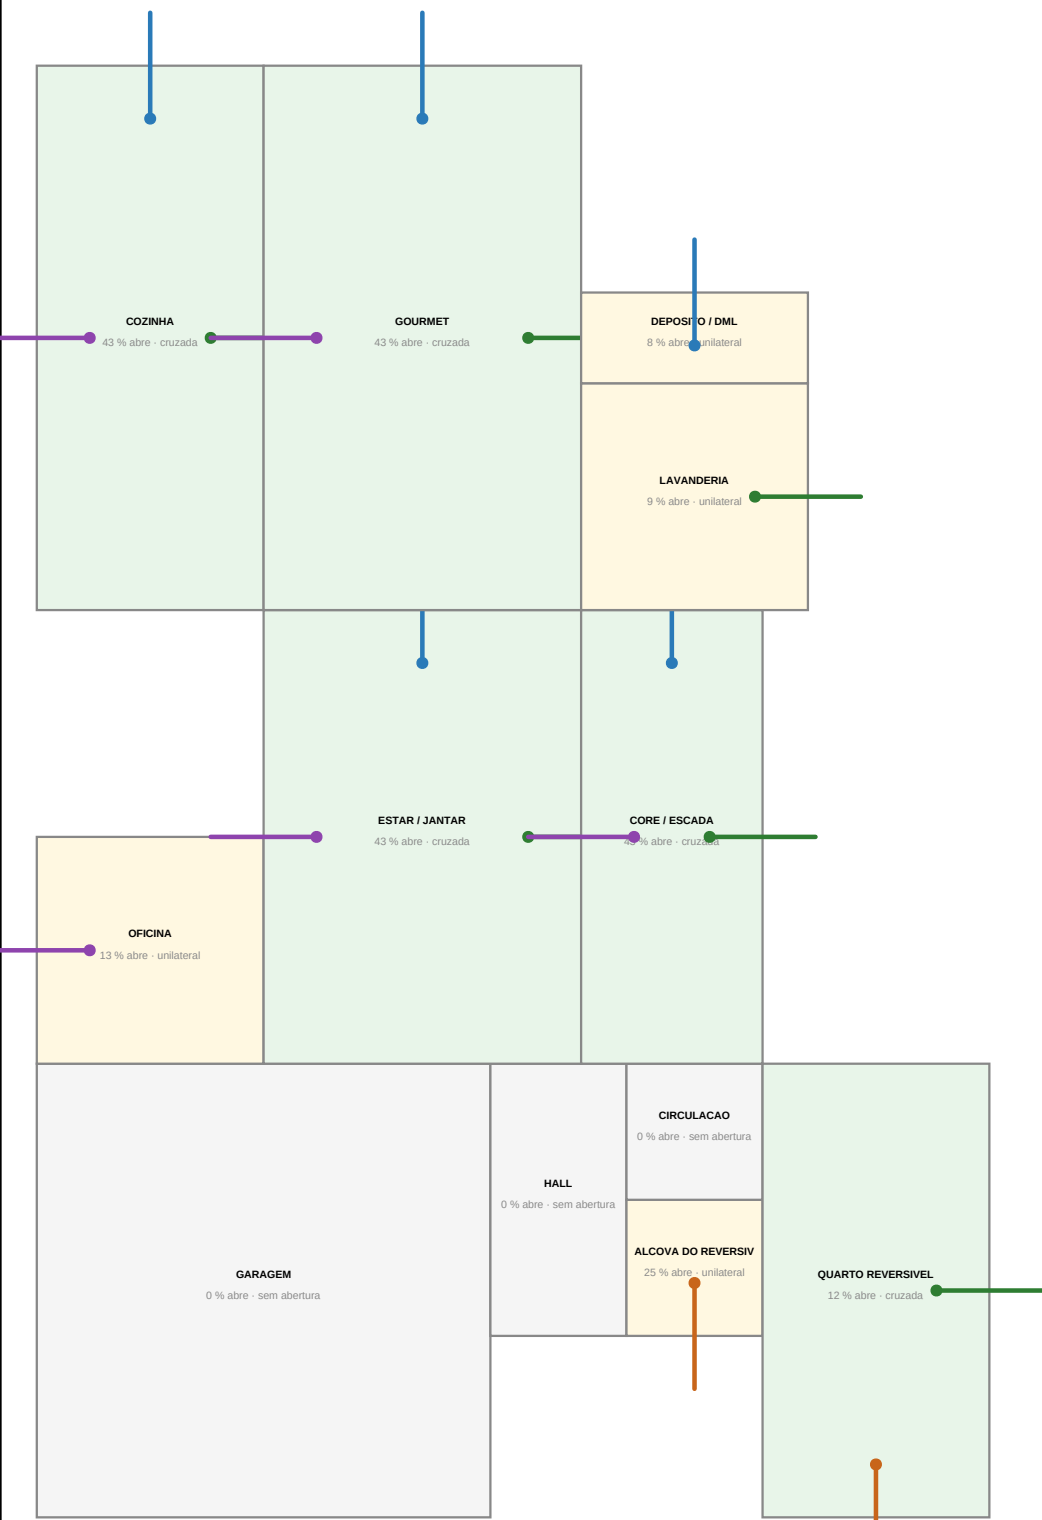

1 TERREO — faces que abrem
ESCALA 1:100

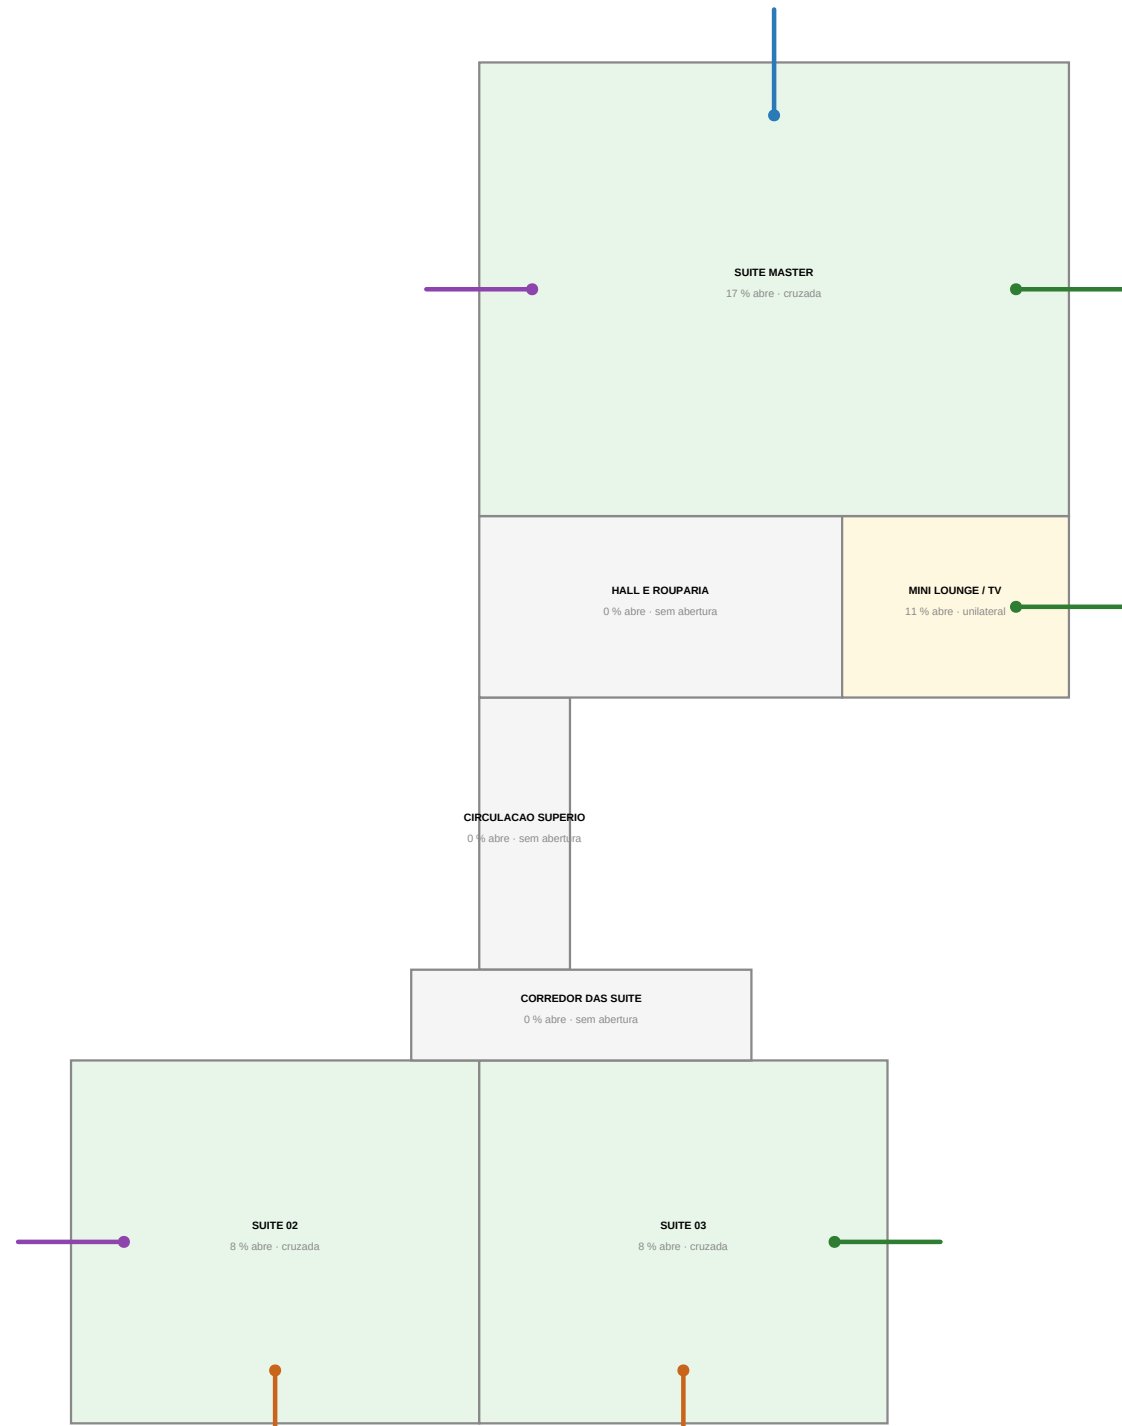

2 SUPERIOR — faces que abrem
ESCALA 1:100

VENTILACAO POR AMBIENTE

COD	AMBIENTE	CAT.	PRO. m²	ABRE. m²	PERIM.	FACIES	TIPO	NOTA
T-001	COZINHA	INTERIO	34,3	0,00	0 m	—	—	Y/N
T-002	HALL	INTERIO	5,8	0,00	0 m	—	—	Y/N
T-003	ALCOVA DO REVERSIVEL	INTERIO	2,8	0,72	25 m	L	unidirecional	OK
T-004	CIRCULACAO	INTERIO	2,8	0,00	0 m	—	—	Y/N
T-005	QUARTO REVERSIVEL	INTERIO	26,7	2,04	22 m	L,N	cruzada	OK
T-006	OFICINA	INTERIO	43	1,08	22 m	S	unidirecional	Y/N
T-007	ESTAR/JANTAR	INTERIO	86,7	36,86	43 m	N,D,S	cruzada	OK
T-008	CORR. ESCADA	INTERIO	86,7	36,86	43 m	N,D,S	cruzada	Y/N
T-009	COZINHA	INTERIO	86,7	36,86	43 m	N,D,S	cruzada	OK
T-010	GOURMET	INTERIO	86,7	36,86	43 m	N,D,S	cruzada	OK
T-011	LAVANDERIA	INTERIO	8,3	0,72	9 m	N	unidirecional	Y/N
T-012	DEPOSITO DmL	INTERIO	3,1	0,24	8 m	O	unidirecional	Y/N
S-001	SUITE 02	INTERIO	26,5	2,04	8 m	L,S	cruzada	OK
S-002	SUITE 03	INTERIO	26,7	2,04	8 m	L,N	cruzada	OK
S-003	CIRCULACAO SUPERIOR	INTERIO	3,8	0,00	0 m	—	—	Y/N
S-004	CORREDOR DAS SUITES	INTERIO	4,6	0,00	0 m	—	—	Y/N
S-005	HALL E ROUPARIA	INTERIO	10,6	0,00	0 m	—	—	Y/N
S-006	MINI LOUNGE / TV	INTERIO	9,5	0,72	11 m	N	unidirecional	OK
S-007	SUITE MASTER	INTERIO	44,9	7,60	17 m	N,D,S	cruzada	OK

PRIVACIDADE — CADA JANELA CONTRA A DIVISA QUE OLHA (art. 1.301 CC)

VAO	AMB	FACE	DIST. m	MIN. m	PROTEC.	ORIE	LEITURA	
001	T-REV	N	8,00	1,50	1500	—	diagonal	OK
002	T-COR	N	8,00	1,50	1500	—	diagonal	OK
003	T-REV	L	7,20	—	1100	BR-L	rua	OK
004	T-REV	N	8,00	1,50	1100	—	diagonal	OK
005	T-ALC	L	9,60	—	1000	—	rua	OK
006	T-OFI	S	3,40	1,50	1100	—	exposto ao vento	OK
007	T-COR	S	3,40	1,50	1100	—	exposto ao vento	OK
008	T-LAV	N	7,40	1,50	1100	—	diagonal	OK
009	T-DEP	O	30,80	1,50	1500	—	diagonal	OK
010	T-COR	N	8,00	1,50	9	—	diagonal	OK
011	T-GOU	N	30,40	1,50	9	—	diagonal	OK
012	T-GOU	O	33,60	1,50	9	BR-O	protetida por telas	OK
013	T-COC	S	5,40	1,50	9	—	diagonal	OK
014	S-GOU	N	4,40	1,50	1100	—	diagonal	OK
015	S-SU2	S	3,40	1,50	1100	—	exposto ao vento	OK
016	S-SU2	L	7,20	—	1100	BR-L	rua	OK
017	S-SU2	L	7,20	—	1200	BR-L	rua	OK
018	S-SU2	N	6,80	1,50	1100	—	diagonal	OK
019	S-SU3	L	7,20	—	1100	BR-L	rua	OK
020	S-SU3	N	6,80	1,50	1200	—	diagonal	OK
021	S-MNS	S	7,80	1,50	1100	—	diagonal	OK
022	S-MNS	O	14,80	1,50	9	—	diagonal	OK
023	S-MNS	N	4,40	1,50	1500	—	diagonal	OK
024	S-MNS	N	4,40	1,50	1100	—	diagonal	OK

- NOTAS
- ¹ Área que ABRE por ambiente contra a área do piso. NBR 15275-4 exige 0 m e região Norte. NBR 15275-3 recomenda 40 m na ZSB (abertura grande).
 - ² Fritas que abrem por janela (JC) contra a parede lateral 200 m, janela de corte 50 m, base lateral 33 m, porta opaca 0 m.
 - ³ Privacidade pelo art. 1.301 do Código Civil: janela que olha a divisa a menos de 2,50 m e proteção. O brisa que protege esta norma.
 - ⁴ Seis em cada face com abertura, duas de mais faces e ventilação cruzada.

PROJETO PORTO REAL

RESIDENCIA UNIFAMILIAR (MANSÃO - AM) | SUITE TATIANA-01

PROJETO ARQUITETONICO

VENTILACAO NATURAL, CRUZADA E PRIVACIDADE

BASE GEOMETRICA União Consolidada Projeto (preliminar) União (preliminar)	ESCALA 1:100 FORMATO A1 MANSÃO 400/500/300	ENTRADA ESTUDO PRELIMINAR R12 UNÃO LIBERADO PARA OBRA SEM ART / RNT	PRIVACIDADE 49 60 m REV R12
--	---	--	-----------------------------------