
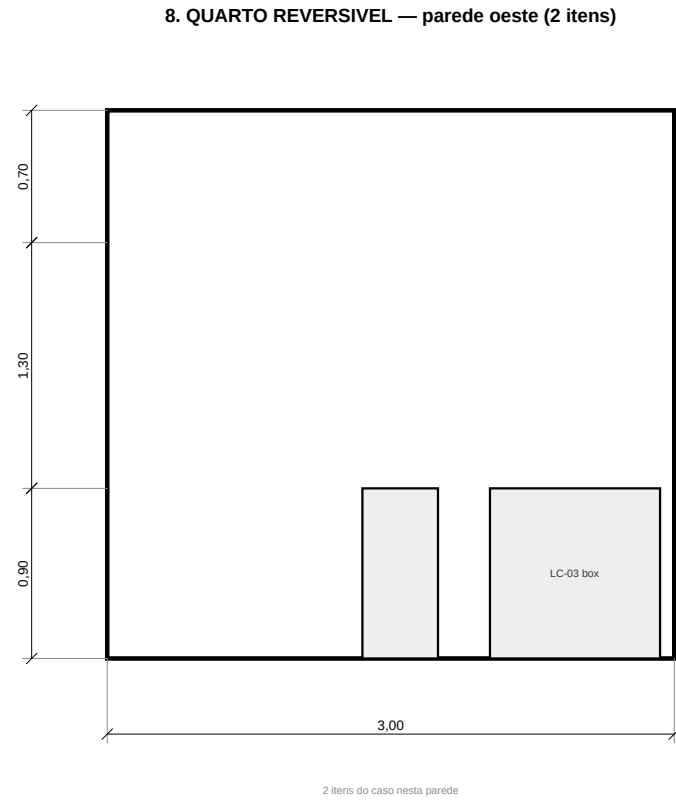
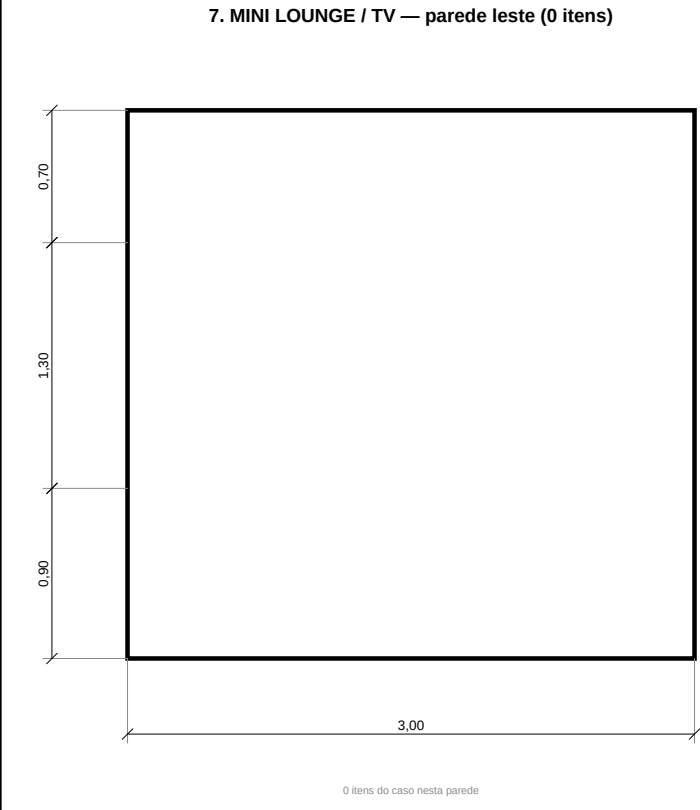
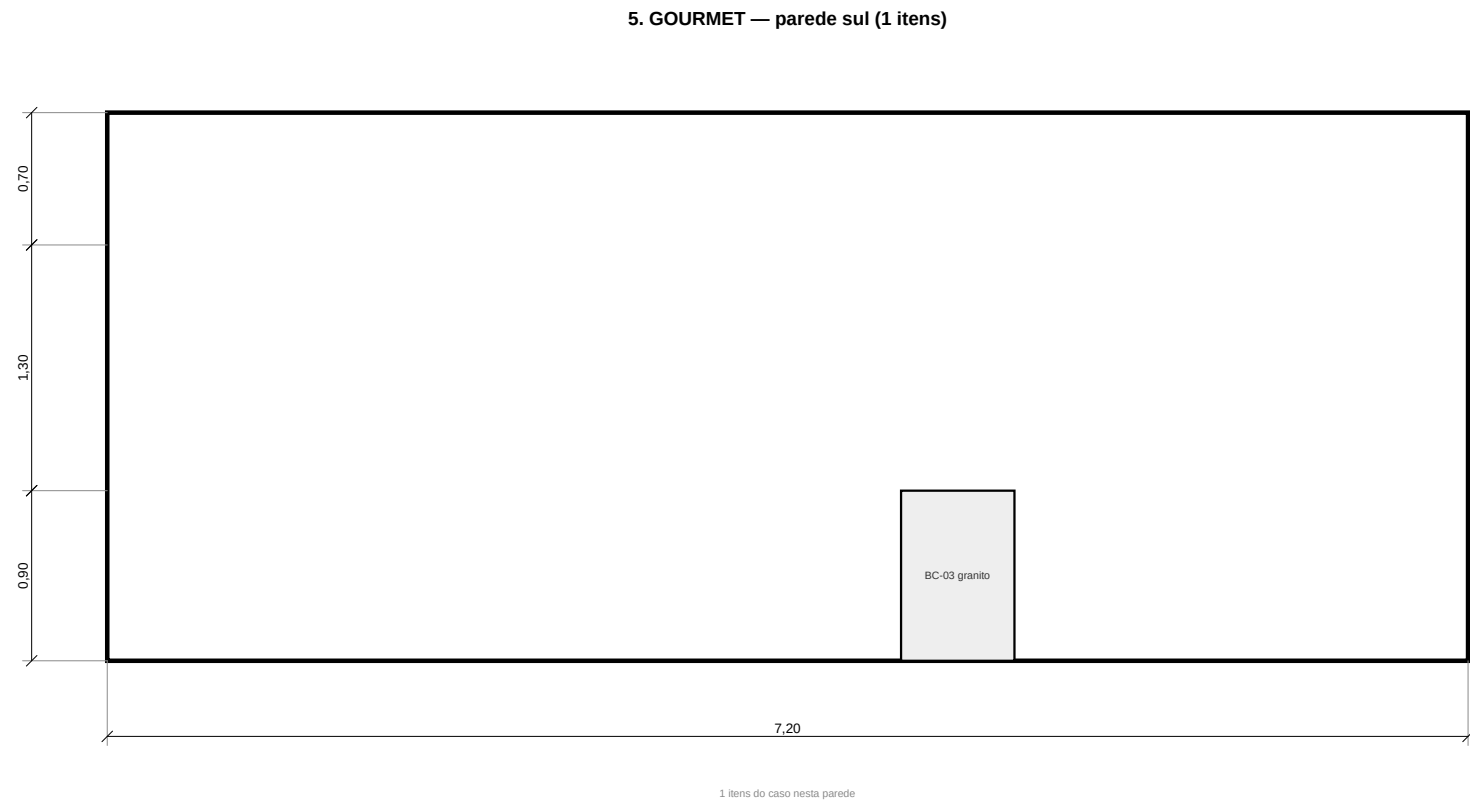
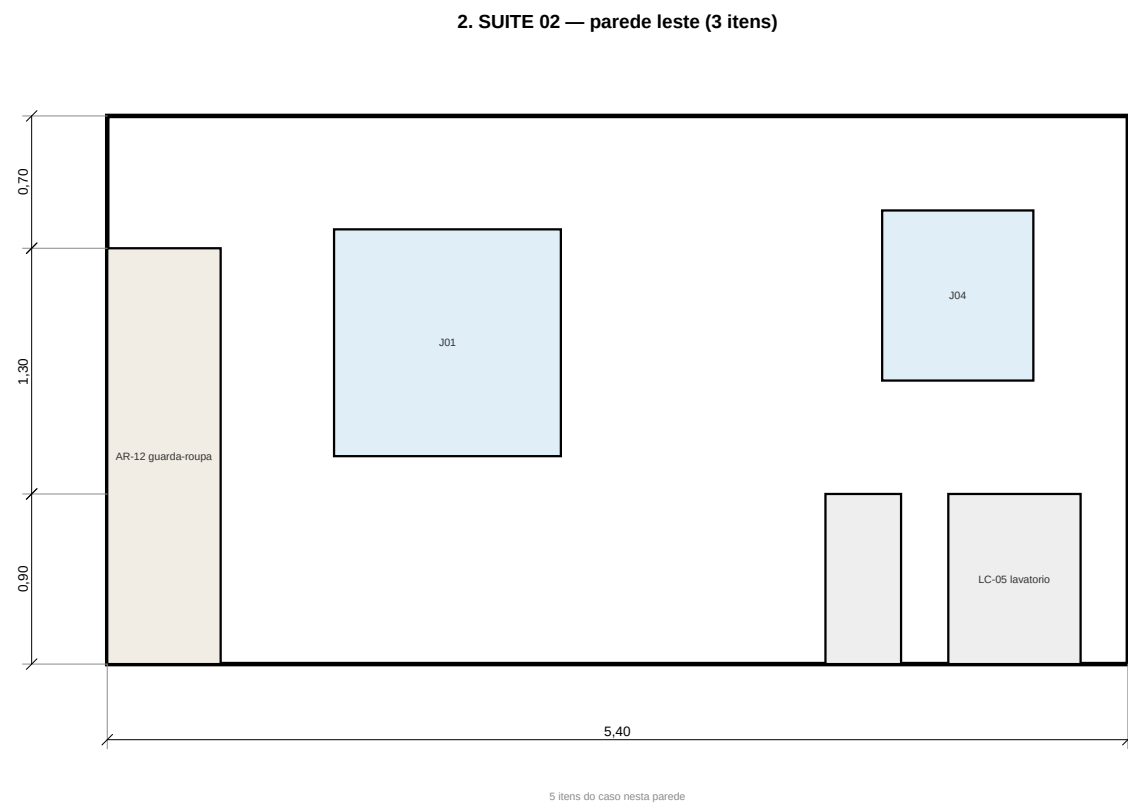


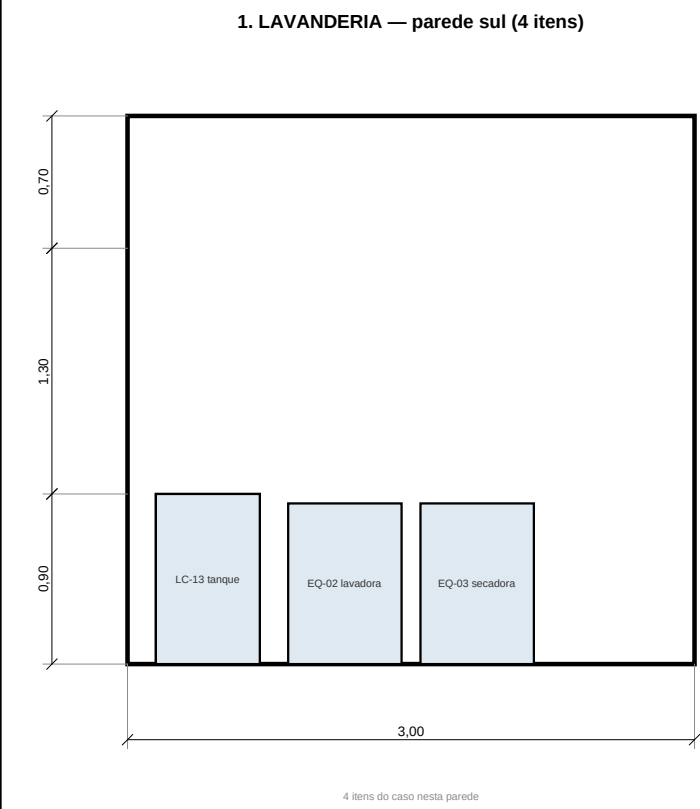

- NOTAS
- Cada item desenvolvido vem de ARMAZENOS, BANCADAS, LOCAIS, EQUIPAMENTOS ou LAYOUT do caso, pelo código, numeração modular fixa digitada nesta planilha.
 - Um item está na parede quando encosta nela a menos de 200 mm. Abaixo por família (F).
 - Janelas e portas da parede vem de VAOCL, com perfil e altura da esquadra.
 - Complementos a PR-10 (piscina, churras, banheiro, quarto master, oficina, lavanderia).

PROJETO PORTO REAL

RESIDENCIA UNIFAMILIAR (MARAUÁ - AM) | SUITE TUPAIA-PS

PROJETO ARQUITETONICO

ELEVACOES INTERNAS II — DERIVADAS DO MODELO

BASE GEOMETRICA	ESCALA	EMISSAO	PROJECION
União Consolidada	1:40	ESTUDO PRELIMINAR R12	51
PR-102 (previsível)	FORMATO A1	IMAG. LIBERADO PARA ORCA	SEM ART / RNT
UNIDADE METRICA: MM	MILHA 465/500/500		6/18 REV R12